Sheet Number	Tekst:	Dato:	Rev.:	Rev. Dato:
ISP2_K07_L2XX_H04_EXX_N930 - Side I1-1	Byg I1 - Index	2026-02-27		
ISP2_K07_L2XX_H04_EXX_N930 - Side I1-2	Byg I1 - Oversigtsplan	2026-02-27		
ISP2_K07_L2XX_H04_EXX_N930 - Side I1-3	Byg I1 - St. til 2. Sal, Byg A	2026-02-27		
ISP2_K07_L2XX_H04_EXX_N930 - Side I1-4	Byg I1 - St. til 2. Sal, Byg B	2026-02-27		
ISP2_K07_L2XX_H04_EXX_N930 - Side I1-5	Byg I1 - St. til 2. Sal, Byg C	2026-02-27		
ISP2_K07_L2XX_H04_EXX_N930 - Side I1-6	Byg I1 - Stueplan, Byg D	2026-02-27		
ISP2_K07_L2XX_H04_EXX_N930 - Side I1-7	Byg I1 - Stueplan, Byg E	2026-02-27		
ISP2_K07_L2XX_H04_EXX_N930 - Side I1-8	Byg I1 - Stueplan, Byg E	2026-02-27		
ISP2_K07_L2XX_H04_EXX_N930 - Side I1-9	Byg I1 - ST. til 2. Sal, Byg F	2026-02-27		
ISP2_K07_L2XX_H04_EXX_N930 - Side I1-10	Byg I1 - ST. til 2. Sal, Byg G	2026-02-27		
ISP2_K07_L2XX_H04_EXX_N930 - Side I1-11	Byg I1 - 1. Sal, Byg D	2026-02-27		
ISP2_K07_L2XX_H04_EXX_N930 - Side I1-12	Byg I1 - 1. Sal, Byg D	2026-02-27		
ISP2_K07_L2XX_H04_EXX_N930 - Side I1-13	Byg I1 - 1. Sal, Byg D	2026-02-27		
ISP2_K07_L2XX_H04_EXX_N930 - Side I1-14	Byg I1 - 1. Sal, Byg E	2026-02-27		
ISP2_K07_L2XX_H04_EXX_N930 - Side I1-15	Byg I1 - 1. Sal, Byg E	2026-02-27		
ISP2_K07_L2XX_H04_EXX_N930 - Side I1-16	Byg I1 - 2. Sal, Byg D	2026-02-27		
ISP2_K07_L2XX_H04_EXX_N930 - Side I1-17	Byg I1 - 2. Sal, Byg D	2026-02-27		
ISP2_K07_L2XX_H04_EXX_N930 - Side I1-18	Byg I1 - 2. Sal, Byg D	2026-02-27		
ISP2_K07_L2XX_H04_EXX_N930 - Side I1-19	Byg I1 - 2. Sal, Byg E	2026-02-27		
ISP2_K07_L2XX_H04_EXX_N930 - Side I1-20	Byg I1 - 2. Sal, Byg E	2026-02-27		
ISP2_K07_L2XX_H04_EXX_N930 - Side I1-21	Byg I1 - 3. Sal, Byg D	2026-02-27		
ISP2_K07_L2XX_H04_EXX_N930 - Side I1-22	Byg I1 - 3. Sal, Byg D	2026-02-27		
ISP2_K07_L2XX_H04_EXX_N930 - Side I1-23	Byg I1 - 3. Sal, Byg E	2026-02-27		
ISP2_K07_L2XX_H04_EXX_N930 - Side I1-24	Byg I1 - 3. Sal, Byg E	2026-02-27		
ISP2_K07_L2XX_H04_EXX_N930 - Side I1-25	Byg I1 - 4. Sal, Byg E	2026-02-27		
ISP2_K07_L2XX_H04_EXX_N930 - Side I1-26	Byg I1 - 4. Sal, Byg E	2026-02-27		

Projekt: Stejlepladsen


Tekst: Elinstallationer - Byg I1 - Index


Tegningsnr.: ISP2_K07_L2XX_H04_EXX_N930


Rev.:

Projektnr.: 1019198 | Dato: 2026-02-27 | Rev. Dato: | Mål: | Side: I1-1


www.arteliagroup.dk | Fil:

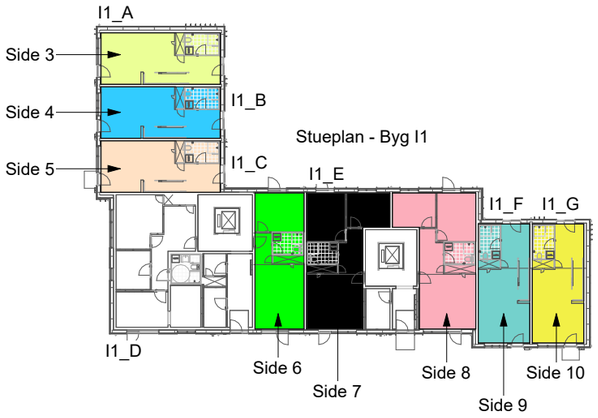

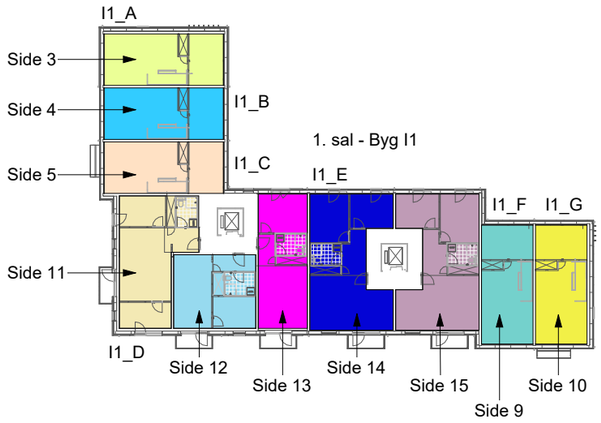

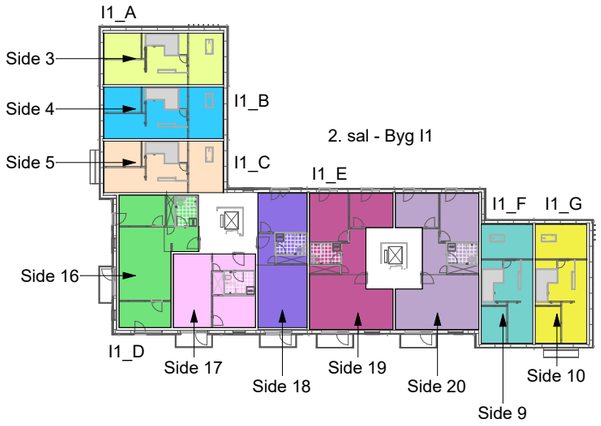



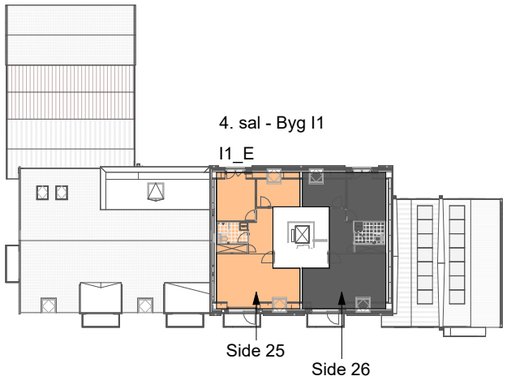

Oversigt, bygning I1:

Side 3:	Rækkehuse, Byg A, st. til 2.sal, 5V	Side 22:	Opgangsbolig, Byg D, 3.sal, 2V
Side 4:	Rækkehuse, Byg B, st. til 2.sal, 5V	Side 23:	Opgangsbolig, Byg E, 3.sal, 3V
Side 5:	Rækkehuse, Byg C, st. til 2.sal, 5V	Side 24:	Opgangsbolig, Byg E, 3.sal, 3V
Side 6:	Opgangsbolig, Byg D, st., 2V	Side 25:	Opgangsbolig, Byg E, 4.sal, 3V
Side 7:	Opgangsbolig, Byg E, st., 3V	Side 26:	Opgangsbolig, Byg E, 4.sal, 3V
Side 8:	Opgangsbolig, Byg E, st., 3V		
Side 9:	Rækkehuse, Byg F, st. til 2.sal, 5V		
Side 10:	Rækkehuse, Byg G, st. til 2.sal, 5V		
Side 11:	Opgangsbolig, Byg D, 1.sal, 3V		
Side 12:	Opgangsbolig, Byg D, 1.sal, 2V		
Side 13:	Opgangsbolig, Byg D 1.sal, 2V		
Side 14:	Opgangsbolig, Byg E, 1.sal, 3V		
Side 15:	Opgangsbolig, Byg E, 1.sal, 3V		
Side 16:	Opgangsbolig, Byg D, 2.sal, 3V		
Side 17:	Opgangsbolig, Byg D, 2.sal, 2V		
Side 18:	Opgangsbolig, Byg D, 2.sal, 2V		
Side 19:	Opgangsbolig, Byg E, 2.sal, 3V		
Side 20:	Opgangsbolig, Byg E, 2.sal, 3V		
Side 21:	Opgangsbolig, Byg D, 3.sal, 4V		

Projekt: Stejlepladsen


Tekst: Elinstallationer - Byg I1 - Oversigtsplan

Tegningsnr.: ISP2_K07_L2XX_H04_EXX_N930


Rev.:

Projektnr.: 1019198 | Dato: 2026-02-27 | Rev. Dato: | Mål: 1 : 500 | Side: I1-2


www.arteliagroup.dk | Fil:

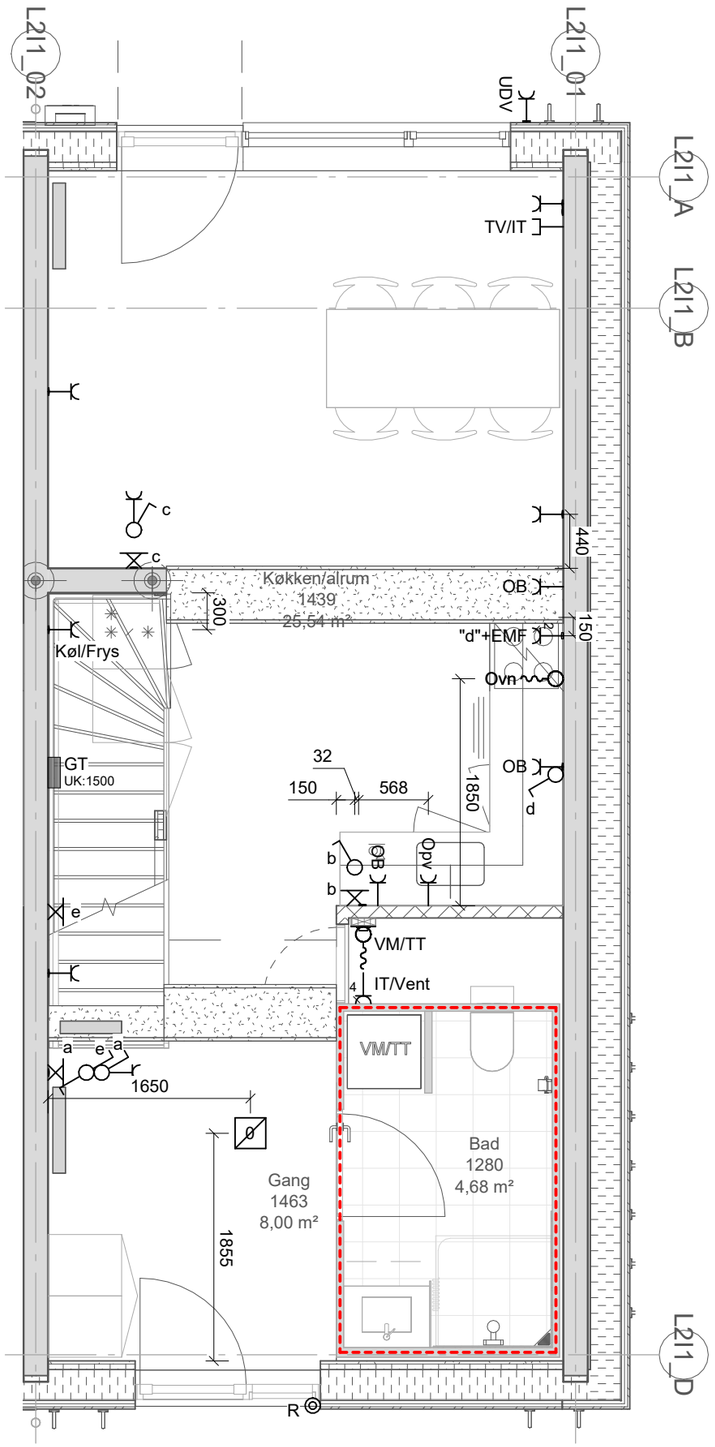

Stue

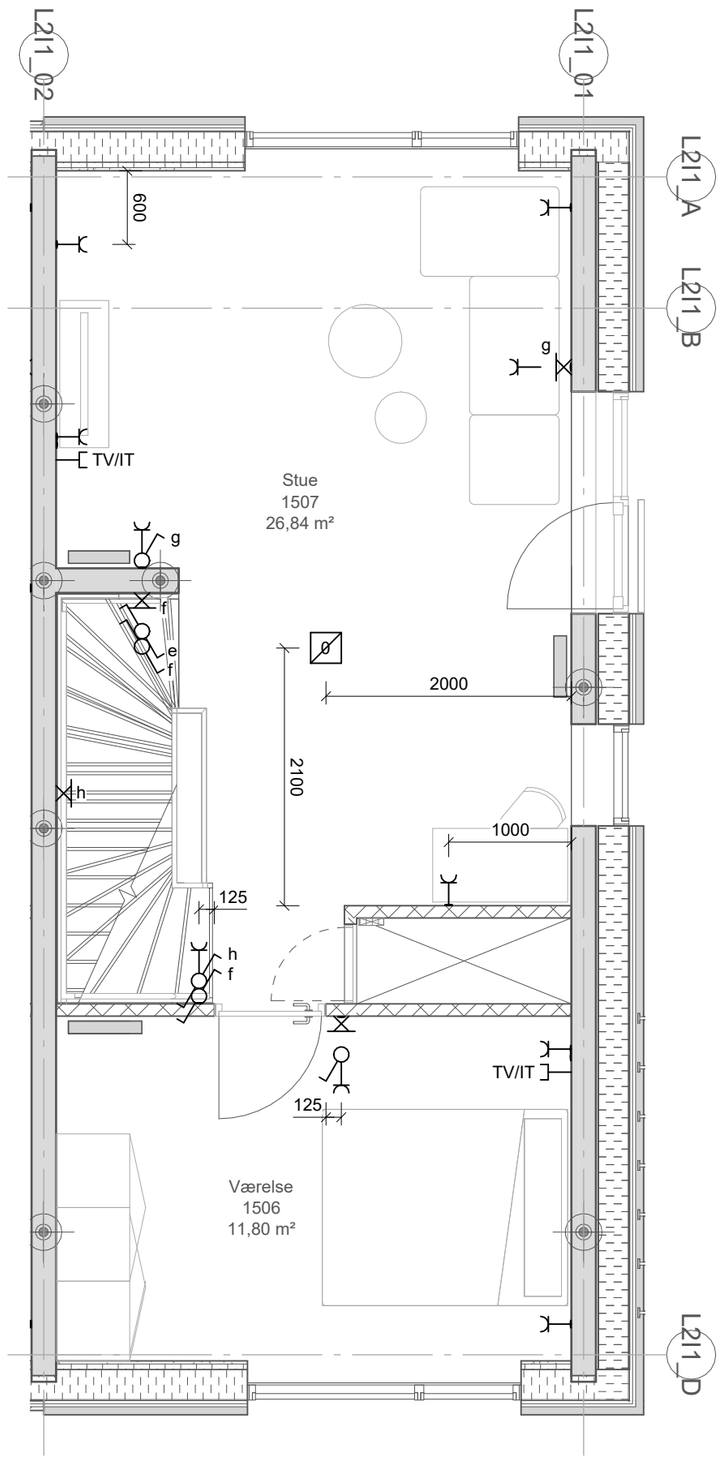

1. sal

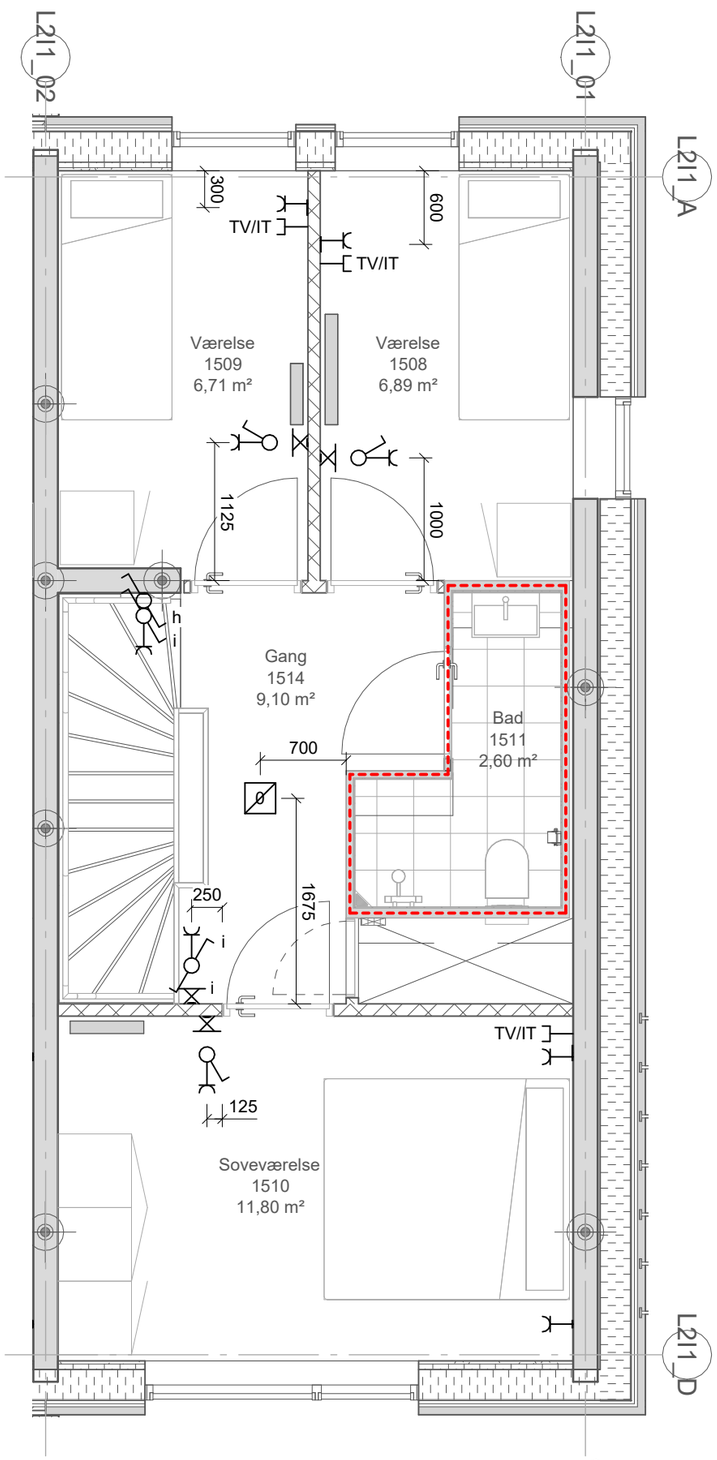

2. sal

Projekt: Stejlepladsen


Tekst: Elinstallationer -
Byg I1 - St. til 2. Sal, Byg A
RK_5V_T30 - Side I1-3

Tegningsnr.: ISP2_K07_L2XX_H04_EXX_N930


Rev.:

Projektnr.: 1019198 | Dato: 2026-02-27 | Rev. Dato: | Mål: 1 : 50 | Side: I1-3


www.arteliagroup.dk | Fil:

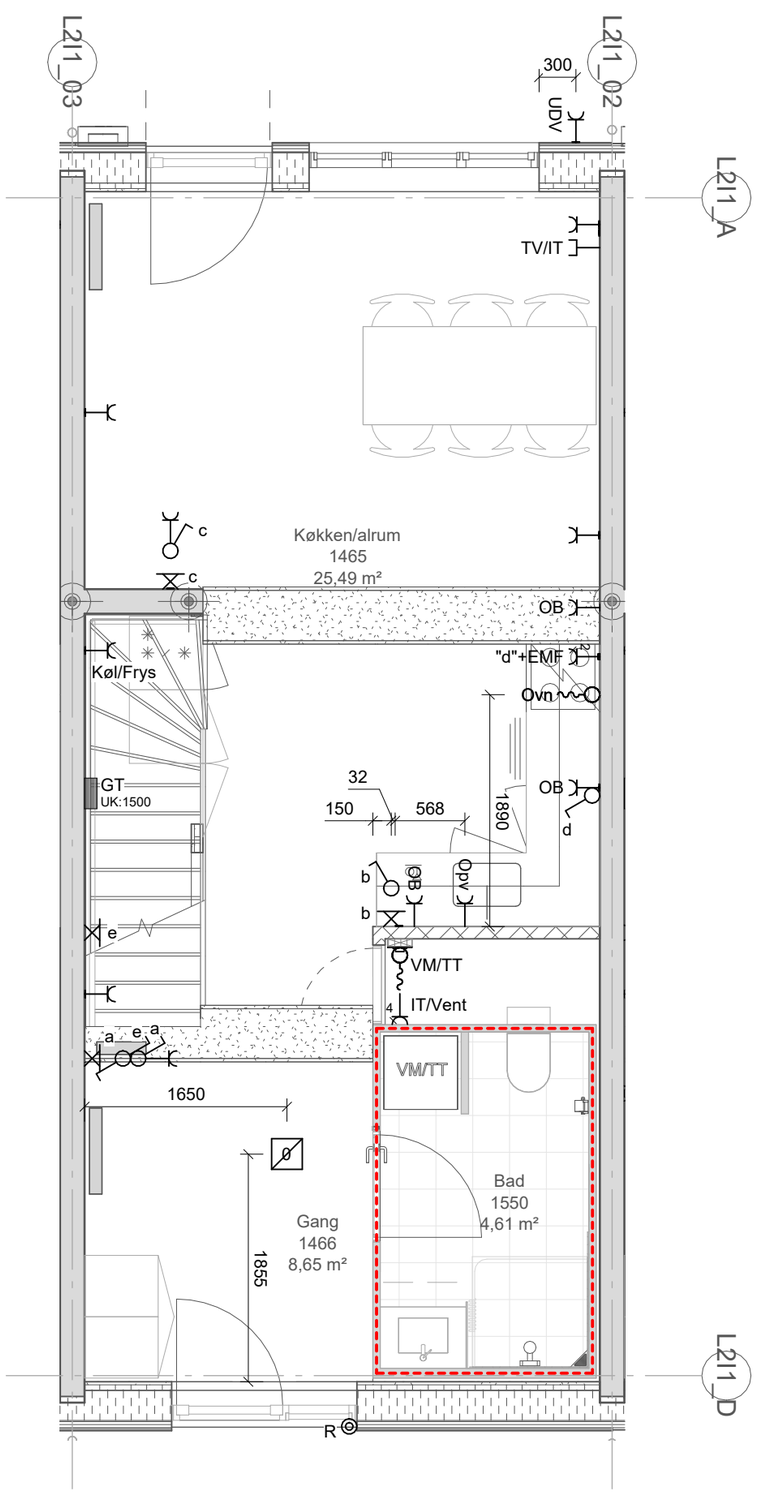

Stue

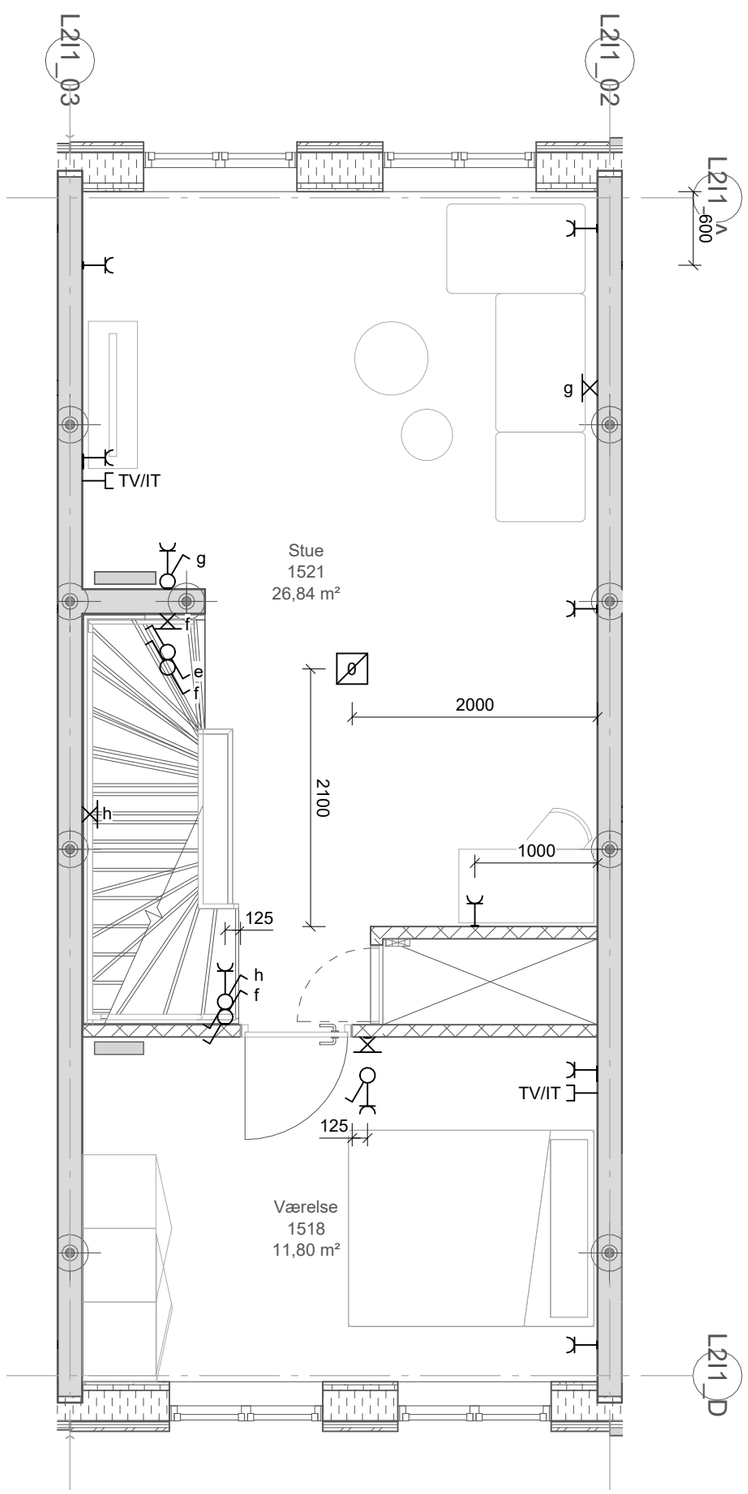

1. sal

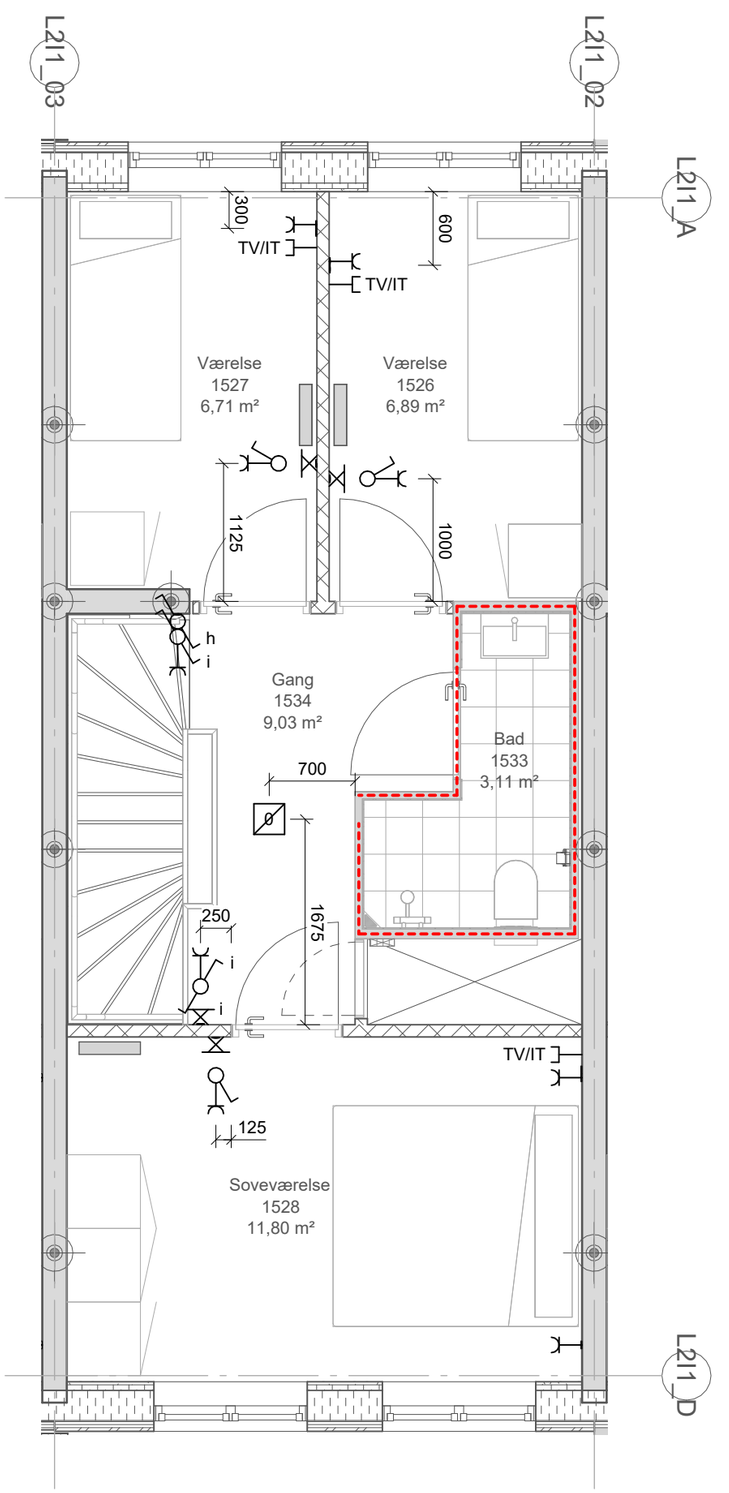

2. sal

Projekt: Stejlepladsen


Tekst: Elinstallationer -
Byg I1 - St. til 2. Sal, Byg B
RK_5V_T30 - Side I1-4

Tegningsnr.: ISP2_K07_L2XX_H04_EXX_N930


Rev.:

Projektnr.: 1019198 | Dato: 2026-02-27 | Rev. Dato: | Mål: 1 : 50 | Side: I1-4


www.arteliagroup.dk | Fil:

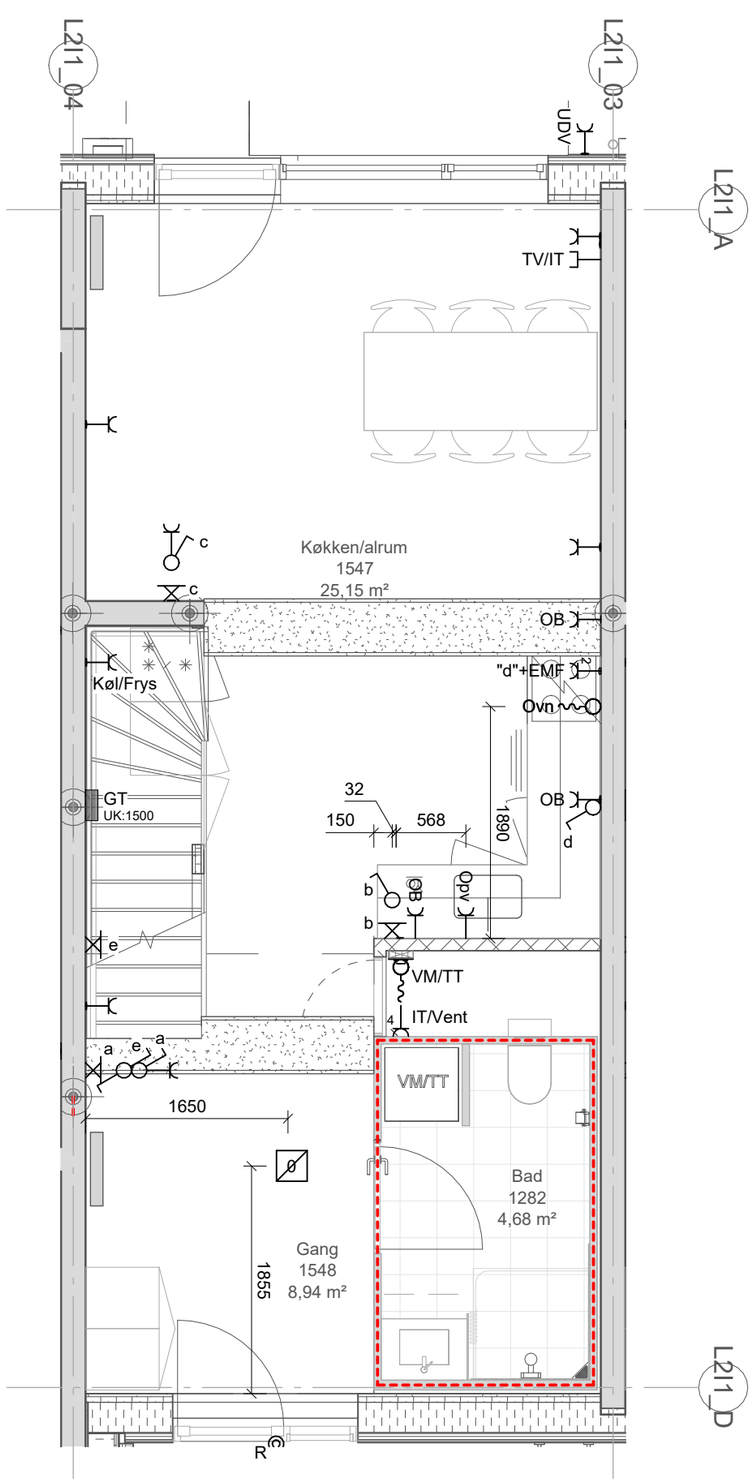

Stue

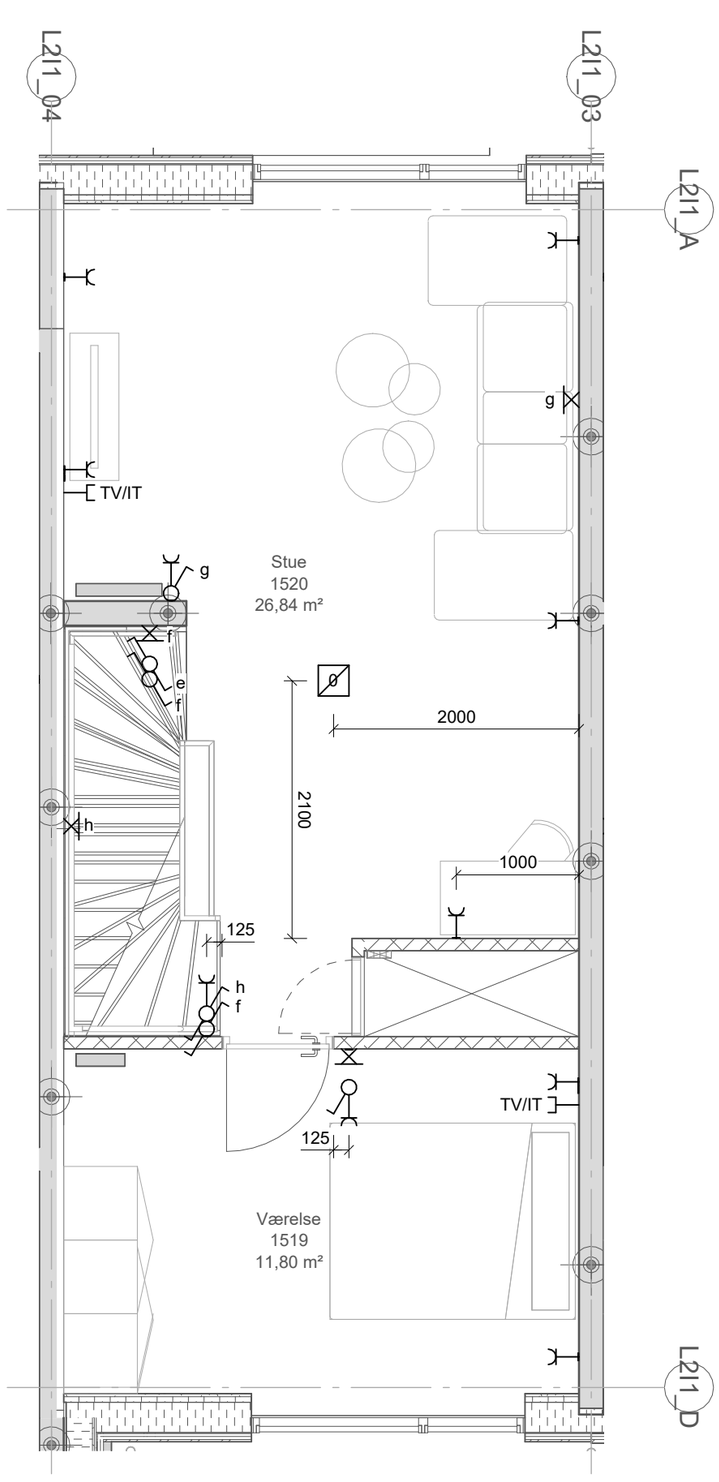

1. sal

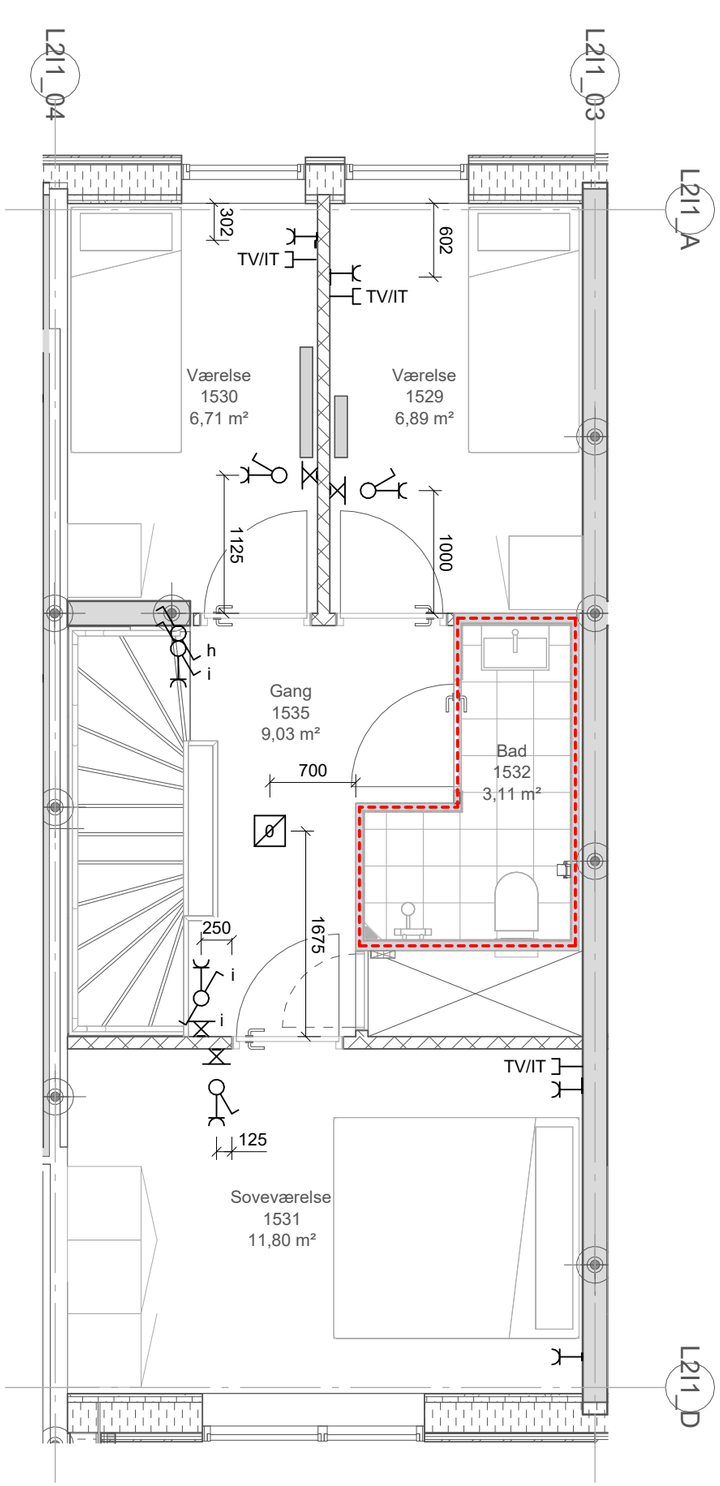

2. sal

Projekt: Stejlepladsen


Tekst: Elinstallationer -
Byg I1 - St. til 2. Sal, Byg C
RK_5V_T30 - Side I1-5

Tegningsnr.: ISP2_K07_L2XX_H04_EXX_N930

Rev.:

Projektnr.: 1019198 | Dato: 2026-02-27 | Rev. Dato: | Mål: 1 : 50 | Side: I1-5

www.arteliagroup.dk | Fil:

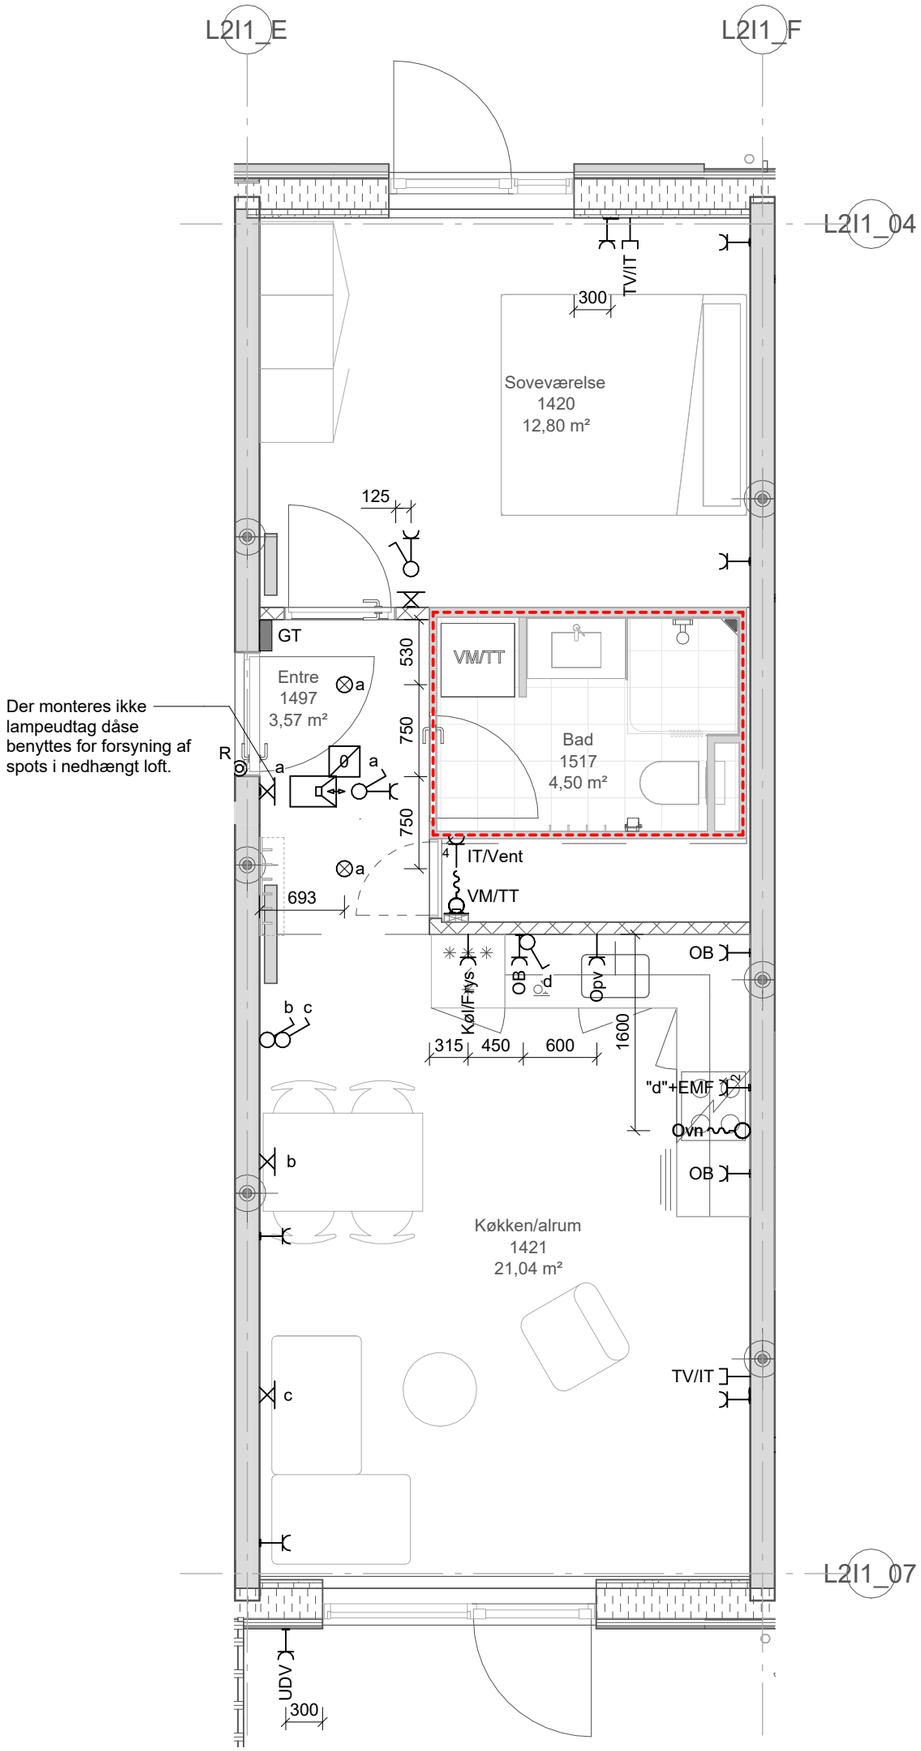

Projekt: Stejlepladsen


Tekst: Elinstallationer -
Byg I1 - Stueplan, Byg D
OPG_2V_T31_ST - Side I1-6

Tegningsnr.: ISP2_K07_L2XX_H04_EXX_N930


Rev.:

Projektnr.: 1019198 | Dato: 2026-02-27 | Rev. Dato: | Mål: 1 : 50 | Side: I1-6

www.arteliagroup.dk | Fil:

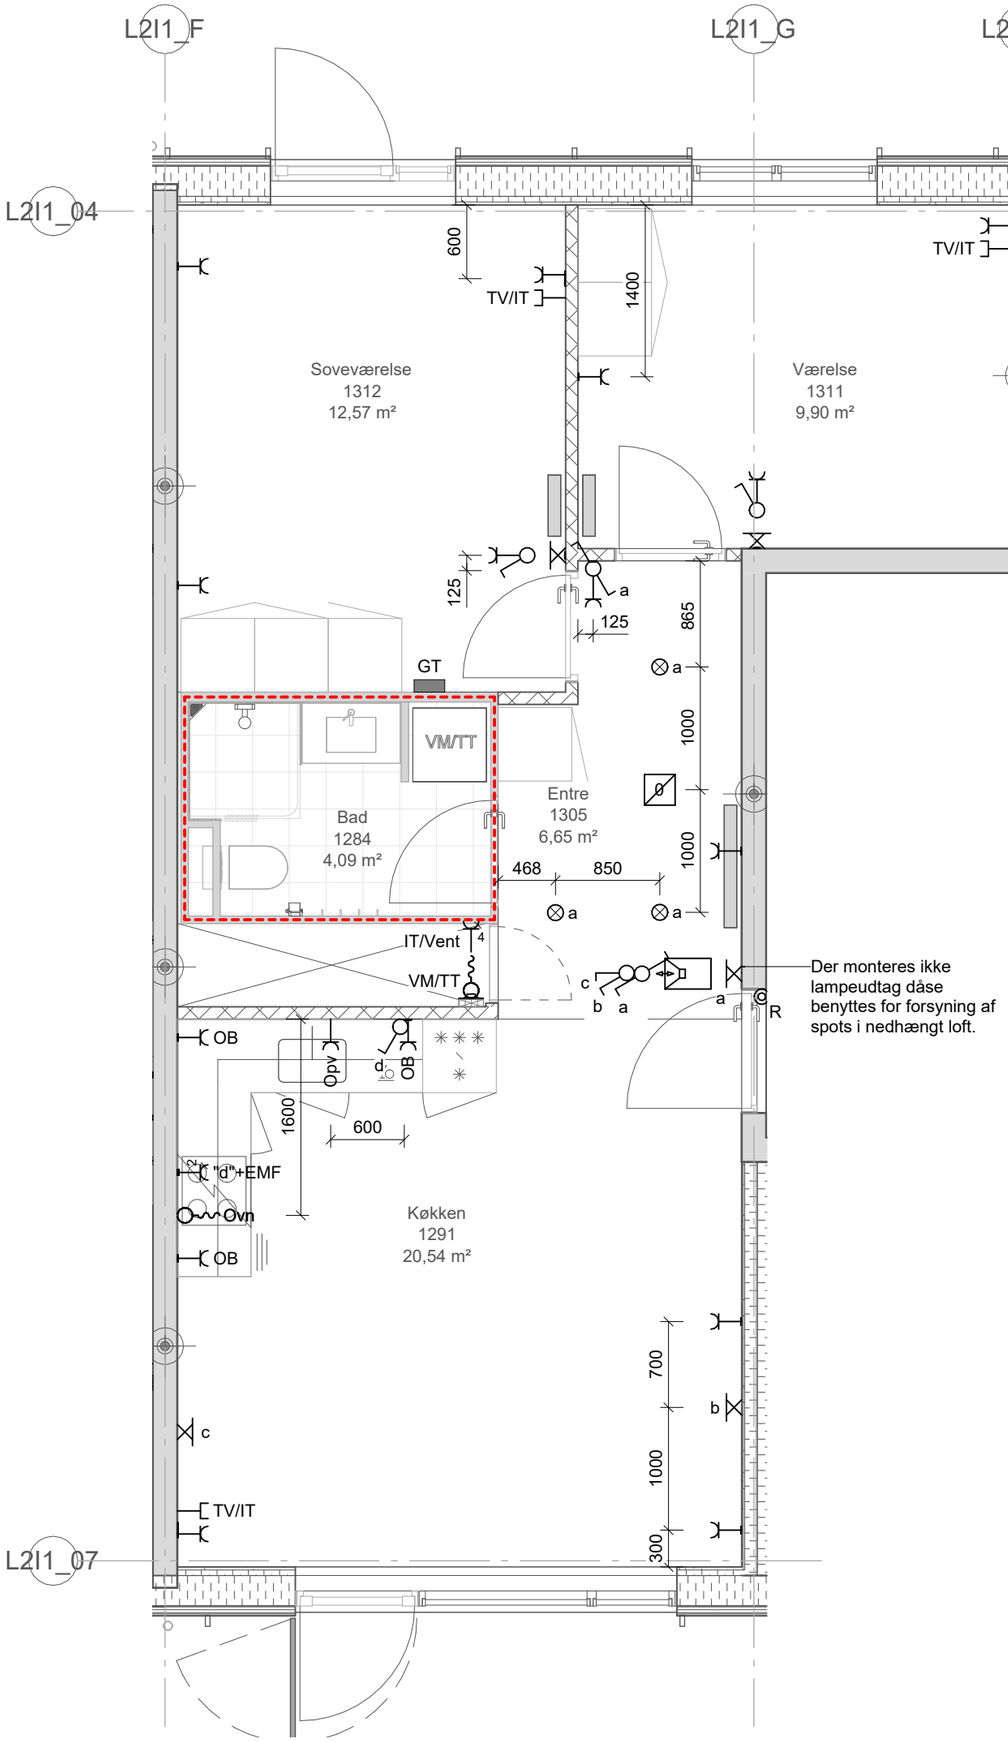

Projekt:	Stejlepladsen				
Tekst:	Elinstallationer - Byg I1 - Stueplan, Byg E OPG_3V_T32_ST - Side I1-7			Tegningsnr.:	Rev.:
				ISP2_K07_L2XX_H04_EXX_N930	
Projektnr.: 1019198	Dato: 2026-02-27	Rev. Dato:		Mål: 1 : 50	Side: I1-7
www.arteliagroup.dk	Fil:				

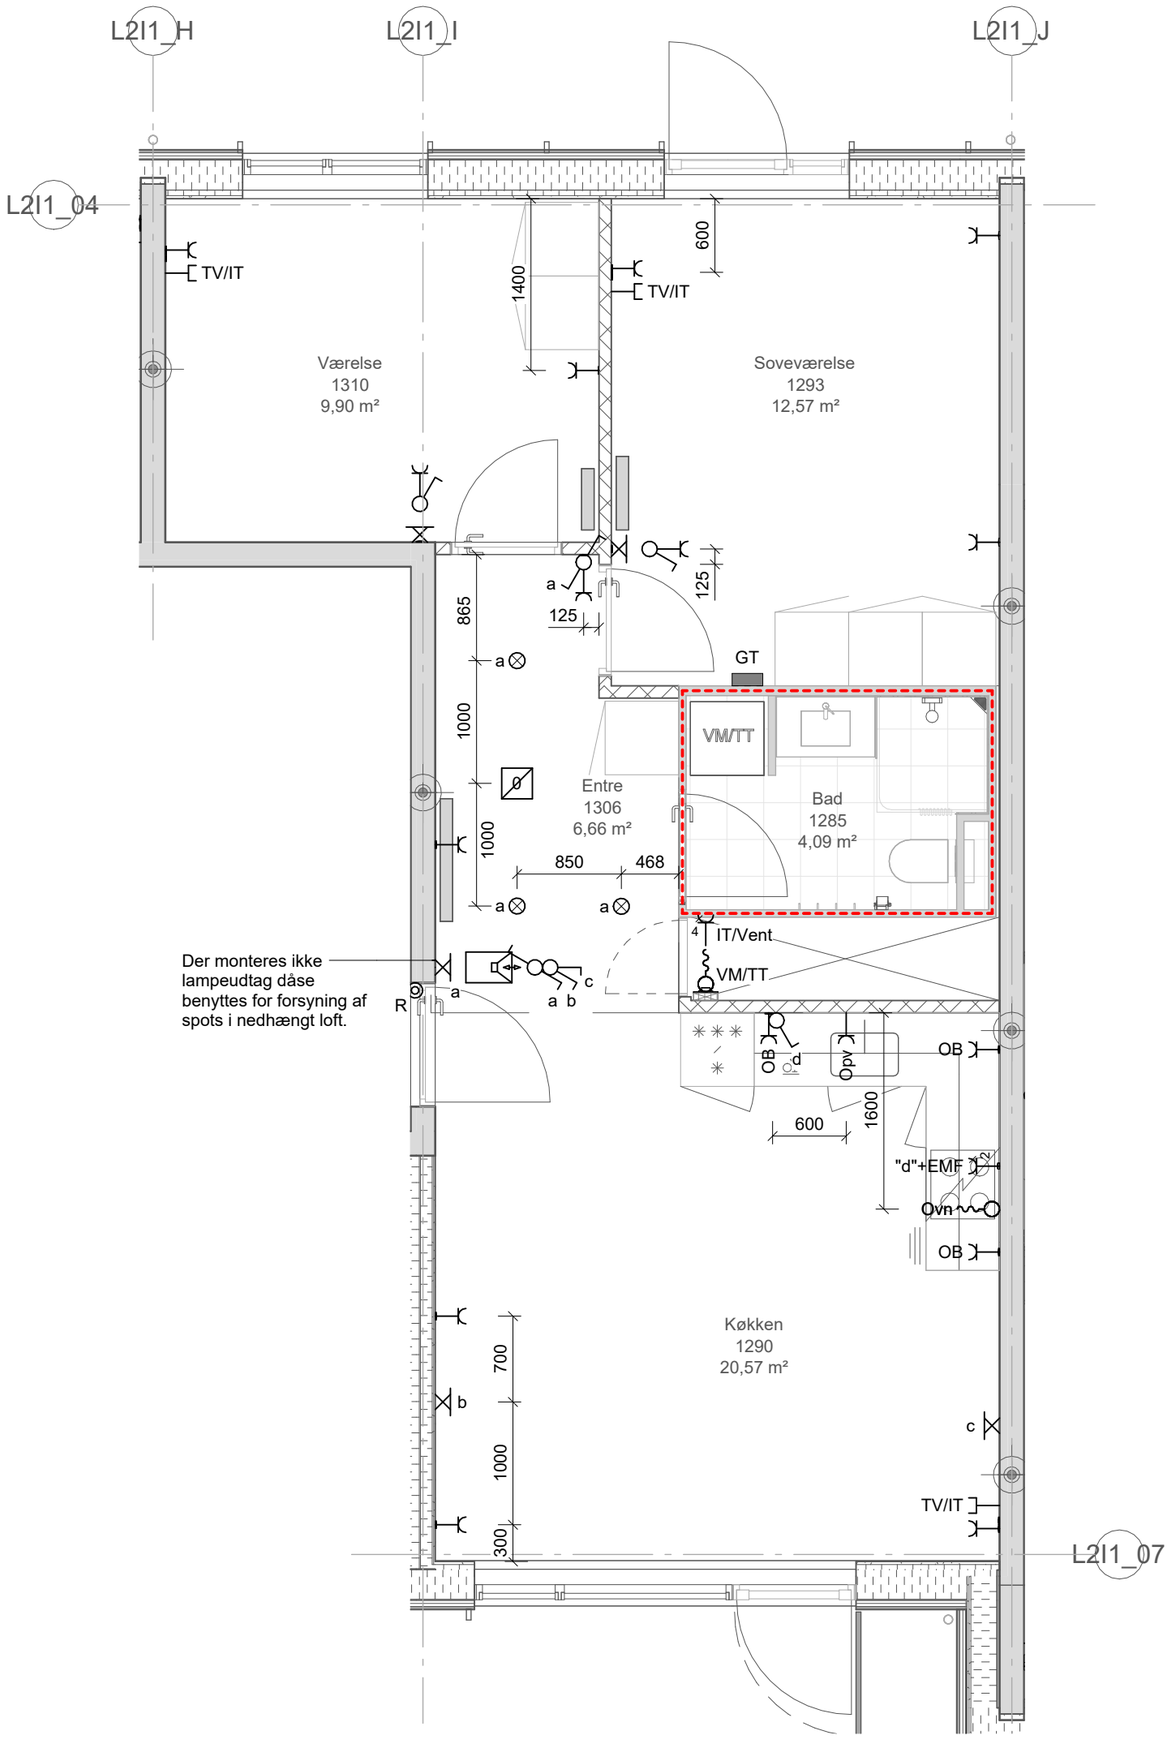

Projekt: Stejlepladsen


Tekst: Elinstallationer -
Byg I1 - Stueplan, Byg E
OPG_3V_T32_ST_S - Side I1-8

Tegningsnr.: ISP2_K07_L2XX_H04_EXX_N930


Rev.:

Projektnr.: 1019198 | Dato: 2026-02-27 | Rev. Dato: | Mål: 1 : 50 | Side: I1-8


www.arteliagroup.dk | Fil:

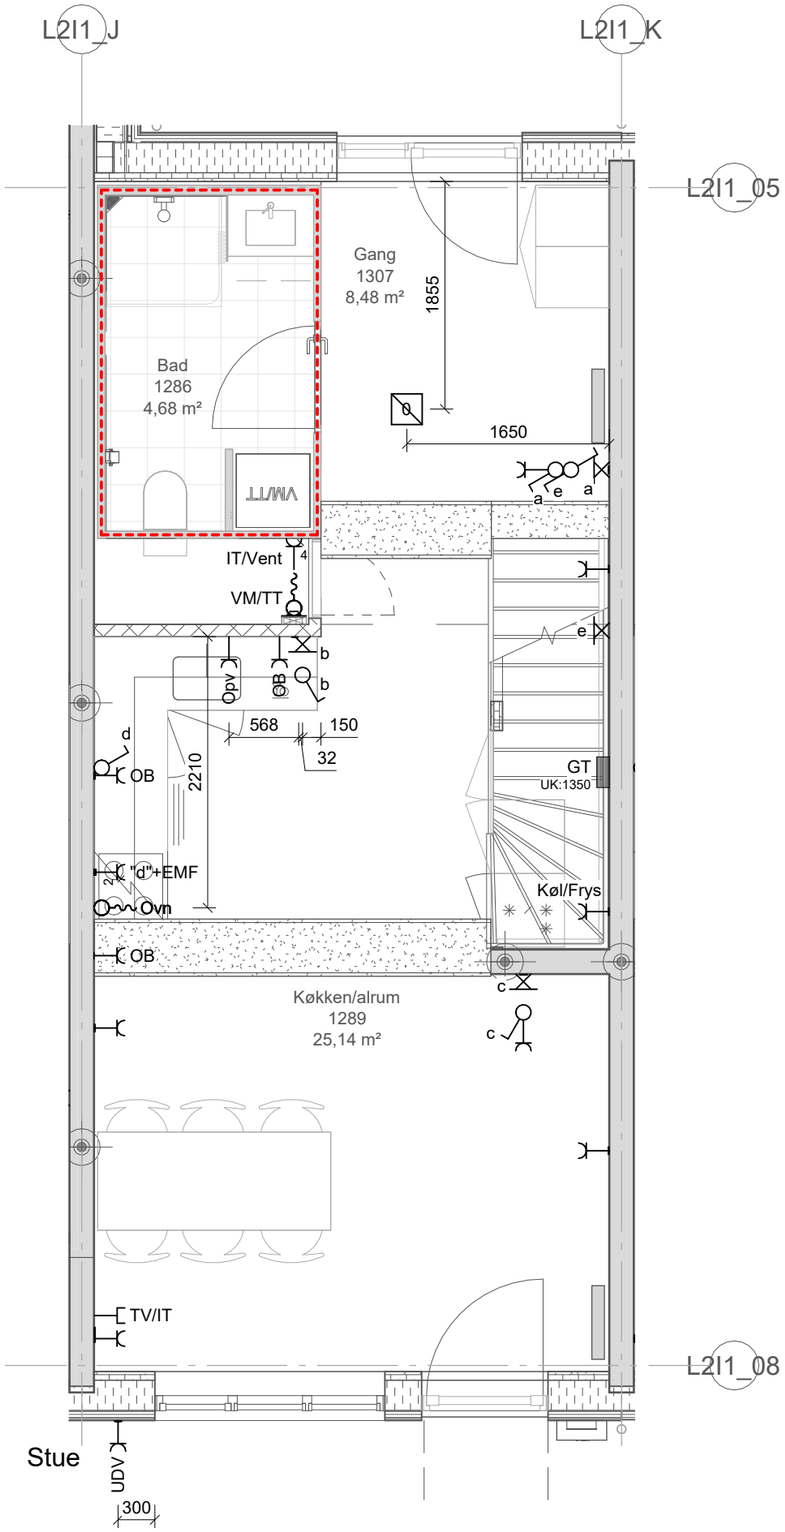

1. sal

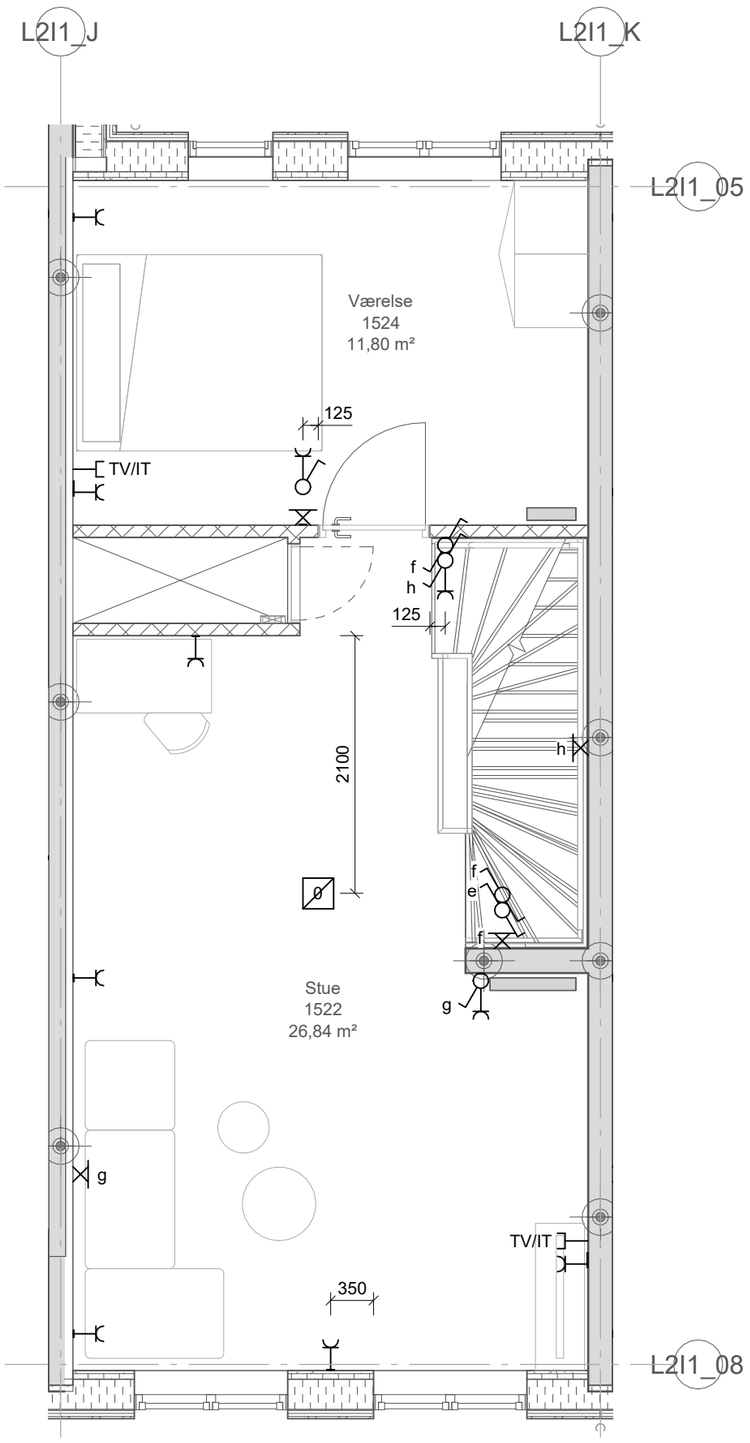

2. sal

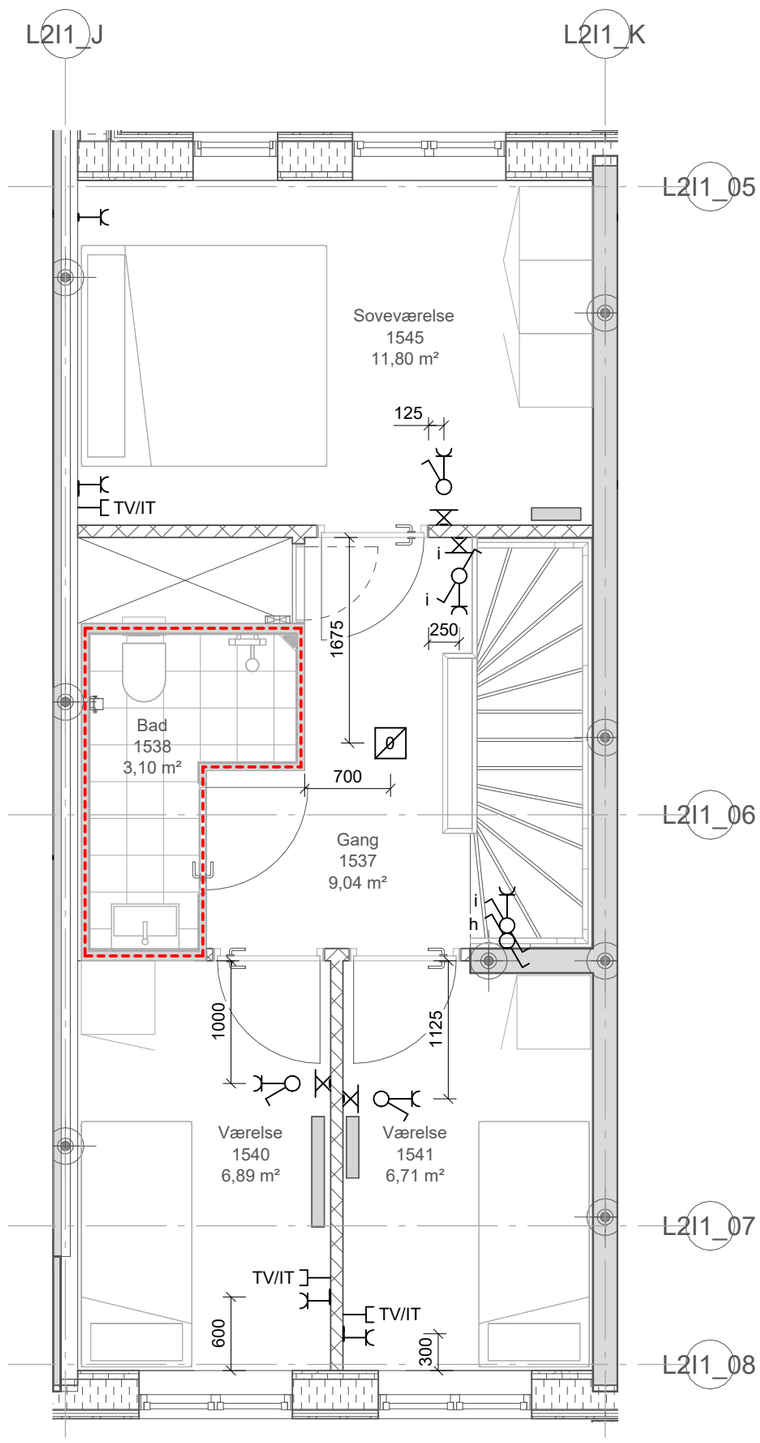

Projekt: Stejlepladsen

ARTELIA


Tekst: Elinstallationer -
Byg I1 - ST. til 2. Sal, Byg F
RK_5V_T30 - Side I1-9

Tegningsnr.: ISP2_K07_L2XX_H04_EXX_N930


Rev.:

Projektnr.: 1019198 | Dato: 2026-02-27 | Rev. Dato: | Mål: 1 : 50 | Side: I1-9


www.arteliagroup.dk | Fil:

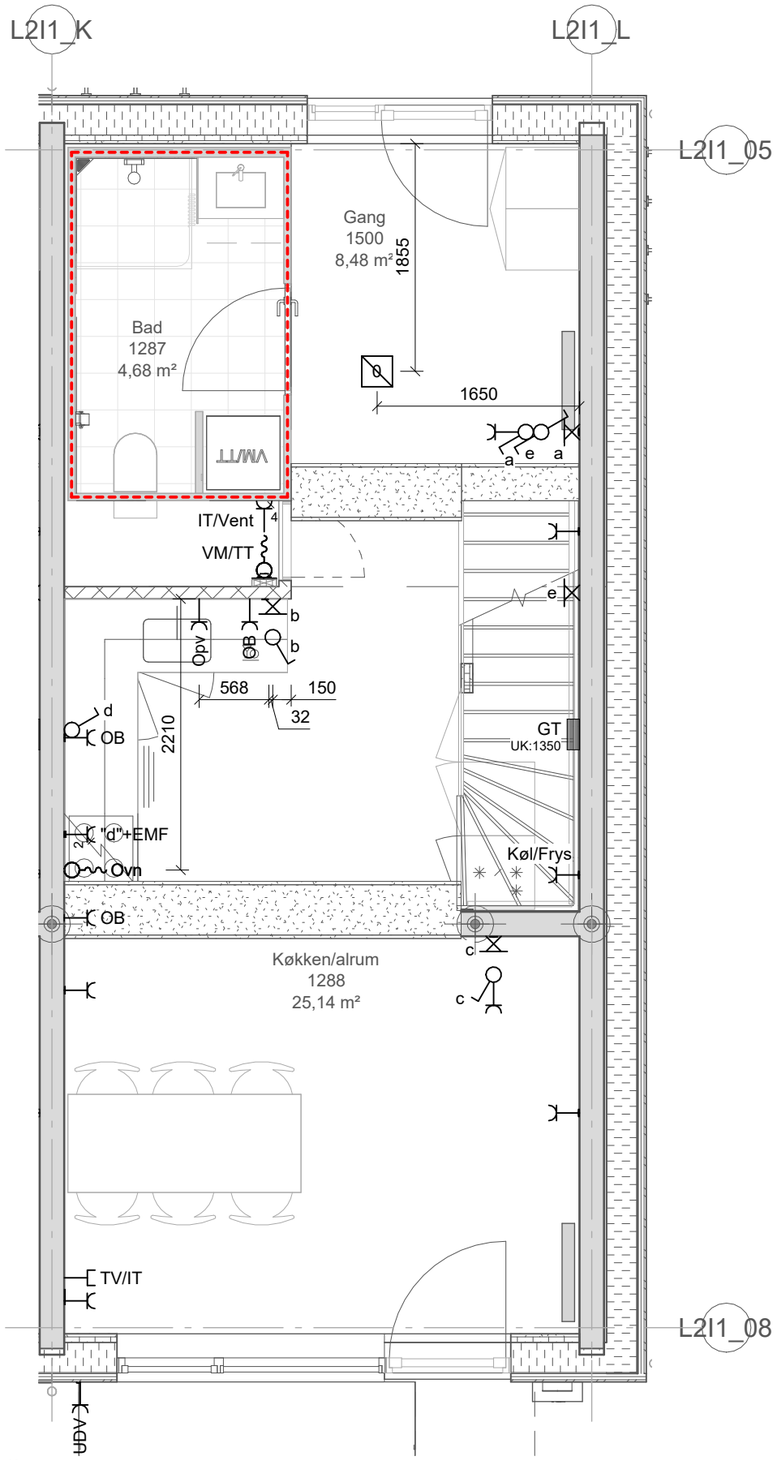

Stue

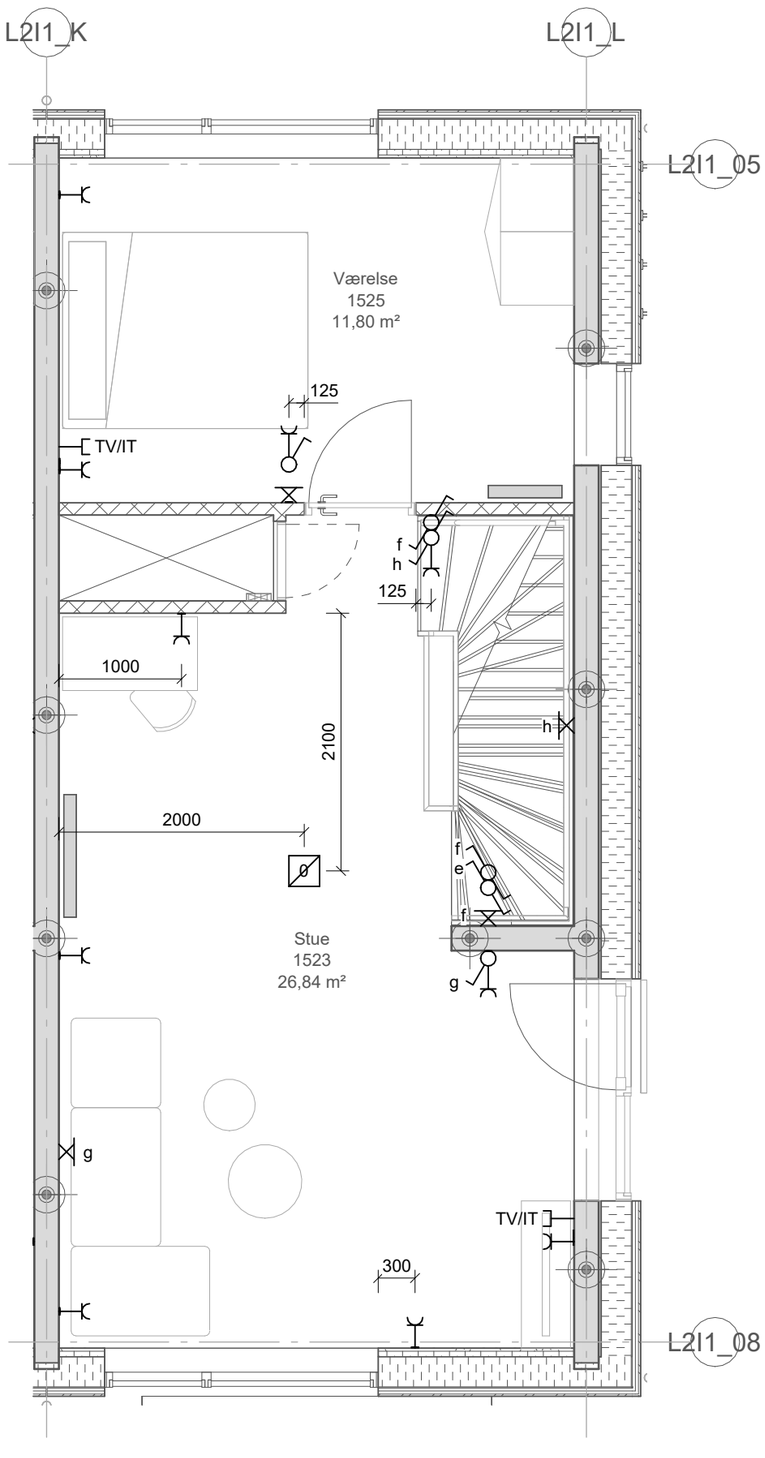

1. sal

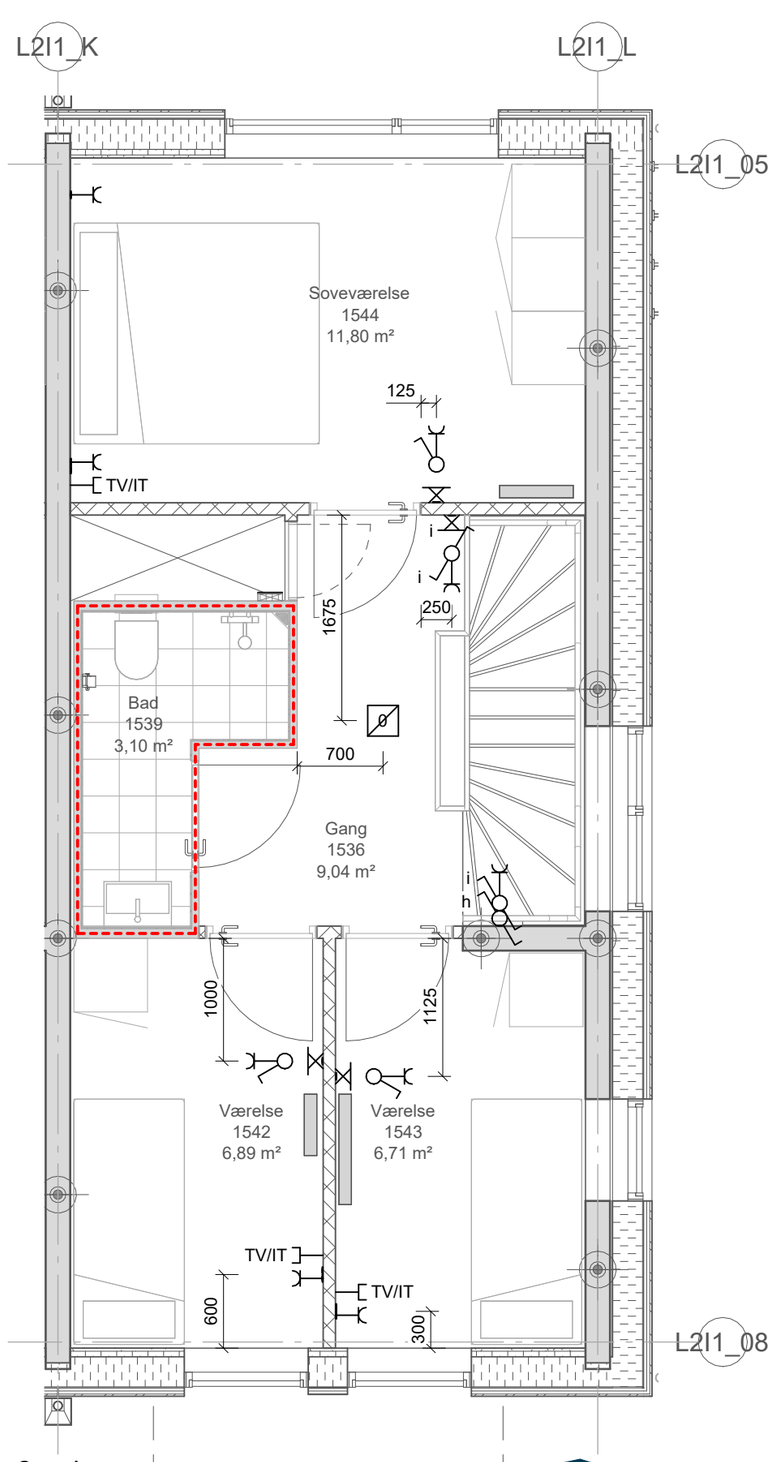

2. sal

Projekt: Stejlepladsen


Tekst: Elinstallationer -
Byg I1 - ST. til 2. Sal, Byg G
RK_5V_T30 - Side I1-10

Tegningsnr.: ISP2_K07_L2XX_H04_EXX_N930

Rev.:

Projektnr.: 1019198 | Dato: 2026-02-27 | Rev. Dato: | Mål: 1 : 50 | Side: I1-10

www.arteliagroup.dk | Fil:

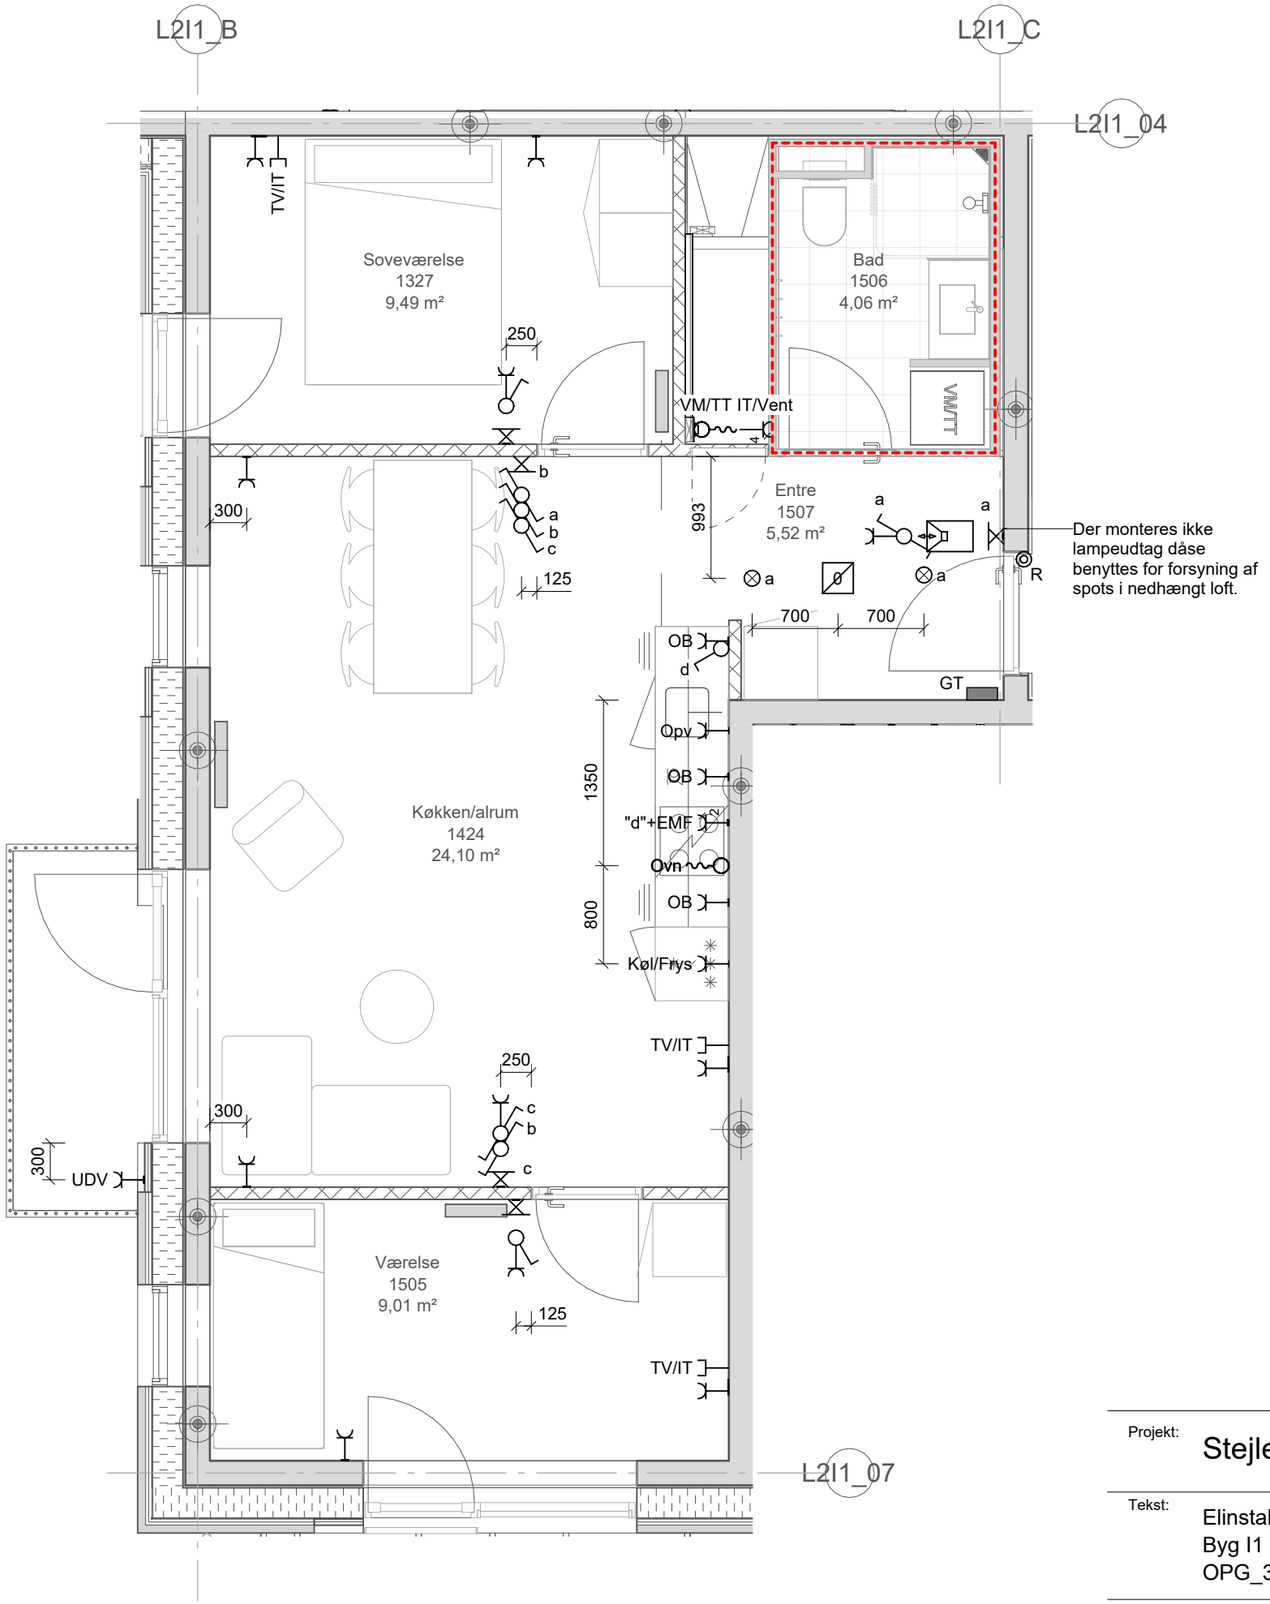

Projekt: Stejlepladsen


Tekst: Elinstallationer -
Byg I1 - 1. Sal, Byg D
OPG_3V_T33 - Side I1-11

Tegningsnr.: ISP2_K07_L2XX_H04_EXX_N930


Rev.:

Projektnr.: 1019198 | Dato: 2026-02-27 | Rev. Dato: | Mål: 1 : 50 | Side: I1-11

www.arteliagroup.dk | Fil:

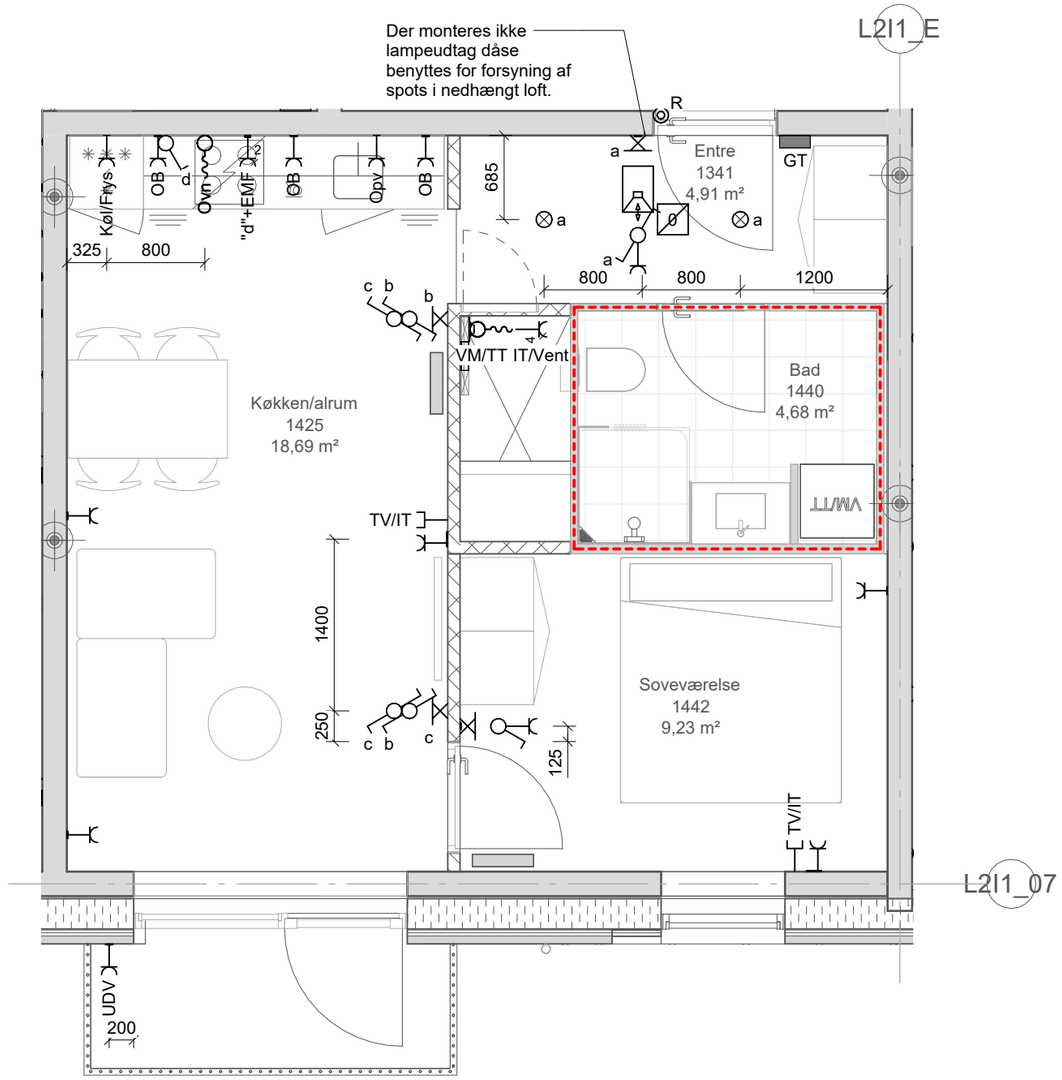

Projekt:	Stejlepladsen				
Tekst:	Elinstallationer - Byg I1 - 1. Sal, Byg D OPG_2V_T30 - Side I1-12			Tegningsnr.:	Rev.:
				ISP2_K07_L2XX_H04_EXX_N930	
Projektnr.: 1019198	Dato: 2026-02-27	Rev. Dato:		Mål: 1 : 50	Side: I1-12
www.arteliagroup.dk	Fil:				

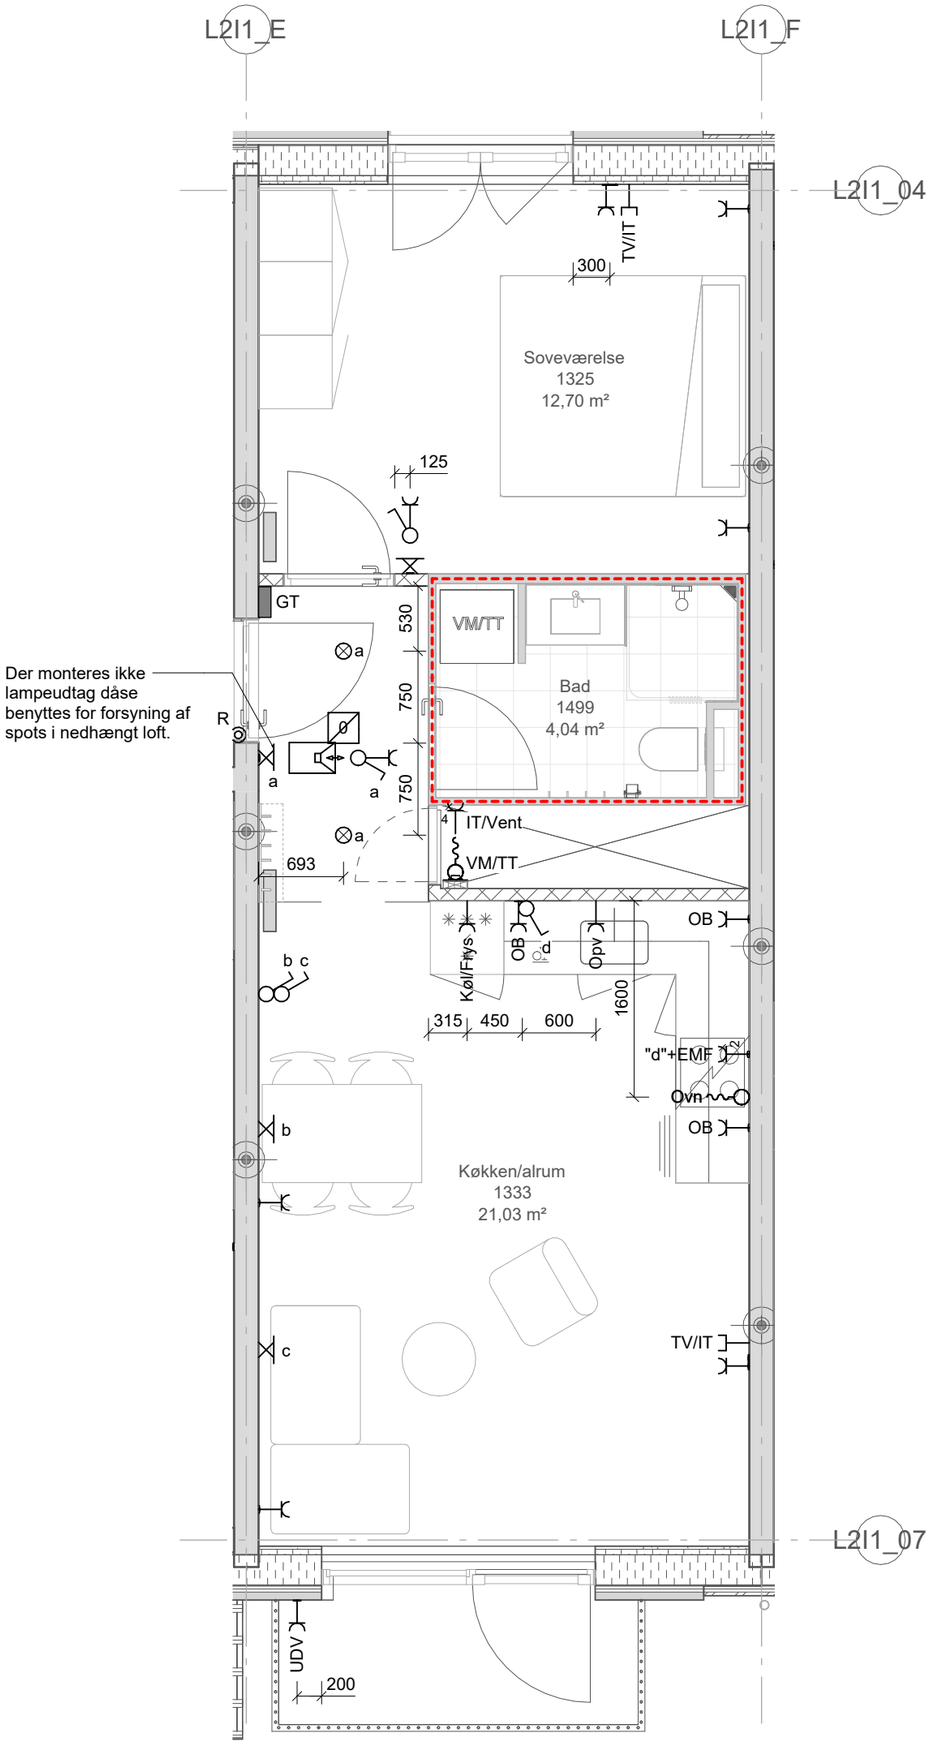

Projekt: Stejlepladsen

ARTELIA


Tekst: Elinstallationer -
Byg I1 - 1. Sal, Byg D
OPG_2V_T31 - Side I1-13

Tegningsnr.: ISP2_K07_L2XX_H04_EXX_N930

Rev.:

Projektnr.: 1019198 | Dato: 2026-02-27 | Rev. Dato: | Mål: 1 : 50 | Side: I1-13

www.arteliagroup.dk | Fil:

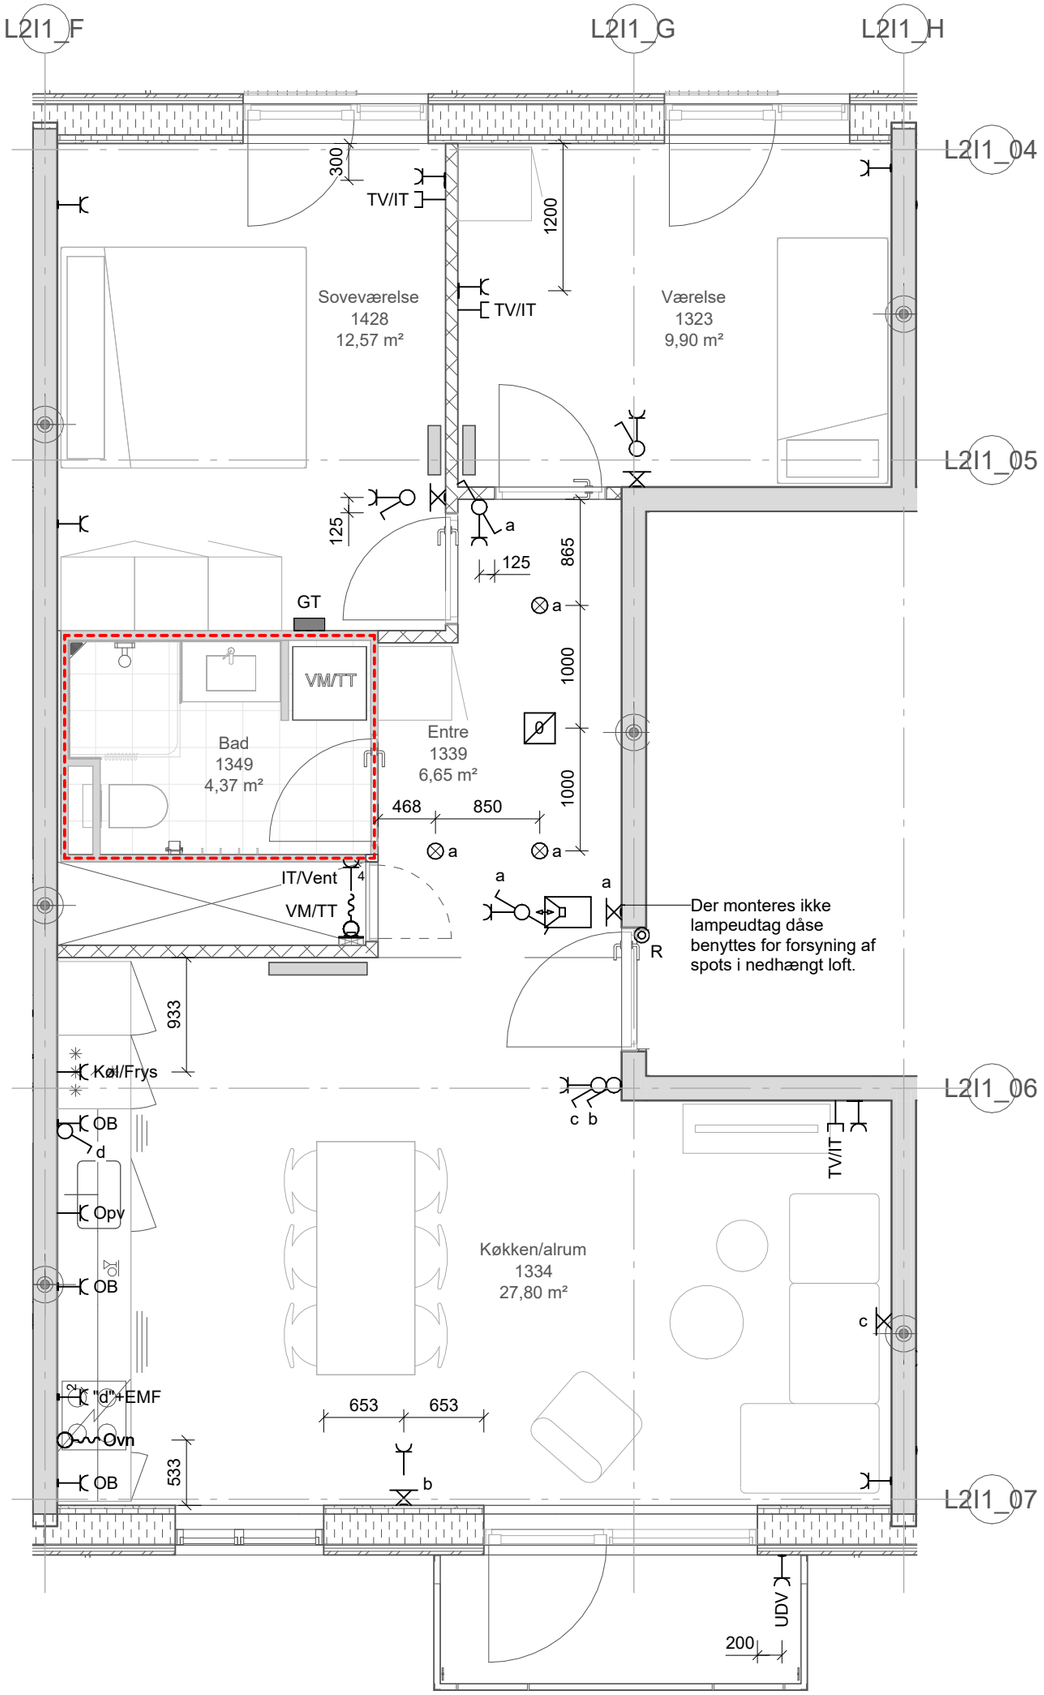

Projekt: Stejlepladsen


Tekst: Elinstallationer -
Byg I1 - 1. Sal, Byg E
OPG_3V_T30 - Side I1-14

Tegningsnr.: ISP2_K07_L2XX_H04_EXX_N930

Rev.:

Projektnr.: 1019198 | Dato: 2026-02-27 | Rev. Dato: | Mål: 1 : 50 | Side: I1-14

www.arteliagroup.dk | Fil:

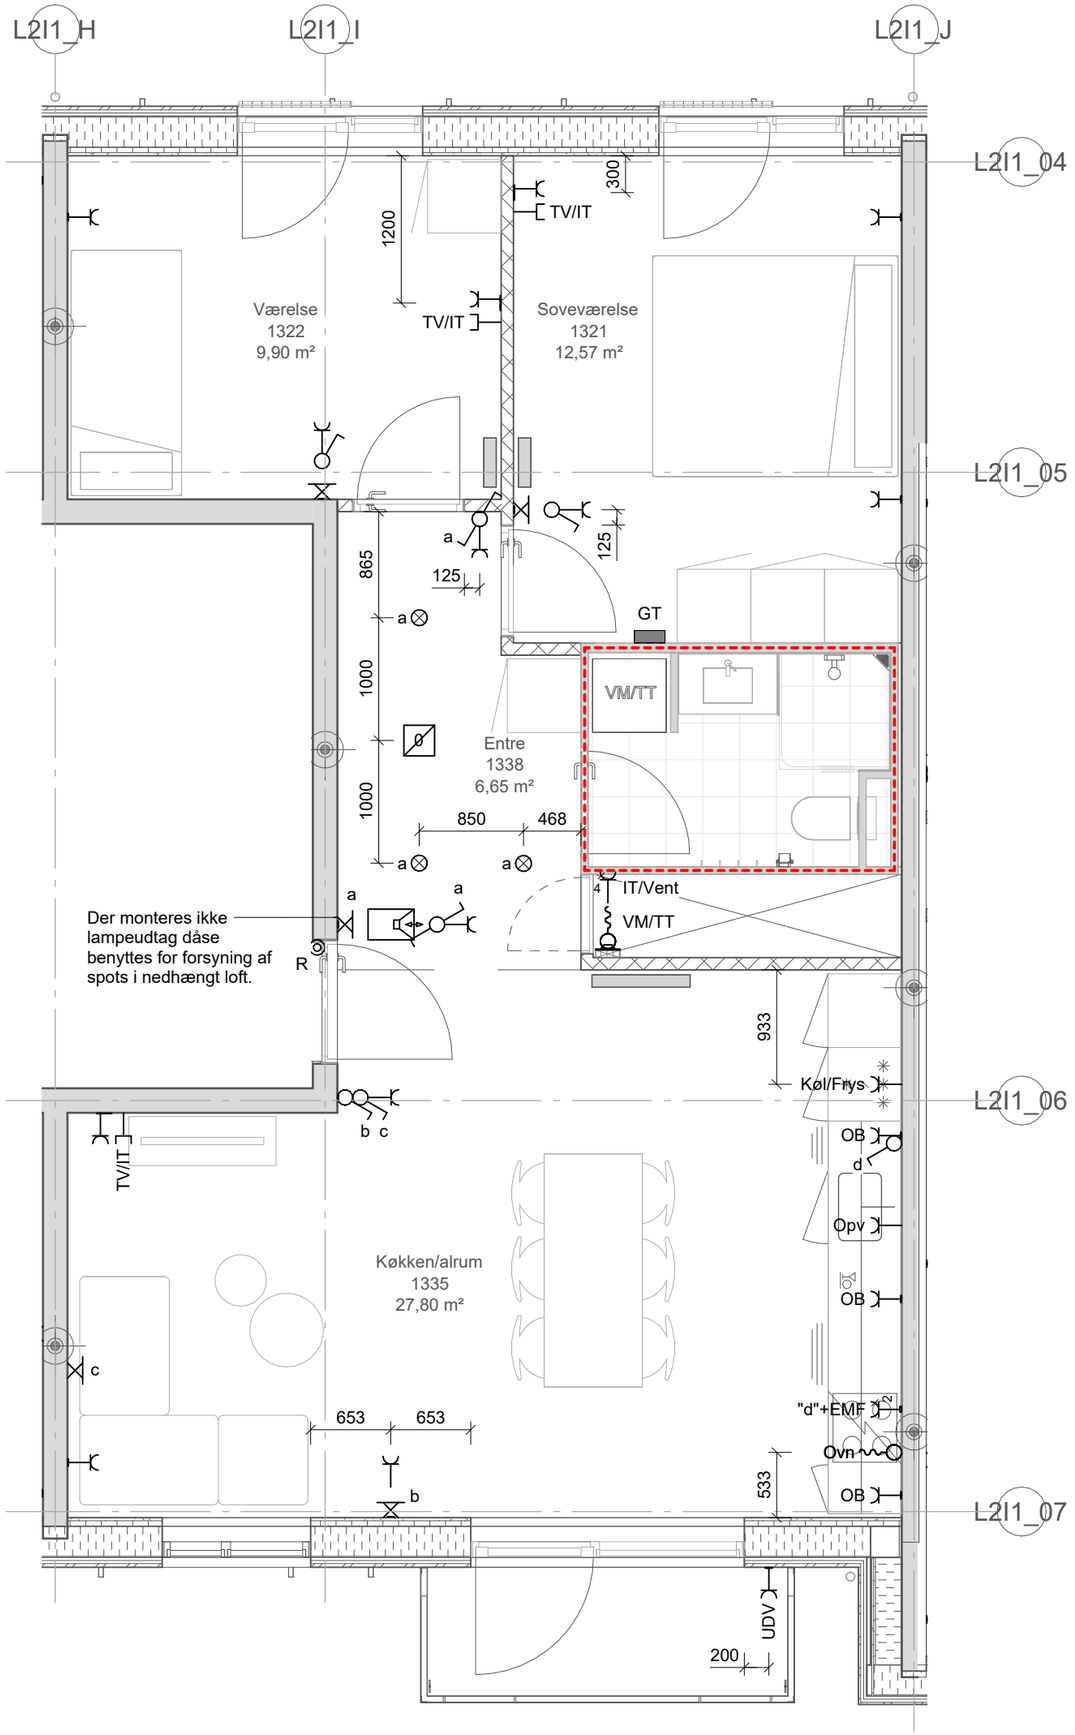

Projekt: Stejlepladsen


Tekst: Elinstallationer -
Byg I1 - 1. Sal, Byg E
OPG_3V_T30_S - Side I1-15

Tegningsnr.: ISP2_K07_L2XX_H04_EXX_N930

Rev.:

Projektnr.: 1019198 | Dato: 2026-02-27 | Rev. Dato: | Mål: 1 : 50 | Side: I1-15

www.arteliagroup.dk | Fil:

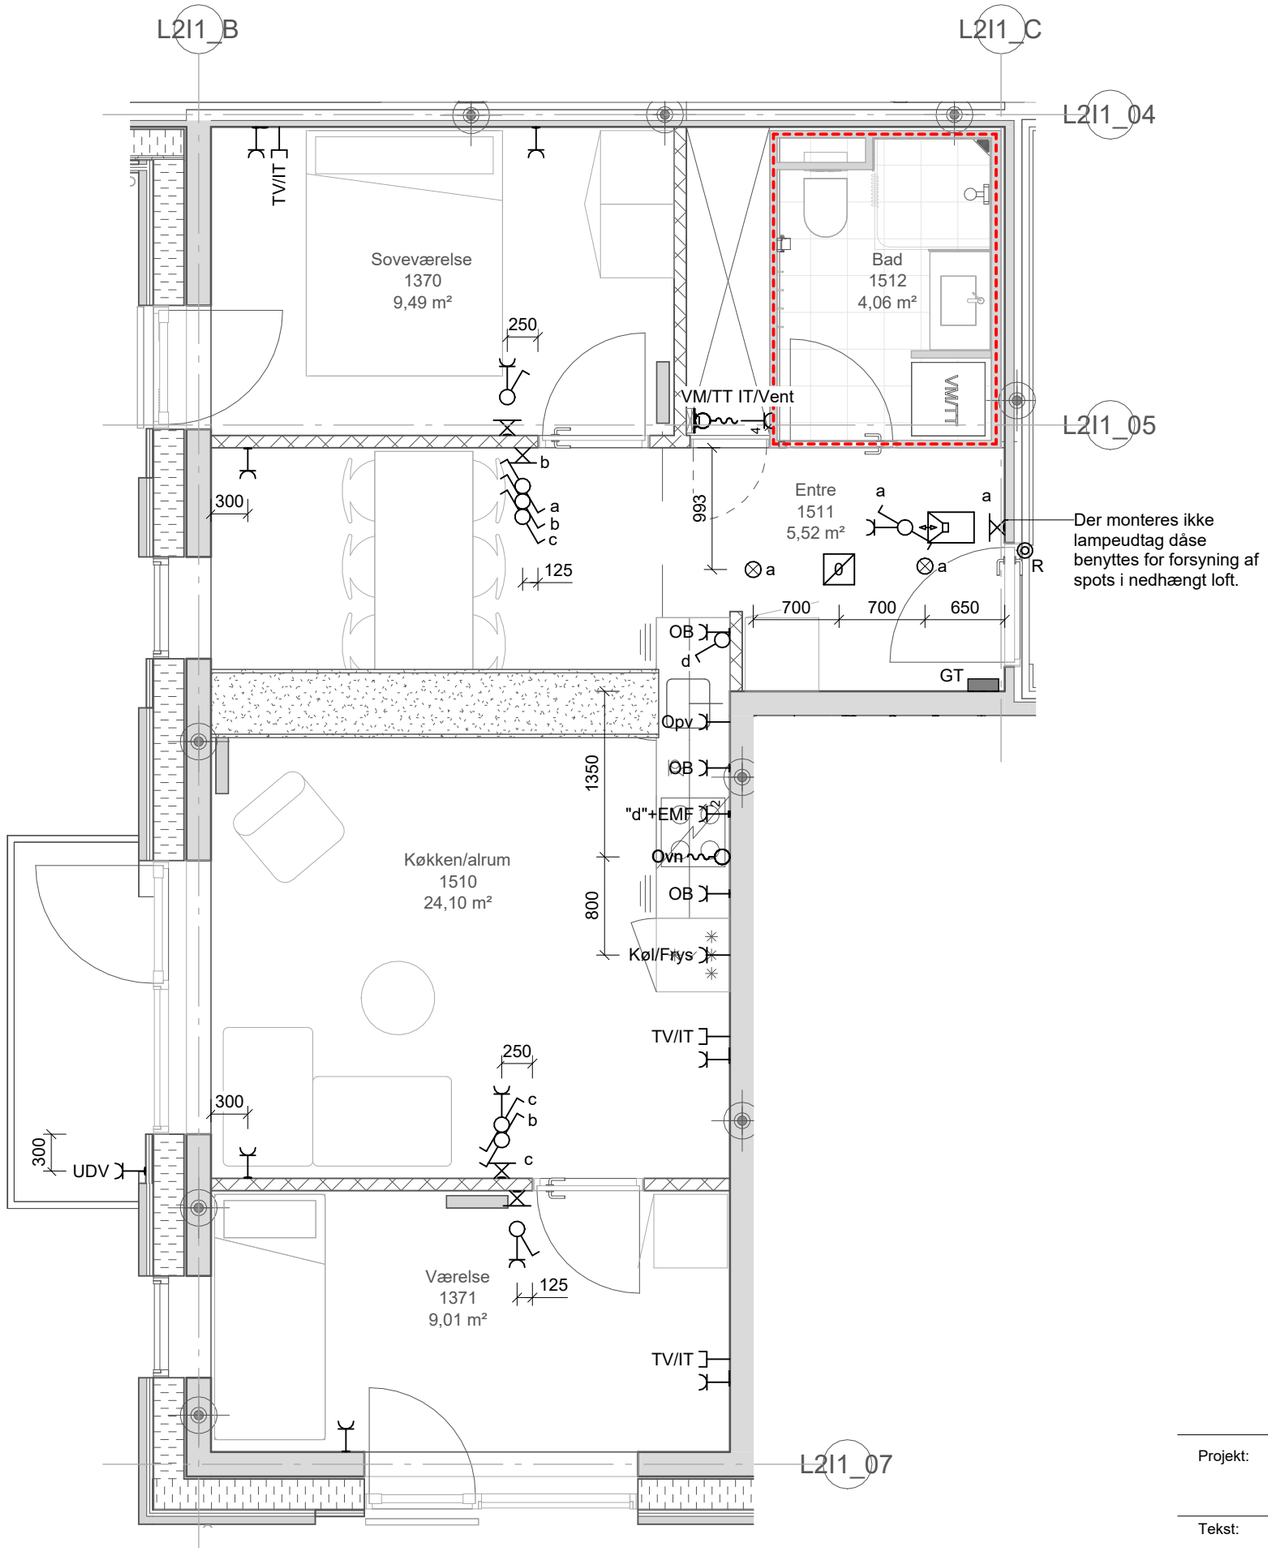

Projekt: Stejlepladsen


Tekst: Elinstallationer -
Byg I1 - 2. Sal, Byg D
OPG_3V_T33 - Side I1-16

Tegningsnr.: ISP2_K07_L2XX_H04_EXX_N930


Rev.:

Projektnr.: 1019198 | Dato: 2026-02-27 | Rev. Dato: | Mål: 1 : 50 | Side: I1-16

www.arteliagroup.dk | Fil:

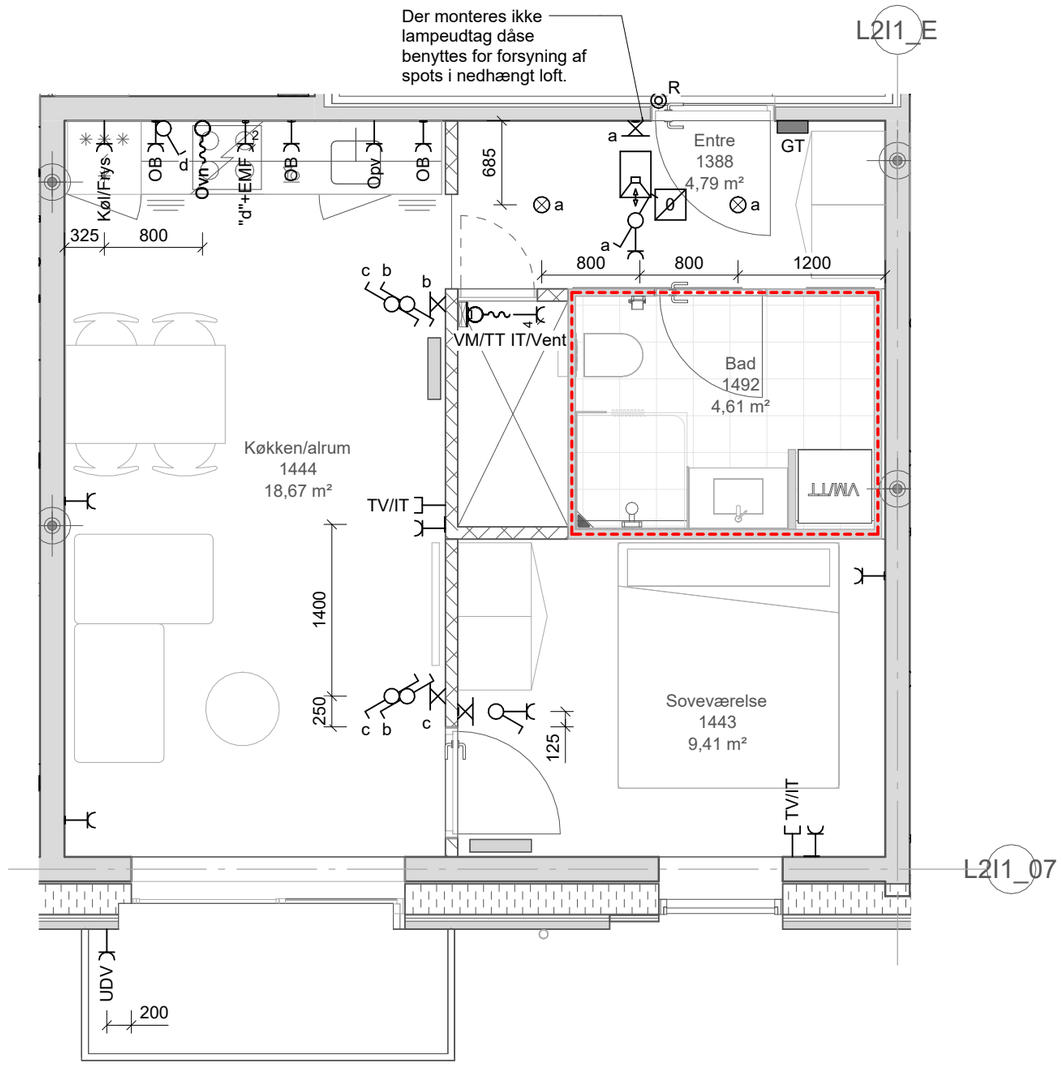

Projekt:	Stejlepladsen				
Tekst:	Elinstallationer - Byg I1 - 2. Sal, Byg D OPG_2V_T30 - Side I1-17			Tegningsnr.:	Rev.:
			ISP2_K07_L2XX_H04_EXX_N930		
Projektnr.: 1019198	Dato: 2026-02-27	Rev. Dato:		Mål: 1 : 50	Side: I1-17
www.arteliagroup.dk	Fil:				

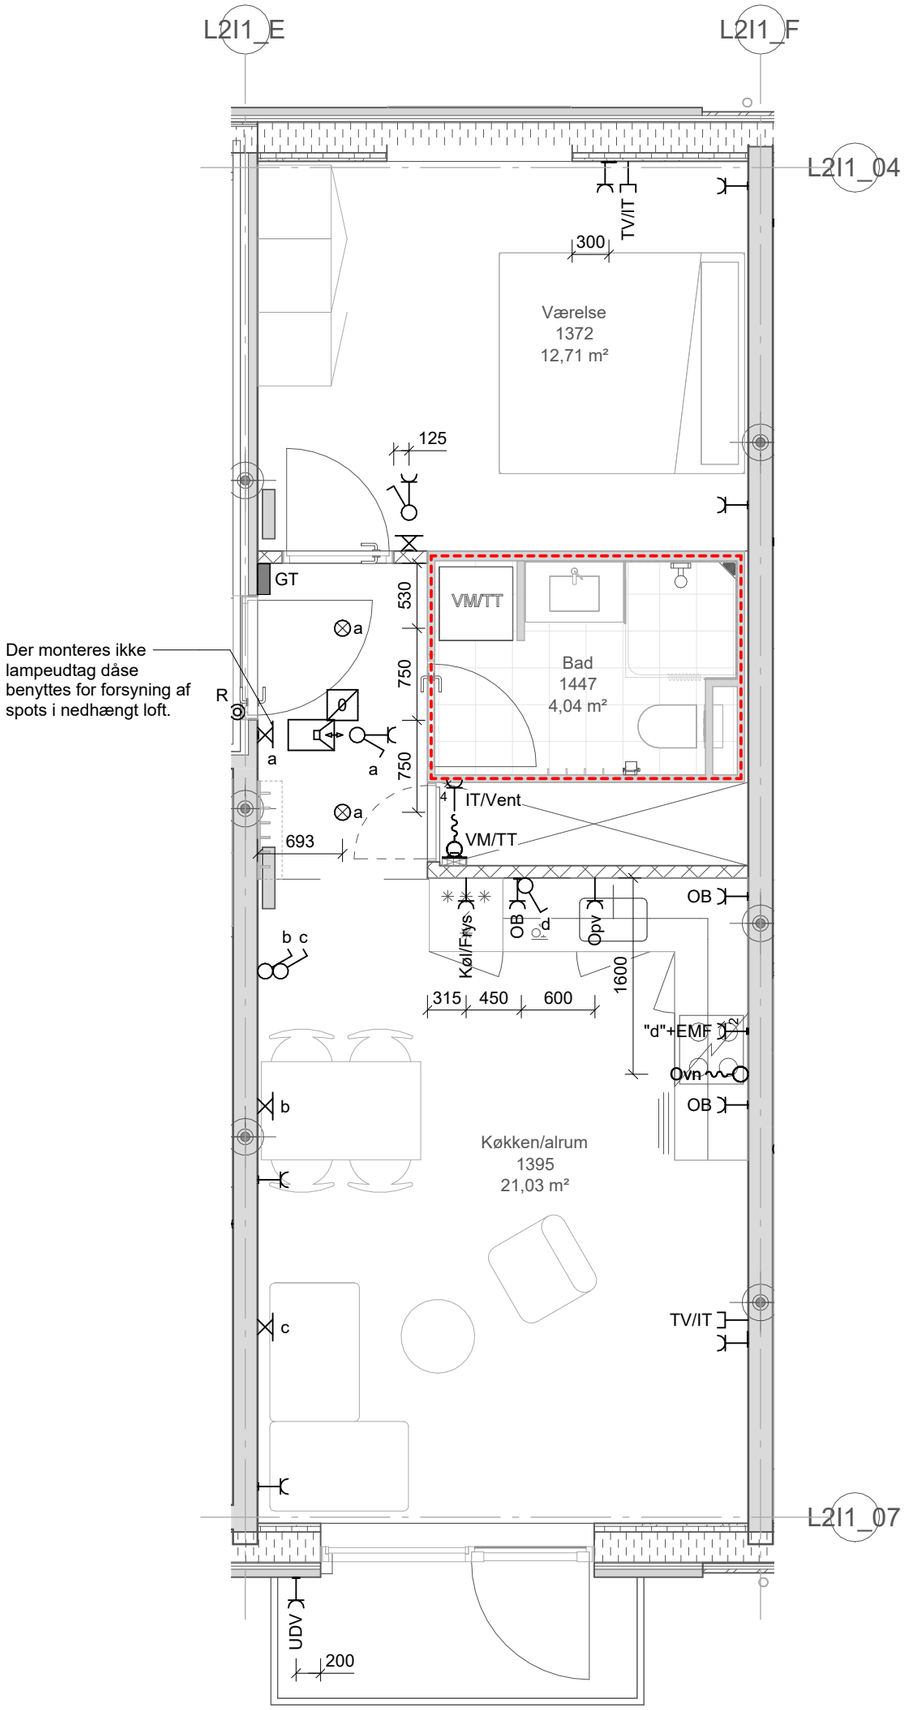

Projekt: Stejlepladsen


Tekst: Elinstallationer -
Byg I1 - 2. Sal, Byg D
OPG_2V_T31 - Side I1-18

Tegningsnr.: ISP2_K07_L2XX_H04_EXX_N930


Rev.:

Projektnr.: 1019198 | Dato: 2026-02-27 | Rev. Dato: | Mål: 1 : 50 | Side: I1-18


www.arteliagroup.dk | Fil:

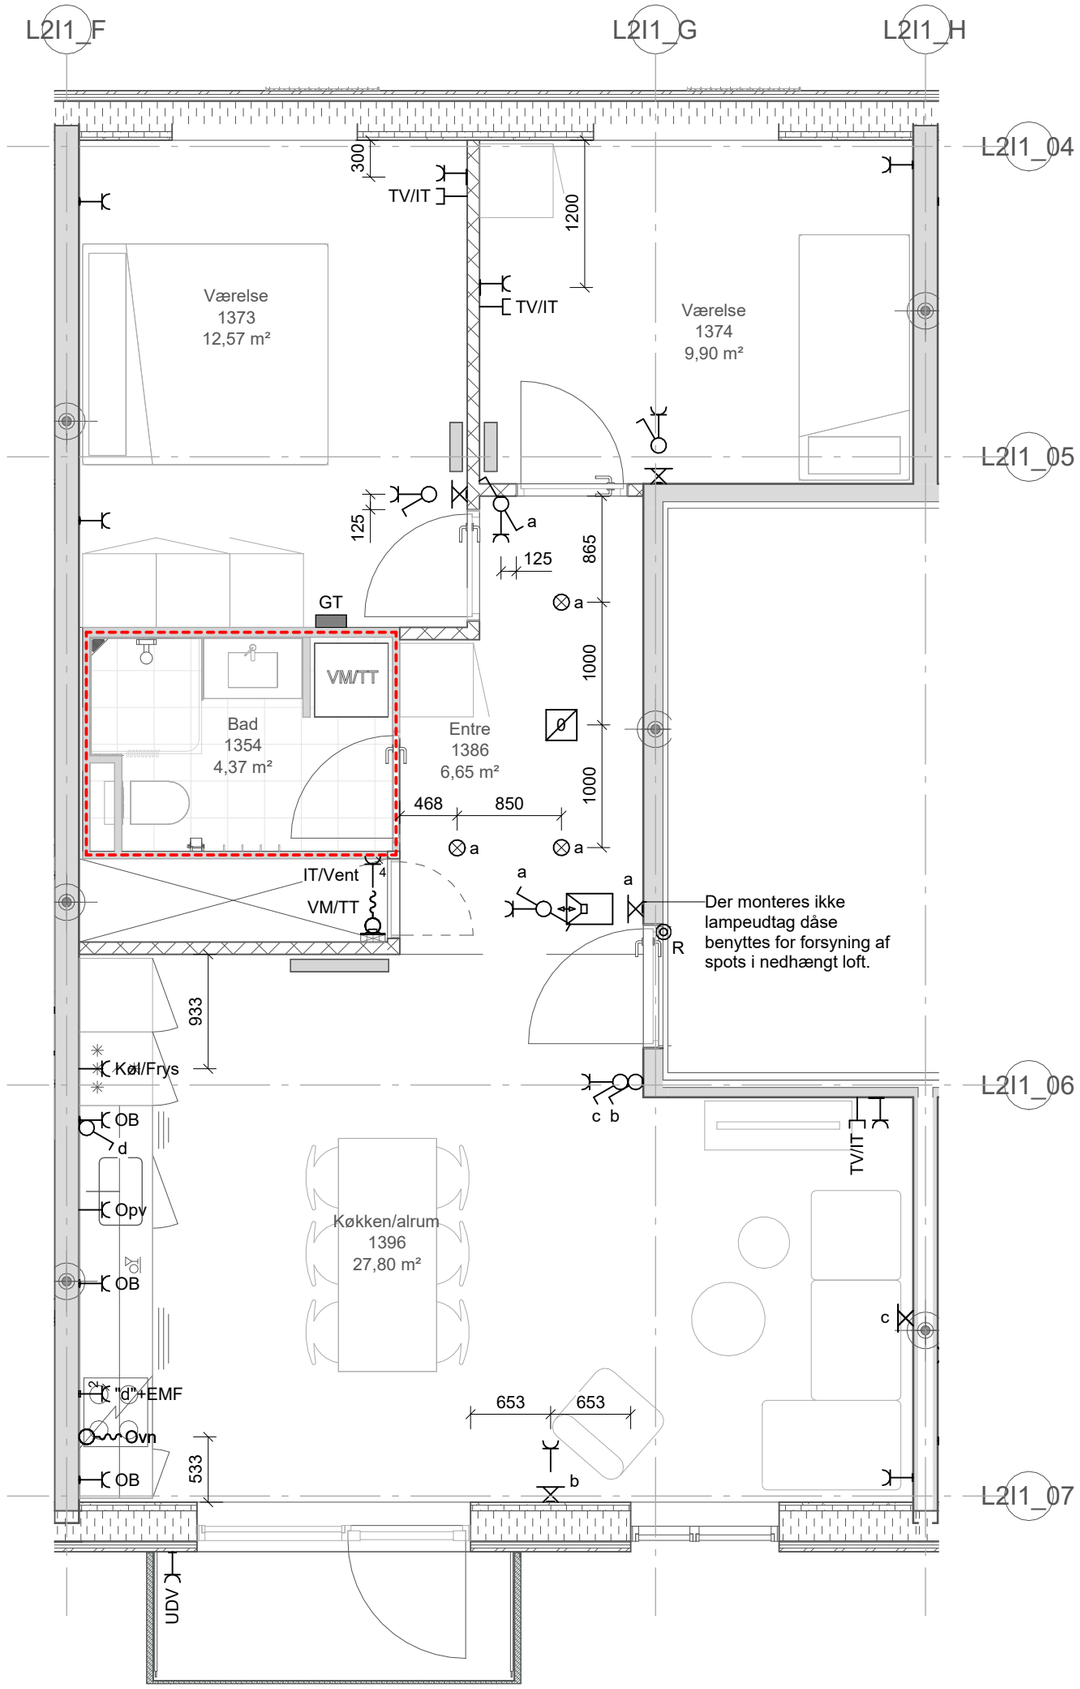


Projekt:	Stejlepladsen				
Tekst:	Elinstallationer - Byg I1 - 2. Sal, Byg E OPG_3V_T30 - Side I1-19			Tegningsnr.:	Rev.:
			ISP2_K07_L2XX_H04_EXX_N930		
Projektnr.: 1019198	Dato: 2026-02-27	Rev. Dato:		Mål: 1 : 50	Side: I1-19
www.arteliagroup.dk	Fil:				

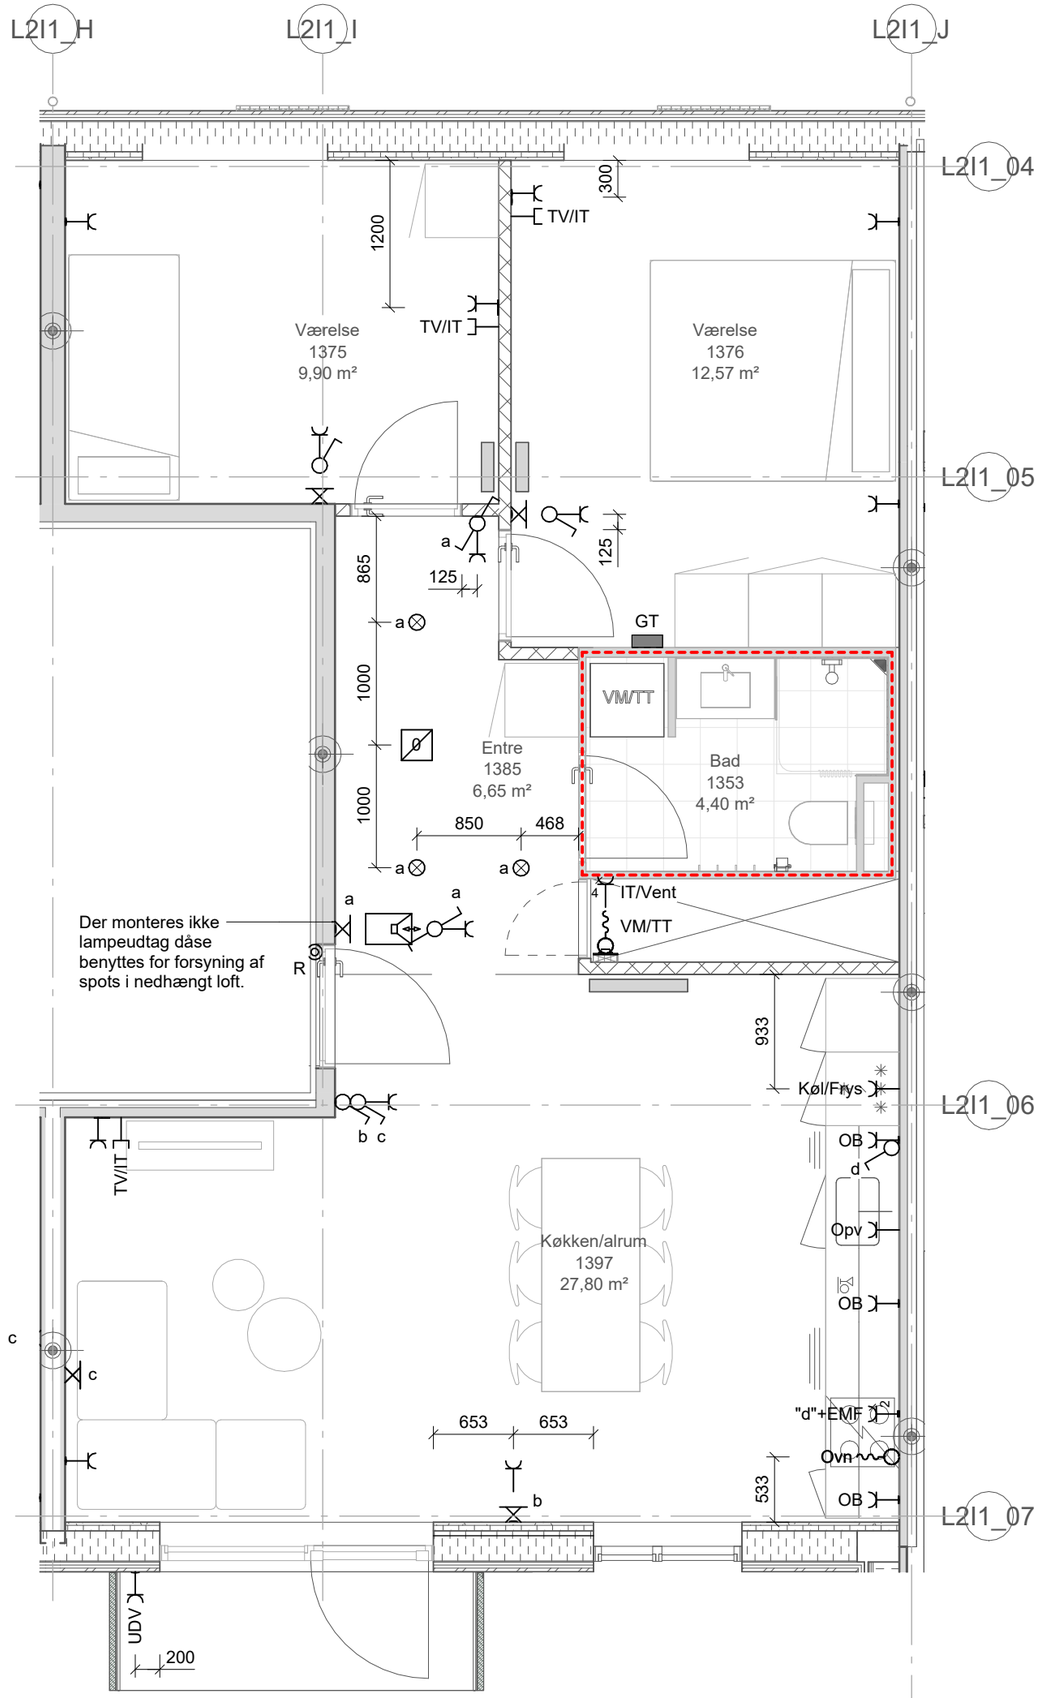

Projekt:	Stejlepladsen				
Tekst:	Elinstallationer - Byg I1 - 2. Sal, Byg E OPG_3V_T30_S - Side I1-20			Tegningsnr.:	Rev.:
				ISP2_K07_L2XX_H04_EXX_N930	
Projektnr.: 1019198	Dato: 2026-02-27	Rev. Dato:		Mål: 1 : 50	Side: I1-20
www.arteliagroup.dk	Fil:				

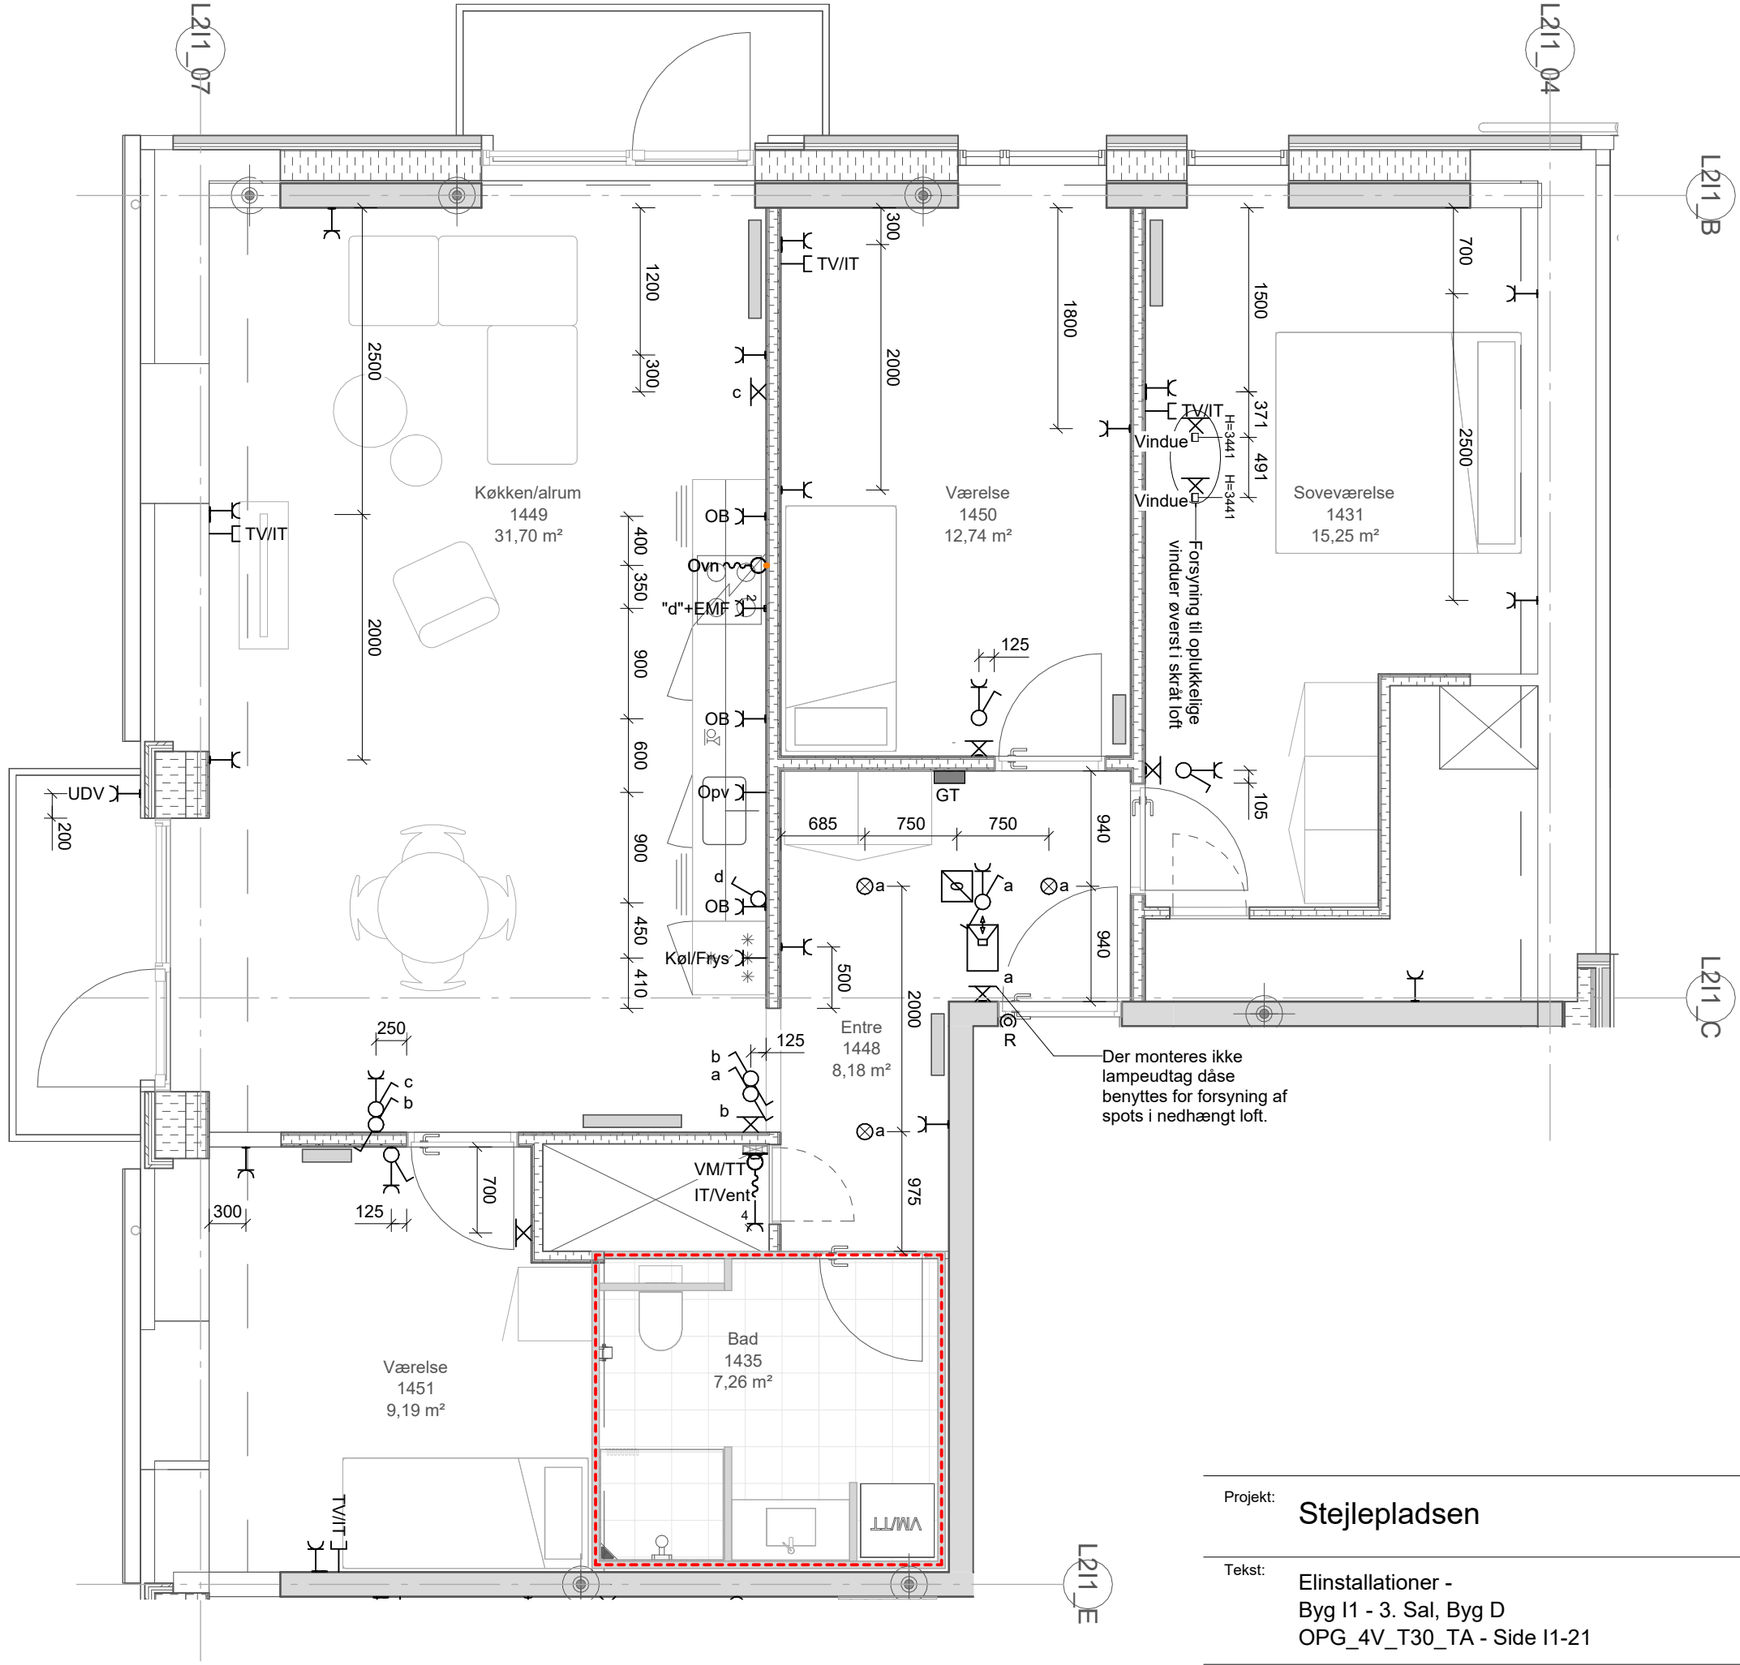


Projekt:	Stejlepladsen				
Tekst:	Elinstallationer - Byg I1 - 3. Sal, Byg D OPG_4V_T30_TA - Side I1-21			Tegningsnr.:	Rev.:
				ISP2_K07_L2XX_H04_EXX_N930	
Projektnr.: 1019198	Dato: 2026-02-27	Rev. Dato:		Mål: 1 : 50	Side: I1-21
www.arteliagroup.dk	Fil:				

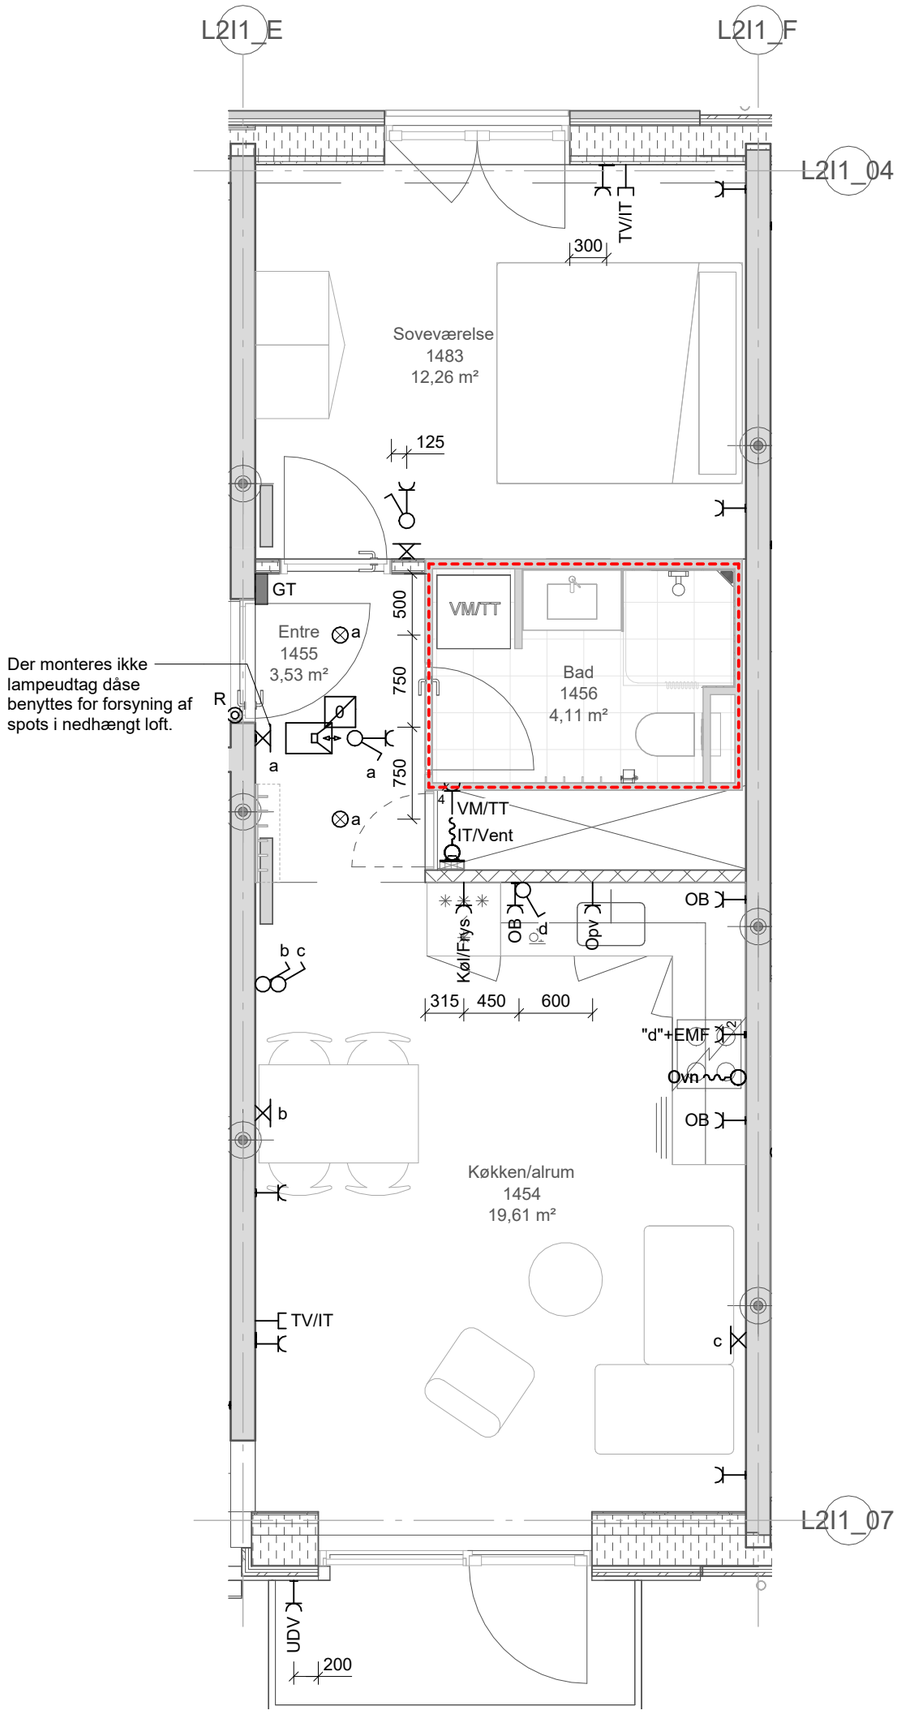


Der monteres ikke lampeudtag dåse benyttes for forsyning af spots i nedhængt loft.


Projekt:	Stejlepladsen				
Tekst:	Elinstallationer - Byg I1 - 3. Sal, Byg D OPG_2V_T31_TA - Side I1-22			Tegningsnr.:	Rev.:
				ISP2_K07_L2XX_H04_EXX_N930	
Projektnr.: 1019198	Dato: 2026-02-27	Rev. Dato:		Mål: 1 : 50	Side: I1-22
www.arteliagroup.dk	Fil:				

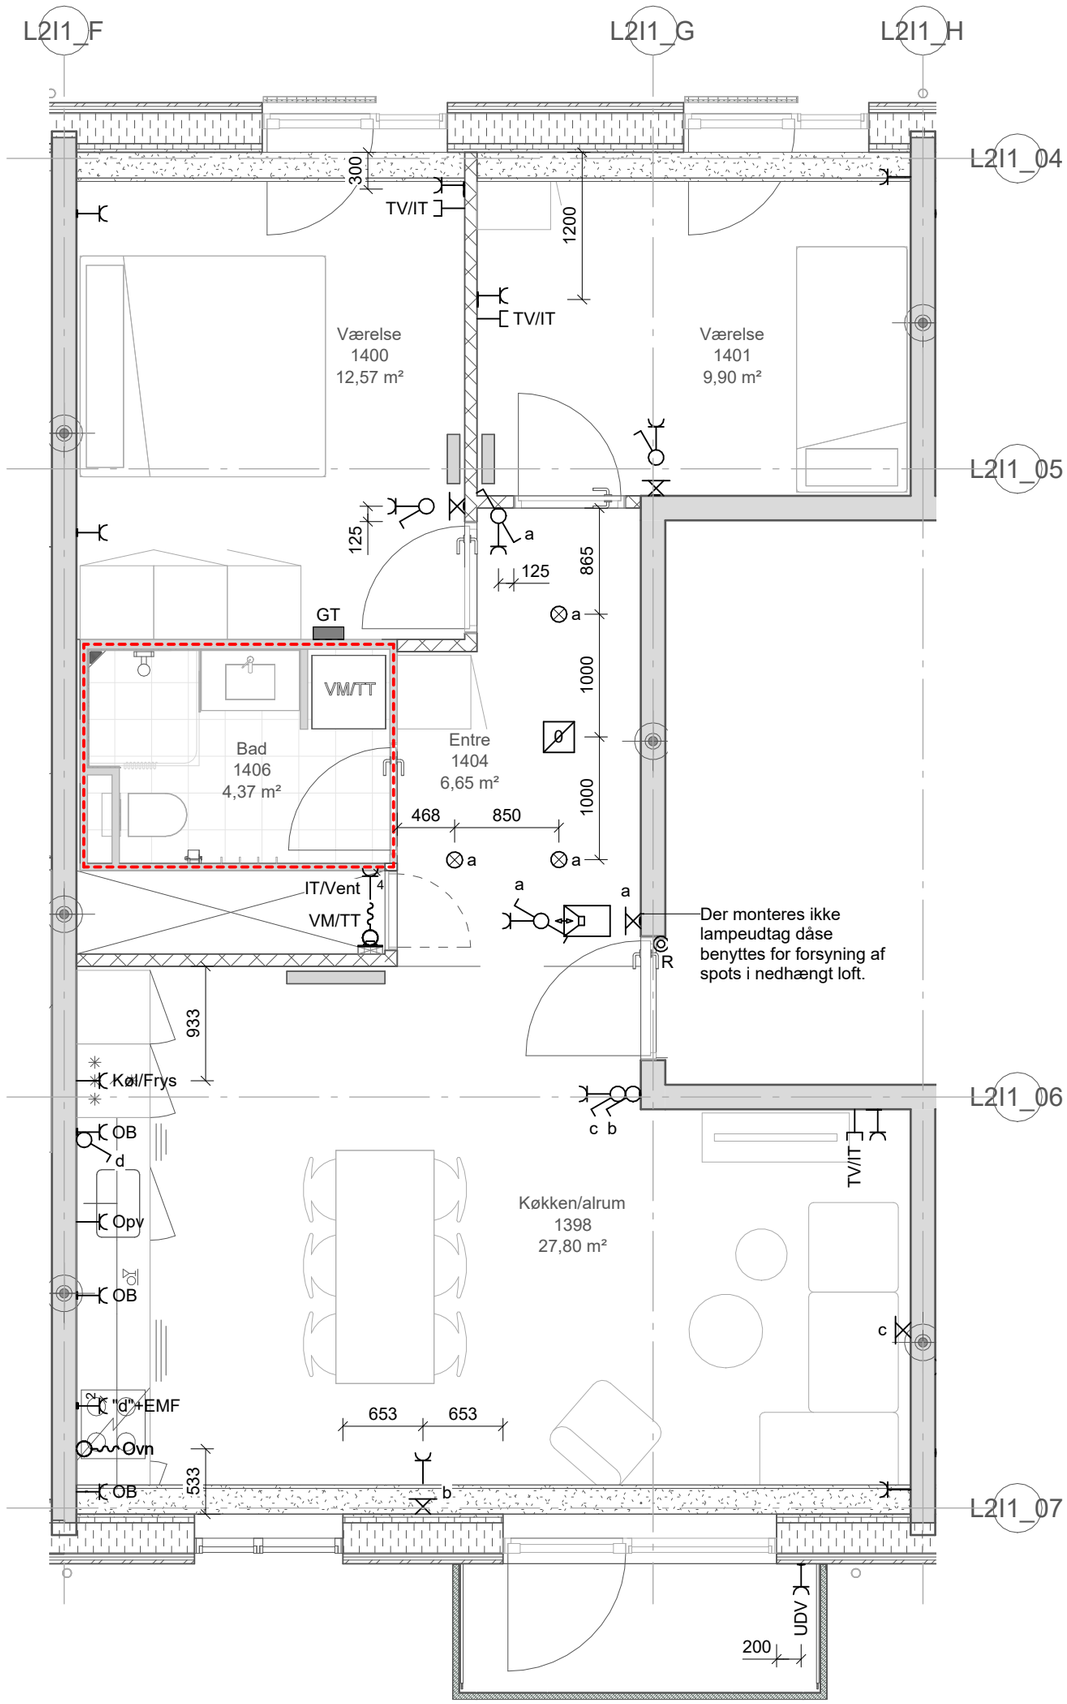

Projekt:	Stejlepladsen				
Tekst:	Elinstallationer - Byg I1 - 3. Sal, Byg E OPG_3V_T30 - Side I1-23			Tegningsnr.:	Rev.:
			ISP2_K07_L2XX_H04_EXX_N930		
Projektnr.: 1019198	Dato: 2026-02-27	Rev. Dato:		Mål: 1 : 50	Side: I1-23
www.arteliagroup.dk	Fil:				

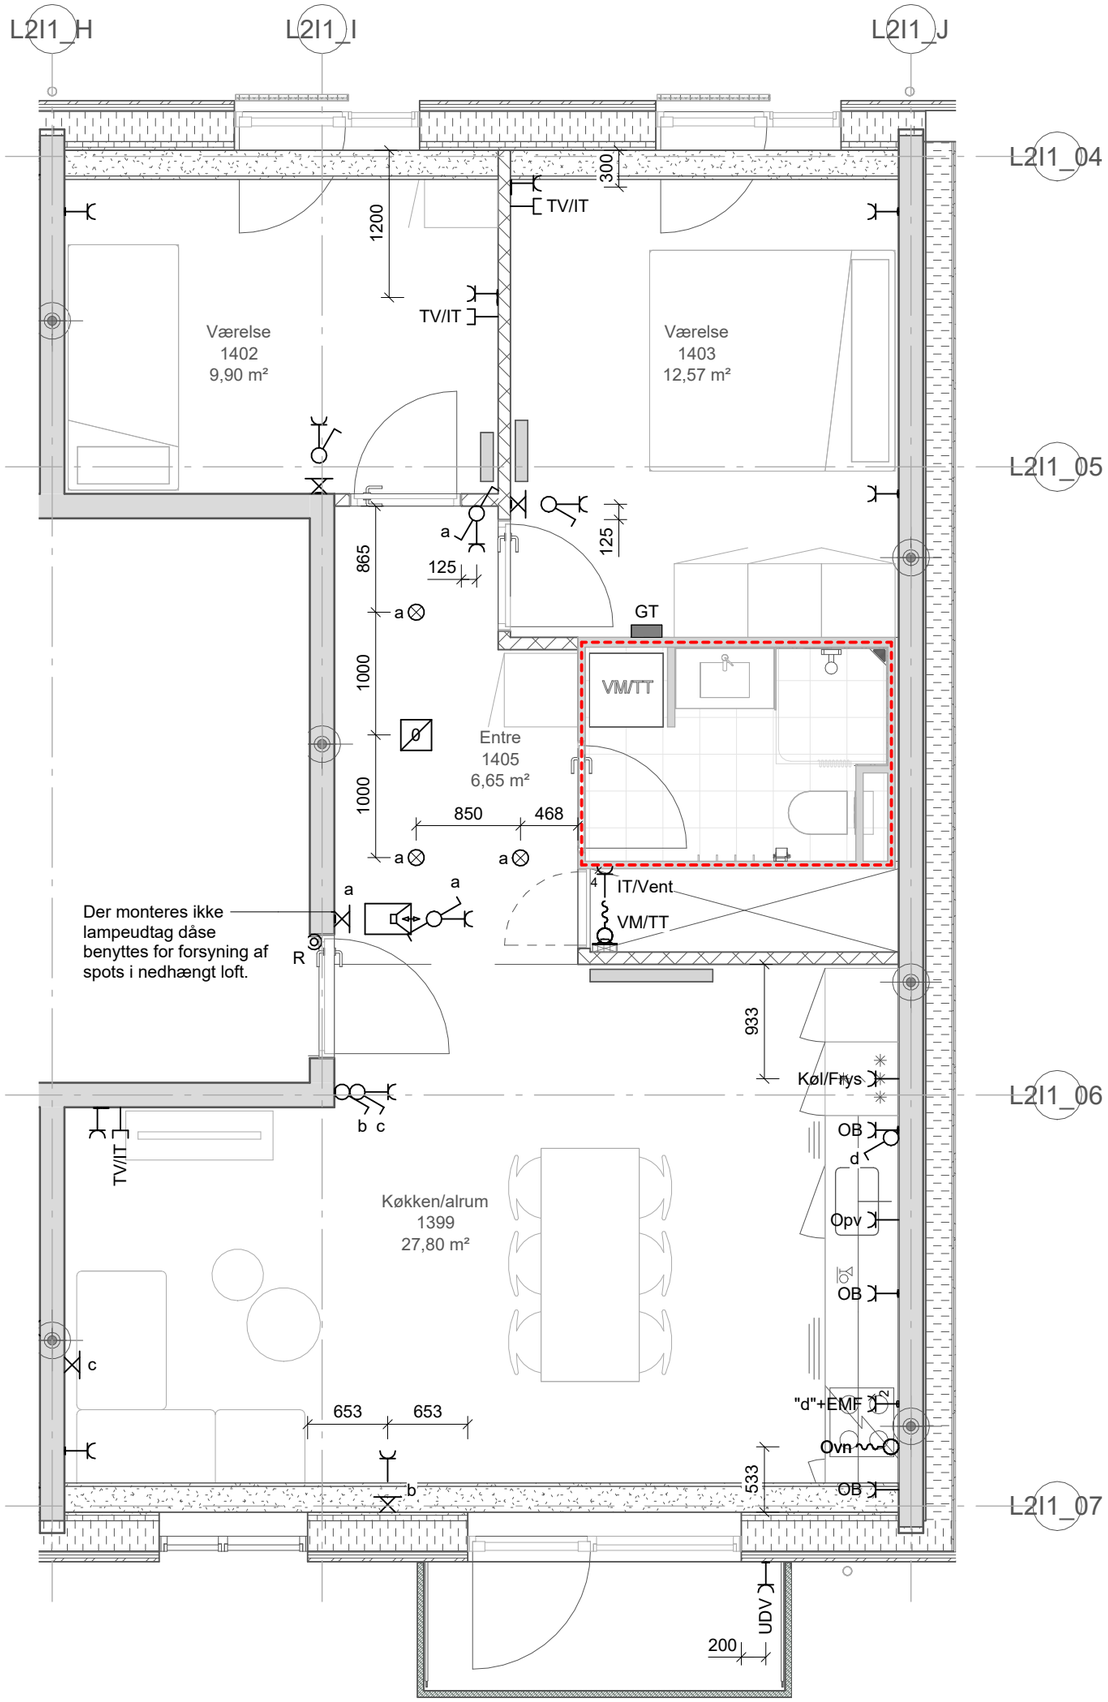

Projekt:	Stejlepladsen				
Tekst:	Elinstallationer - Byg I1 - 3. Sal, Byg E OPG_3V_T30_S - Side I1-24			Tegningsnr.:	Rev.:
			ISP2_K07_L2XX_H04_EXX_N930		
Projektnr.: 1019198	Dato: 2026-02-27	Rev. Dato:		Mål: 1 : 50	Side: I1-24
www.arteliagroup.dk	Fil:				

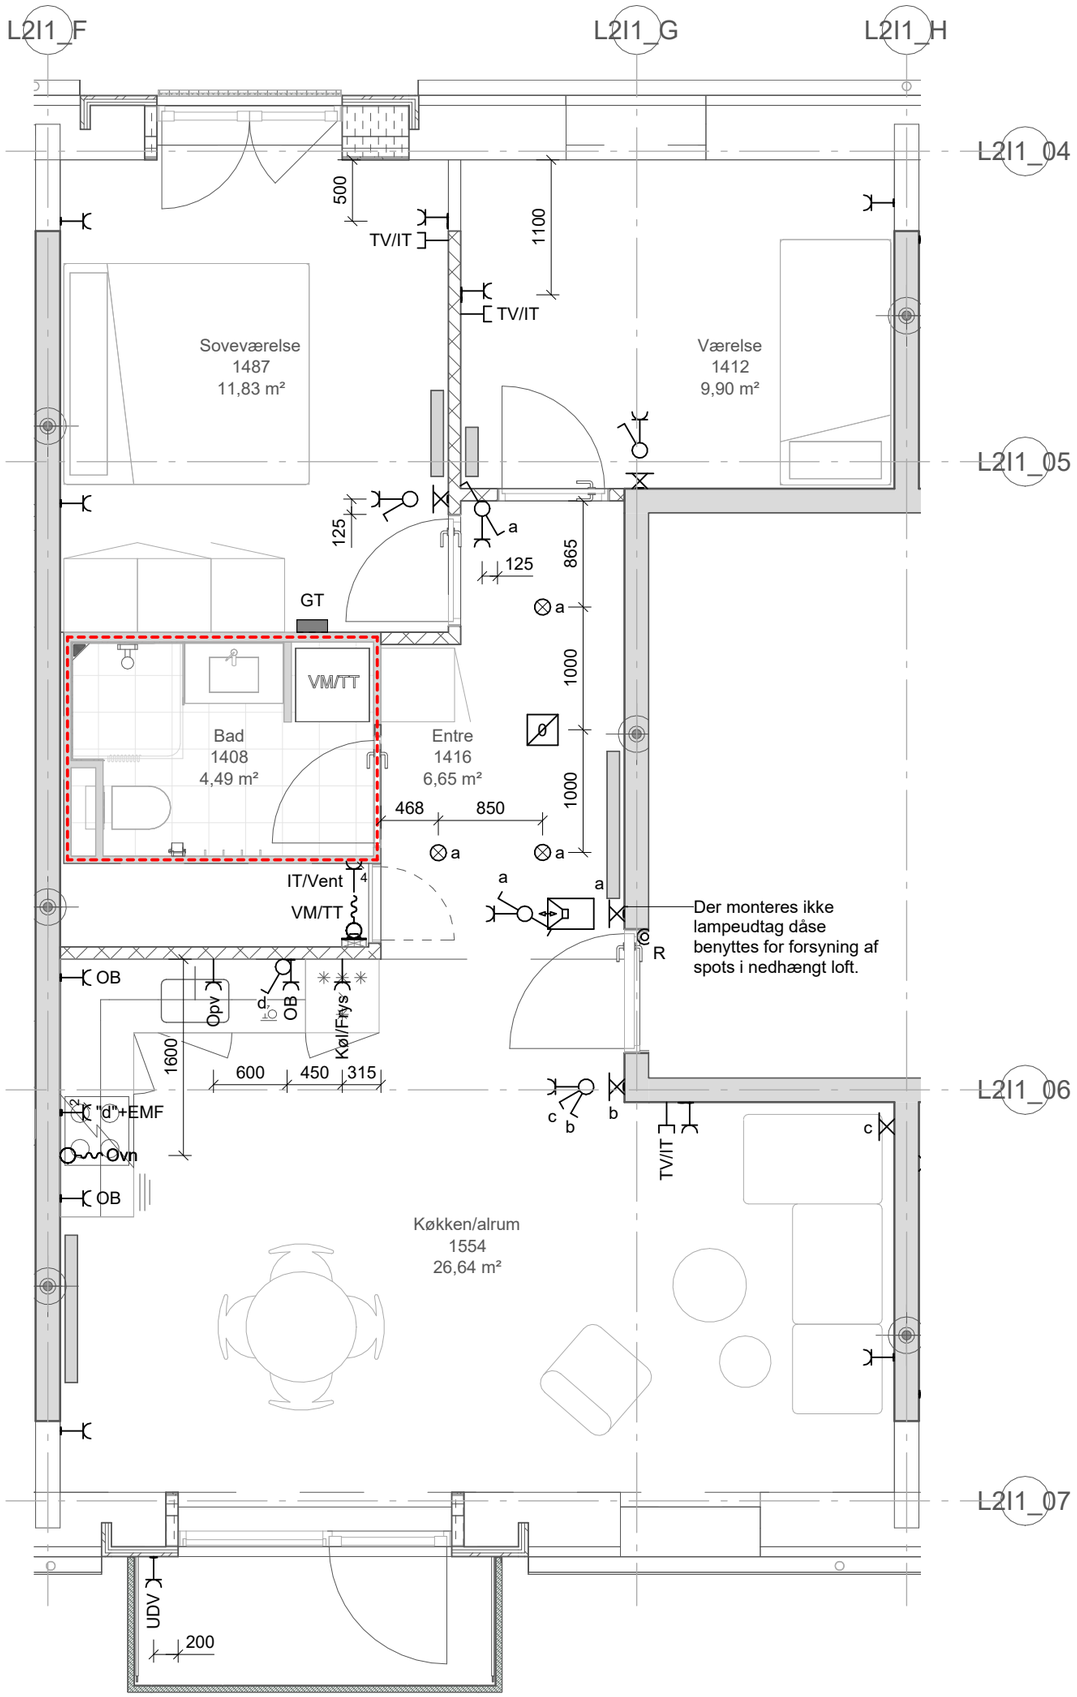

Projekt: Stejlepladsen


Tekst: Elinstallationer -
Byg I1 - 4. Sal, Byg E
OPG_3V_T31_TA - Side I1-25

Tegningsnr.: ISP2_K07_L2XX_H04_EXX_N930

Rev.:

Projektnr.: 1019198 | Dato: 2026-02-27 | Rev. Dato: | Mål: 1 : 50 | Side: I1-25

www.arteliagroup.dk | Fil:

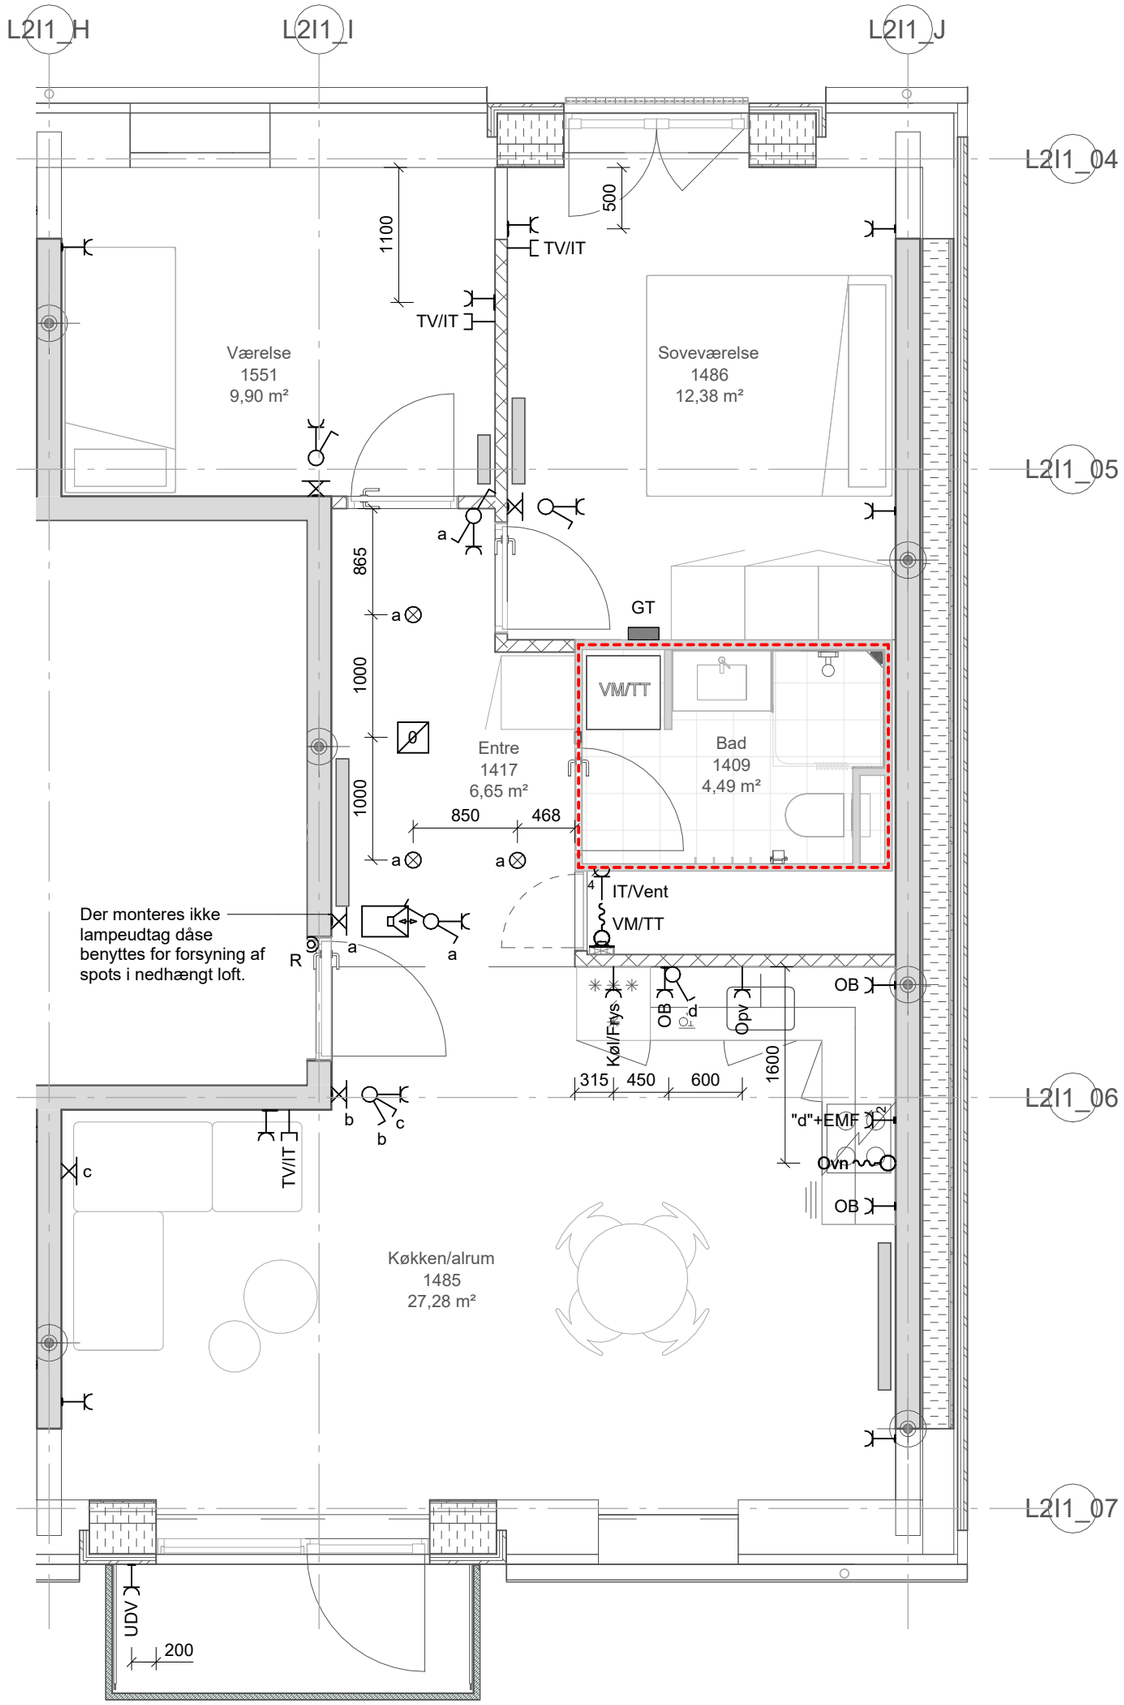

Projekt: Stejlepladsen

Tekst: Elinstallationer -
Byg I1 - 4. Sal, Byg E
OPG_3V_T31_TA_S - Side I1-26

Tegningsnr.: ISP2_K07_L2XX_H04_EXX_N930

Rev.:

Projektnr.: 1019198 | Dato: 2026-02-27 | Rev. Dato: | Mål: 1 : 50 | Side: I1-26

www.arteliagroup.dk | Fil: