Sheet Number	Tekst:	Dato:	Rev.:	Rev. Dato:
ISP2_K07_L2XX_H04_EXX_N930 - Side J1-1	Byg J1 - Index	2026-02-27		
ISP2_K07_L2XX_H04_EXX_N930 - Side J1-2	Byg J1 - Oversigtsplan	2026-02-27		
ISP2_K07_L2XX_H04_EXX_N930 - Side J1-3	Byg J1 - Stueplan, Byg A	2026-02-27		
ISP2_K07_L2XX_H04_EXX_N930 - Side J1-4	Byg J1 - Stueplan, Byg B	2026-02-27		
ISP2_K07_L2XX_H04_EXX_N930 - Side J1-5	Byg J1 - Stueplan, Byg B	2026-02-27		
ISP2_K07_L2XX_H04_EXX_N930 - Side J1-6	Byg J1 - Stueplan, Byg B	2026-02-27		
ISP2_K07_L2XX_H04_EXX_N930 - Side J1-7	Byg J1 - Stueplan, Byg B	2026-02-27		
ISP2_K07_L2XX_H04_EXX_N930 - Side J1-8	Byg J1 - Stueplan, Byg C	2026-02-27		
ISP2_K07_L2XX_H04_EXX_N930 - Side J1-9	Byg J1 - Stueplan, Byg C	2026-02-27		
ISP2_K07_L2XX_H04_EXX_N930 - Side J1-10	Byg J1 - Stueplan , Byg D	2026-02-27		
ISP2_K07_L2XX_H04_EXX_N930 - Side J1-11	Byg J1 - Stueplan, Byg D	2026-02-27		
ISP2_K07_L2XX_H04_EXX_N930 - Side J1-12	Byg J1 - 1. Sal, Byg A	2026-02-27		
ISP2_K07_L2XX_H04_EXX_N930 - Side J1-13	Byg J1 - 1. Sal, Byg A	2026-02-27		
ISP2_K07_L2XX_H04_EXX_N930 - Side J1-14	Byg J1 - 1. Sal, Byg B	2026-02-27		
ISP2_K07_L2XX_H04_EXX_N930 - Side J1-15	Byg J1 - 1. Sal, Byg B	2026-02-27		
ISP2_K07_L2XX_H04_EXX_N930 - Side J1-16	Byg J1 - 1. Sal, Byg B	2026-02-27		
ISP2_K07_L2XX_H04_EXX_N930 - Side J1-17	Byg J1 - 1. Sal, Byg B	2026-02-27		
ISP2_K07_L2XX_H04_EXX_N930 - Side J1-18	Byg J1 - 1. Sal, Byg C	2026-02-27		
ISP2_K07_L2XX_H04_EXX_N930 - Side J1-19	Byg J1 - 1. Sal, Byg C	2026-02-27		
ISP2_K07_L2XX_H04_EXX_N930 - Side J1-20	Byg J1 - 1. Sal, Byg D	2026-02-27		
ISP2_K07_L2XX_H04_EXX_N930 - Side J1-21	Byg J1 - 1. Sal, Byg D	2026-02-27		
ISP2_K07_L2XX_H04_EXX_N930 - Side J1-22	Byg J1 - 2. Sal, Byg A	2026-02-27		
ISP2_K07_L2XX_H04_EXX_N930 - Side J1-23	Byg J1 - 2. Sal, Byg A	2026-02-27		
ISP2_K07_L2XX_H04_EXX_N930 - Side J1-24	Byg J1 - 2. Sal, Byg B	2026-02-27		
ISP2_K07_L2XX_H04_EXX_N930 - Side J1-25	Byg J1 - 2. Sal, Byg B	2026-02-27		
ISP2_K07_L2XX_H04_EXX_N930 - Side J1-26	Byg J1 - 2. Sal, Byg B	2026-02-27		
ISP2_K07_L2XX_H04_EXX_N930 - Side J1-27	Byg J1 - 2. Sal, Byg B	2026-02-27		
ISP2_K07_L2XX_H04_EXX_N930 - Side J1-28	Byg J1 - 2. Sal, Byg C	2026-02-27		
ISP2_K07_L2XX_H04_EXX_N930 - Side J1-29	Byg J1 - 2. Sal, Byg C	2026-02-27		
ISP2_K07_L2XX_H04_EXX_N930 - Side J1-30	Byg J1 - 2. Sal, Byg D	2026-02-27		
ISP2_K07_L2XX_H04_EXX_N930 - Side J1-31	Byg J1 - 2. Sal, Byg D	2026-02-27		
ISP2_K07_L2XX_H04_EXX_N930 - Side J1-32	Byg J1 - 3. Sal, Byg A	2026-02-27		
ISP2_K07_L2XX_H04_EXX_N930 - Side J1-33	Byg J1 - 3. Sal, Byg A	2026-02-27		
ISP2_K07_L2XX_H04_EXX_N930 - Side J1-34	Byg J1 - 3. Sal, Byg B	2026-02-27		
ISP2_K07_L2XX_H04_EXX_N930 - Side J1-35	Byg J1 - 3. Sal, Byg B	2026-02-27		
ISP2_K07_L2XX_H04_EXX_N930 - Side J1-36	Byg J1 - 3. Sal, Byg B	2026-02-27		
ISP2_K07_L2XX_H04_EXX_N930 - Side J1-37	Byg J1 - 3. Sal, Byg B	2026-02-27		
ISP2_K07_L2XX_H04_EXX_N930 - Side J1-38	Byg J1 - 3. Sal, Byg C	2026-02-27		
ISP2_K07_L2XX_H04_EXX_N930 - Side J1-39	Byg J1 - 3. Sal, Byg C	2026-02-27		
ISP2_K07_L2XX_H04_EXX_N930 - Side J1-40	Byg J1 - 3. Sal, Byg D	2026-02-27		
ISP2_K07_L2XX_H04_EXX_N930 - Side J1-41	Byg J1 - 3. Sal, Byg D	2026-02-27		
ISP2_K07_L2XX_H04_EXX_N930 - Side J1-42	Byg J1 - 4. Sal, Byg A	2026-02-27		
ISP2_K07_L2XX_H04_EXX_N930 - Side J1-43	Byg J1 - 4. Sal, Byg A	2026-02-27		
ISP2_K07_L2XX_H04_EXX_N930 - Side J1-44	Byg J1 - 4. Sal, Byg B	2026-02-27		
ISP2_K07_L2XX_H04_EXX_N930 - Side J1-45	Byg J1 - 4. Sal, Byg B	2026-02-27		
ISP2_K07_L2XX_H04_EXX_N930 - Side J1-46	Byg J1 - 4. Sal, Byg B	2026-02-27		
ISP2_K07_L2XX_H04_EXX_N930 - Side J1-47	Byg J1 - 4. Sal, Byg B	2026-02-27		
ISP2_K07_L2XX_H04_EXX_N930 - Side J1-48	Byg J1 - 4. Sal, Byg C	2026-02-27		
ISP2_K07_L2XX_H04_EXX_N930 - Side J1-49	Byg J1 - 4. Sal, Byg C	2026-02-27		
ISP2_K07_L2XX_H04_EXX_N930 - Side J1-50	Byg J1 - 4. Sal, Byg D	2026-02-27		
ISP2_K07_L2XX_H04_EXX_N930 - Side J1-51	Byg J1 - 4. Sal, Byg D	2026-02-27		
ISP2_K07_L2XX_H04_EXX_N930 - Side J1-52	Byg J1 - 5. Sal, Byg A	2026-02-27		
ISP2_K07_L2XX_H04_EXX_N930 - Side J1-53	Byg J1 - 5. Sal, Byg A	2026-02-27		
ISP2_K07_L2XX_H04_EXX_N930 - Side J1-54	Byg J1 - 5. Sal, Byg C	2026-02-27		
ISP2_K07_L2XX_H04_EXX_N930 - Side J1-55	Byg J1 - 5. Sal, Byg C	2026-02-27		

Projekt: Stejlepladsen

Tekst: Elinstallationer - Byg J1 - Index

Tegningsnr.: ISP2_K07_L2XX_H04_EXX_N930

Rev.:


Projektnr.: 1019198 | Dato: 2026-02-27 | Rev. Dato: | Mål: | Side: J1-1

www.arteliagroup.dk | Fil:


Stueplan - Byg J1




1. sal - Byg J1

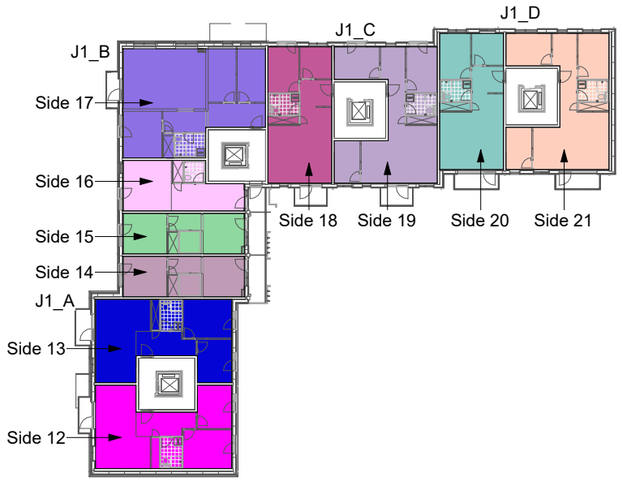


2. sal - Byg J1

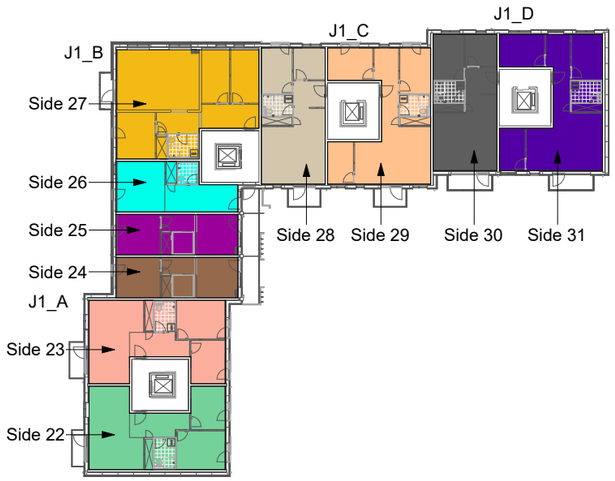


3. sal - Byg J1

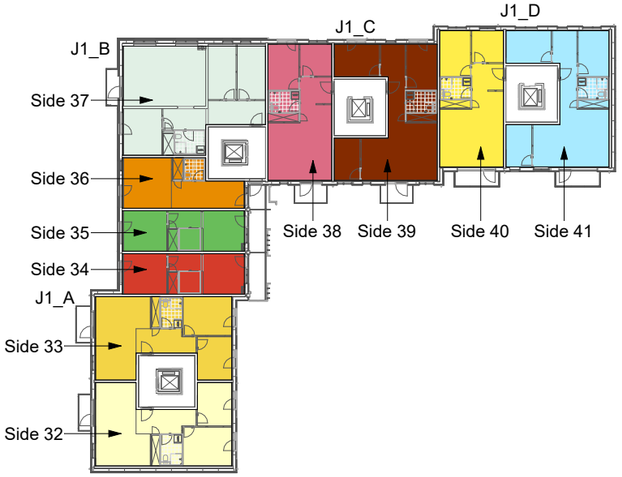

4. sal - Byg J1

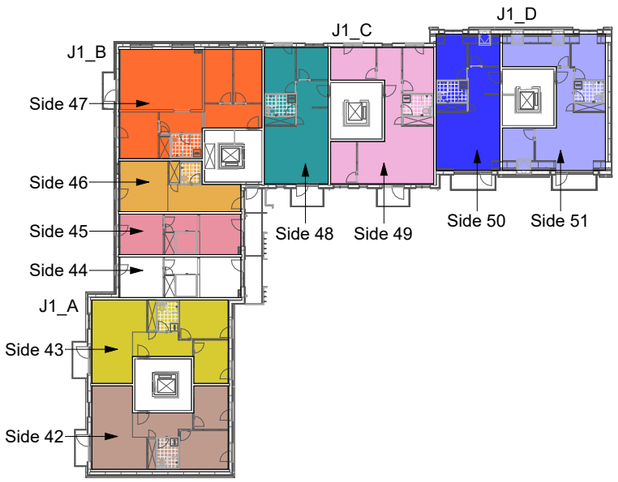

5. sal - Byg J1

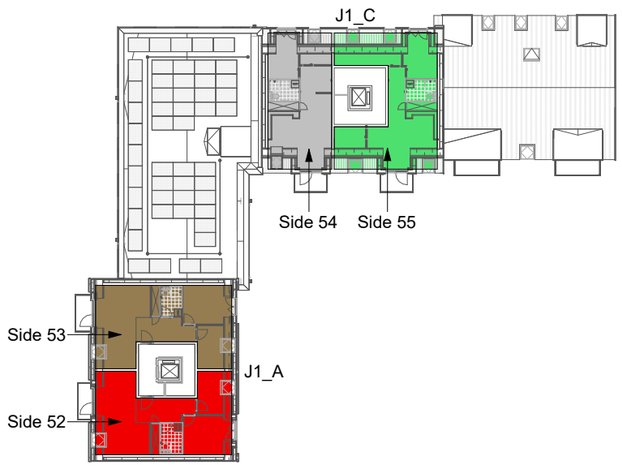

Oversigt, bygning J1:

Side 3:	Opgangsbolig, Byg A, st., 3V	Side 28:	Opgangsbolig, Byg C, 2.sal, 3V	Side 53:	Opgangsbolig, Byg A, 5.sal, 3V
Side 4:	Altangangsbolig, Byg B, st., 1V	Side 29:	Opgangsbolig, Byg C, 2.sal, 4V	Side 54:	Opgangsbolig, Byg C, 5.sal, 3V
Side 5:	Altangangsbolig, Byg B, st., 1V	Side 30:	Opgangsbolig, Byg D, 2.sal, 3V	Side 55:	Opgangsbolig, Byg C, 5.sal, 4V
Side 6:	Altangangsbolig, Byg B, st., 1V	Side 31:	Opgangsbolig, Byg D, 2.sal, 4V		
Side 7:	Opgangsbolig, Byg B, st., 2V	Side 32:	Opgangsbolig, Byg A, 3.sal, 3V		
Side 8:	Opgangsbolig, Byg C, st., 3V	Side 33:	Opgangsbolig, Byg A, 3.sal, 3V		
Side 9:	Opgangsbolig, Byg C, st., 3V	Side 34:	Altangangsbolig, Byg B, 3.sal, 1V		
Side 10:	Opgangsbolig, Byg D, st., 3V	Side 35:	Altangangsbolig, Byg B, 3.sal, 1V		
Side 11:	Opgangsbolig, Byg D, st., 3V	Side 36:	Altangangsbolig, Byg B, 3.sal, 1V		
Side 12:	Opgangsbolig, Byg A 1.sal, 3V	Side 37:	Opgangsbolig, Byg B, 3.sal, 4V		
Side 13:	Opgangsbolig, Byg A, 1.sal, 3V	Side 38:	Opgangsbolig, Byg C, 3.sal, 3V		
Side 14:	Altangangsbolig, Byg B, 1.sal, 1V	Side 39:	Opgangsbolig, Byg C, 3.sal, 4V		
Side 15:	Altangangsbolig, Byg B, 1.sal, 1V	Side 40:	Opgangsbolig, Byg D, 3.sal, 3V		
Side 16:	Altangangsbolig, Byg B, 1.sal, 1V	Side 41:	Opgangsbolig, Byg D, 3.sal, 4V		
Side 17:	Opgangsbolig, Byg B, 1.sal, 4V	Side 42:	Opgangsbolig, Byg A, 4.sal, 3V		
Side 18:	Opgangsbolig, Byg C, 1.sal, 3V	Side 43:	Opgangsbolig, Byg A, 4.sal, 3V		
Side 19:	Opgangsbolig, Byg C, 1.sal, 4V	Side 44:	Altangangsbolig, Byg B, 4.sal, 1V		
Side 20:	Opgangsbolig, Byg D, 1.sal, 3V	Side 45:	Altangangsbolig, Byg B, 4.sal, 1V		
Side 21:	Opgangsbolig, Byg D, 1.sal, 4V	Side 46:	Altangangsbolig, Byg B, 4.sal, 1V		
Side 22:	Opgangsbolig, Byg A, 2.sal, 3V	Side 47:	Opgangsbolig, Byg B, 4.sal, 4V		
Side 23:	Opgangsbolig, Byg A, 2.sal, 3V	Side 48:	Opgangsbolig, Byg C, 4.sal, 3V		
Side 24:	Altangangsbolig, Byg B, 2.sal, 1V	Side 49:	Opgangsbolig, Byg C, 4.sal, 4V		
Side 25:	Altangangsbolig, Byg B, 2.sal, 1V	Side 50:	Opgangsbolig, Byg D, 4.sal, 3V		
Side 26:	Altangangsbolig, Byg B, 2.sal, 1V	Side 51:	Opgangsbolig, Byg D, 4.sal, 4V		
Side 27:	Opgangsbolig, Byg B, 2.sal, 4V	Side 52:	Opgangsbolig, Byg A, 5.sal, 3V		

Projekt: Stejlepladsen


Tekst: Elinstallationer - Byg J1 - Oversigtsplan

Tegningsnr.: ISP2_K07_L2XX_H04_EXX_N930

Rev.:

Projektnr.: 1019198 | Dato: 2026-02-27 | Rev. Dato: | Mål: 1 : 500 | Side: J1-2

www.arteliagroup.dk | Fil:

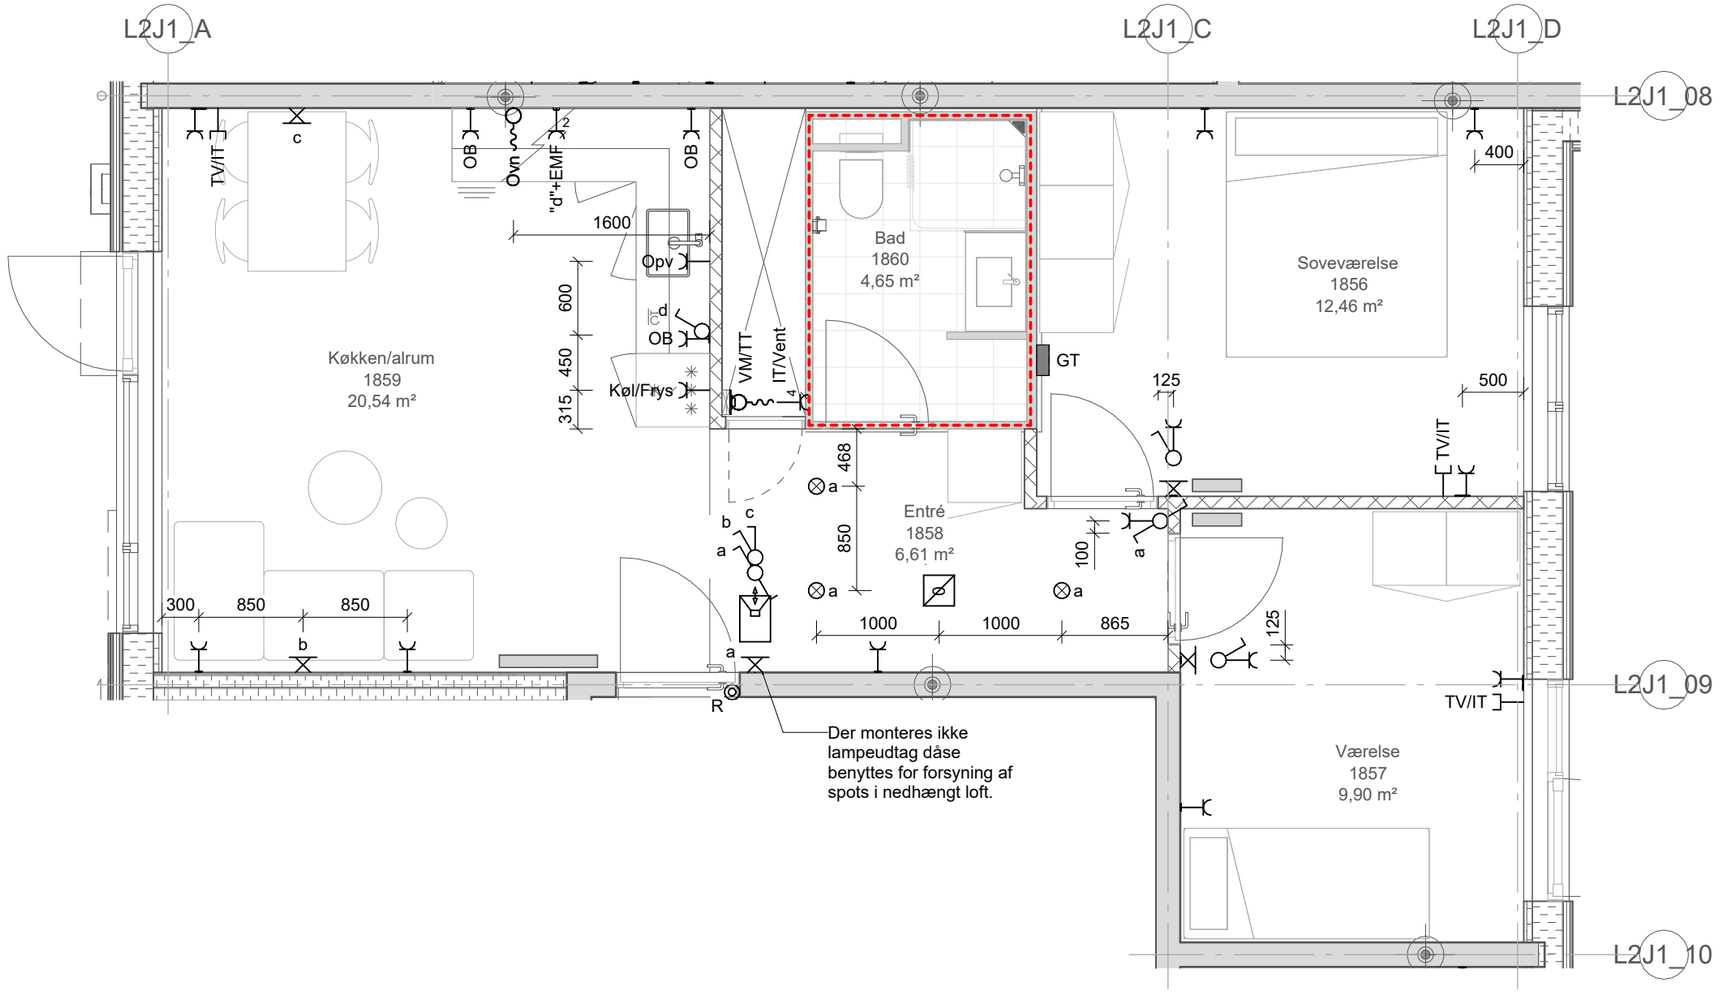

Projekt: Stejlepladsen


Tekst: Elinstallationer -
Byg J1 - Stueplan, Byg A
OPG_3V_T32_ST - Side J1-3

Tegningsnr.: ISP2_K07_L2XX_H04_EXX_N930

Rev.:

Projektnr.: 1019198 | Dato: 2026-02-27 | Rev. Dato: | Mål: 1 : 50 | Side: J1-3

www.arteliagroup.dk | Fil:

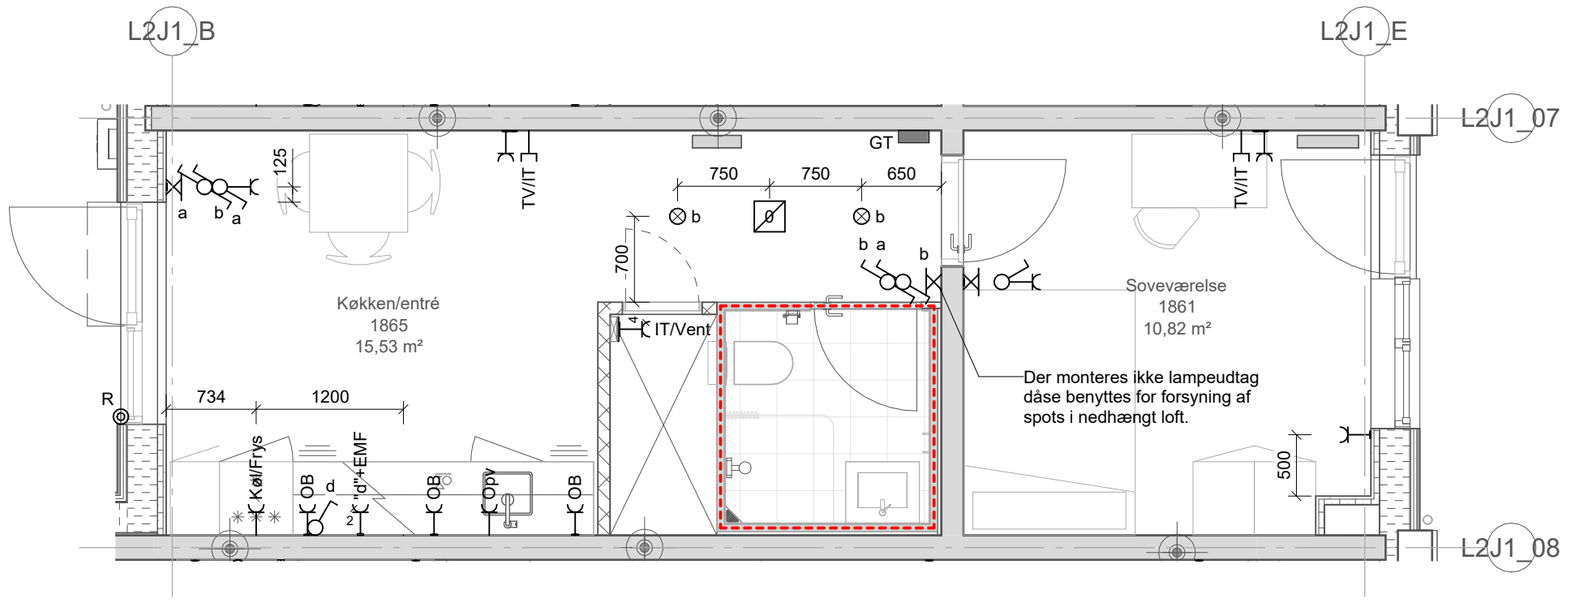

Projekt: Stejlepladsen


Tekst: Elinstallationer -
Byg J1 - Stueplan, Byg B
ALT_1V_T32_ST_A - Side J1-4

Tegningsnr.: ISP2_K07_L2XX_H04_EXX_N930

Rev.:

Projektnr.: 1019198 | Dato: 2026-02-27 | Rev. Dato: | Mål: 1 : 50 | Side: J1-4

www.arteliagroup.dk | Fil:

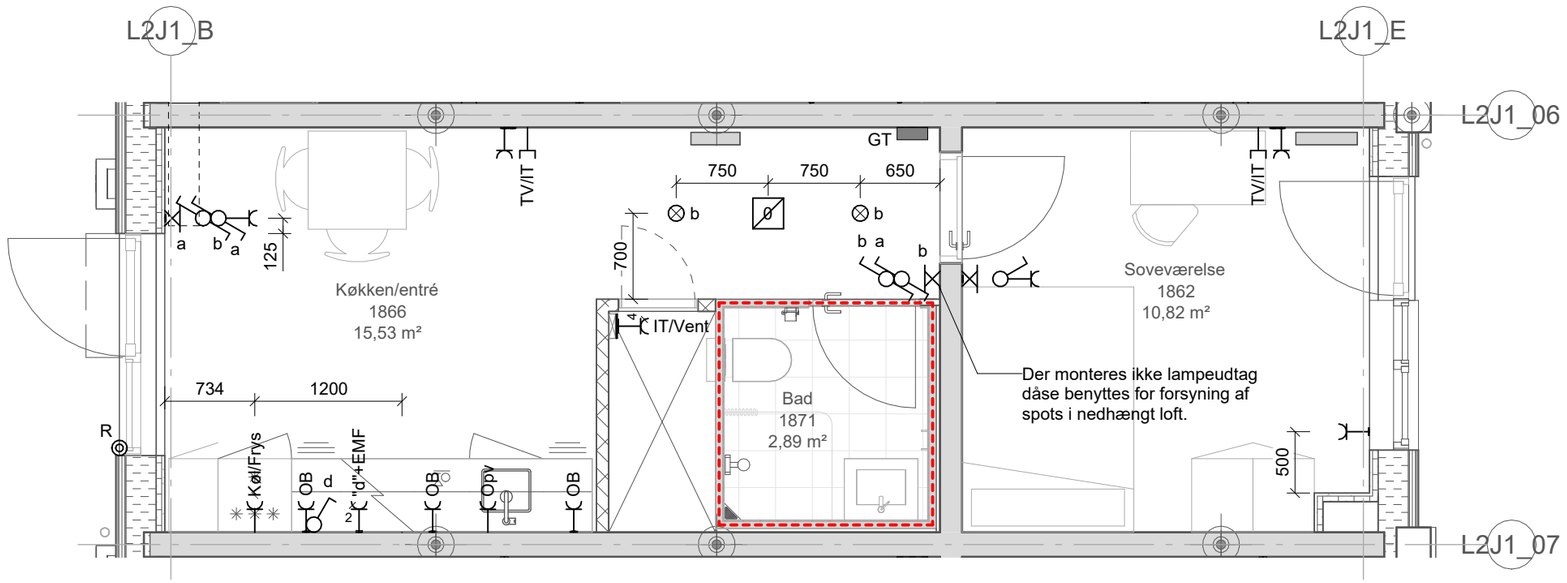

Projekt: Stejlepladsen

ARTELIA


Tekst: Elinstallationer -
Byg J1 - Stueplan, Byg B
ALT_1V_T32_ST_B - Side J1-5

Tegningsnr.: ISP2_K07_L2XX_H04_EXX_N930


Rev.:

Projektnr.: 1019198 | Dato: 2026-02-27 | Rev. Dato: | Mål: 1 : 50 | Side: J1-5

www.arteliagroup.dk | Fil:

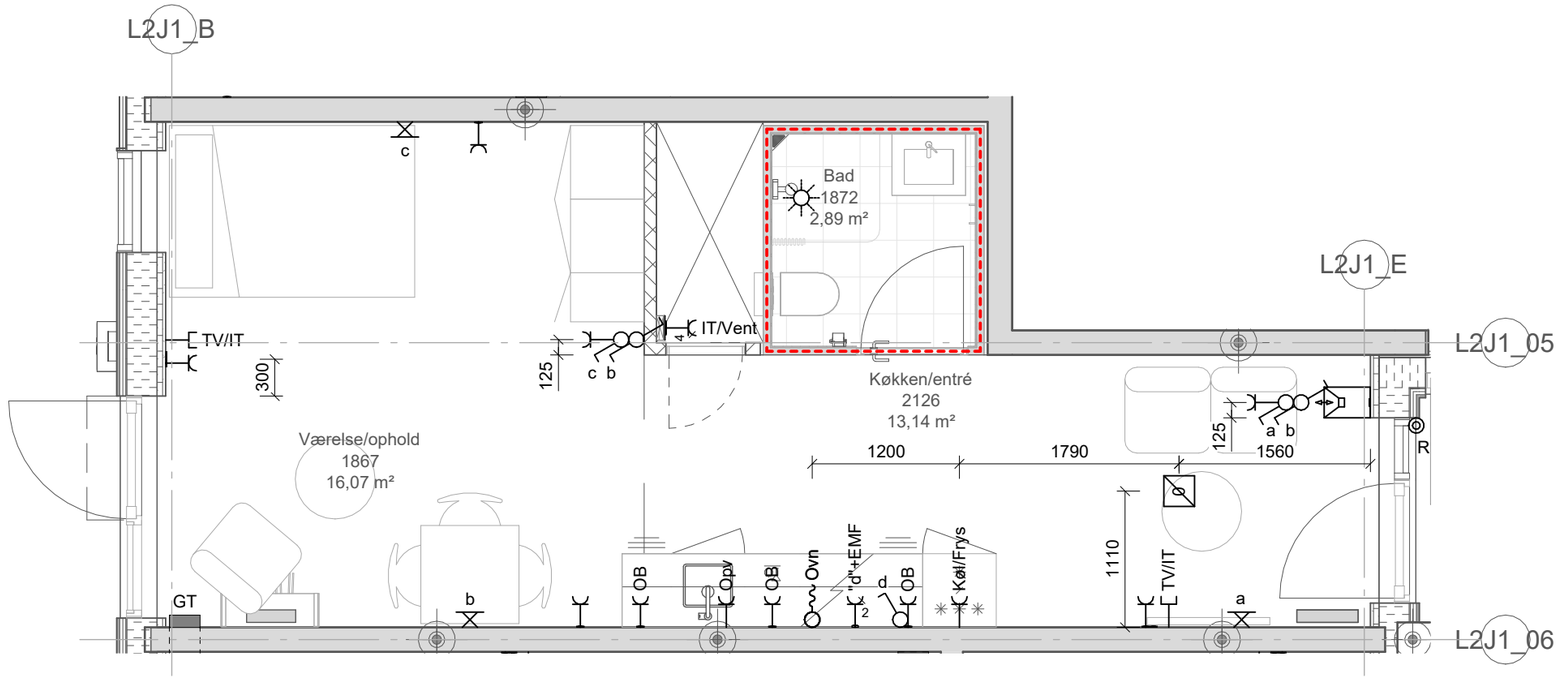

Projekt:	Stejlepladsen				
Tekst:	Elinstallationer - Byg J1 - Stueplan, Byg B ALT_1V_T30_ST - Side J1-6			Tegningsnr.:	Rev.:
			ISP2_K07_L2XX_H04_EXX_N930		
Projektnr.: 1019198	Dato: 2026-02-27	Rev. Dato:		Mål: 1 : 50	Side: J1-6
www.arteliagroup.dk	Fil:				

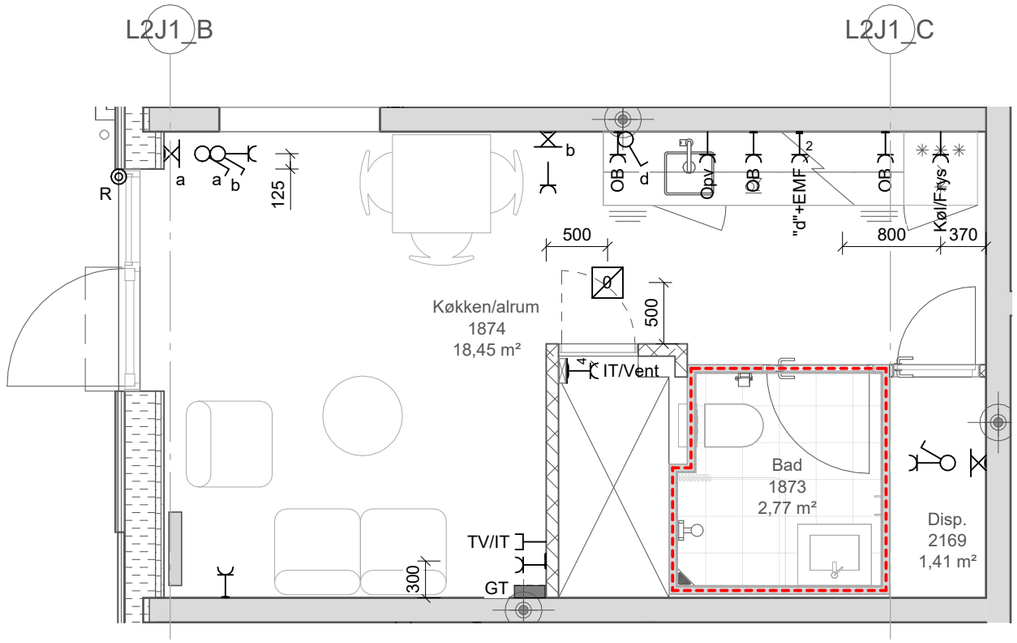

Projekt: Stejlepladsen


Tekst: Elinstallationer -
Byg J1 - Stueplan, Byg B
OPG_2V_T32_ST - Side J1-7

Tegningsnr.: ISP2_K07_L2XX_H04_EXX_N930

Rev.:

Projektnr.: 1019198 | Dato: 2026-02-27 | Rev. Dato: | Mål: 1 : 50 | Side: J1-7

www.arteliagroup.dk | Fil:

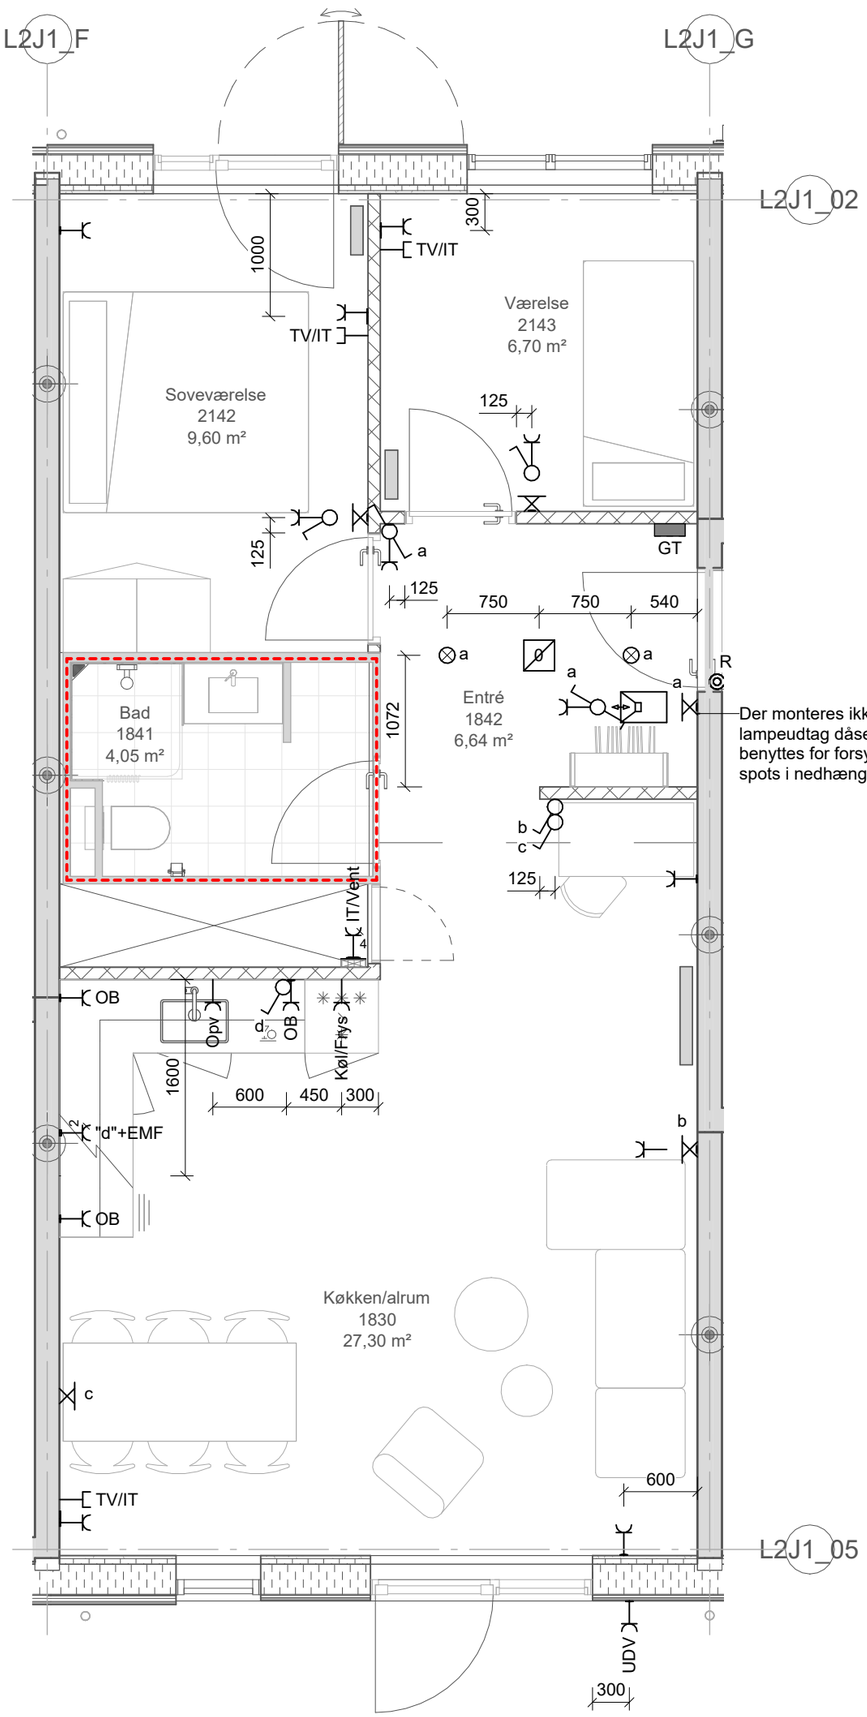

Projekt: Stejlepladsen


Tekst: Elinstallationer -
Byg J1 - Stueplan, Byg C
OPG_3V_T34_ST - Side J1-8

Tegningsnr.: ISP2_K07_L2XX_H04_EXX_N930

Rev.:

Projektnr.: 1019198 | Dato: 2026-02-27 | Rev. Dato: | Mål: 1 : 50 | Side: J1-8

www.arteliagroup.dk | Fil:

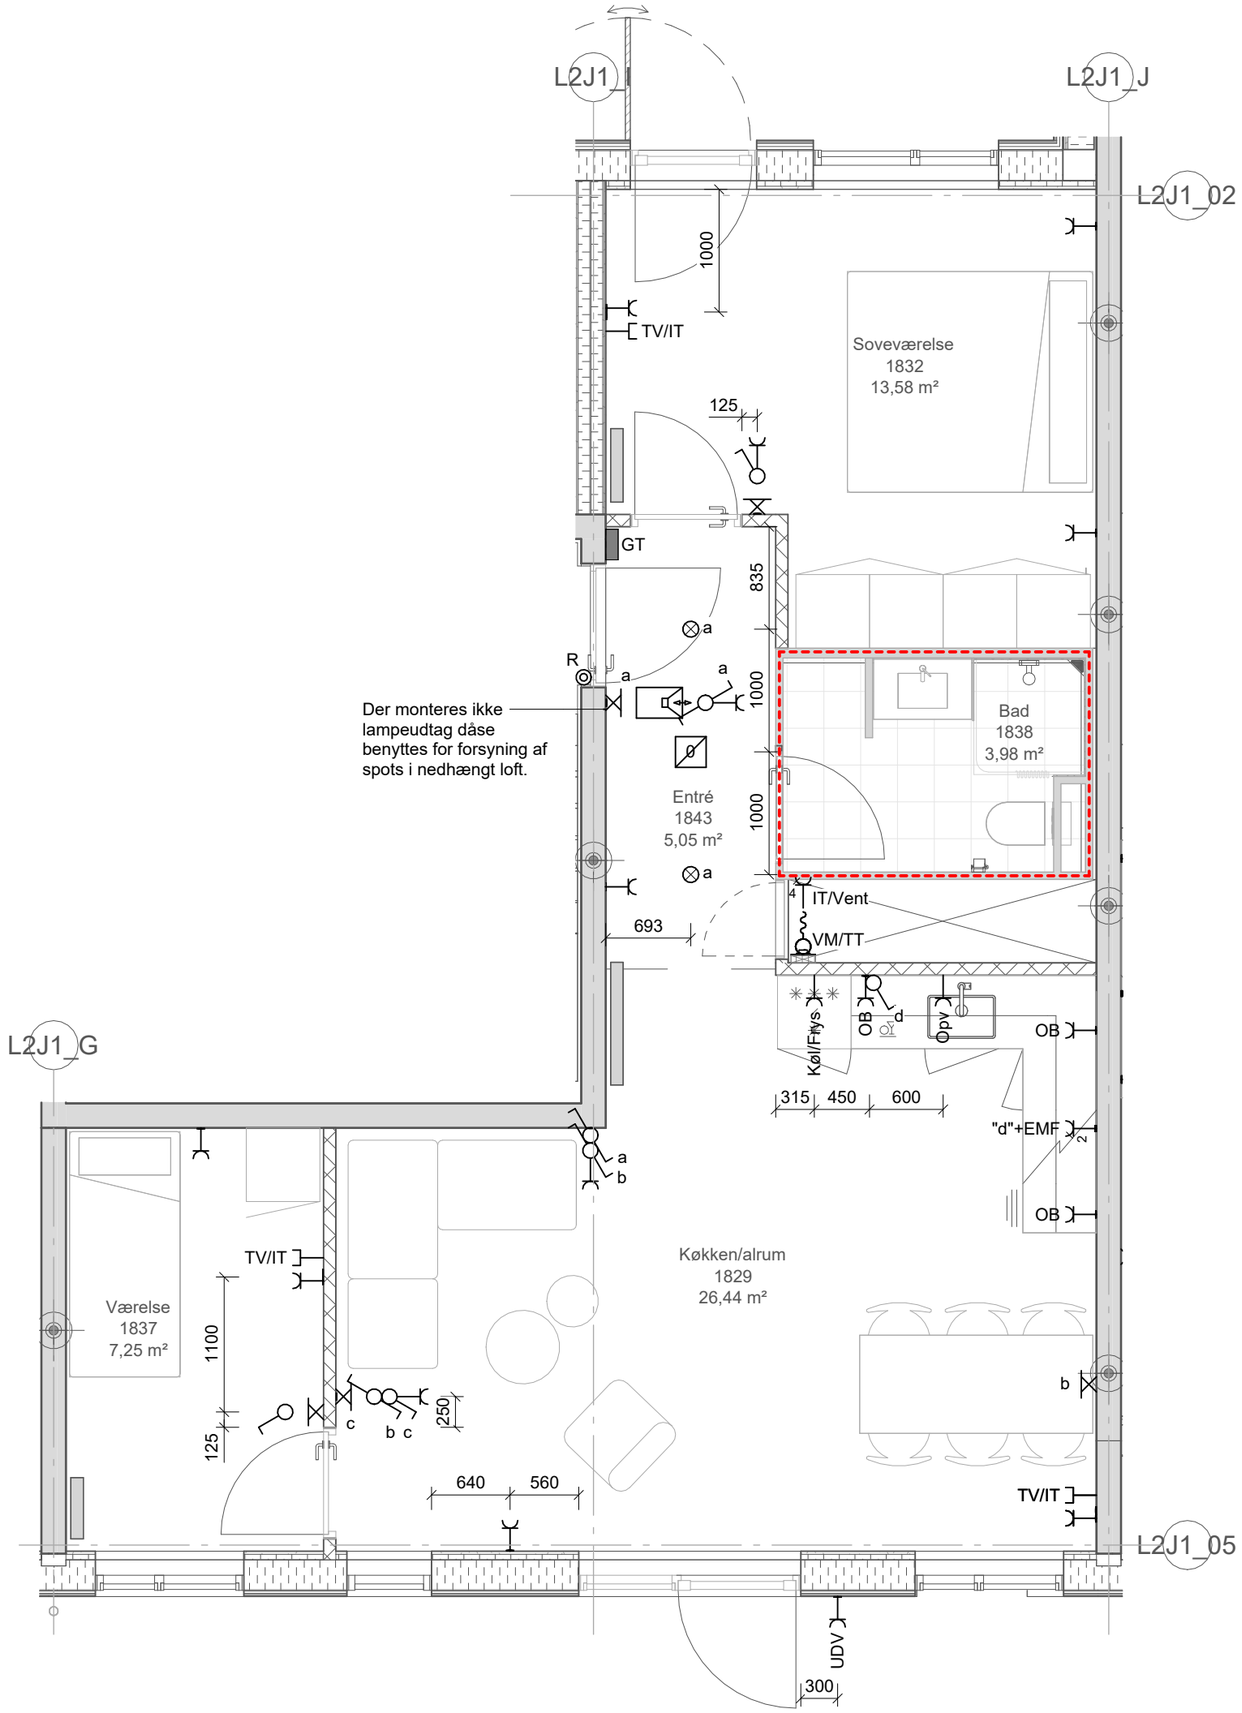

Projekt: Stejlepladsen

ARTELIA


Tekst: Elinstallationer -
Byg J1 - Stueplan, Byg C
OPG_3V_T35_ST - Side J1-9

Tegningsnr.: ISP2_K07_L2XX_H04_EXX_N930

Rev.:

Projektnr.: 1019198 | Dato: 2026-02-27 | Rev. Dato: | Mål: 1 : 50 | Side: J1-9

www.arteliagroup.dk | Fil:

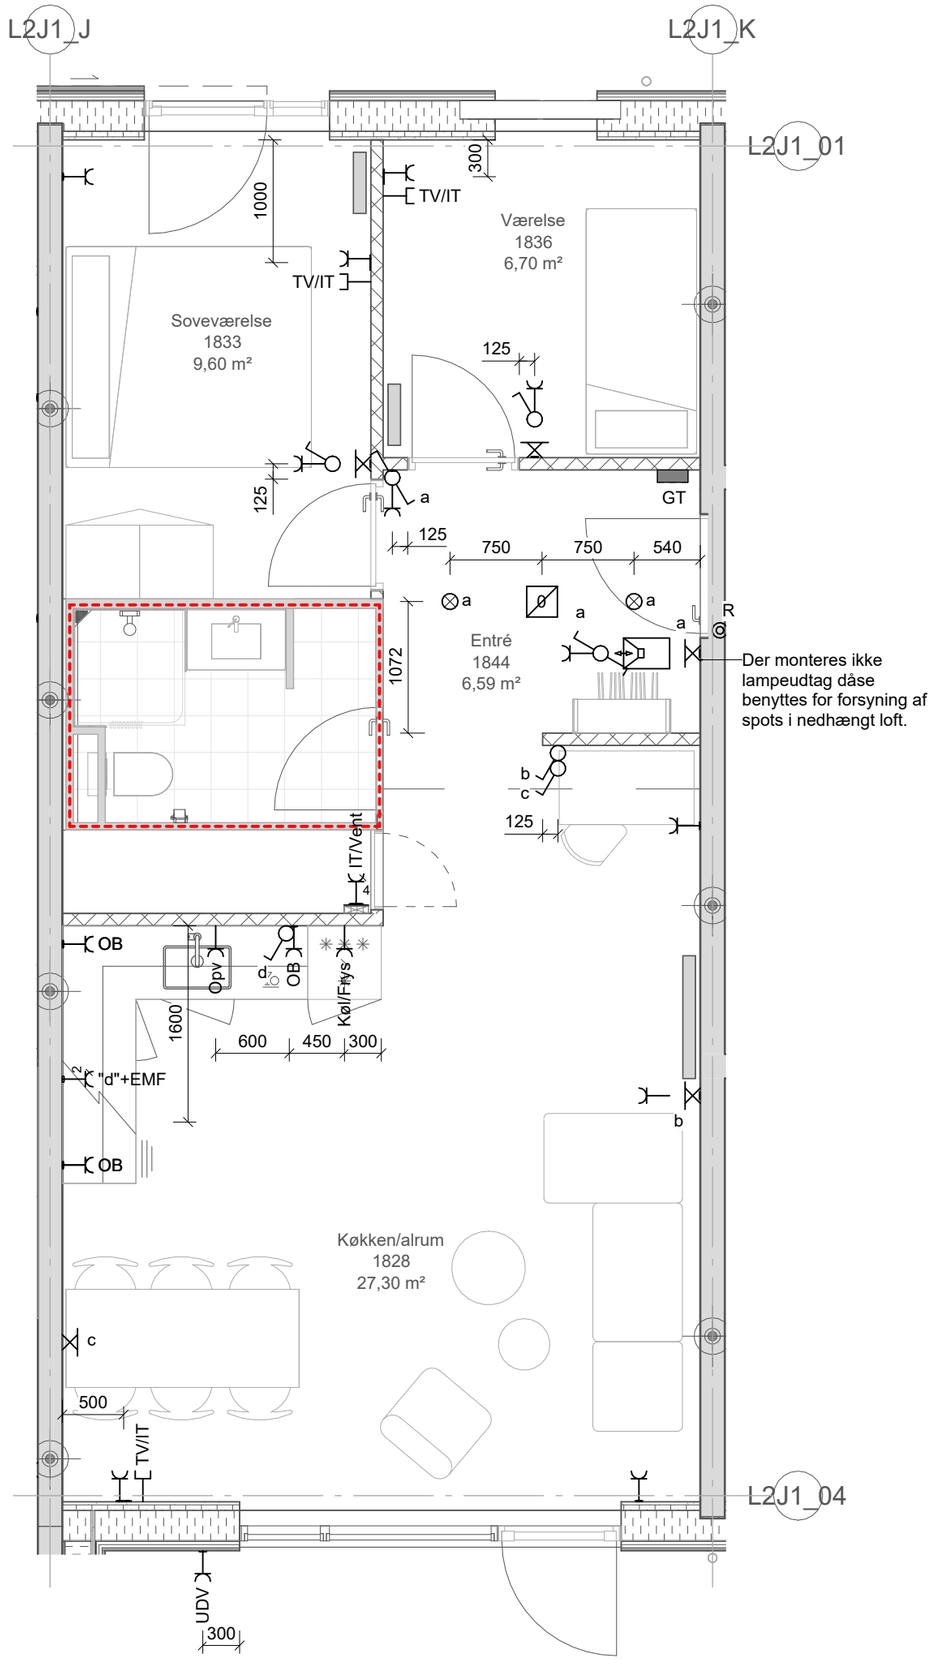

Projekt: Stejlepladsen


Tekst: Elinstallationer -
Byg J1 - Stueplan , Byg D
OPG_3V_T34_ST - Side J1-10

Tegningsnr.: ISP2_K07_L2XX_H04_EXX_N930

Rev.:

Projektnr.: 1019198 | Dato: 2026-02-27 | Rev. Dato: | Mål: 1 : 50 | Side: J1-10

www.arteliagroup.dk | Fil:

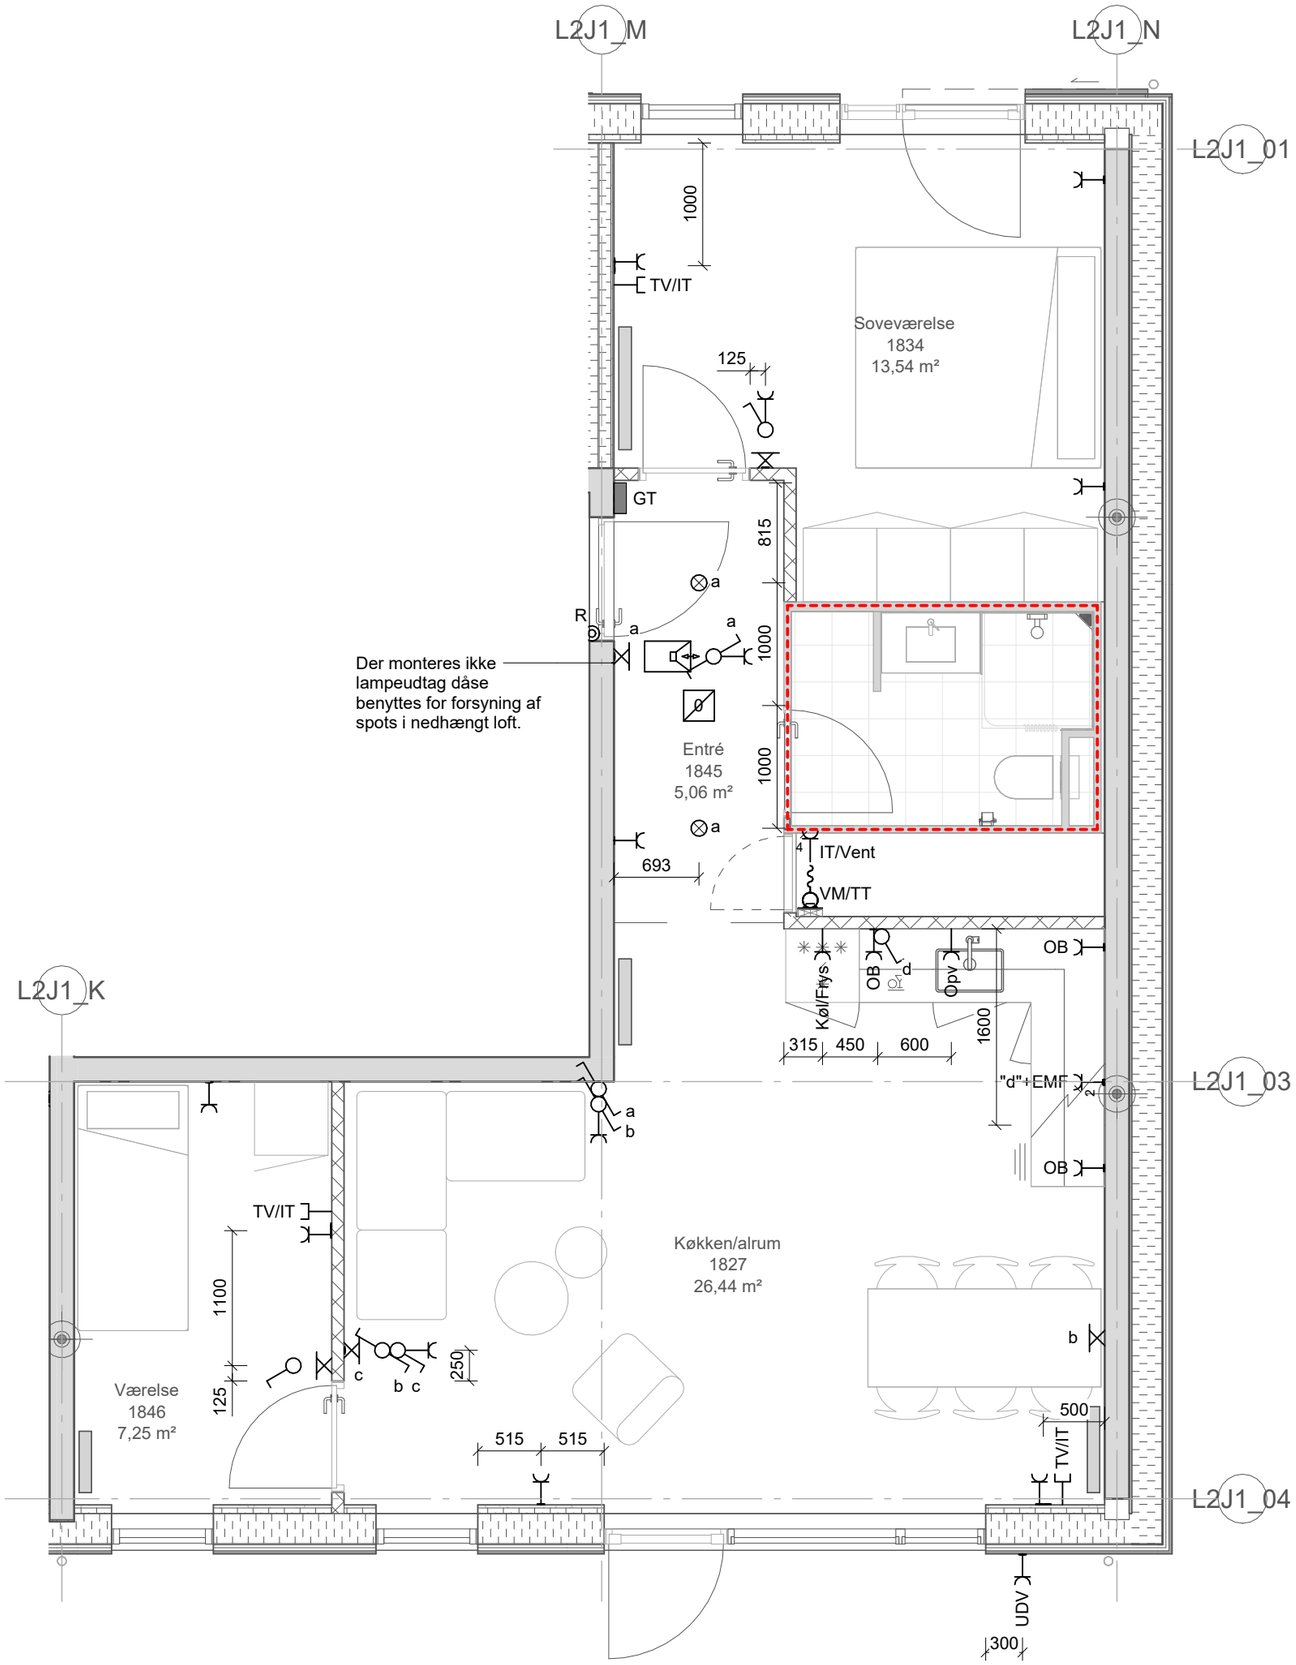

Projekt: Stejlepladsen


Tekst: Elinstallationer -
Byg J1 - Stueplan, Byg D
OPG_3V_T35_ST - Side J1-11

Tegningsnr.: ISP2_K07_L2XX_H04_EXX_N930

Rev.:

Projektnr.: 1019198 | Dato: 2026-02-27 | Rev. Dato: | Mål: 1 : 50 | Side: J1-11

www.arteliagroup.dk | Fil:

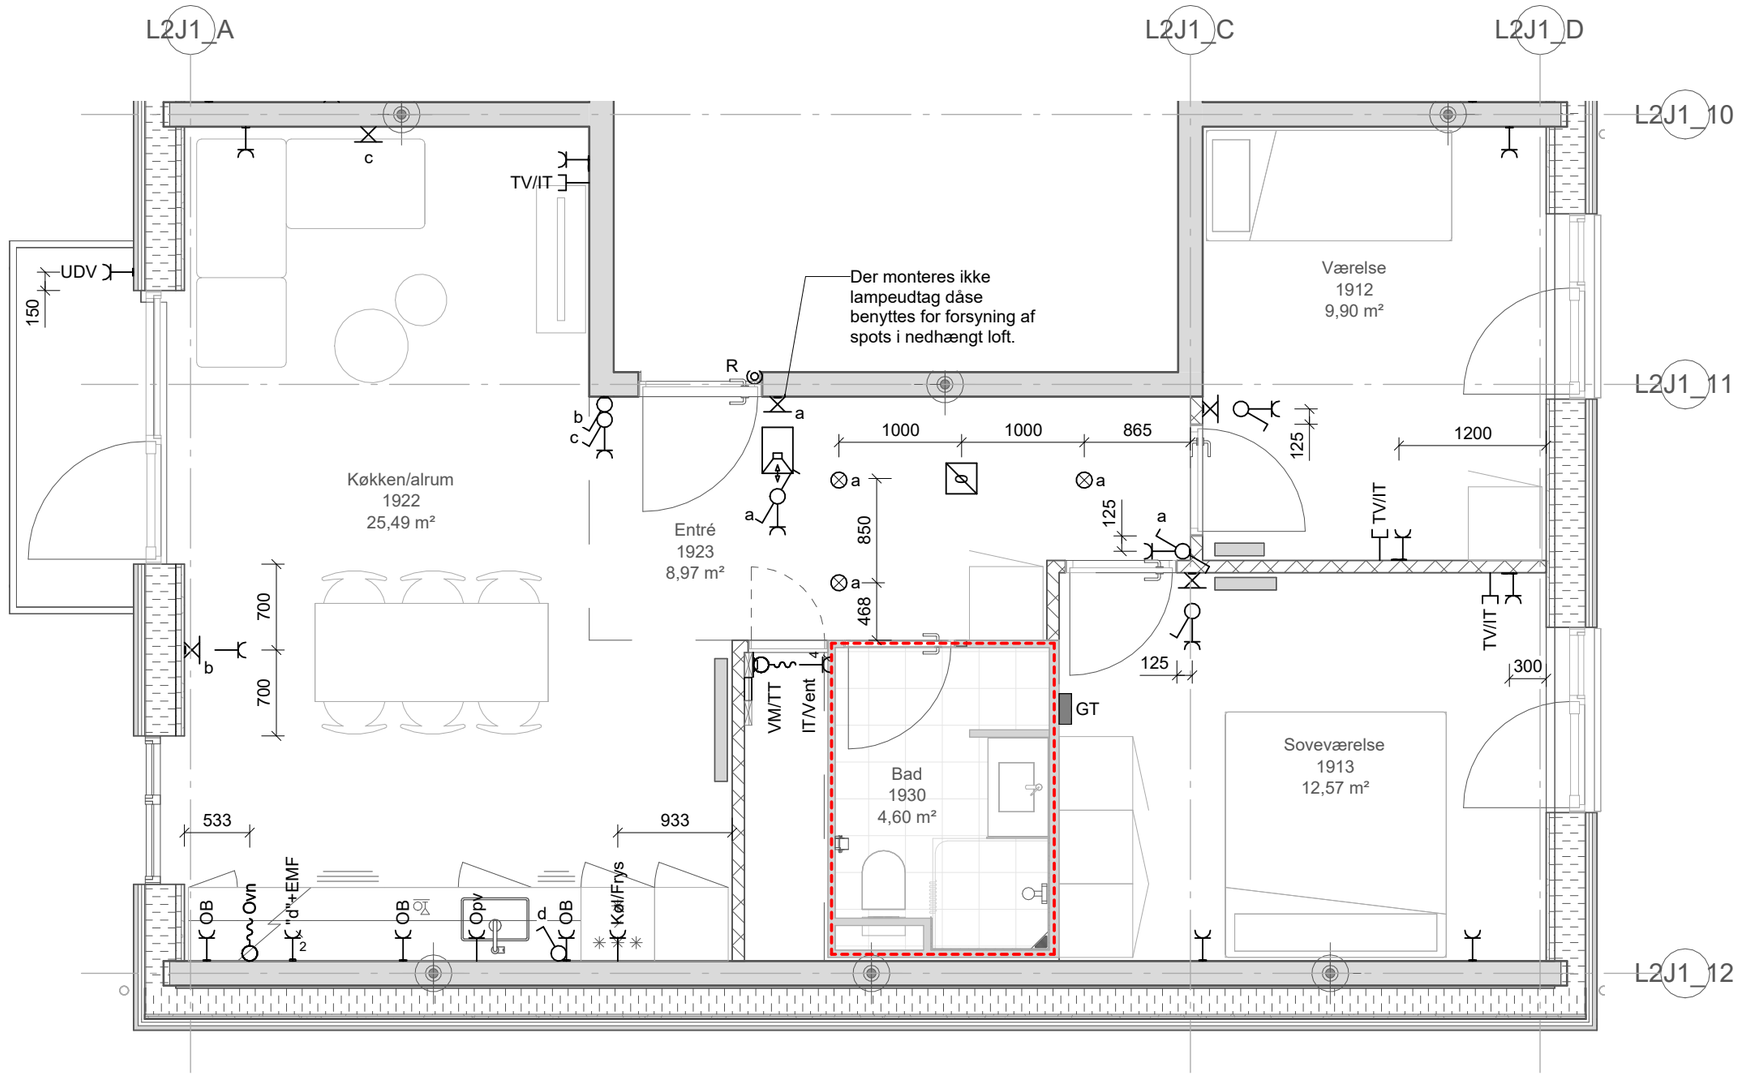

Projekt: Stejlepladsen


Tekst: Elinstallationer -
Byg J1 - 1. Sal, Byg A
OPG_3V_T30_S - Side J1-12

Tegningsnr.: ISP2_K07_L2XX_H04_EXX_N930

Rev.:

Projektnr.: 1019198 | Dato: 2026-02-27 | Rev. Dato: | Mål: 1 : 50 | Side: J1-12

www.arteliagroup.dk | Fil:

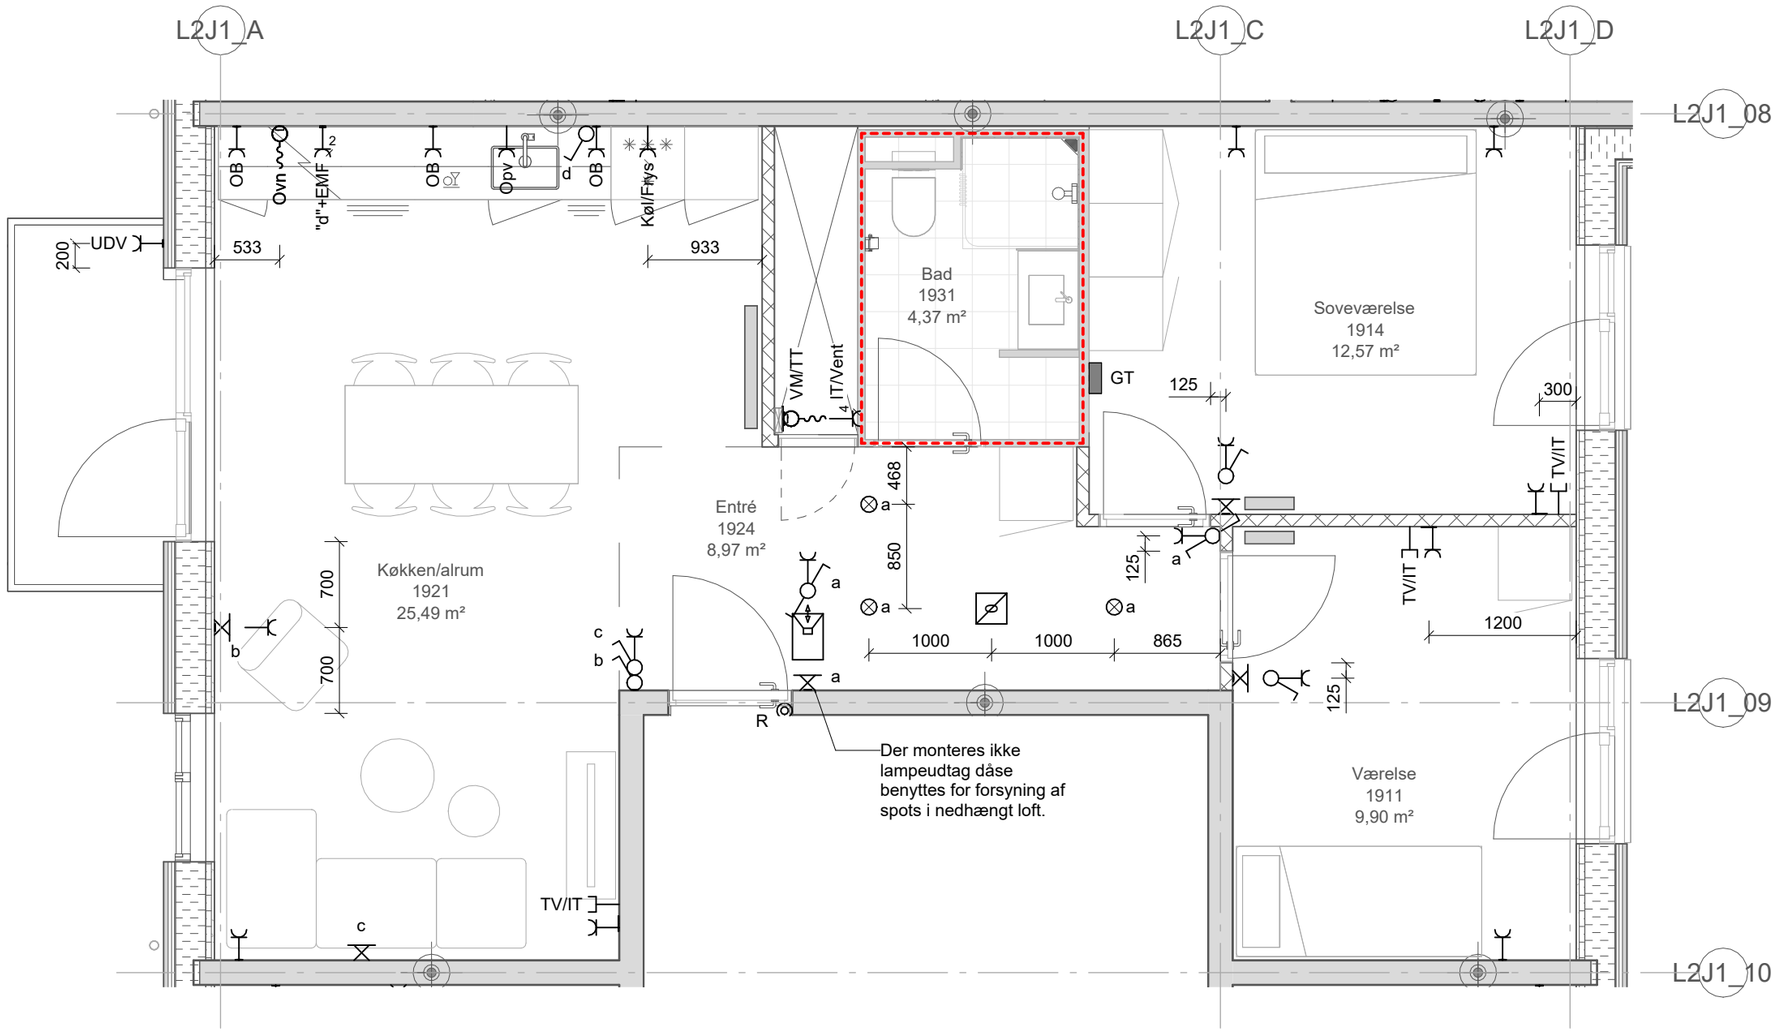

Projekt: Stejlepladsen


Tekst: Elinstallationer -
Byg J1 - 1. Sal, Byg A
OPG_3V_T30 - Side J1-13

Tegningsnr.: ISP2_K07_L2XX_H04_EXX_N930

Rev.:

Projektnr.: 1019198 | Dato: 2026-02-27 | Rev. Dato: | Mål: 1 : 50 | Side: J1-13

www.arteliagroup.dk | Fil:

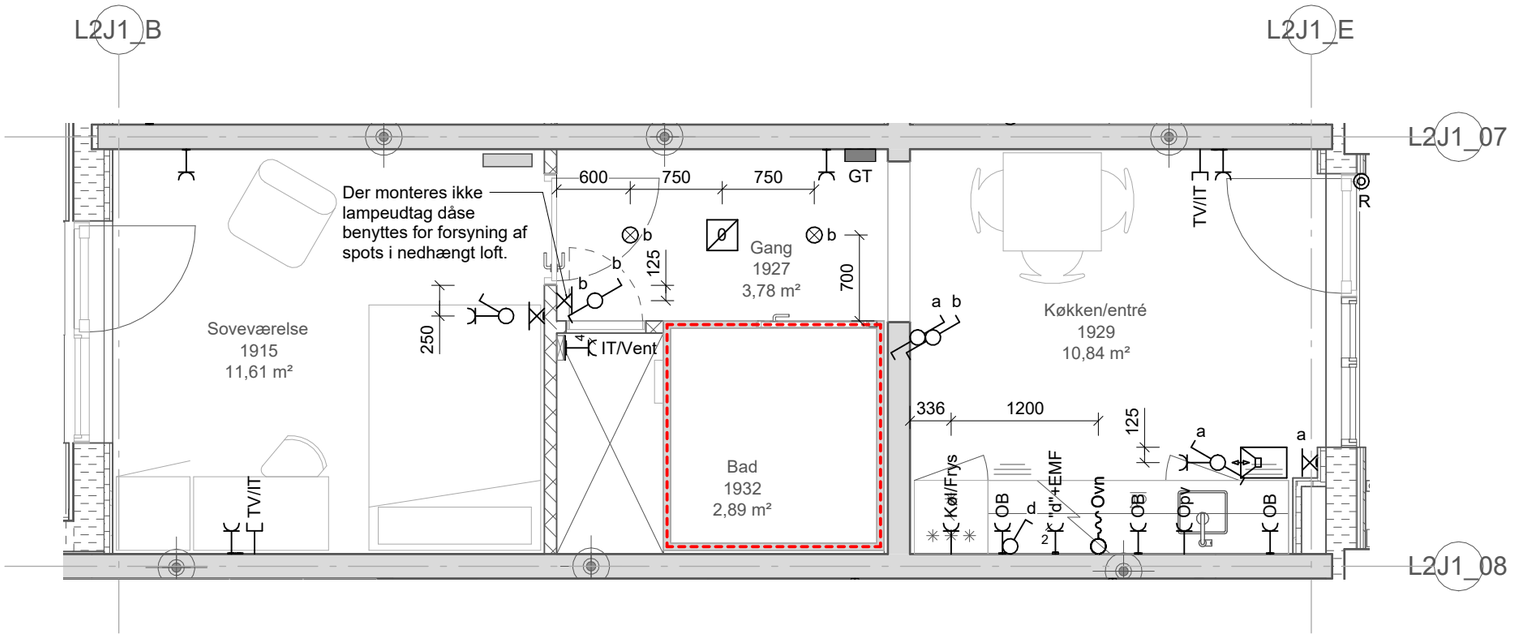

Projekt: Stejlepladsen


Tekst: Elinstallationer -
Byg J1 - 1. Sal, Byg B
ALT_1V_T31 - Side J1-14

Tegningsnr.: ISP2_K07_L2XX_H04_EXX_N930


Rev.:

Projektnr.: 1019198 | Dato: 2026-02-27 | Rev. Dato: | Mål: 1 : 50 | Side: J1-14

www.arteliagroup.dk | Fil:

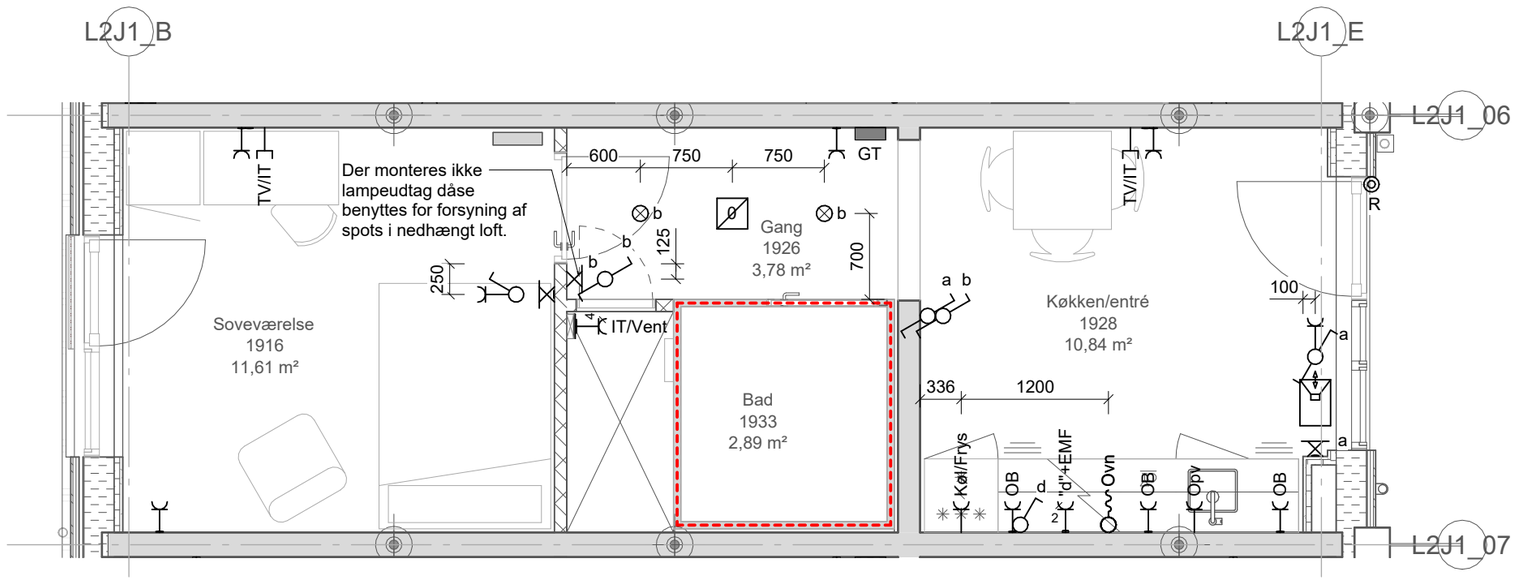

Projekt:	Stejlepladsen				
Tekst:	Elinstallationer - Byg J1 - 1. Sal, Byg B ALT_1V_T31.1 - Side J1-15			Tegningsnr.:	Rev.:
				ISP2_K07_L2XX_H04_EXX_N930	
Projektnr.: 1019198	Dato: 2026-02-27	Rev. Dato:		Mål: 1 : 50	Side: J1-15
www.arteliagroup.dk	Fil:				

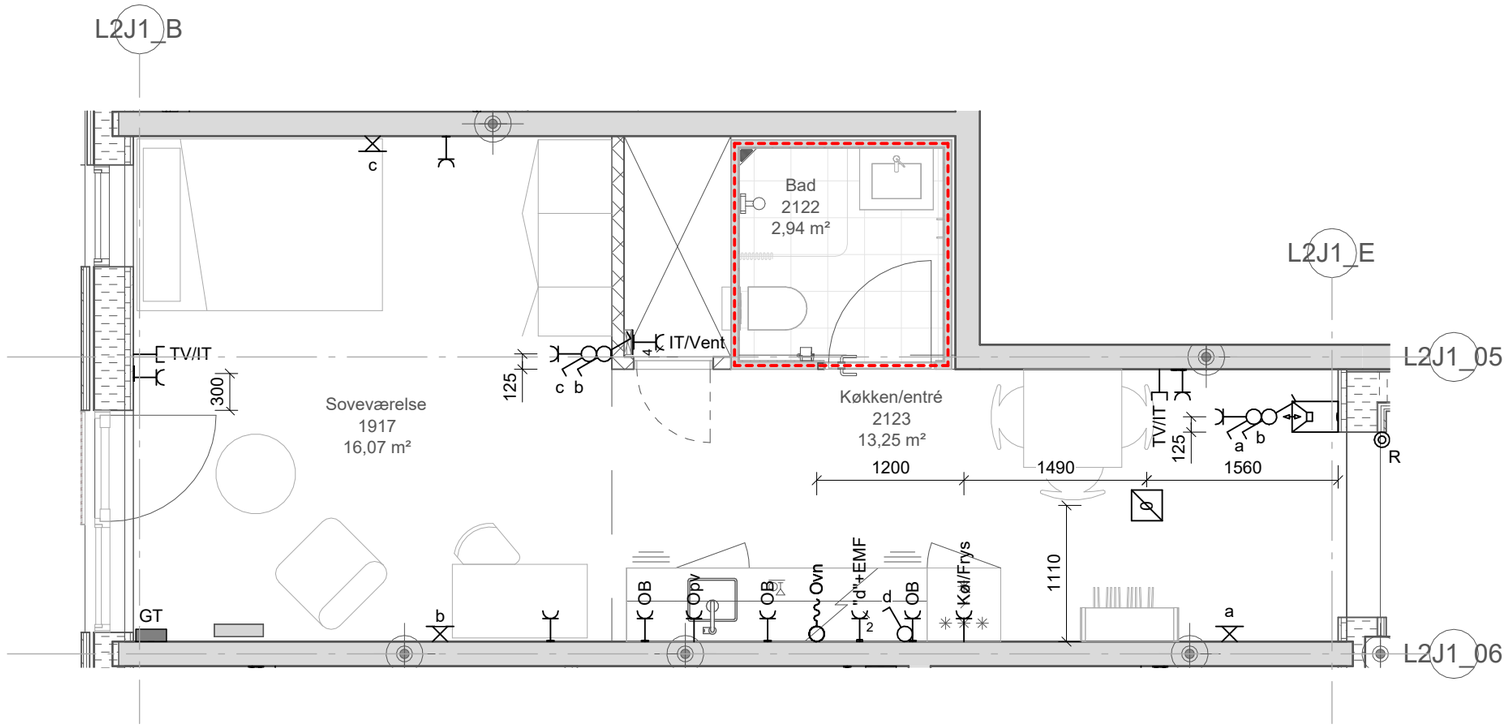

Projekt: Stejlepladsen


Tekst: Elinstallationer -
Byg J1 - 1. Sal, Byg B
ALT_1V_T30 - Side J1-16

Tegningsnr.: ISP2_K07_L2XX_H04_EXX_N930


Rev.:

Projektnr.: 1019198 | Dato: 2026-02-27 | Rev. Dato: | Mål: 1 : 50 | Side: J1-16


www.arteliagroup.dk | Fil:

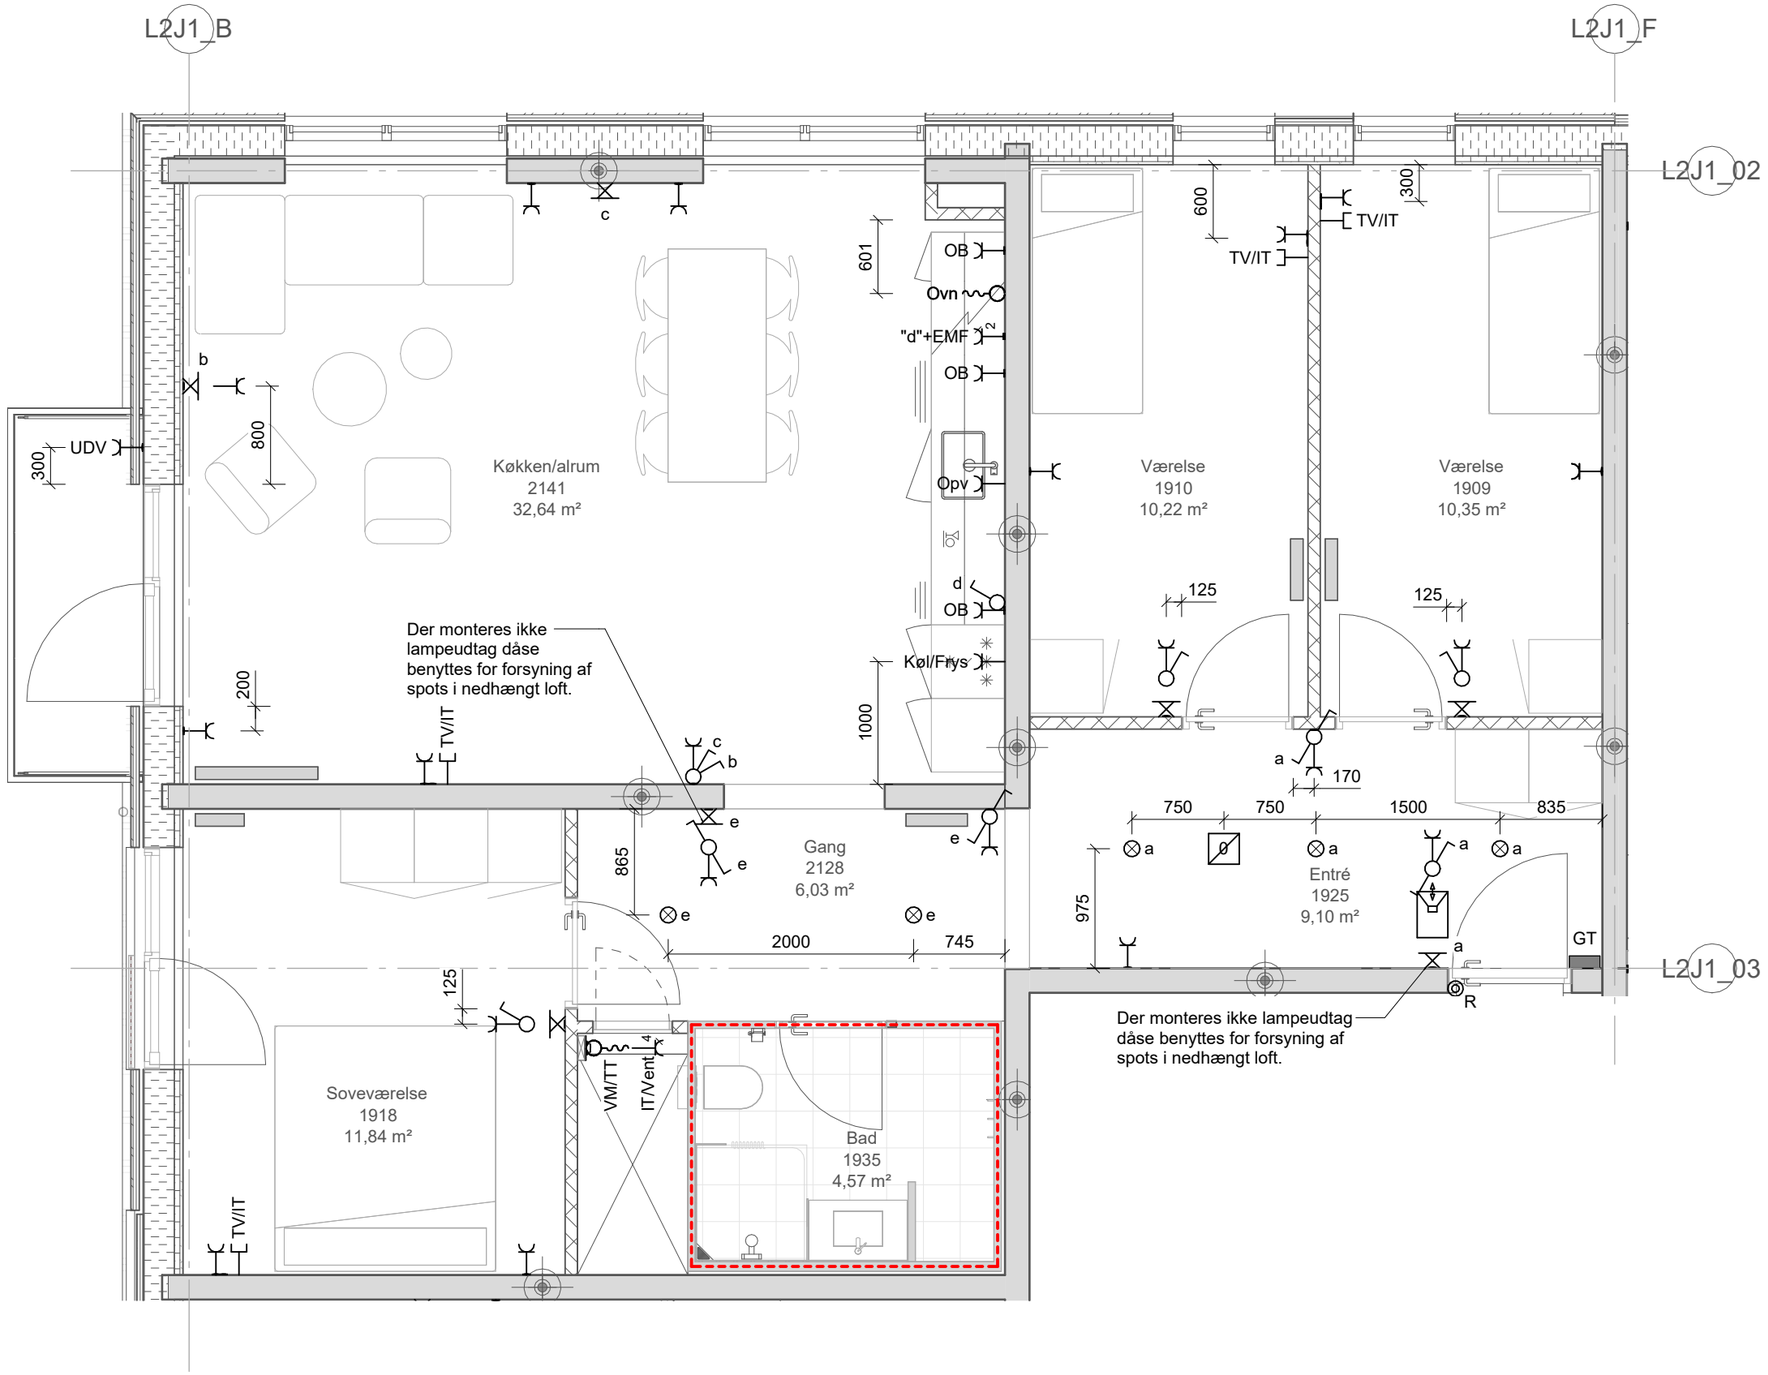

Projekt:	Stejlepladsen				
Tekst:	Elinstallationer - Byg J1 - 1. Sal, Byg B OPG_4V_T31 - Side J1-17			Tegningsnr.:	Rev.:
			ISP2_K07_L2XX_H04_EXX_N930		
Projektnr.: 1019198	Dato: 2026-02-27	Rev. Dato:		Mål: 1 : 50	Side: J1-17
www.arteliagroup.dk	Fil:				

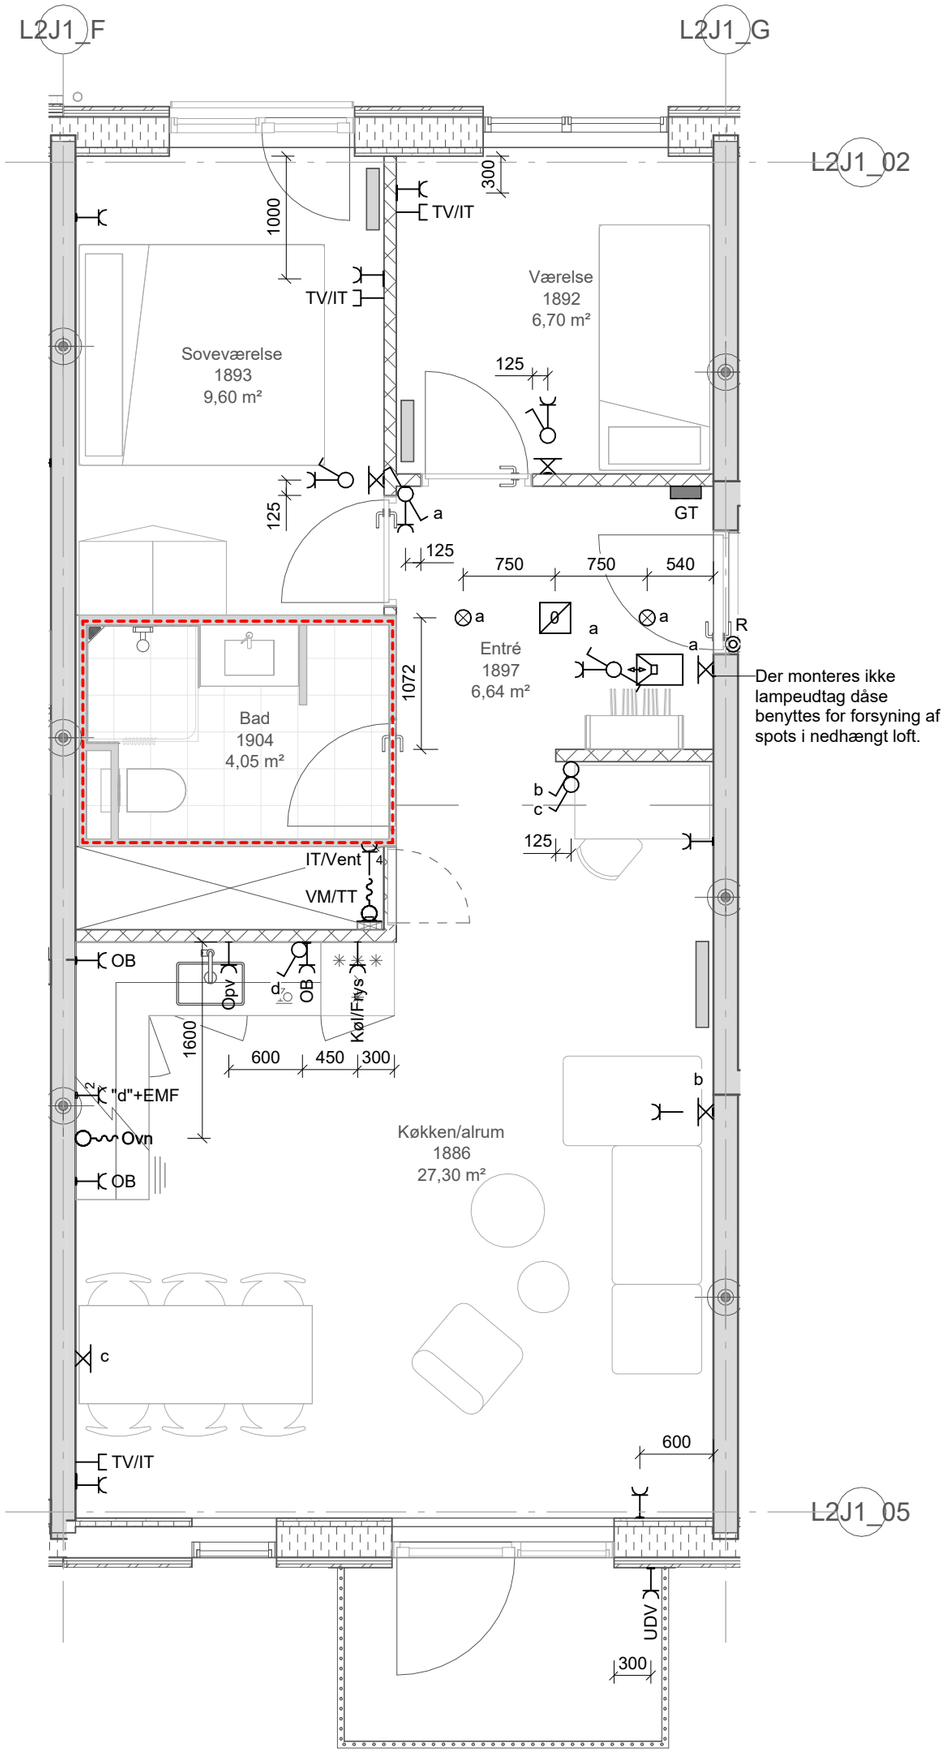

Projekt:	Stejlepladsen				
Tekst:	Elinstallationer - Byg J1 - 1. Sal, Byg C OPG_3V_T34 - Side J1-18			Tegningsnr.:	Rev.:
				ISP2_K07_L2XX_H04_EXX_N930	
Projektnr.: 1019198	Dato: 2026-02-27	Rev. Dato:		Mål: 1 : 50	Side: J1-18
www.arteliagroup.dk	Fil:				

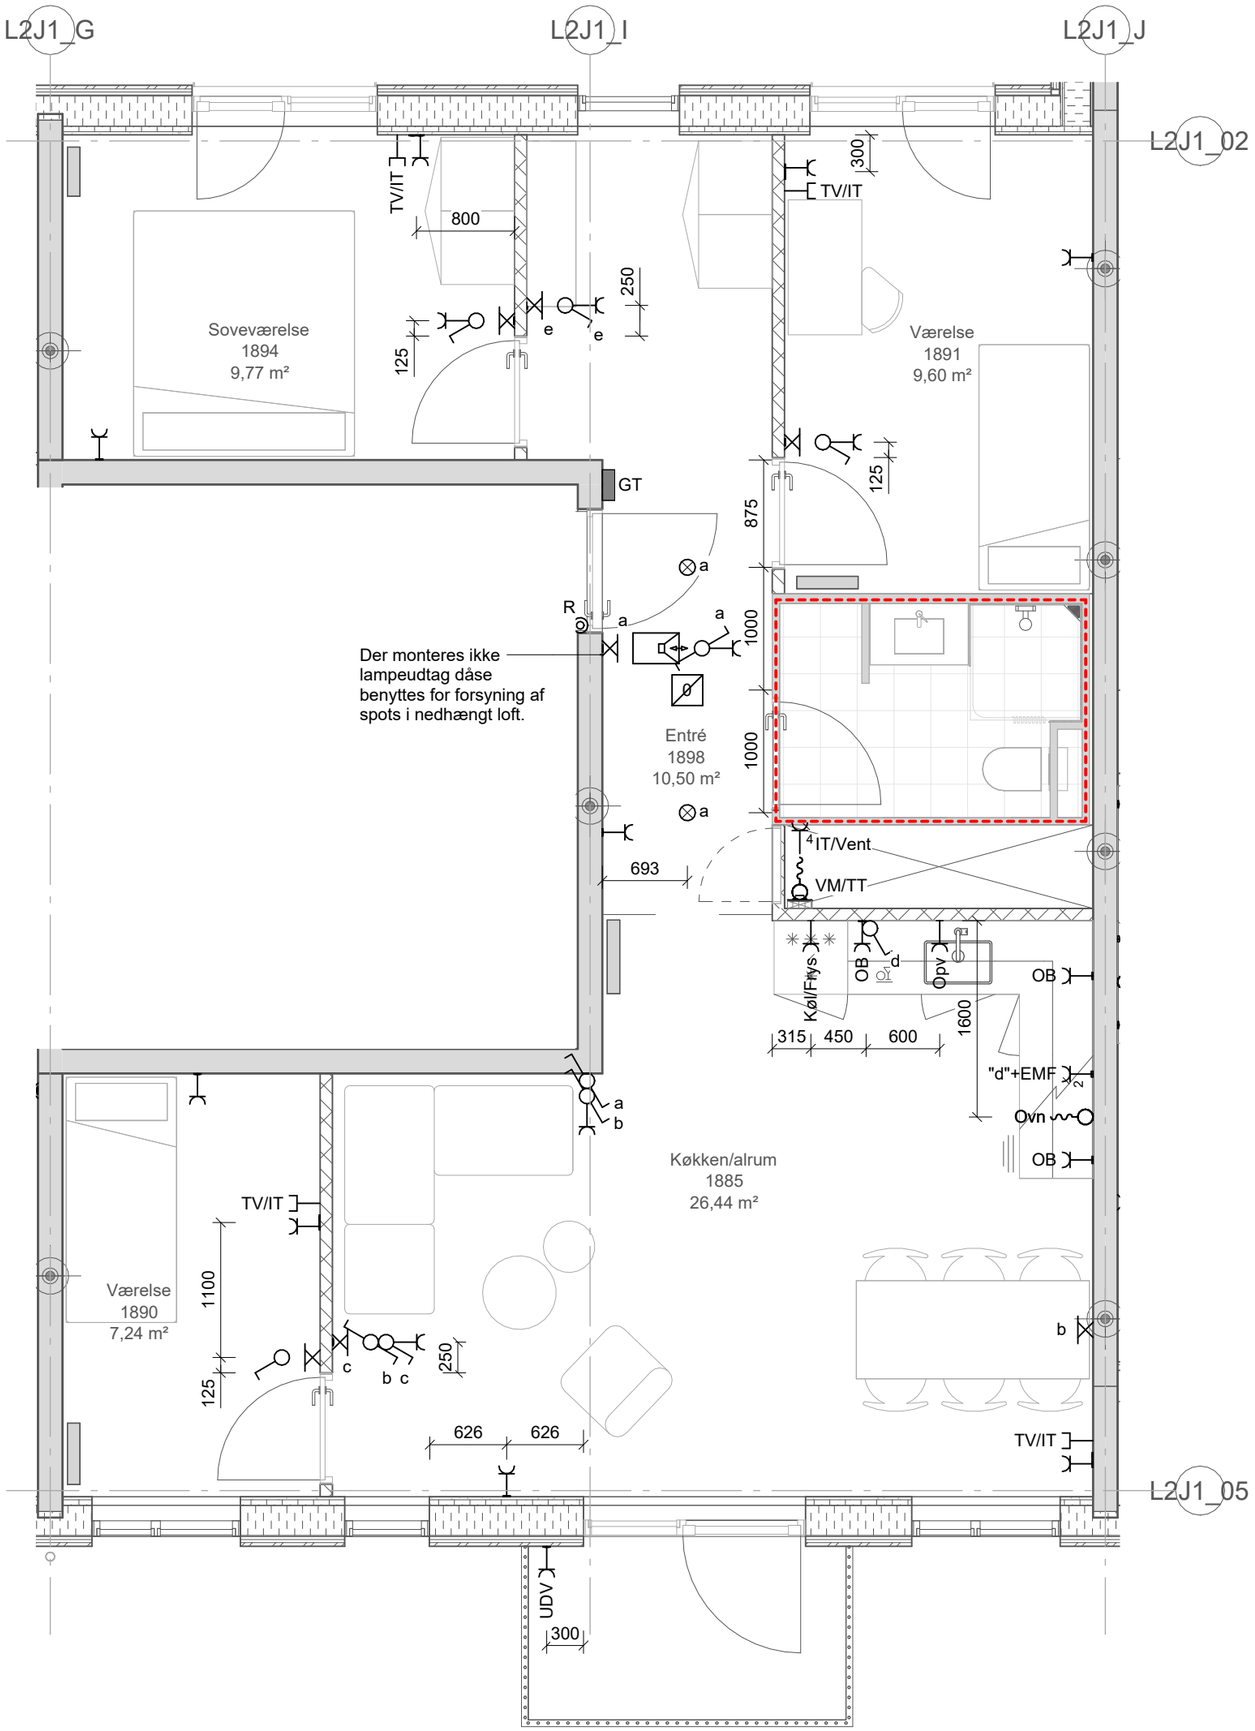

Projekt: Stejlepladsen


Tekst: Elinstallationer -
Byg J1 - 1. Sal, Byg C
OPG_4V_T32 - Side J1-19

Tegningsnr.: ISP2_K07_L2XX_H04_EXX_N930

Rev.:

Projektnr.: 1019198 | Dato: 2026-02-27 | Rev. Dato: | Mål: 1 : 50 | Side: J1-19

www.arteliagroup.dk | Fil:

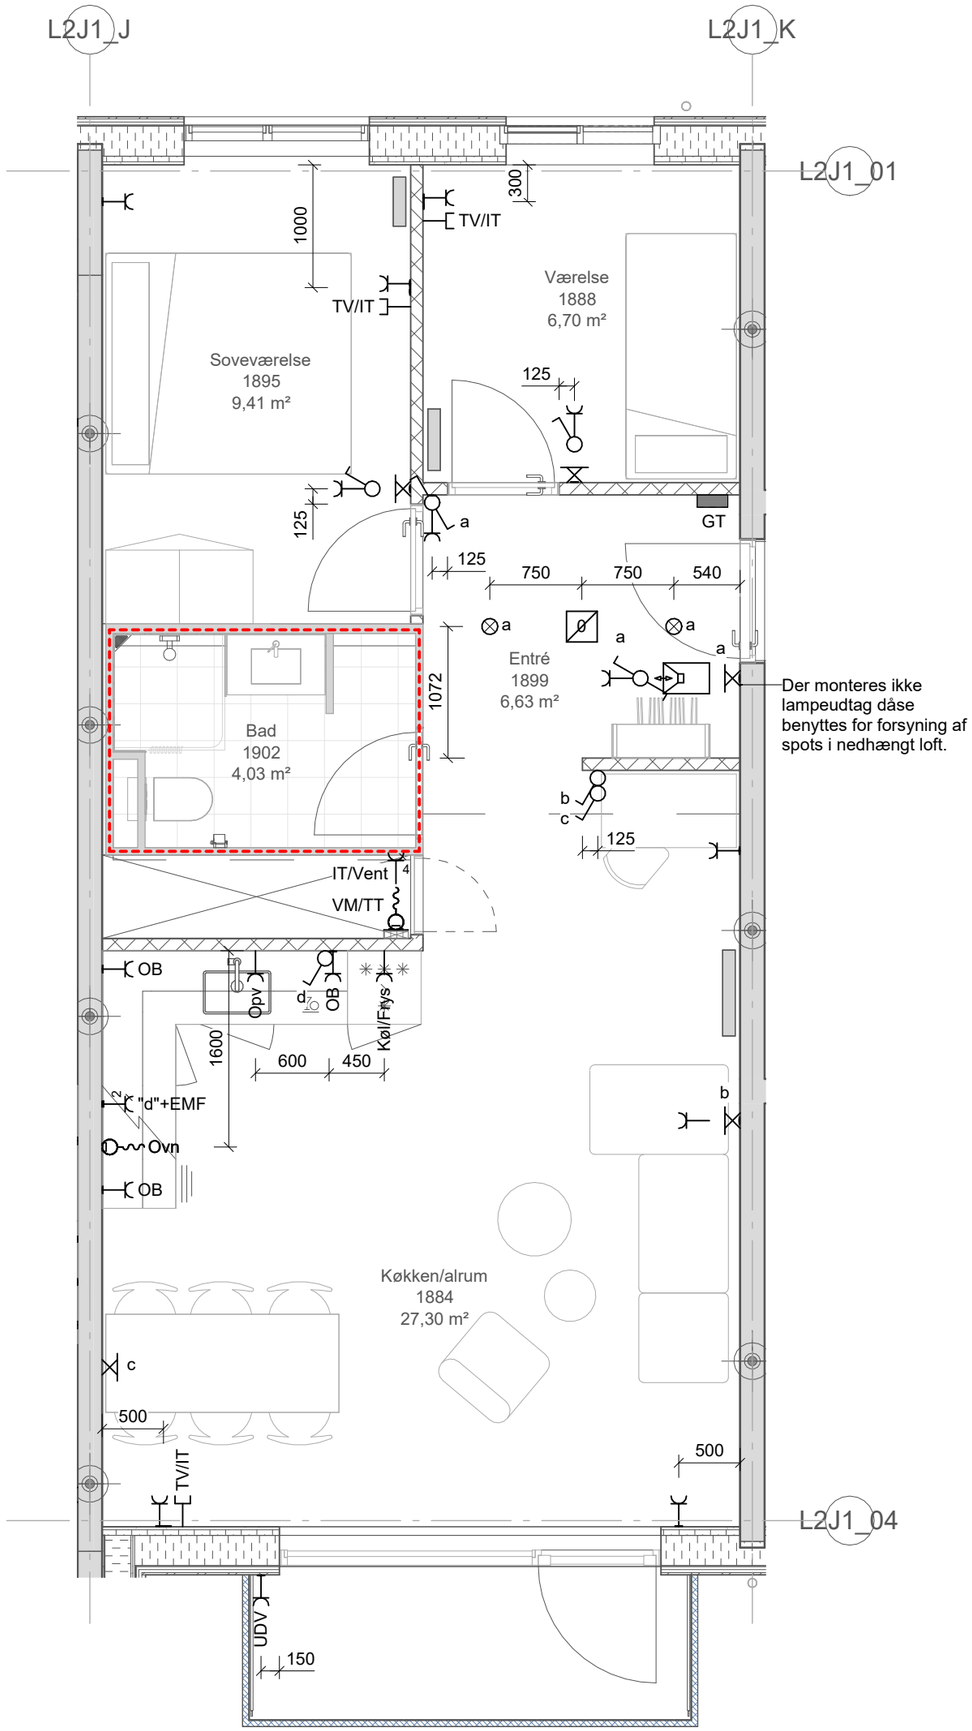

Projekt: Stejlepladsen


Tekst: Elinstallationer -
Byg J1 - 1. Sal, Byg D
OPG_3V_T34.a - Side J1-20

Tegningsnr.: ISP2_K07_L2XX_H04_EXX_N930


Rev.:

Projektnr.: 1019198 | Dato: 2026-02-27 | Rev. Dato: | Mål: 1 : 50 | Side: J1-20

www.arteliagroup.dk | Fil:

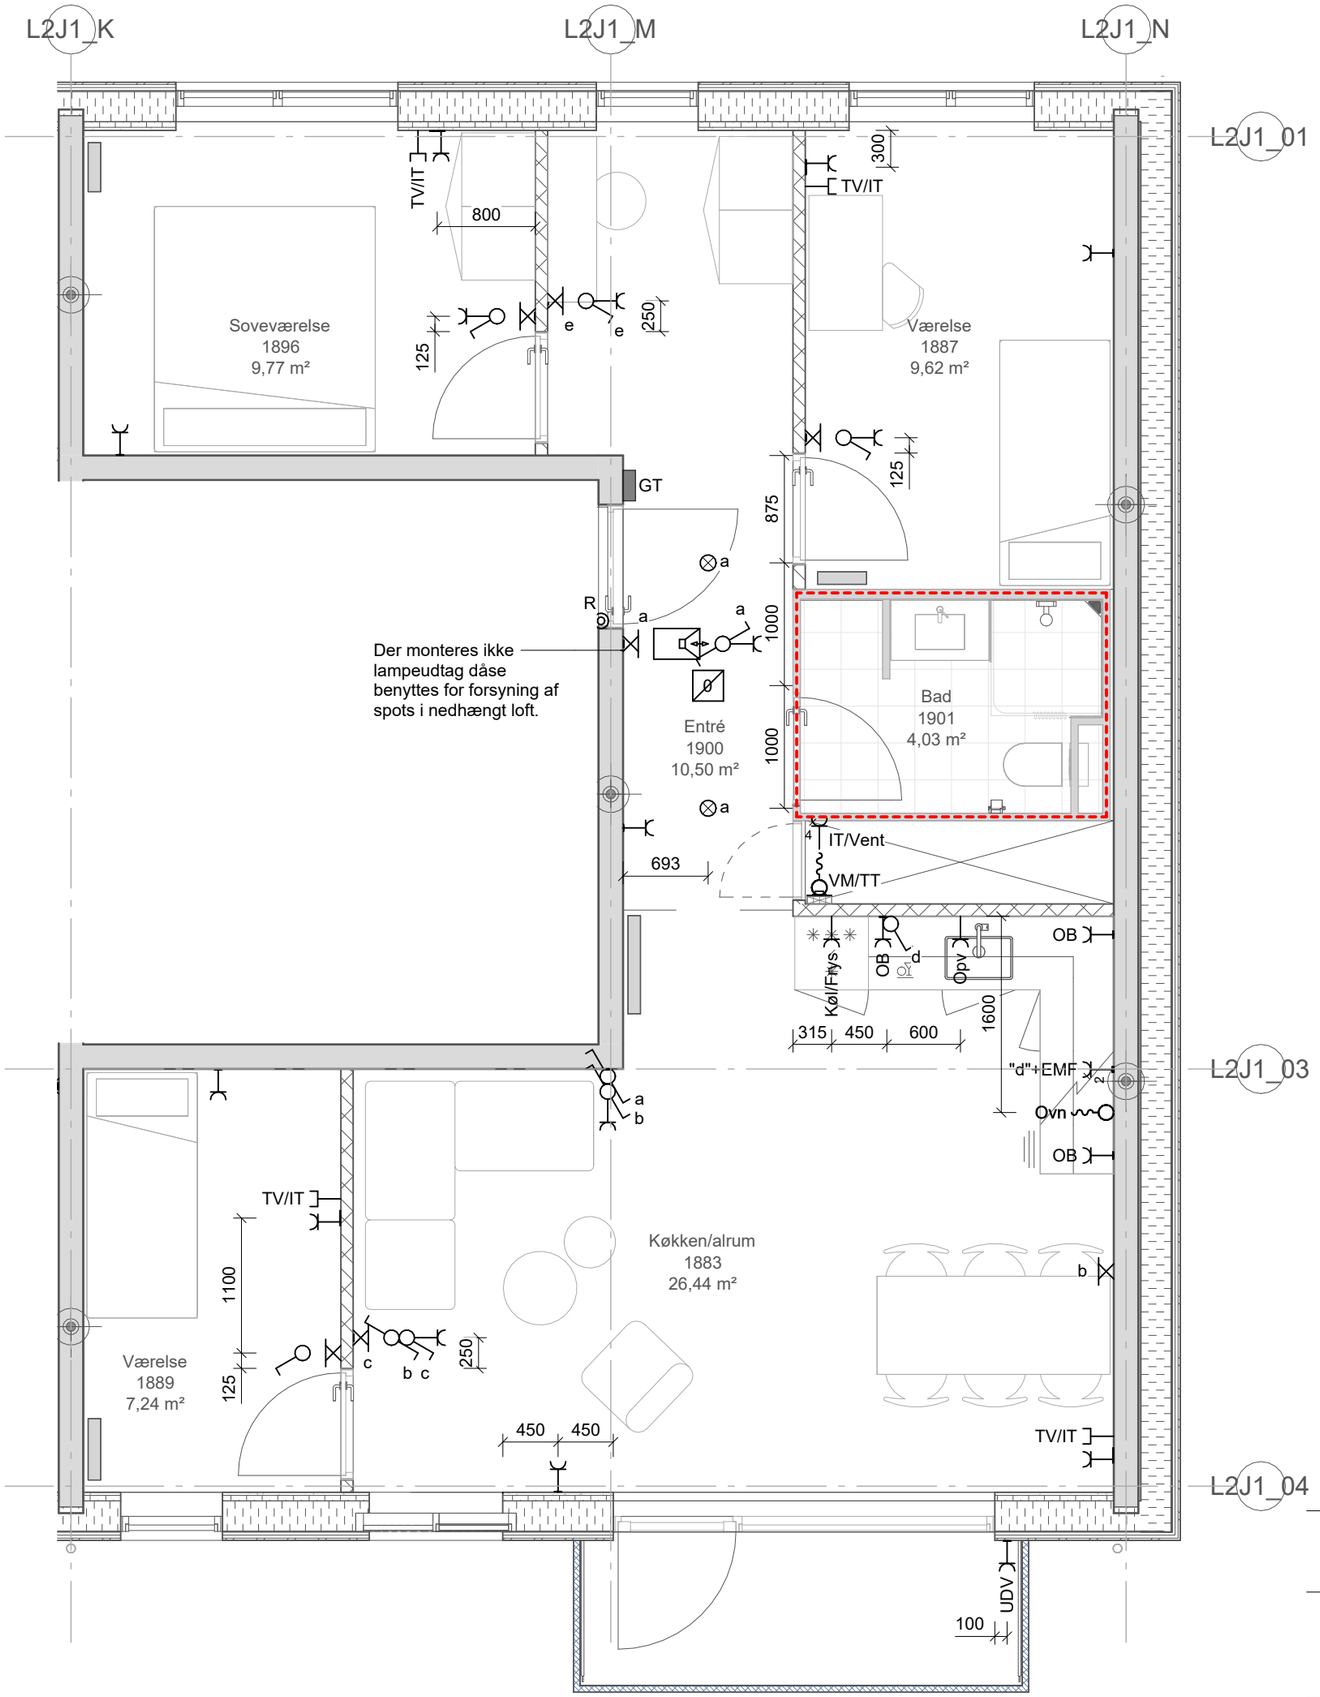

Projekt:	Stejlepladsen				
Tekst:	Elinstallationer - Byg J1 - 1. Sal, Byg D OPG_4V_T32.a - Side J1-21			Tegningsnr.:	Rev.:
			ISP2_K07_L2XX_H04_EXX_N930		
Projektnr.: 1019198	Dato: 2026-02-27	Rev. Dato:		Mål: 1 : 50	Side: J1-21
www.arteliagroup.dk	Fil:				

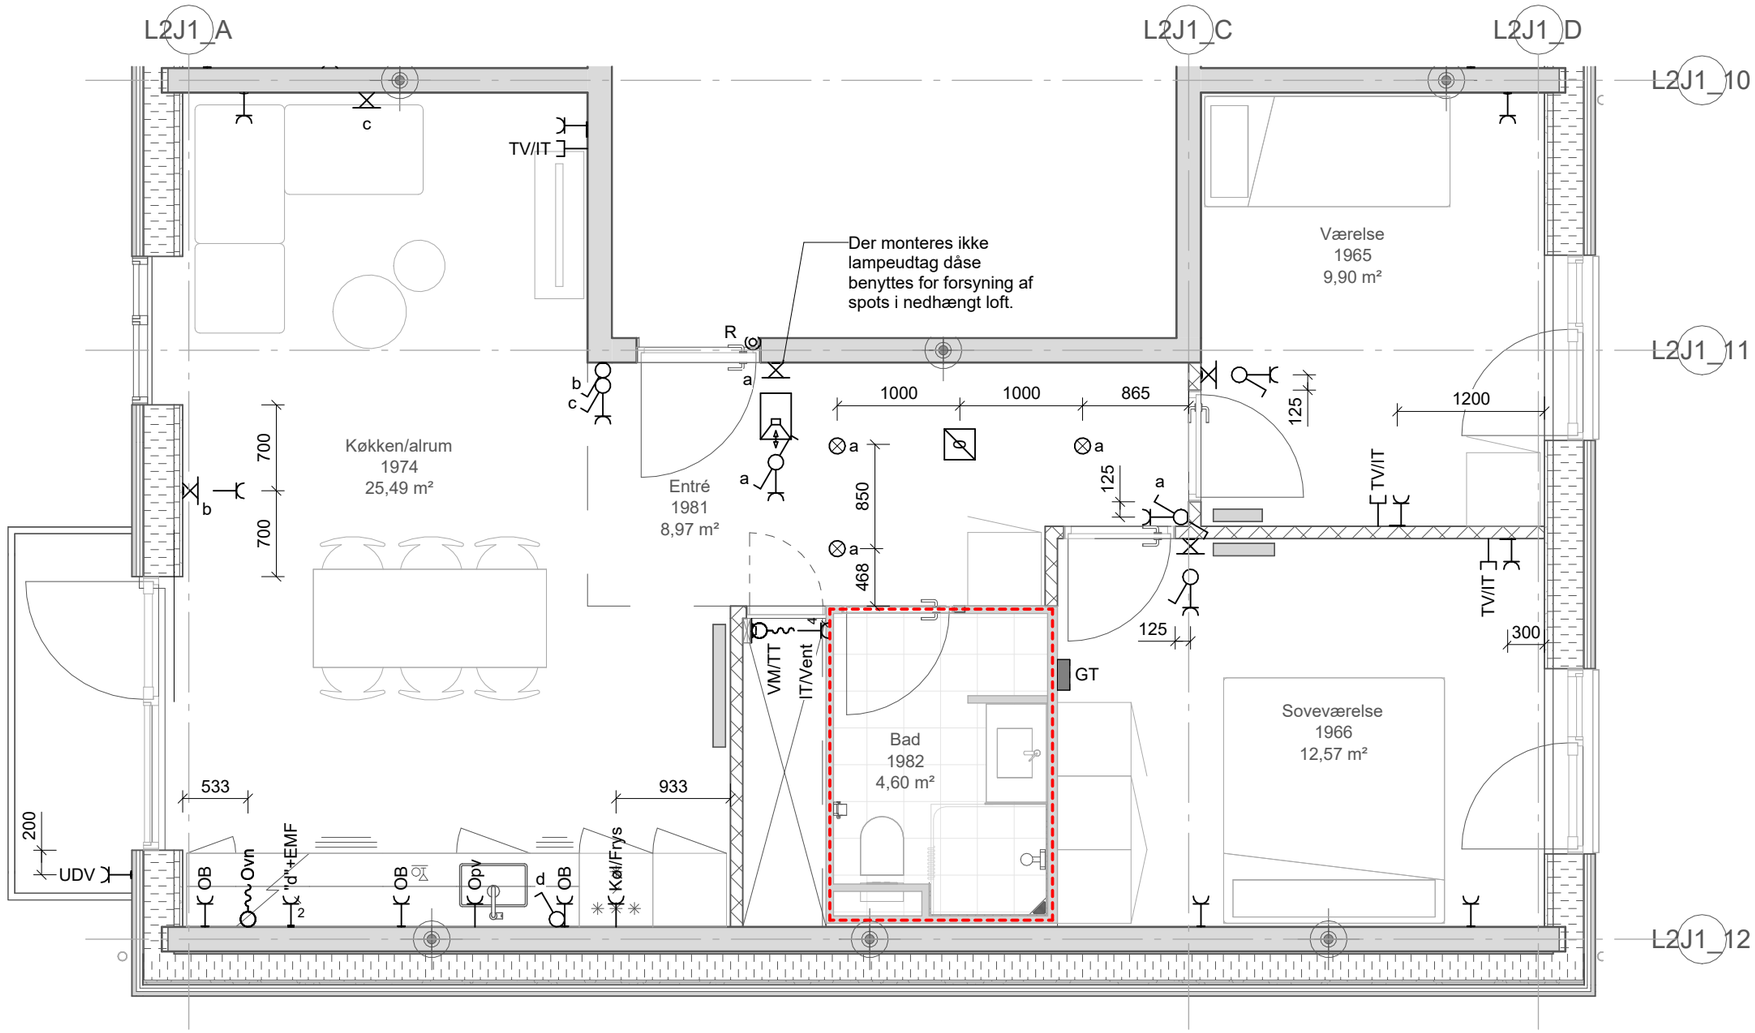

Projekt: Stejlepladsen


Tekst: Elinstallationer -
Byg J1 - 2. Sal, Byg A
OPG_3V_T30_S - Side J1-22

Tegningsnr.: ISP2_K07_L2XX_H04_EXX_N930

Rev.:

Projektnr.: 1019198 | Dato: 2026-02-27 | Rev. Dato: | Mål: 1 : 50 | Side: J1-22

www.arteliagroup.dk | Fil:

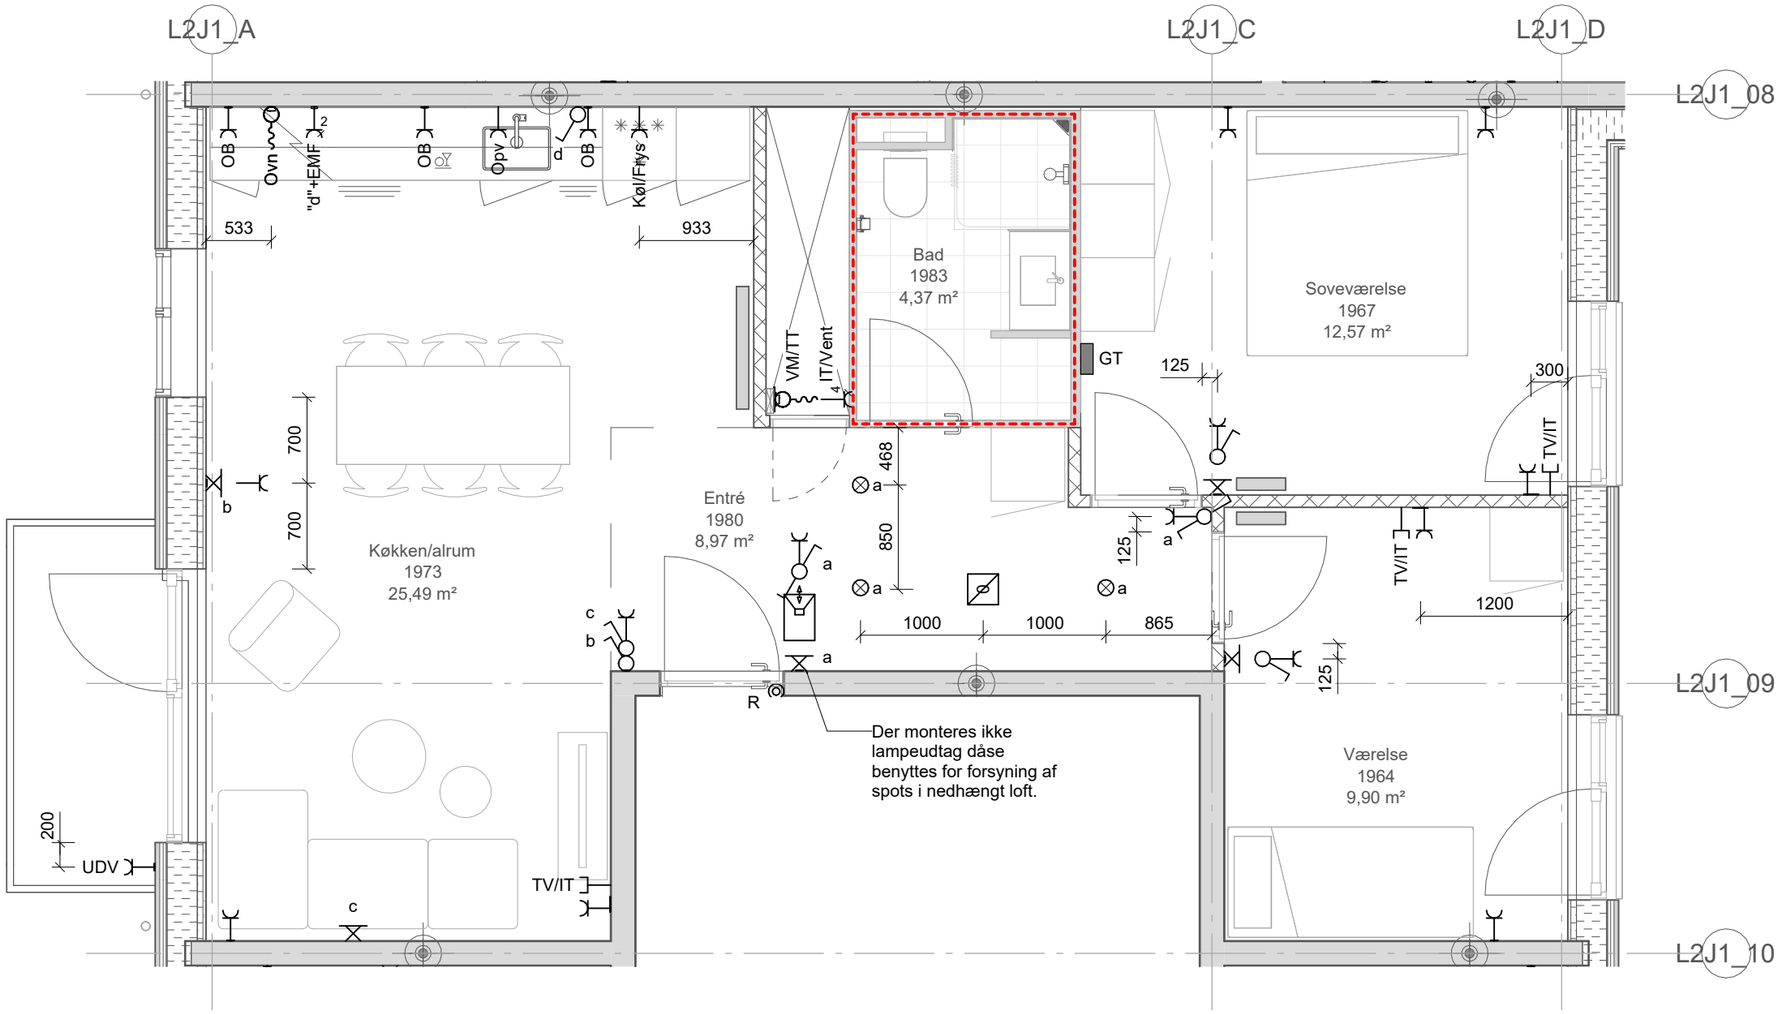

Projekt: Stejlepladsen


Tekst: Elinstallationer -
Byg J1 - 2. Sal, Byg A
OPG_3V_T30 - Side J1-23

Tegningsnr.: ISP2_K07_L2XX_H04_EXX_N930

Rev.:

Projektnr.: 1019198 | Dato: 2026-02-27 | Rev. Dato: | Mål: 1 : 50 | Side: J1-23

www.arteliagroup.dk | Fil:

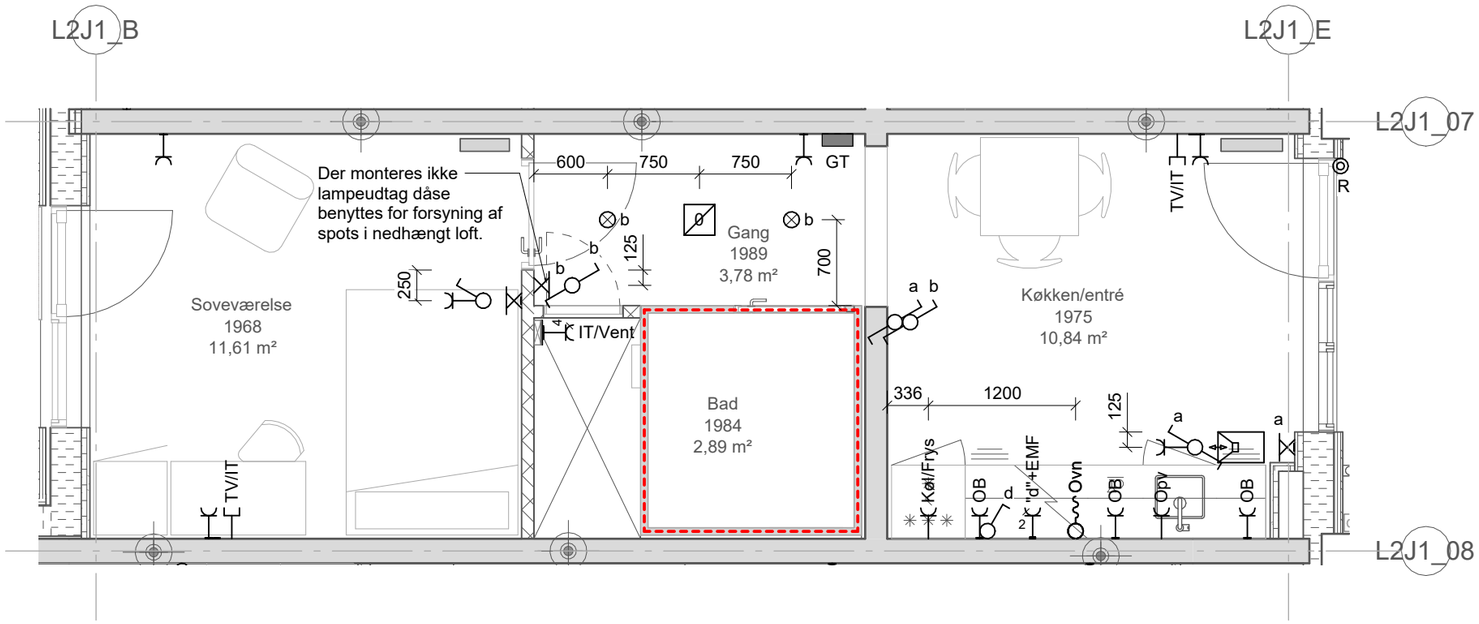

Projekt: Stejlepladsen


Tekst: Elinstallationer -
Byg J1 - 2. Sal, Byg B
ALT_1V_T31 - Side J1-24

Tegningsnr.: ISP2_K07_L2XX_H04_EXX_N930


Rev.:

Projektnr.: 1019198 | Dato: 2026-02-27 | Rev. Dato: | Mål: 1 : 50 | Side: J1-24

www.arteliagroup.dk | Fil:

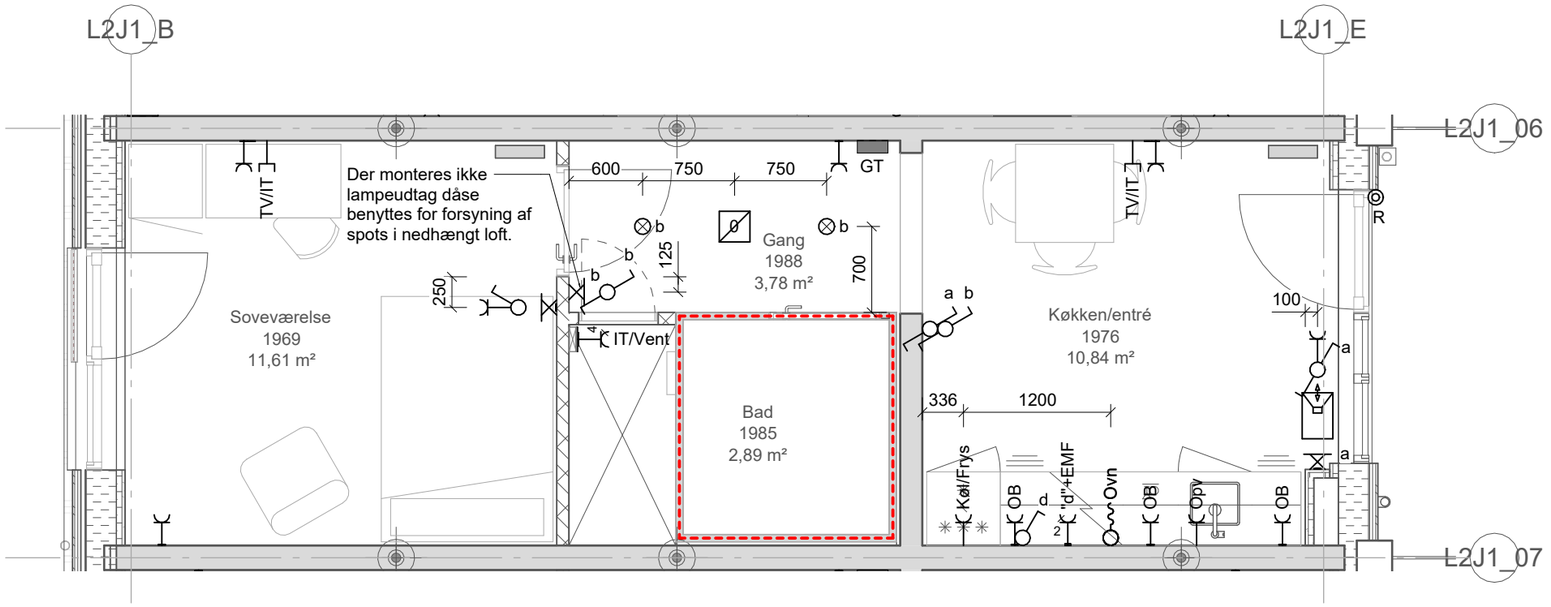

Projekt:	Stejlepladsen				
Tekst:	Elinstallationer - Byg J1 - 2. Sal, Byg B ALT_1V_T31.2 - Side J1-25			Tegningsnr.:	Rev.:
			ISP2_K07_L2XX_H04_EXX_N930		
Projektnr.: 1019198	Dato: 2026-02-27	Rev. Dato:		Mål: 1 : 50	Side: J1-25
www.arteliagroup.dk	Fil:				

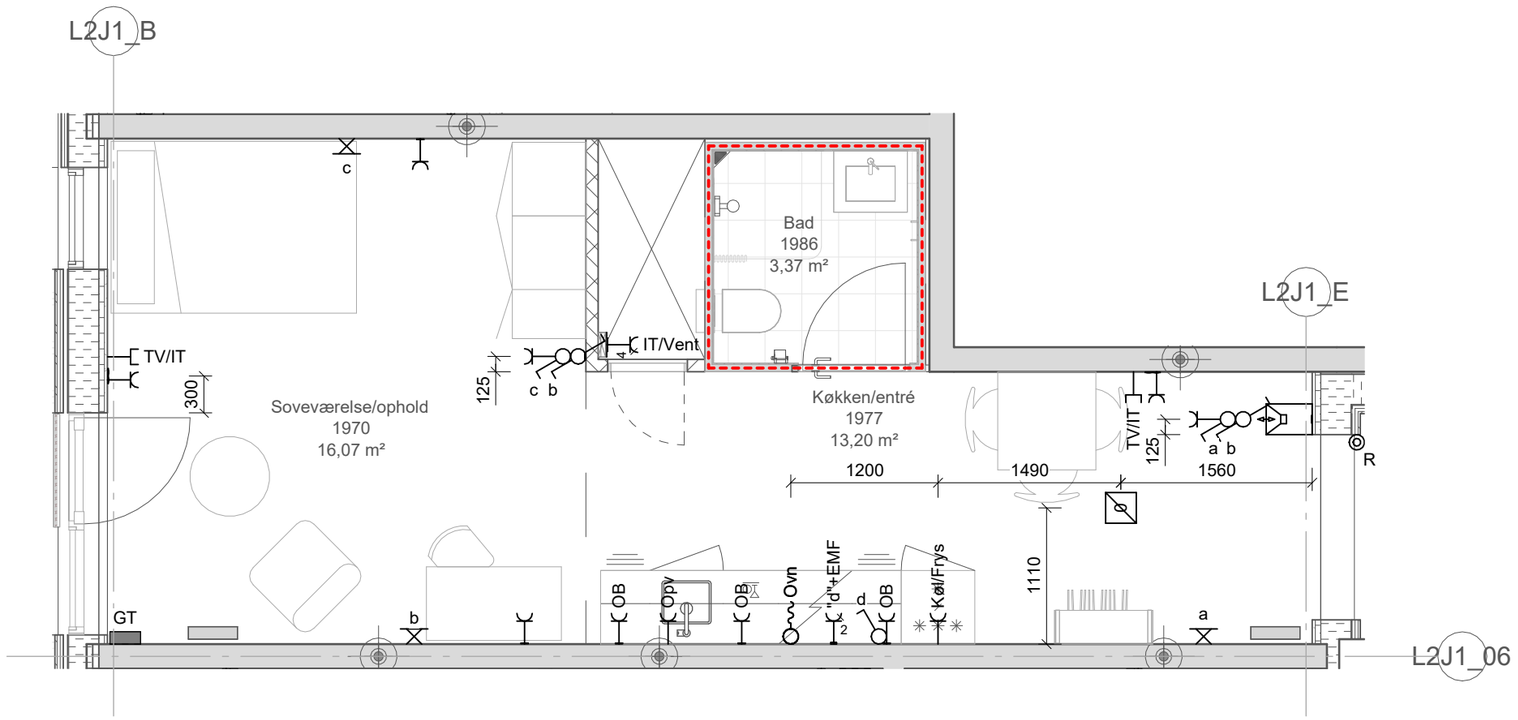

Projekt: Stejlepladsen


Tekst: Elinstallationer -
Byg J1 - 2. Sal, Byg B
ALT_1V_T30 - Side J1-26

Tegningsnr.: ISP2_K07_L2XX_H04_EXX_N930

Rev.:

Projektnr.: 1019198 | Dato: 2026-02-27 | Rev. Dato: | Mål: 1 : 50 | Side: J1-26

www.arteliagroup.dk | Fil:

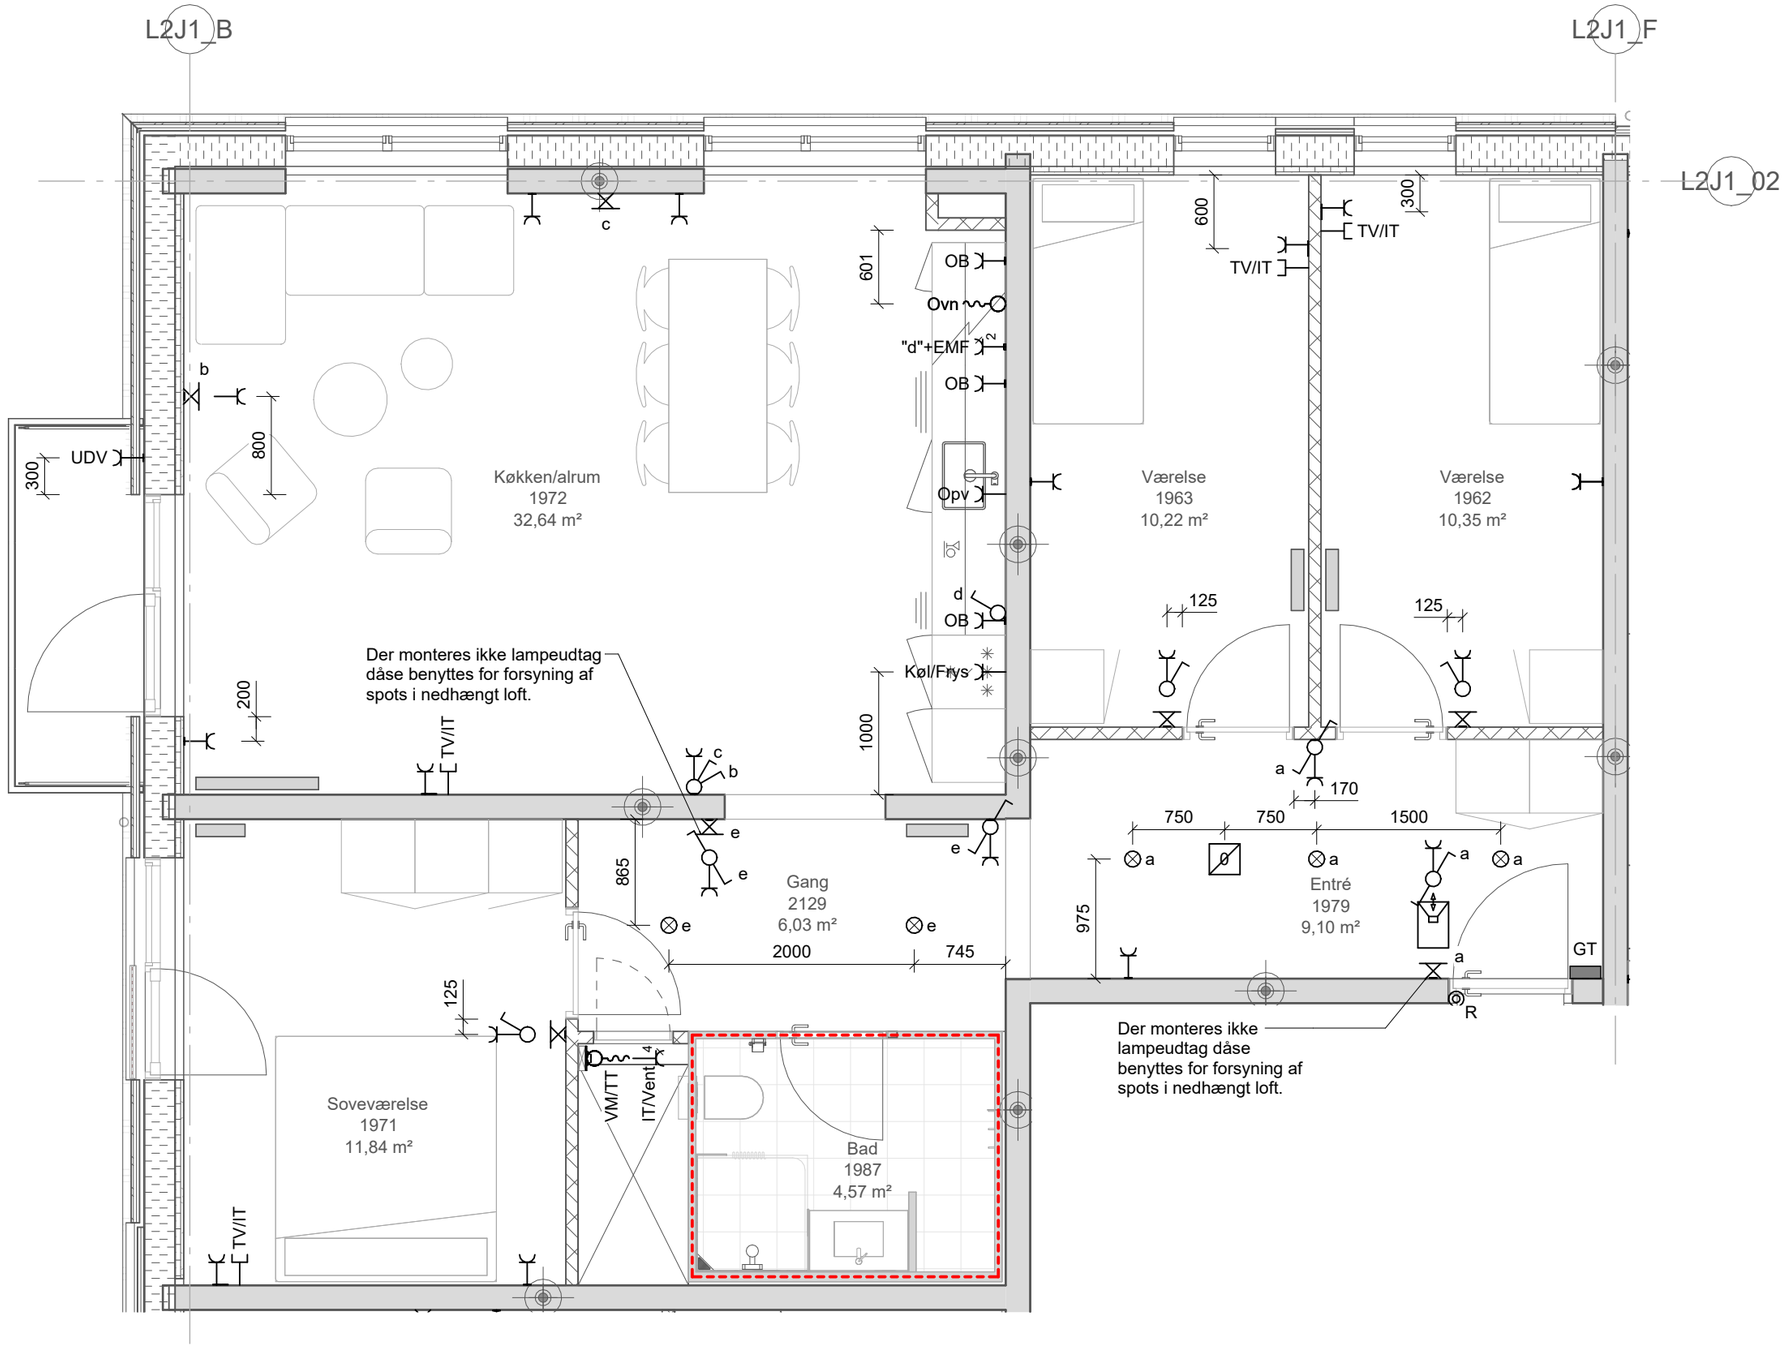

Projekt: Stejlepladsen


Tekst: Elinstallationer -
Byg J1 - 2. Sal, Byg B
OPG_4V_T31 - J1-27

Tegningsnr.: ISP2_K07_L2XX_H04_EXX_N930

Rev.:

Projektnr.: 1019198 | Dato: 2026-02-27 | Rev. Dato: | Mål: 1 : 50 | Side: J1-27

www.arteliagroup.dk | Fil:

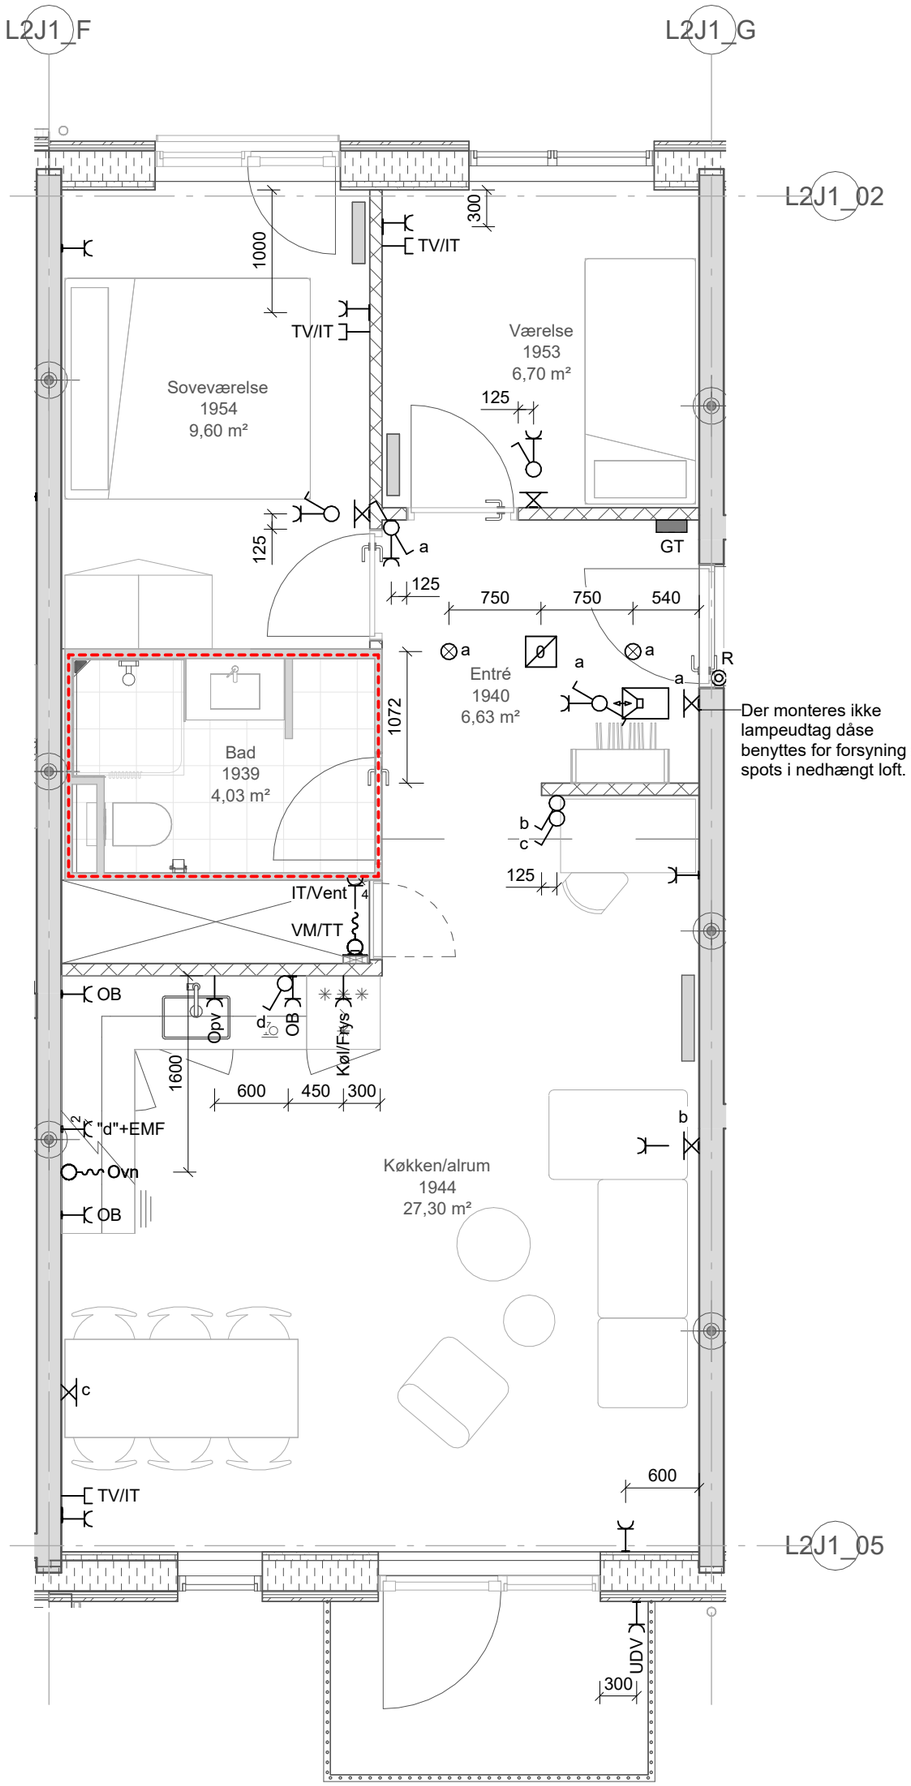

Projekt: Stejlepladsen


Tekst: Elinstallationer -
Byg J1 - 2. Sal, Byg C
OPG_3V_T34 - Side J1-28

Tegningsnr.: ISP2_K07_L2XX_H04_EXX_N930


Rev.:

Projektnr.: 1019198 | Dato: 2026-02-27 | Rev. Dato: | Mål: 1 : 50 | Side: J1-28

www.arteliagroup.dk | Fil:

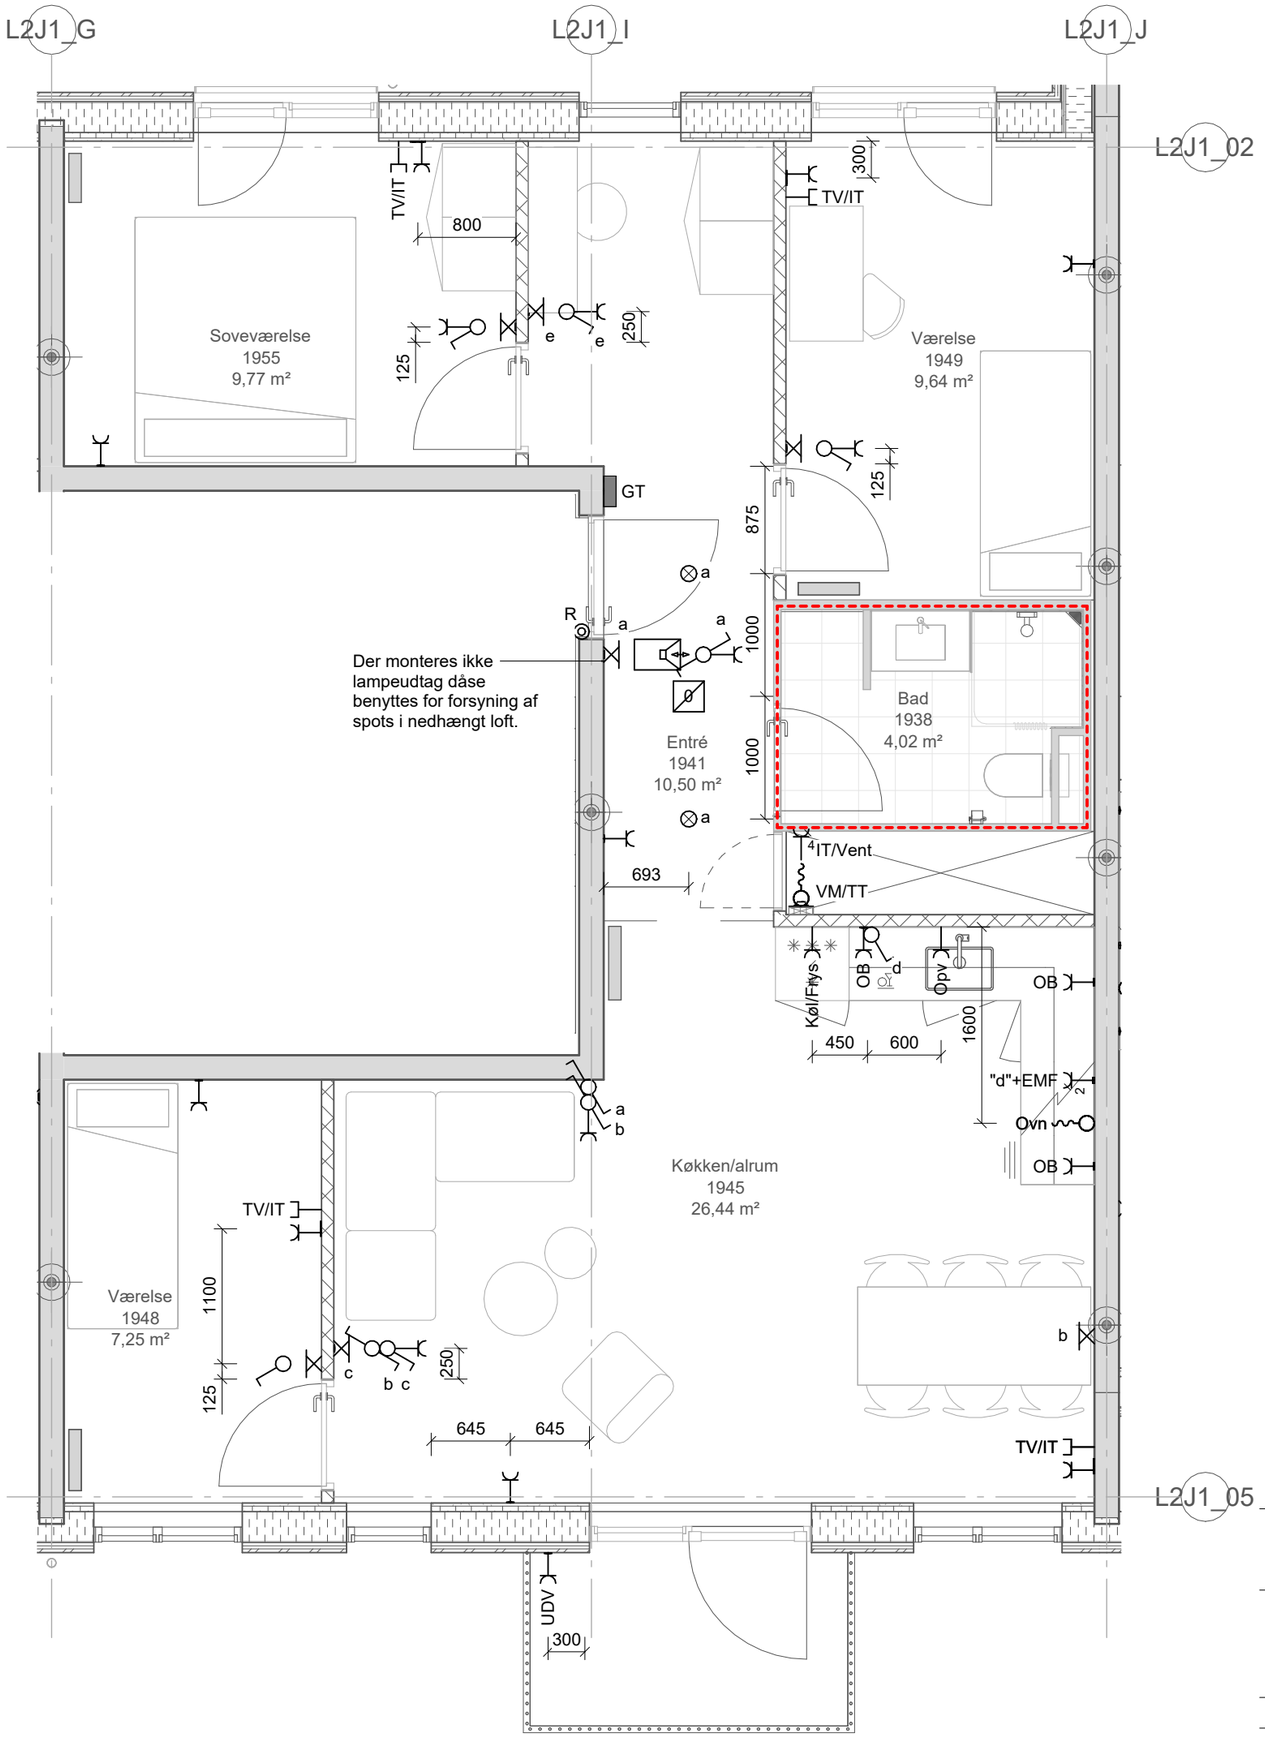

Projekt:	Stejlepladsen				
Tekst:	Elinstallationer - Byg J1 - 2. Sal, Byg C OPG_4V_T32 - Side J1-29			Tegningsnr.:	Rev.:
				ISP2_K07_L2XX_H04_EXX_N930	
Projektnr.: 1019198	Dato: 2026-02-27	Rev. Dato:		Mål: 1 : 50	Side: J1-29
www.arteliagroup.dk	Fil:				

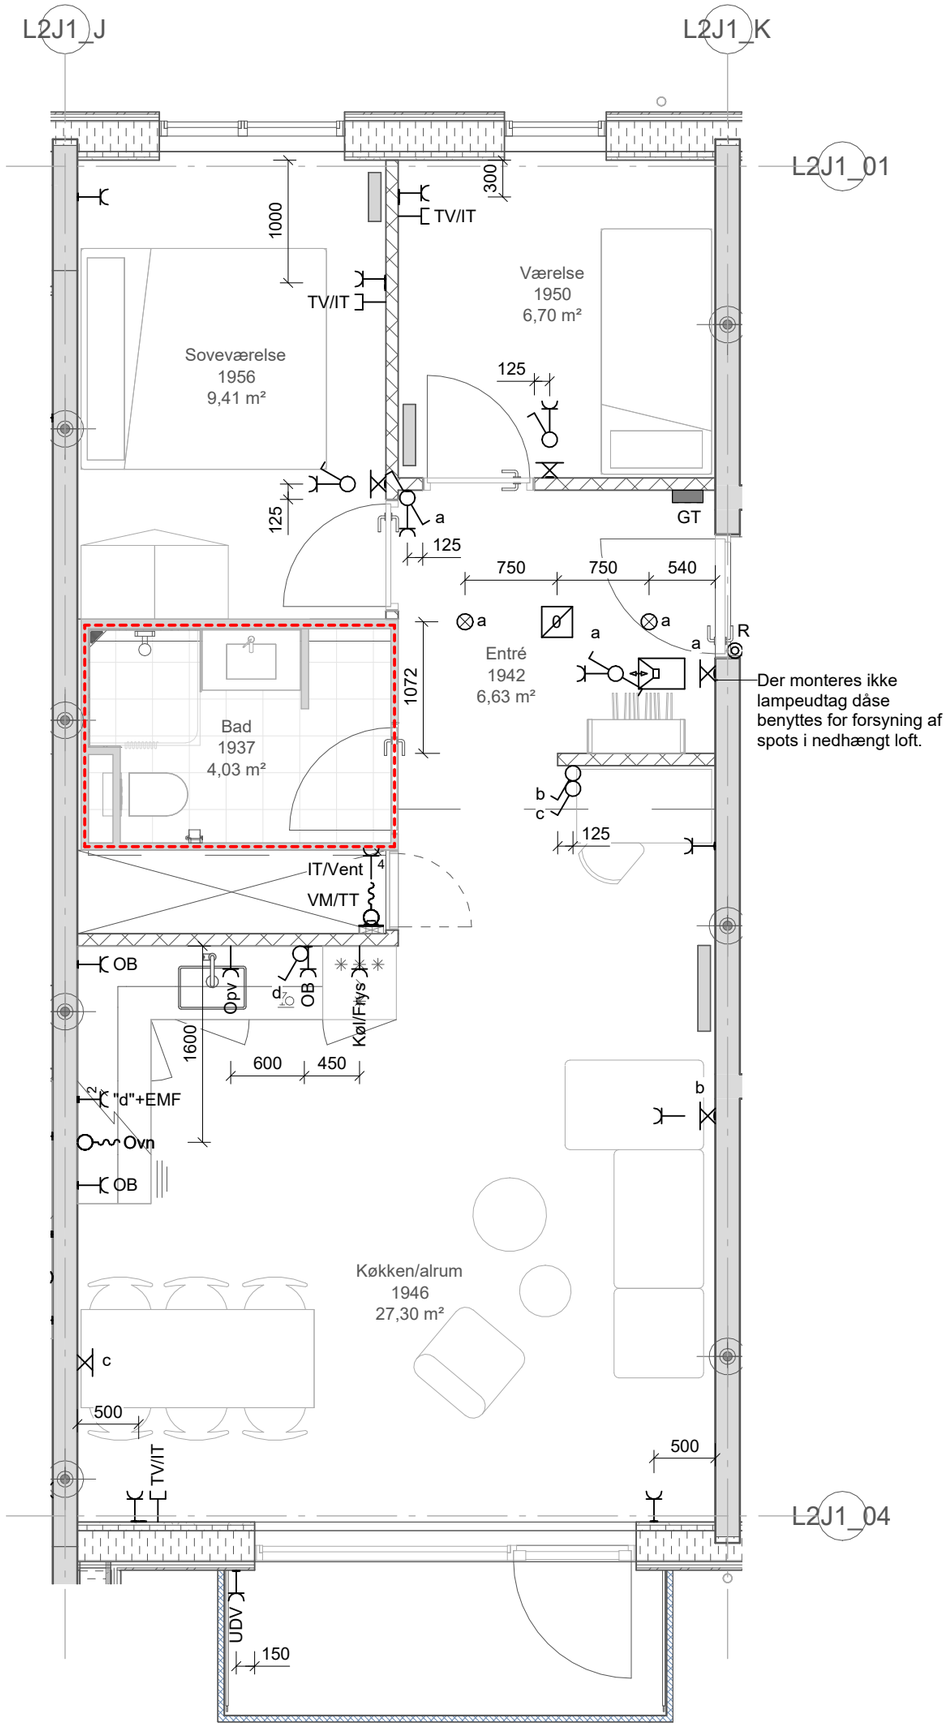

Projekt: Stejlepladsen


Tekst: Elinstallationer -
Byg J1 - 2. Sal, Byg D
OPG_3V_T34.2 - Side J1-30

Tegningsnr.: ISP2_K07_L2XX_H04_EXX_N930

Rev.:

Projektnr.: 1019198 | Dato: 2026-02-27 | Rev. Dato: | Mål: 1 : 50 | Side: J1-30

www.arteliagroup.dk | Fil:

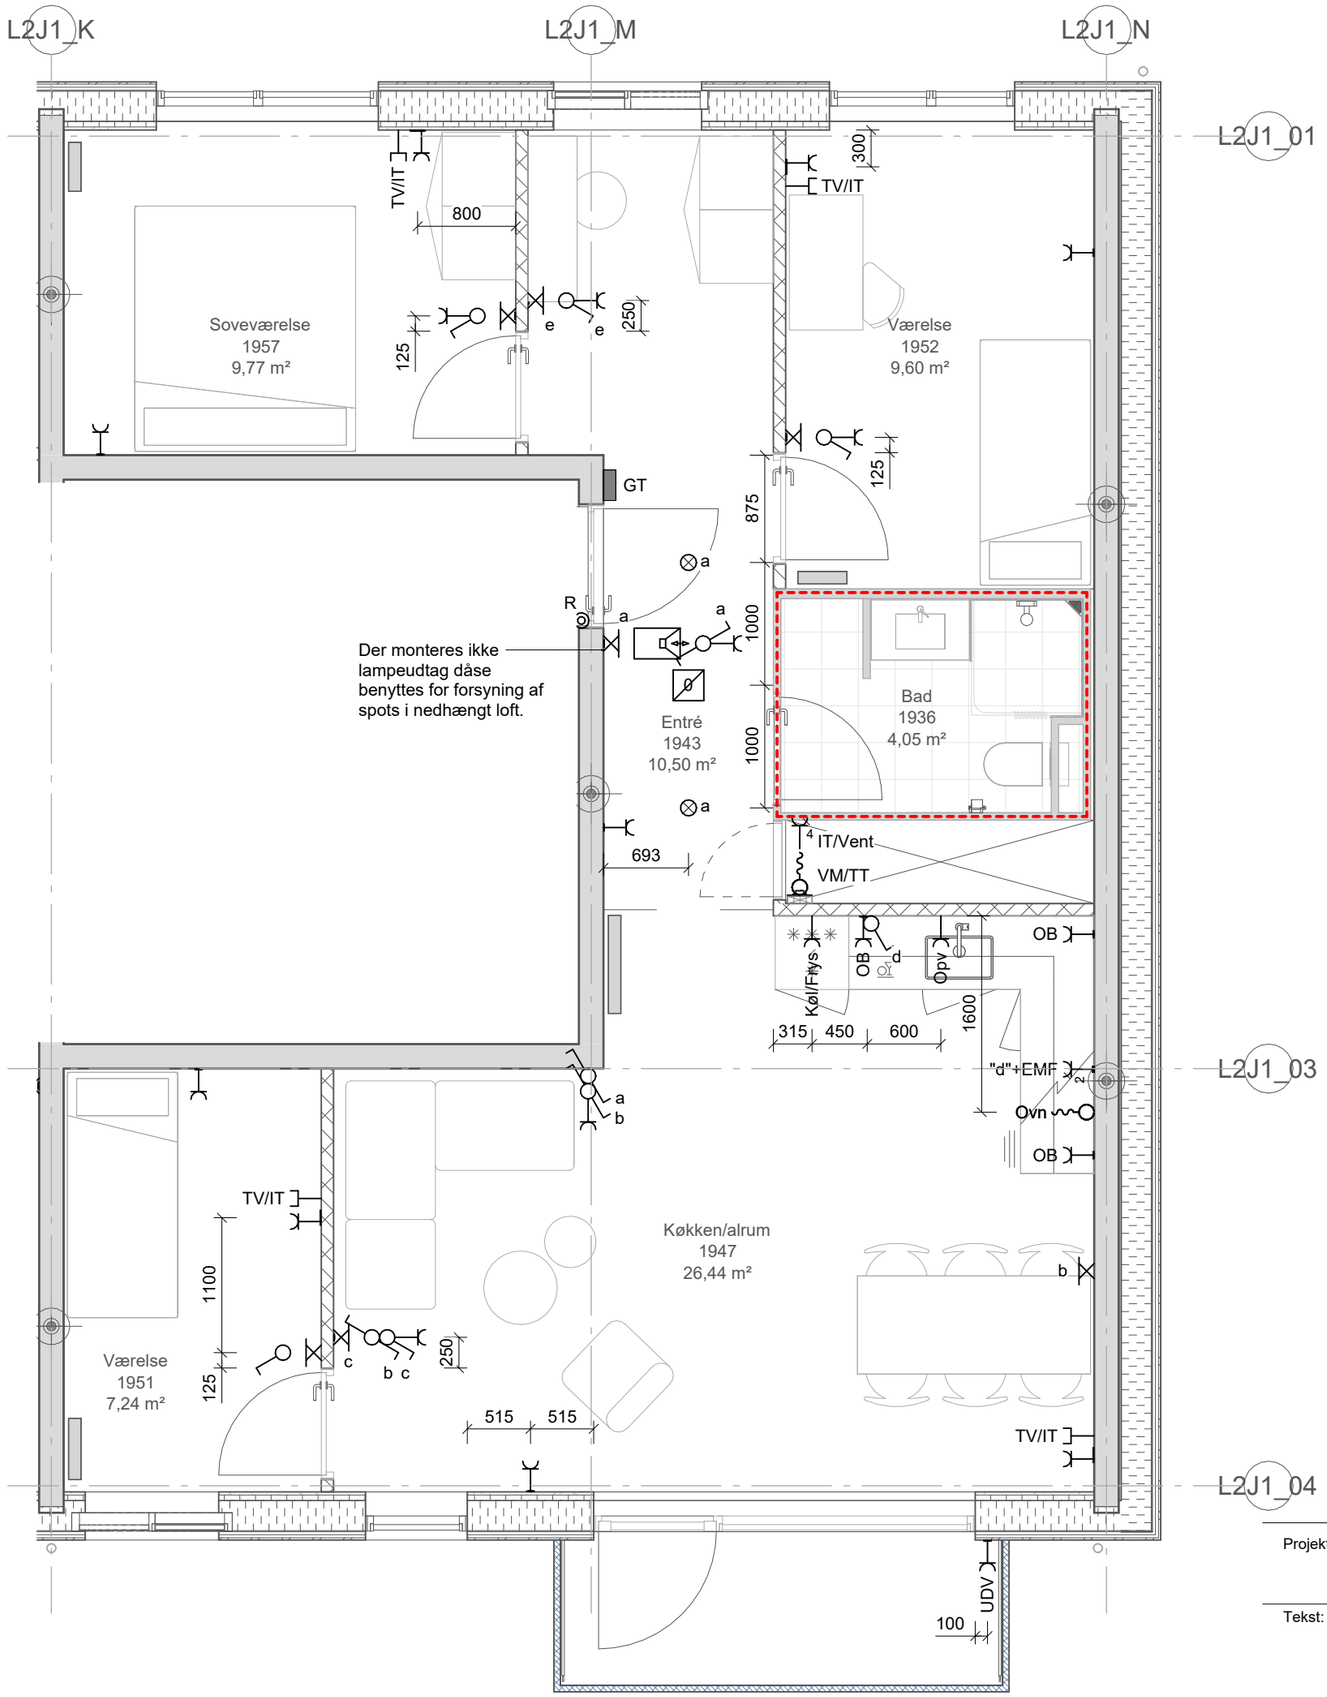

Projekt: Stejlepladsen


Tekst: Elinstallationer -
Byg J1 - 2. Sal, Byg D
OPG_4V_T32.2 - Side J1-31

Tegningsnr.: ISP2_K07_L2XX_H04_EXX_N930


Rev.:

Projektnr.: 1019198 | Dato: 2026-02-27 | Rev. Dato: | Mål: 1 : 50 | Side: J1-31

www.arteliagroup.dk | Fil:

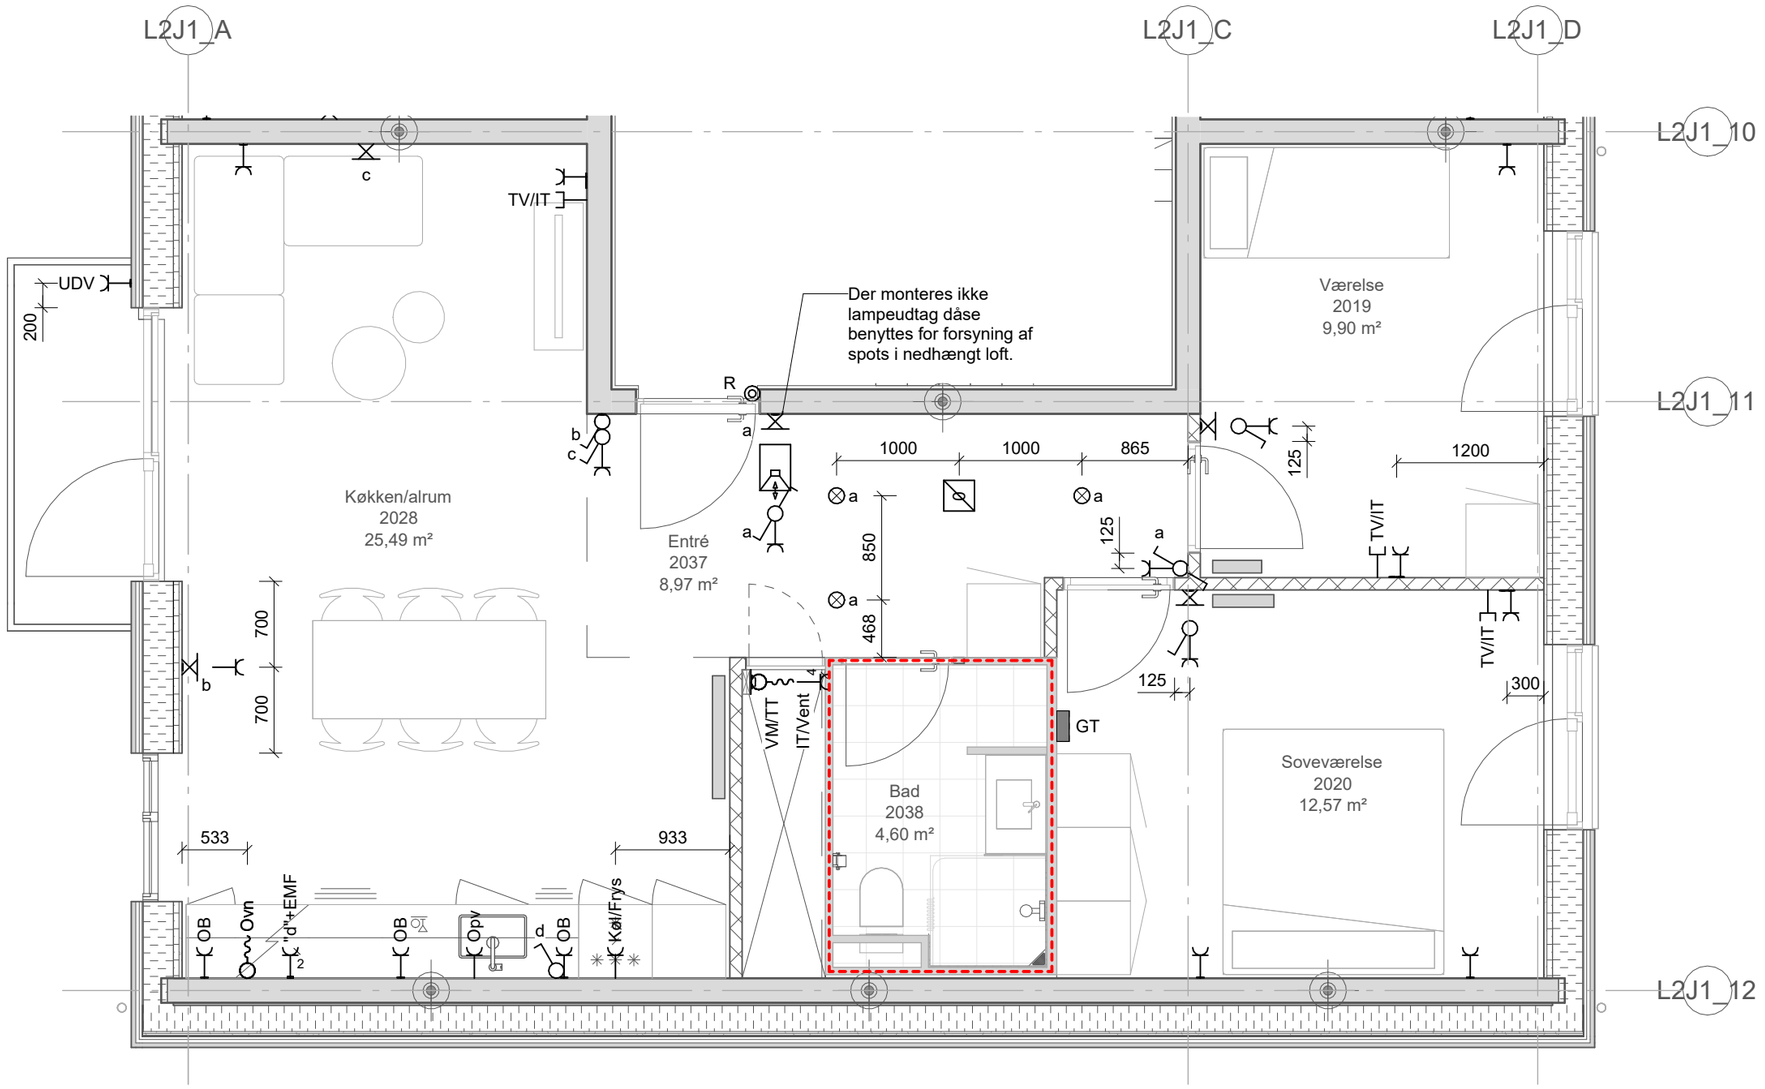

Projekt:	Stejlepladsen				
Tekst:	Elinstallationer - Byg J1 - 3. Sal, Byg A OPG_3V_T30_S - Side J1-32			Tegningsnr.:	Rev.:
				ISP2_K07_L2XX_H04_EXX_N930	
Projektnr.: 1019198	Dato: 2026-02-27	Rev. Dato:		Mål: 1 : 50	Side: J1-32
www.arteliagroup.dk	Fil:				

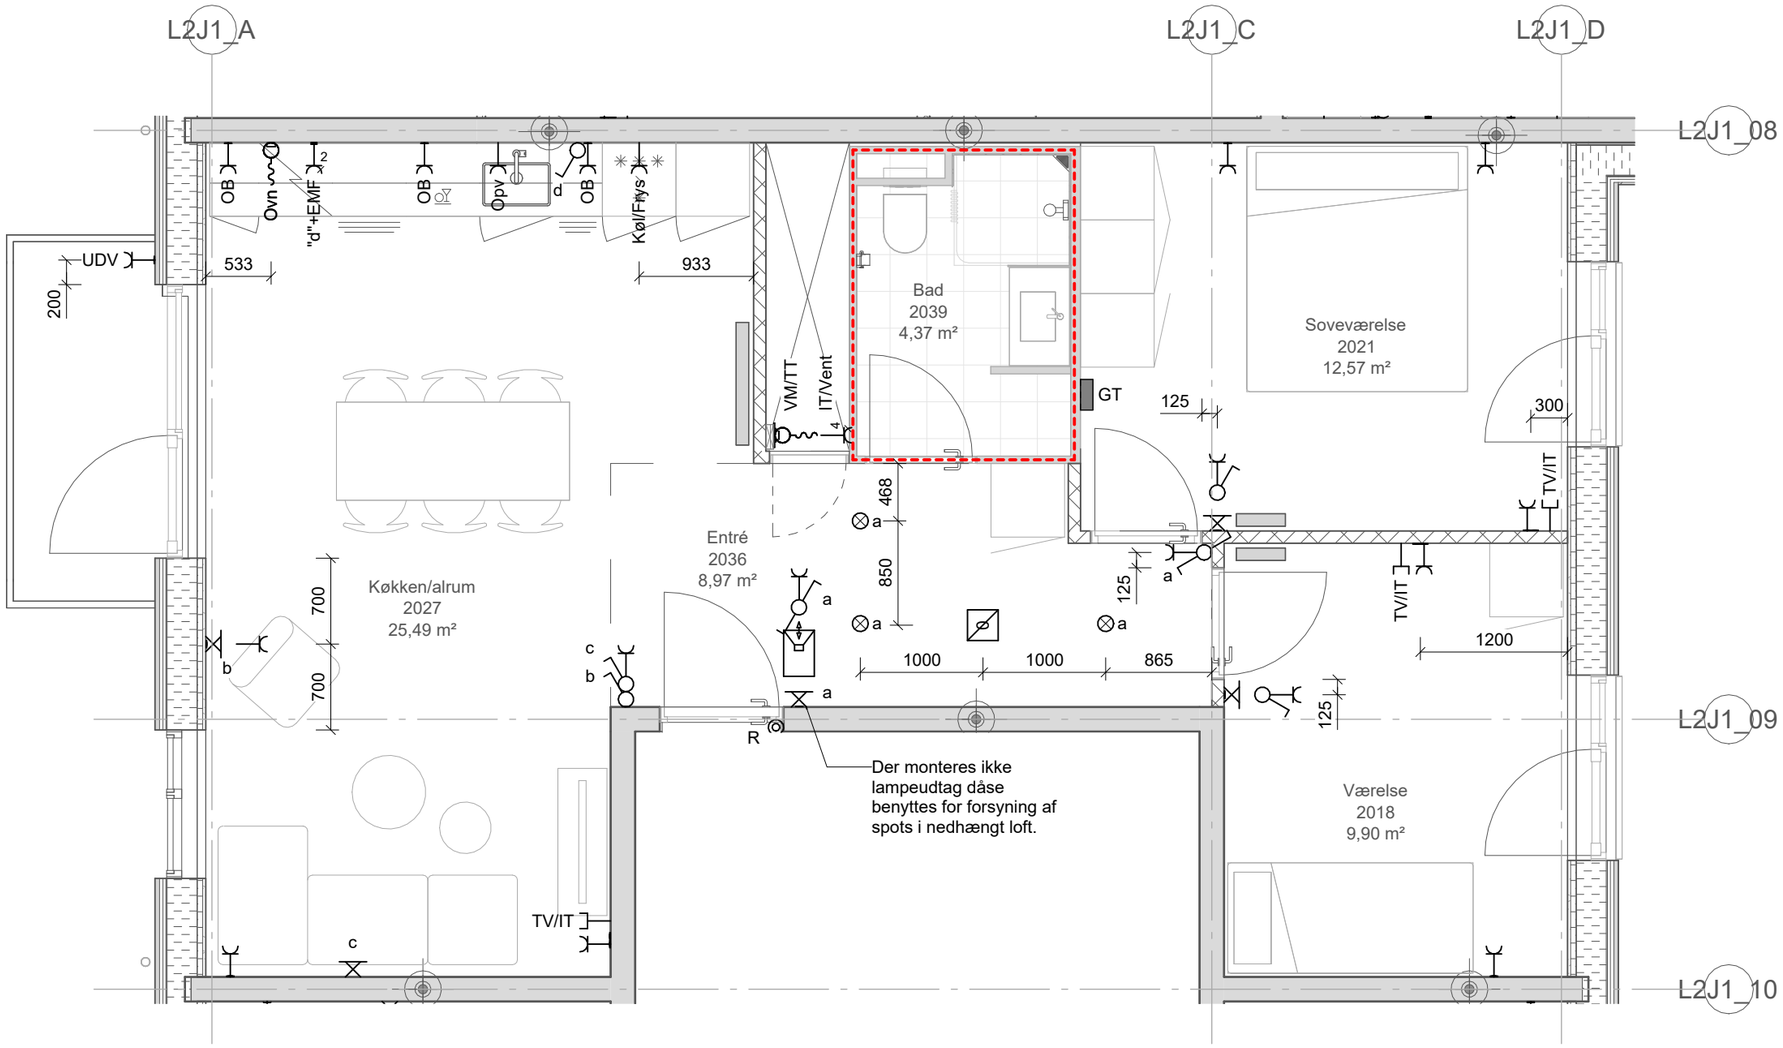

Projekt: Stejlepladsen


Tekst: Elinstallationer -
Byg J1 - 3. Sal, Byg A
OPG_3V_T30 - Side J1-33

Tegningsnr.: ISP2_K07_L2XX_H04_EXX_N930

Rev.:

Projektnr.: 1019198 | Dato: 2026-02-27 | Rev. Dato: | Mål: 1 : 50 | Side: J1-33

www.arteliagroup.dk | Fil:

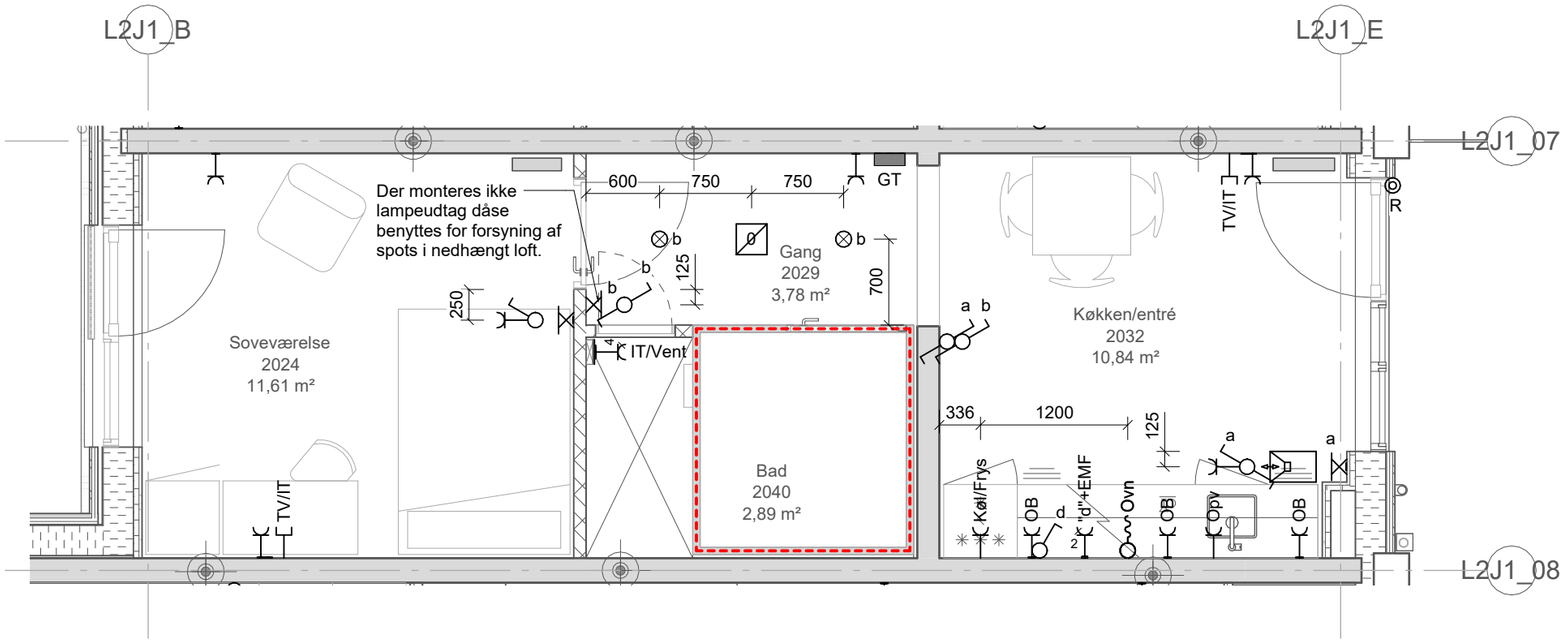

Projekt: Stejlepladsen


Tekst: Elinstallationer -
Byg J1 - 3. Sal, Byg B
ALT_1V_T31 - Side J1-34

Tegningsnr.: ISP2_K07_L2XX_H04_EXX_N930

Rev.:

Projektnr.: 1019198 | Dato: 2026-02-27 | Rev. Dato: | Mål: 1 : 50 | Side: J1-34

www.arteliagroup.dk | Fil:

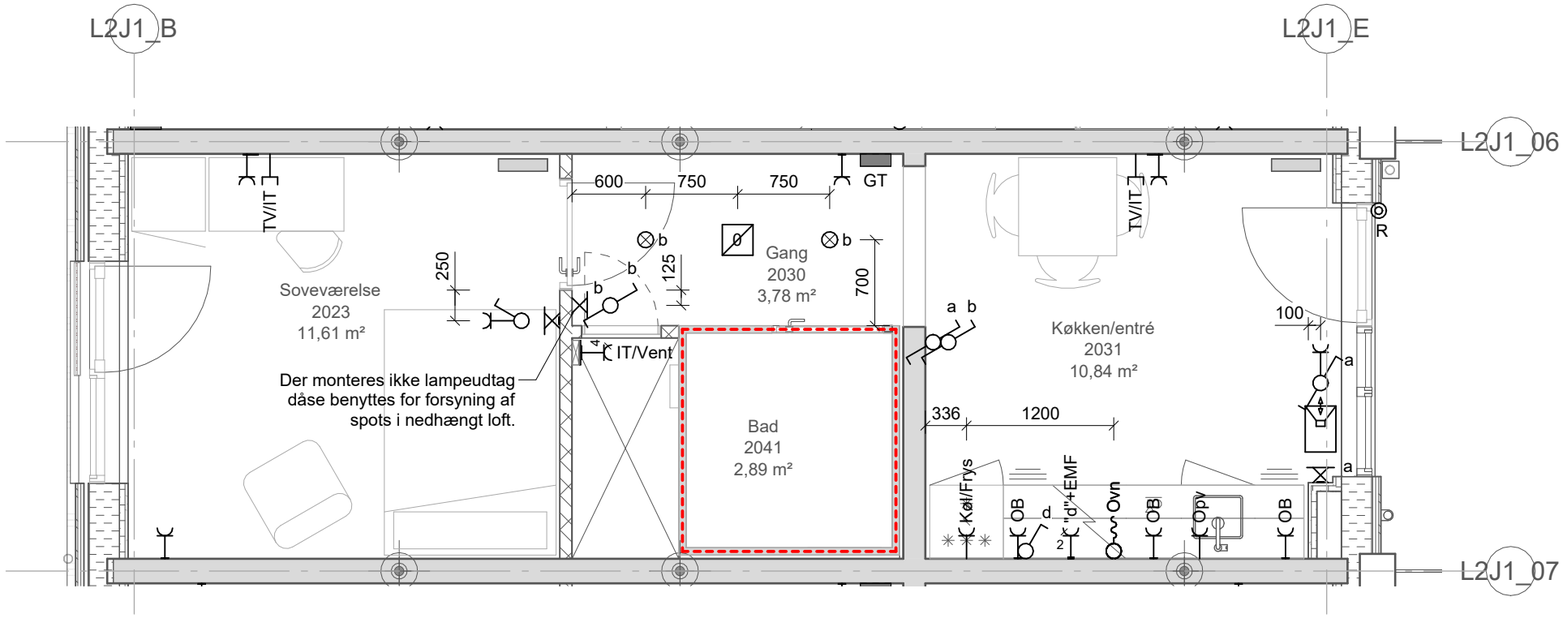

Projekt: Stejlepladsen


Tekst: Elinstallationer -
Byg J1 - 3. Sal, Byg B
ALT_1V_T31.3 - Side J1-35

Tegningsnr.: ISP2_K07_L2XX_H04_EXX_N930


Rev.:

Projektnr.: 1019198 | Dato: 2026-02-27 | Rev. Dato: | Mål: 1 : 50 | Side: J1-35


www.arteliagroup.dk | Fil:

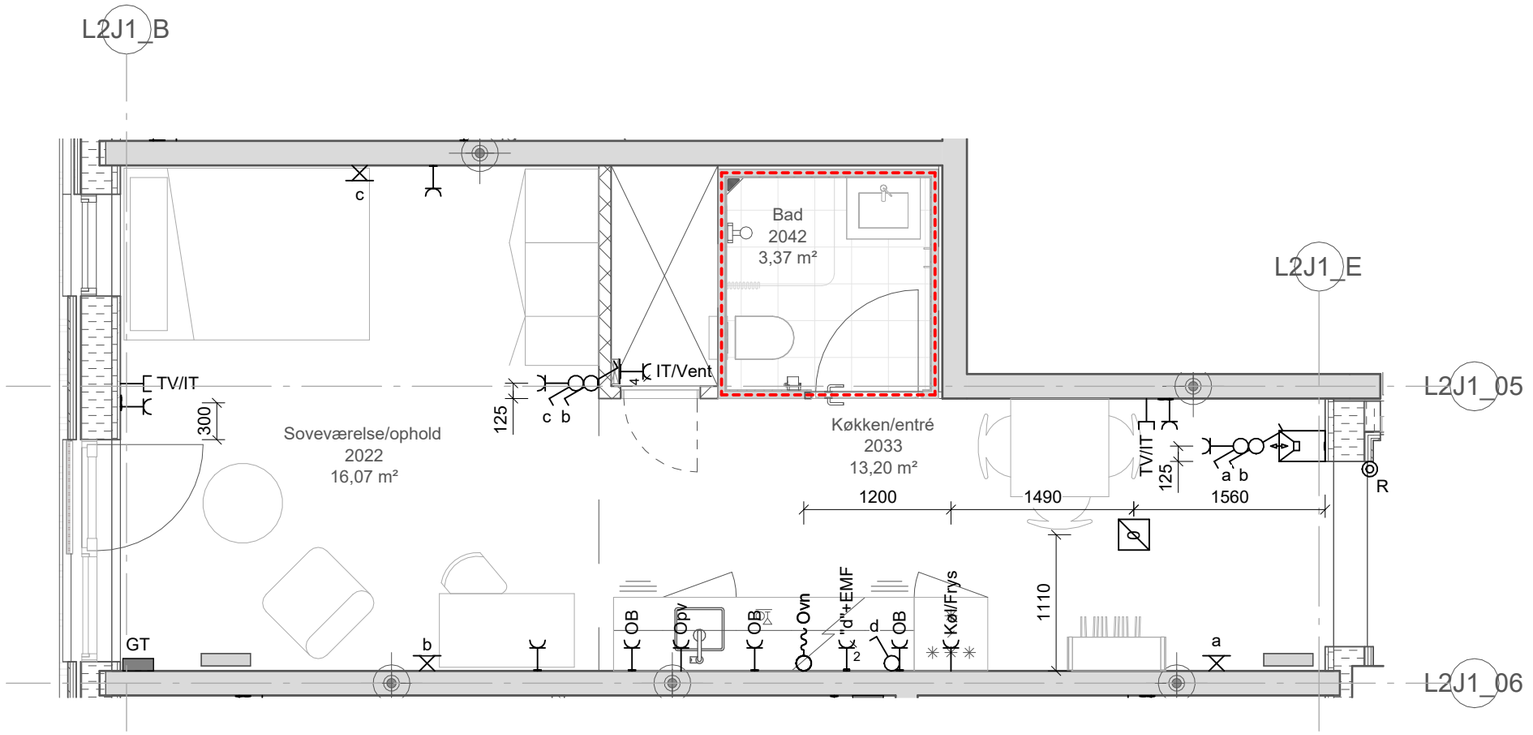

Projekt:	Stejlepladsen				
Tekst:	Elinstallationer - Byg J1 - 3. Sal, Byg B ALT_1V_T30 - Side J1-36			Tegningsnr.:	Rev.:
			ISP2_K07_L2XX_H04_EXX_N930		
Projektnr.: 1019198	Dato: 2026-02-27	Rev. Dato:		Mål: 1 : 50	Side: J1-36
www.arteliagroup.dk	Fil:				

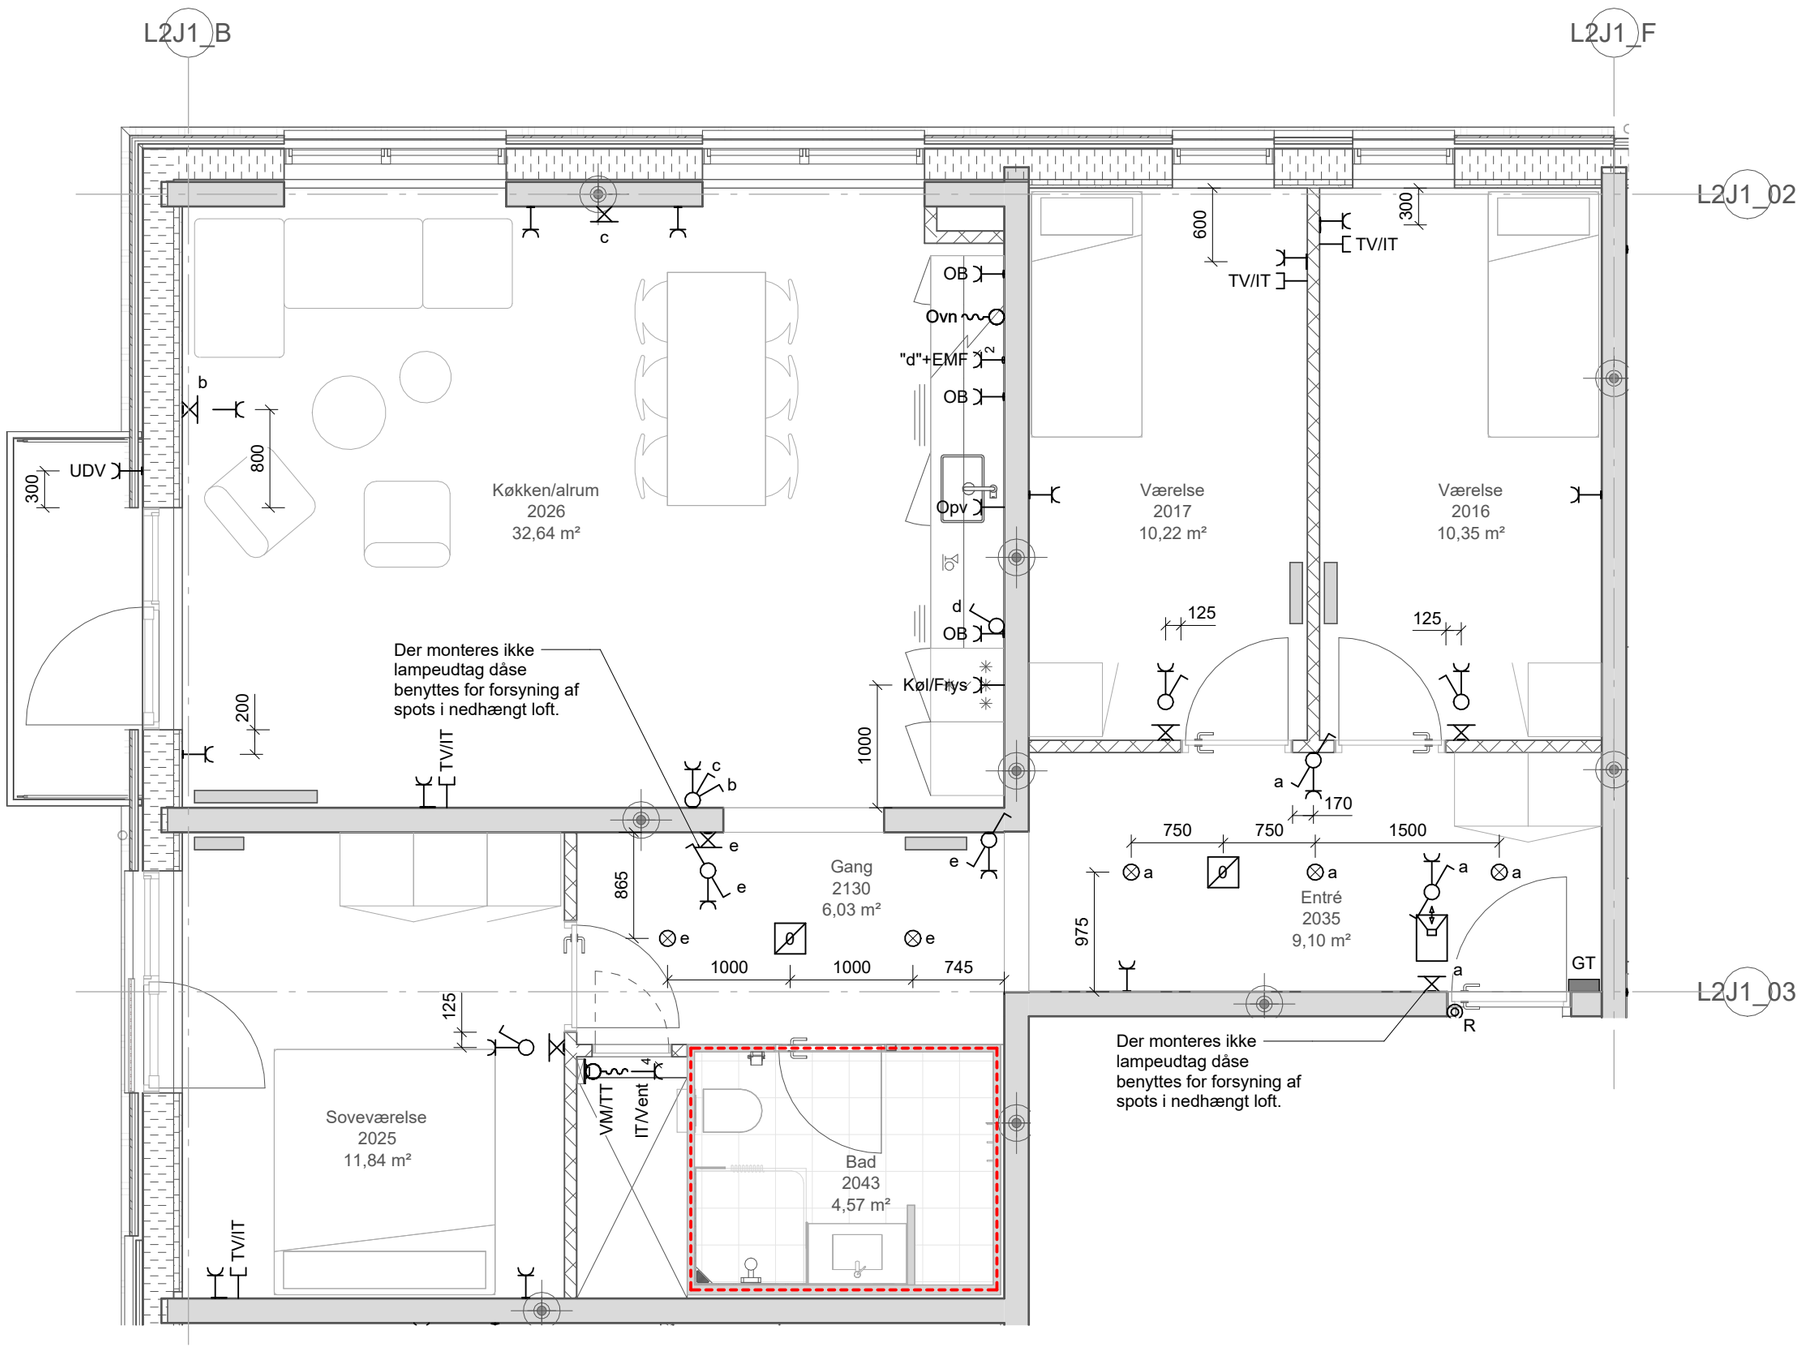

Projekt:	Stejlepladsen				
Tekst:	Elinstallationer - Byg J1 - 3. Sal, Byg B OPG_4V_T31 - Side J1-37			Tegningsnr.:	Rev.:
				ISP2_K07_L2XX_H04_EXX_N930	
Projektnr.: 1019198	Dato: 2026-02-27	Rev. Dato:		Mål: 1 : 50	Side: J1-37
www.arteliagroup.dk	Fil:				

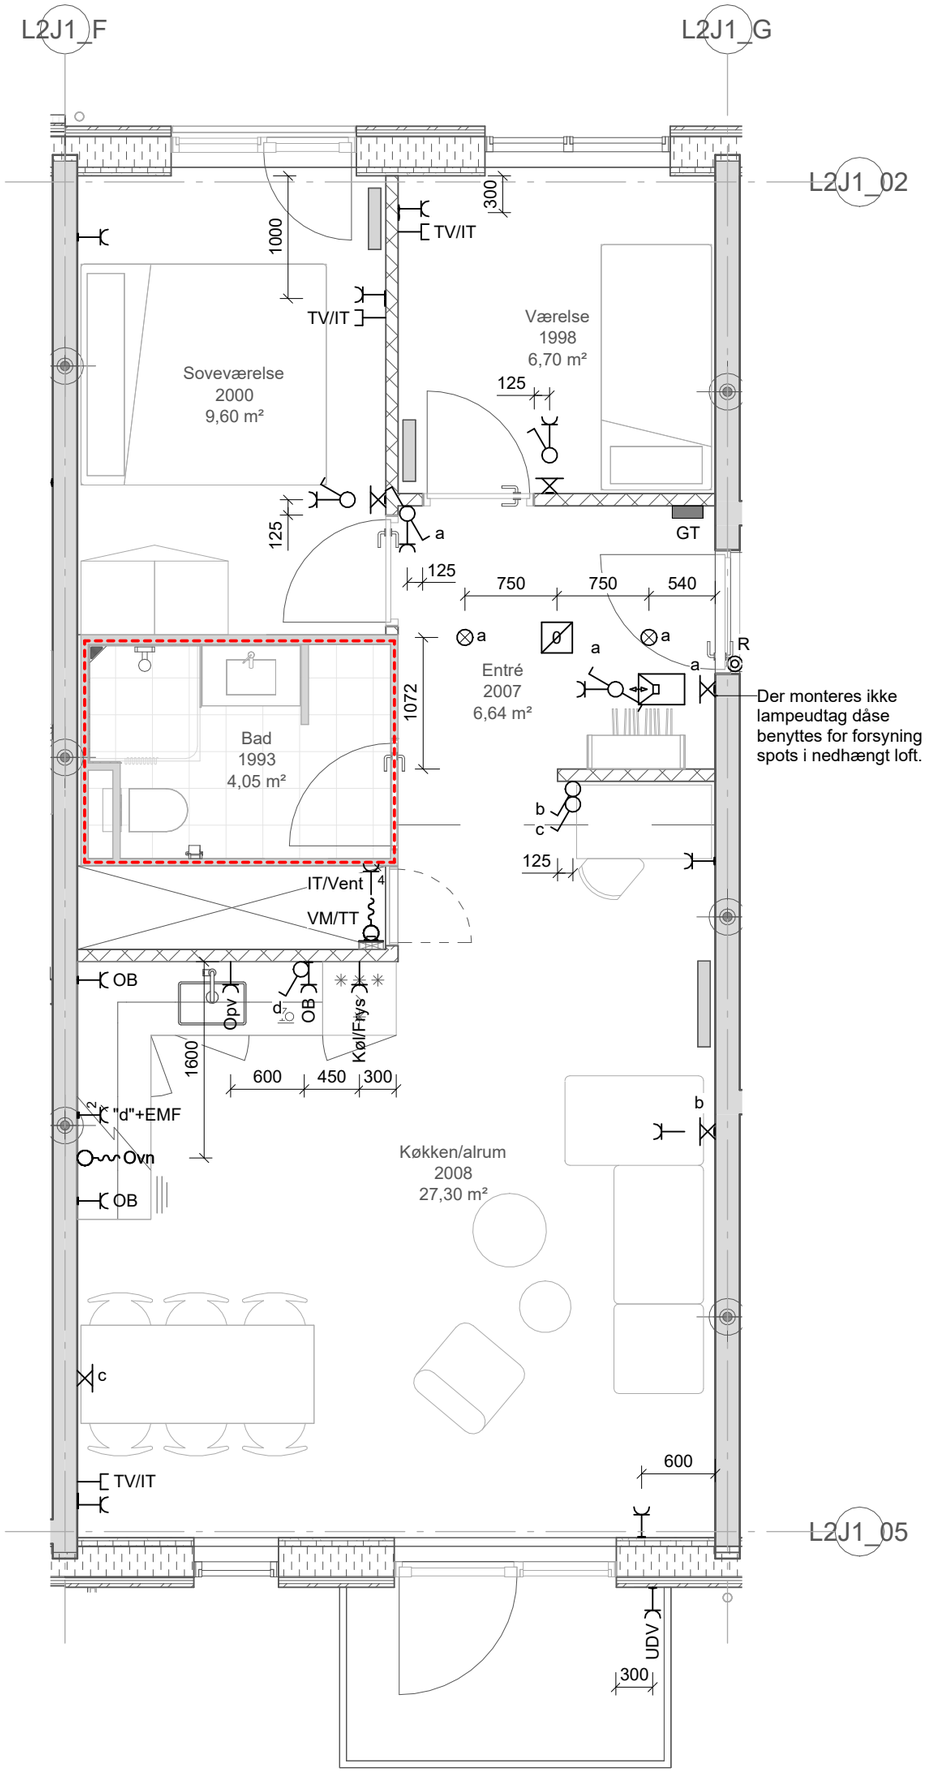

Projekt: Stejlepladsen


Tekst: Elinstallationer -
Byg J1 - 3. Sal, Byg C
OPG_3V_T34 - Side J1-38

Tegningsnr.: ISP2_K07_L2XX_H04_EXX_N930


Rev.:

Projektnr.: 1019198 | Dato: 2026-02-27 | Rev. Dato: | Mål: 1 : 50 | Side: J1-38

www.arteliagroup.dk | Fil:

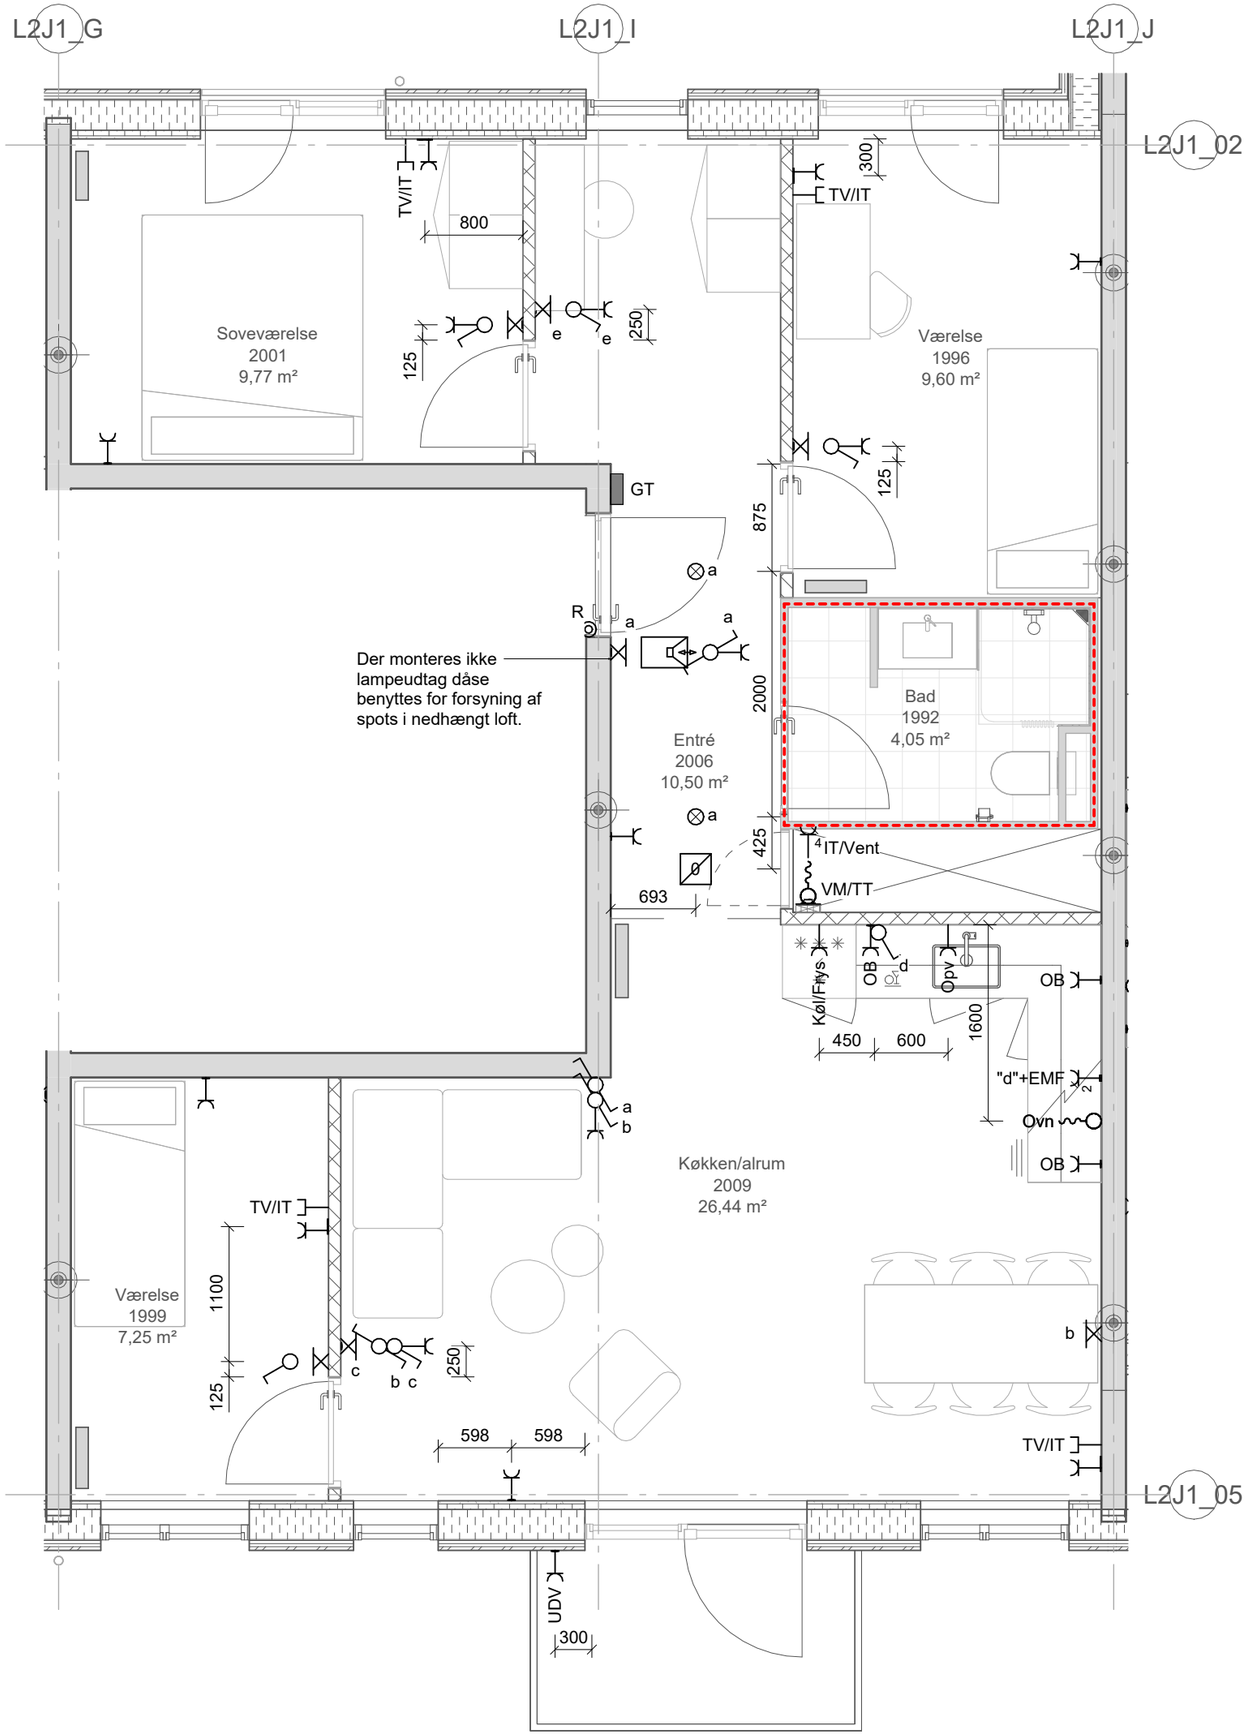

Projekt:	Stejlepladsen				
Tekst:	Elinstallationer - Byg J1 - 3. Sal, Byg C OPG_4V_T32 - Side J1-39			Tegningsnr.:	Rev.:
				ISP2_K07_L2XX_H04_EXX_N930	
Projektnr.: 1019198	Dato: 2026-02-27	Rev. Dato:		Mål: 1 : 50	Side: J1-39
www.arteliagroup.dk	Fil:				

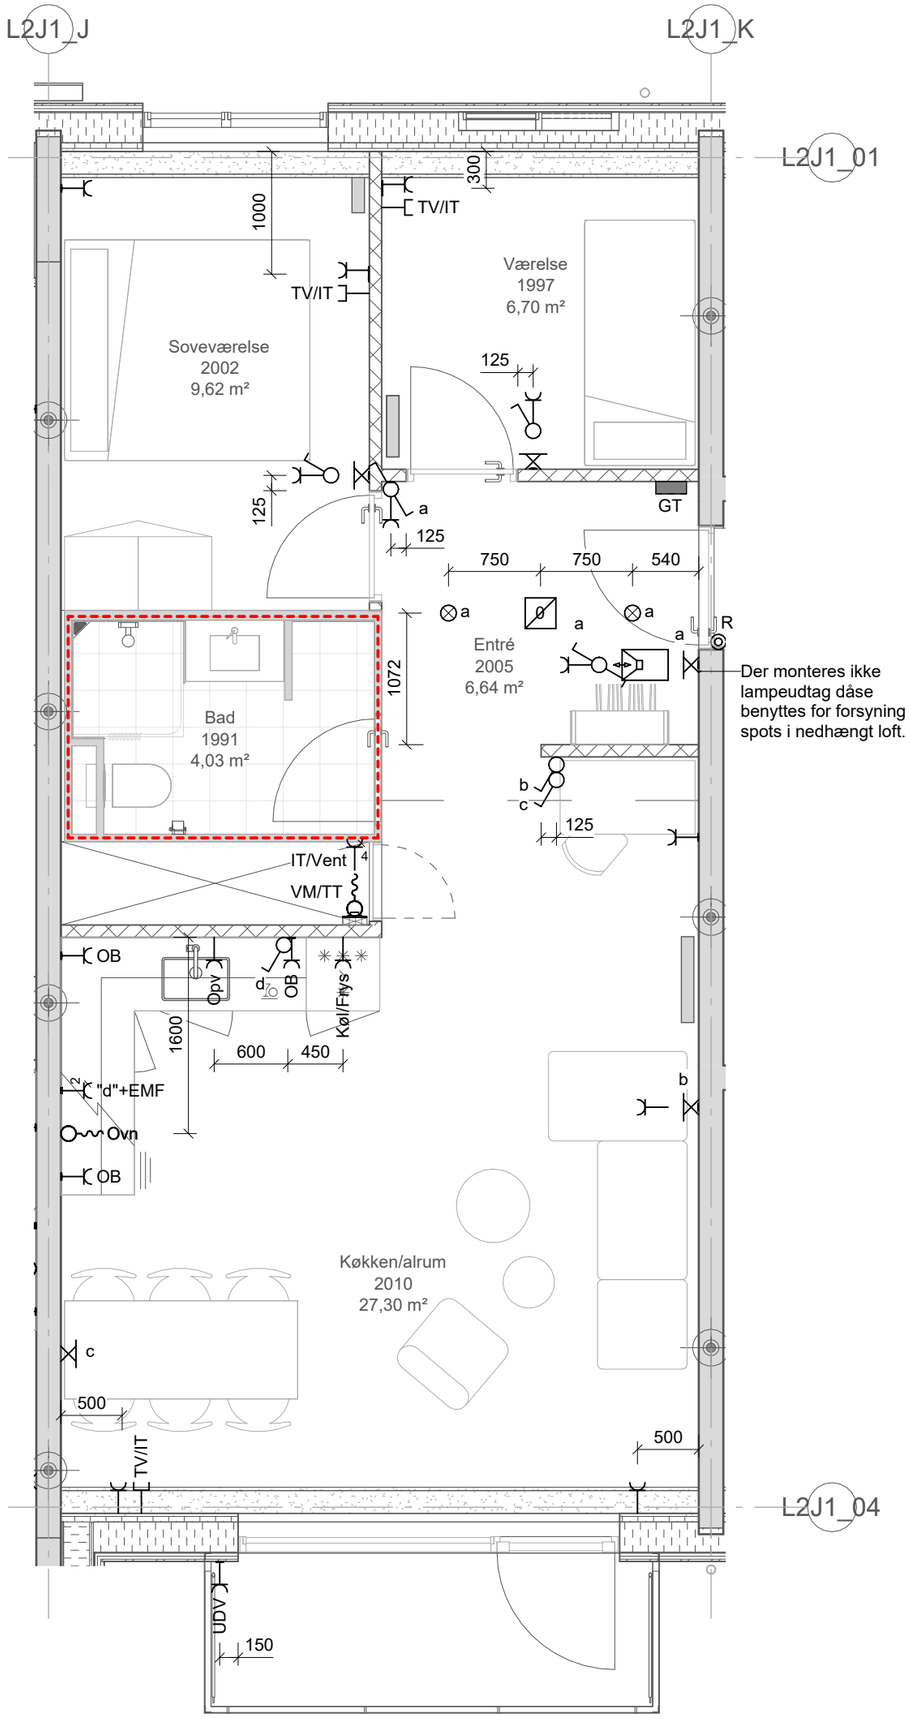

Projekt: Stejlepladsen


Tekst: Elinstallationer -
Byg J1 - 3. Sal, Byg D
OPG_3V_T34.3 - Side J1-40

Tegningsnr.: ISP2_K07_L2XX_H04_EXX_N930

Rev.:

Projektnr.: 1019198 | Dato: 2026-02-27 | Rev. Dato: | Mål: 1 : 50 | Side: J1-40

www.arteliagroup.dk | Fil:

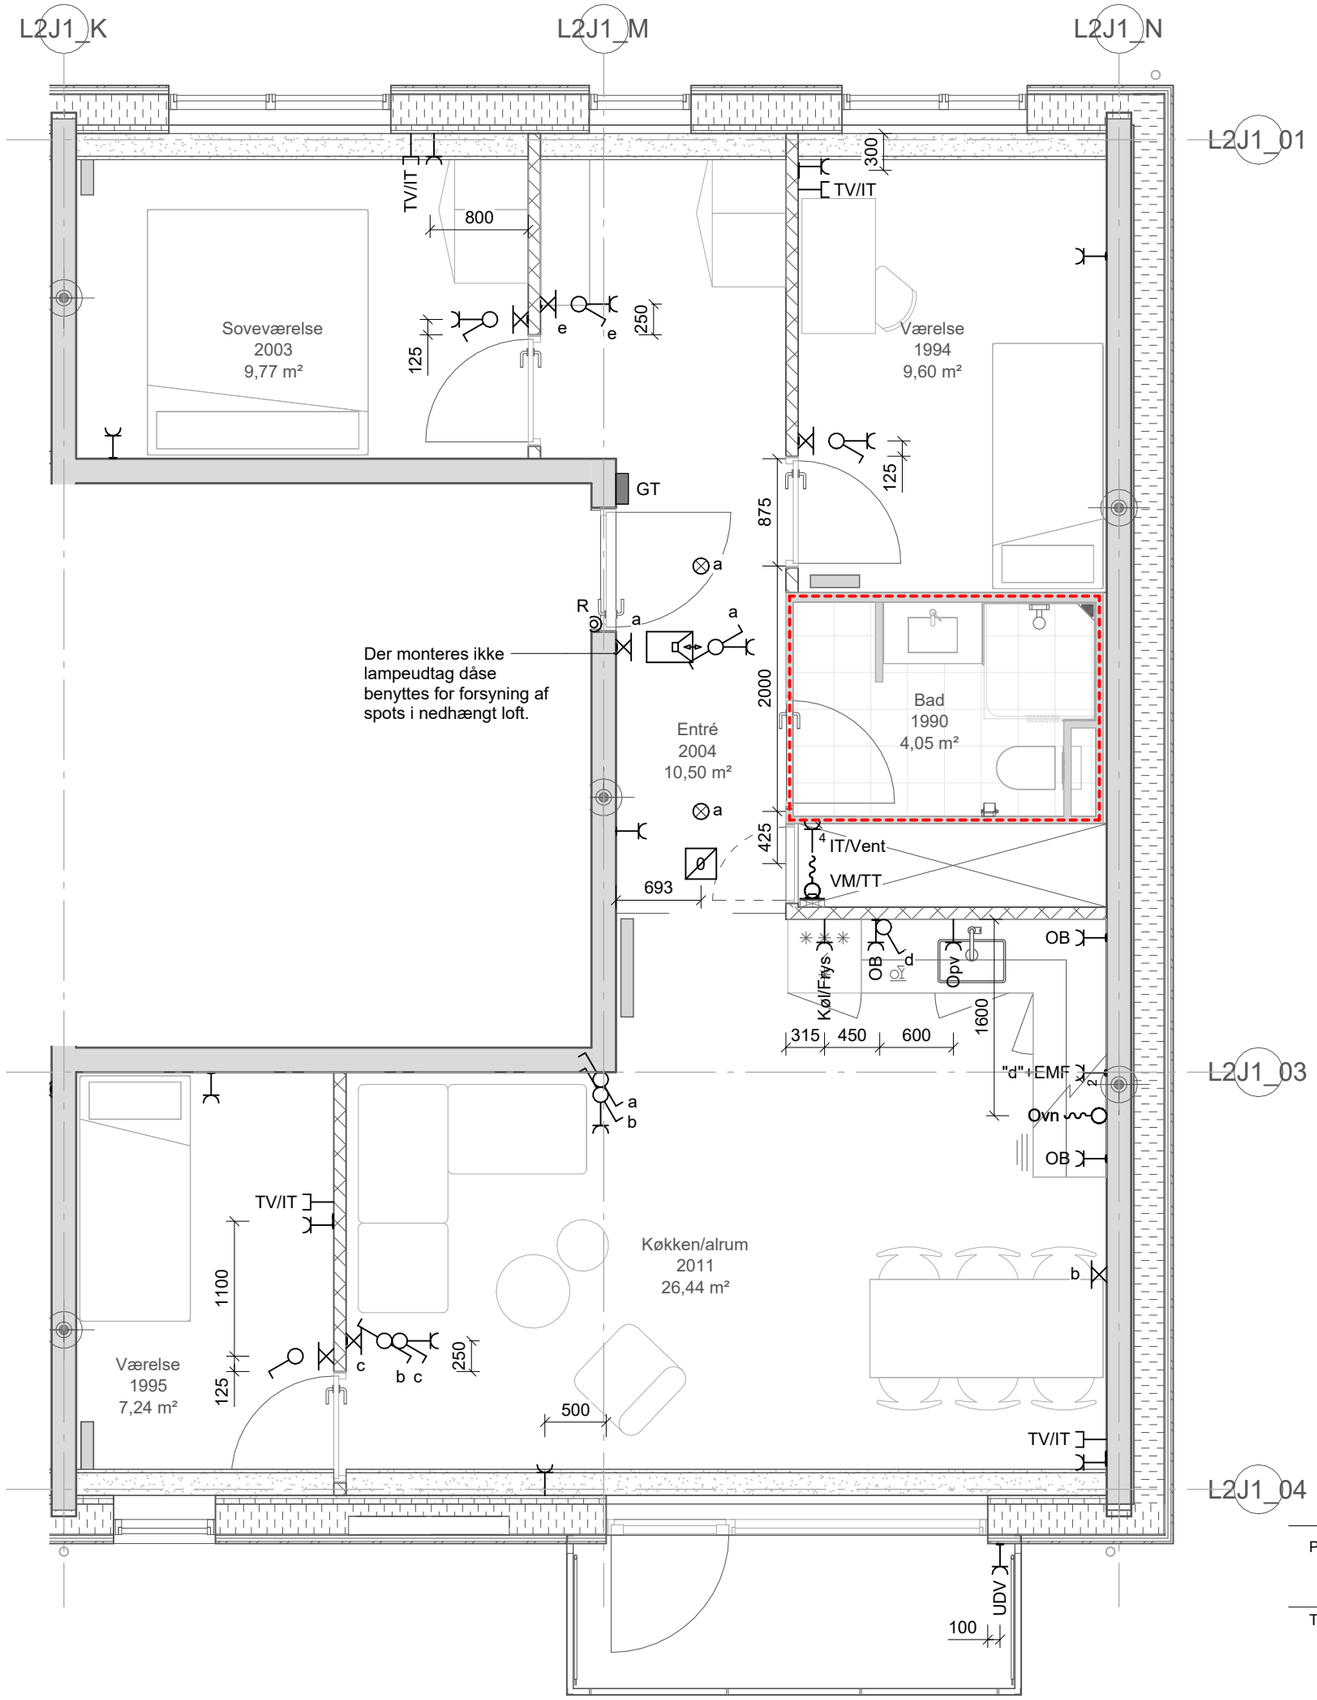

Projekt: Stejlepladsen


Tekst: Elinstallationer -
Byg J1 - 3. Sal, Byg D
OPG_4V_T32.3 - Side J1-41

Tegningsnr.: ISP2_K07_L2XX_H04_EXX_N930

Rev.:

Projektnr.: 1019198 | Dato: 2026-02-27 | Rev. Dato: | Mål: 1 : 50 | Side: J1-41

www.arteliagroup.dk | Fil:

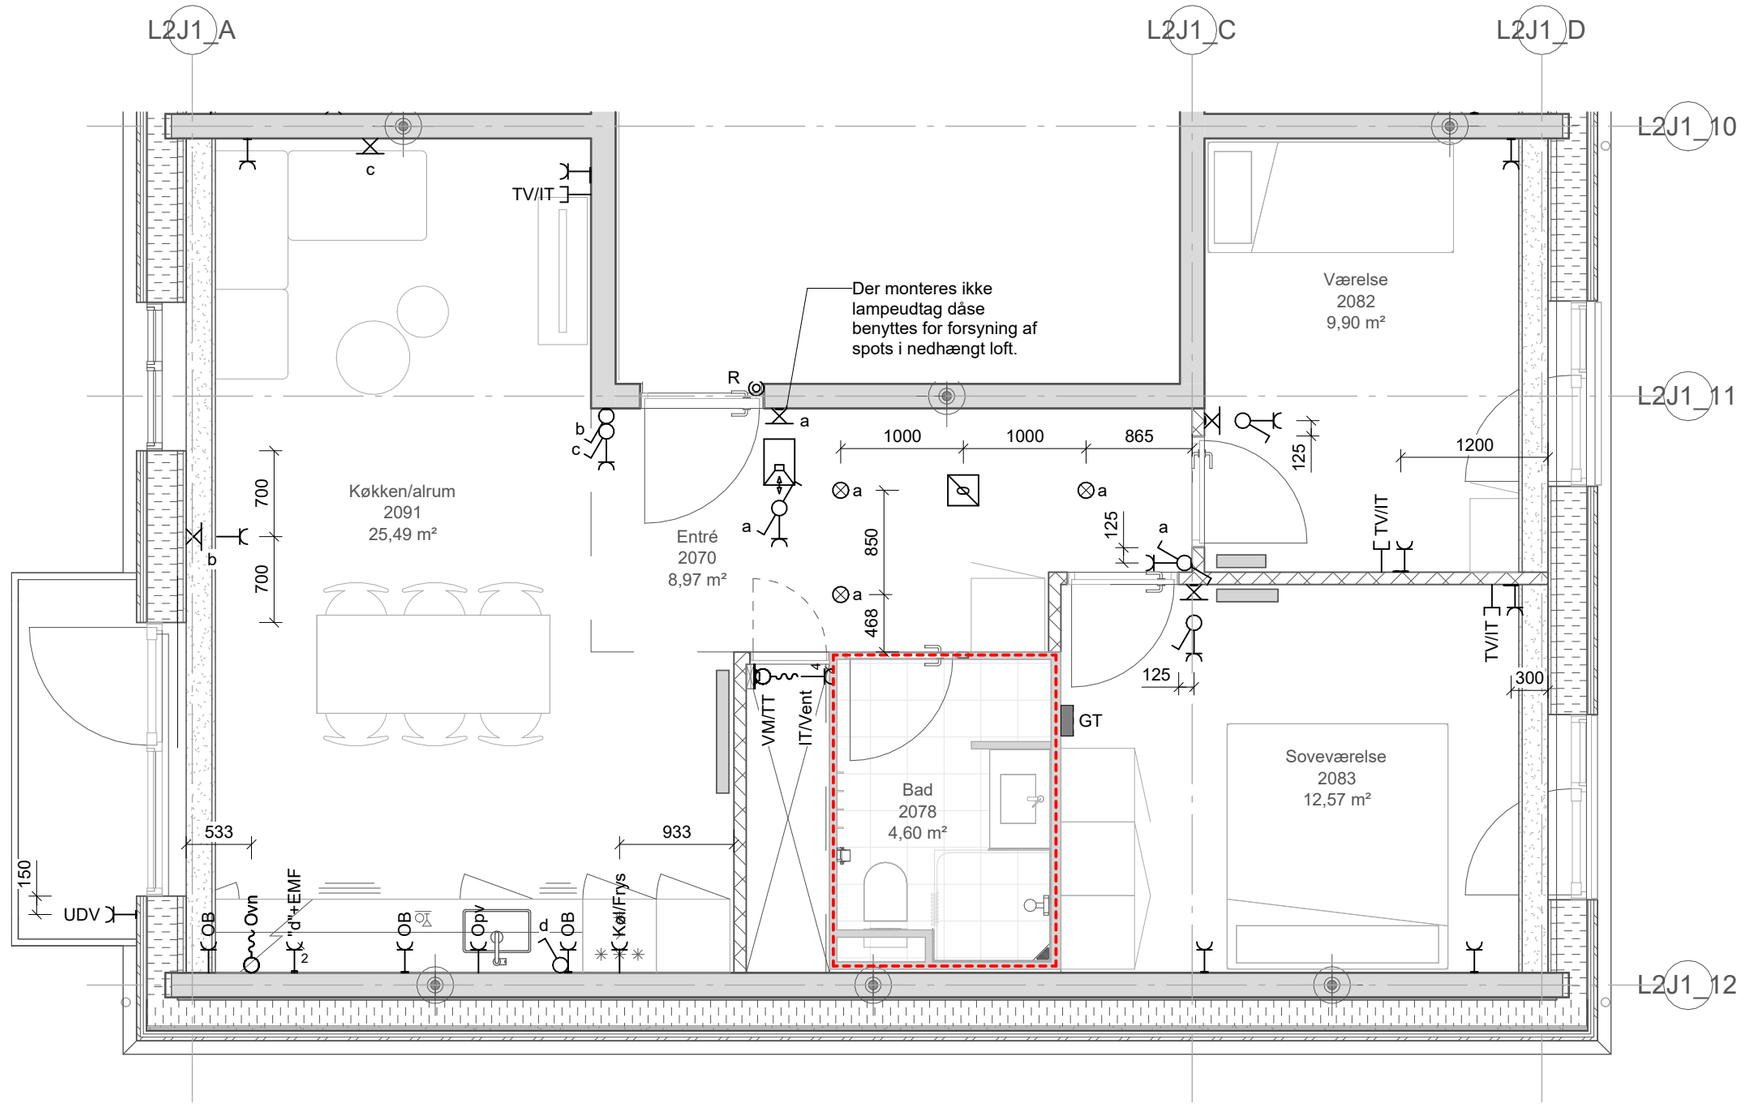

Projekt: Stejlepladsen


Tekst: Elinstallationer -
Byg J1 - 4. Sal, Byg A
OPG_3V_T30_S - Side J1-42

Tegningsnr.: ISP2_K07_L2XX_H04_EXX_N930

Rev.:

Projektnr.: 1019198 | Dato: 2026-02-27 | Rev. Dato: | Mål: 1 : 50 | Side: J1-42

www.arteliagroup.dk | Fil:

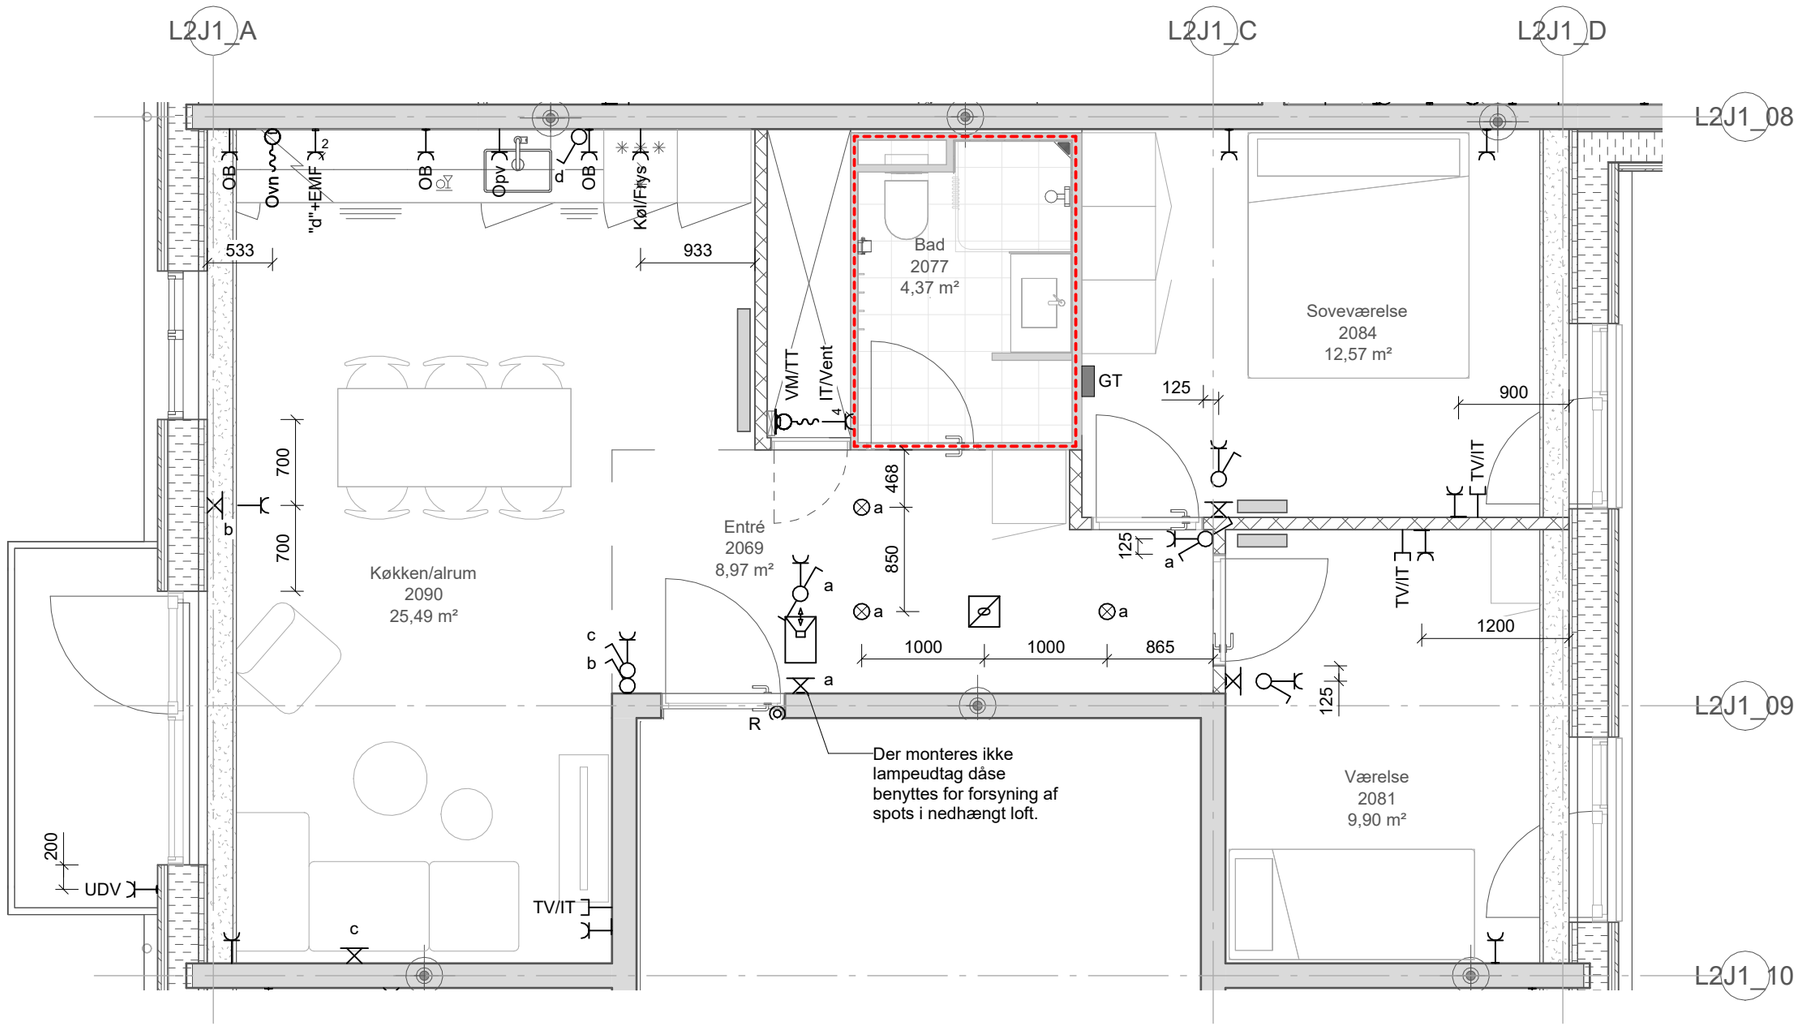

Projekt: Stejlepladsen


Tekst: Elinstallationer -
Byg J1 - 4. Sal, Byg A
OPG_3V_T30 - Side J1-43

Tegningsnr.: ISP2_K07_L2XX_H04_EXX_N930

Rev.:

Projektnr.: 1019198 | Dato: 2026-02-27 | Rev. Dato: | Mål: 1 : 50 | Side: J1-43

www.arteliagroup.dk | Fil:

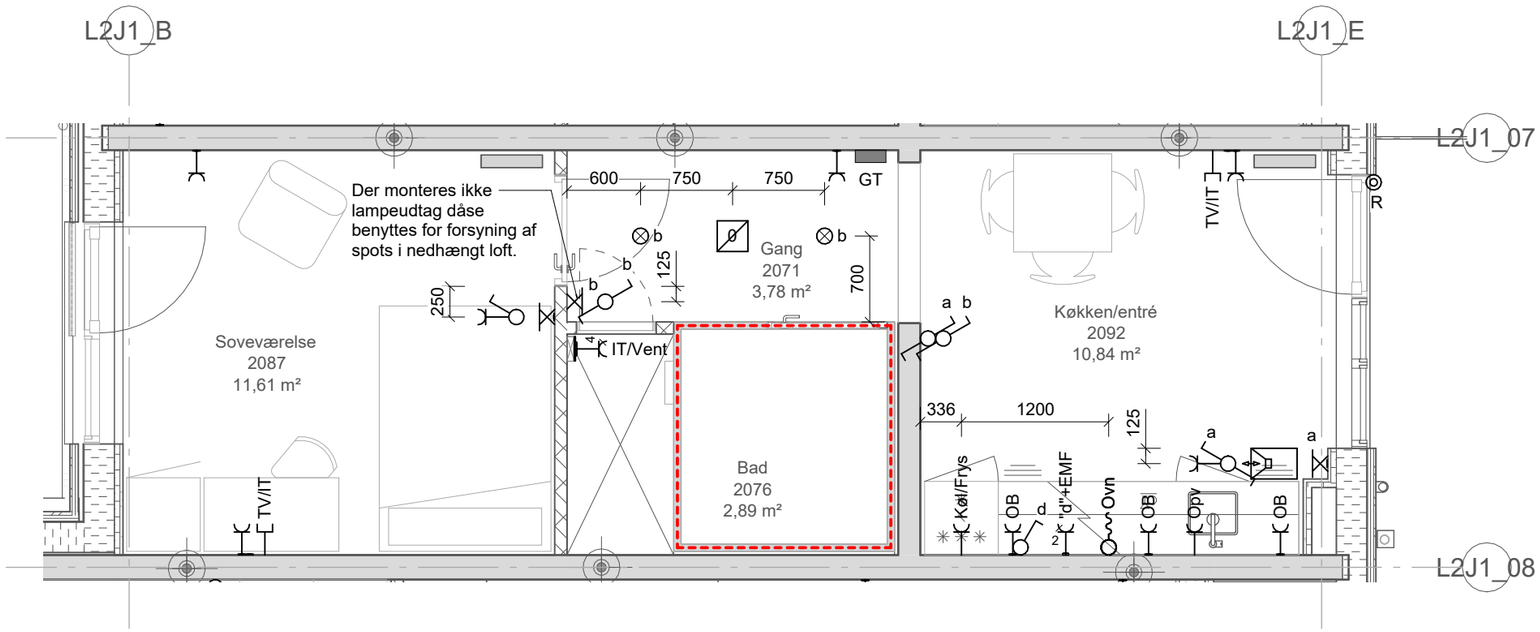

Projekt: Stejlepladsen


Tekst: Elinstallationer -
Byg J1 - 4. Sal, Byg B
ALT_1V_T31 - Side J1-44

Tegningsnr.: ISP2_K07_L2XX_H04_EXX_N930


Rev.:

Projektnr.: 1019198 | Dato: 2026-02-27 | Rev. Dato: | Mål: 1 : 50 | Side: J1-44

www.arteliagroup.dk | Fil:

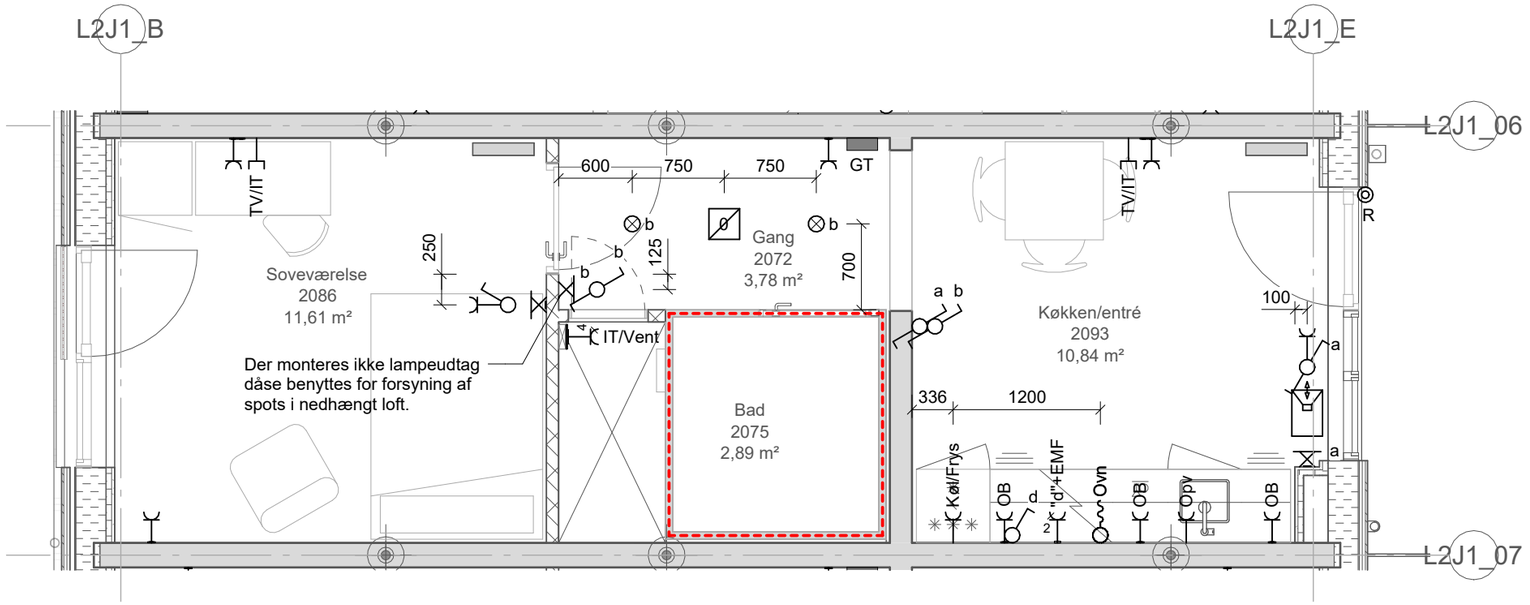

Projekt:	Stejlepladsen				
Tekst:	Elinstallationer - Byg J1 - 4. Sal, Byg B ALT_1V_T31.4 - Side J1-45			Tegningsnr.:	Rev.:
			ISP2_K07_L2XX_H04_EXX_N930		
Projektnr.: 1019198	Dato: 2026-02-27	Rev. Dato:		Mål: 1 : 50	Side: J1-45
www.arteliagroup.dk	Fil:				

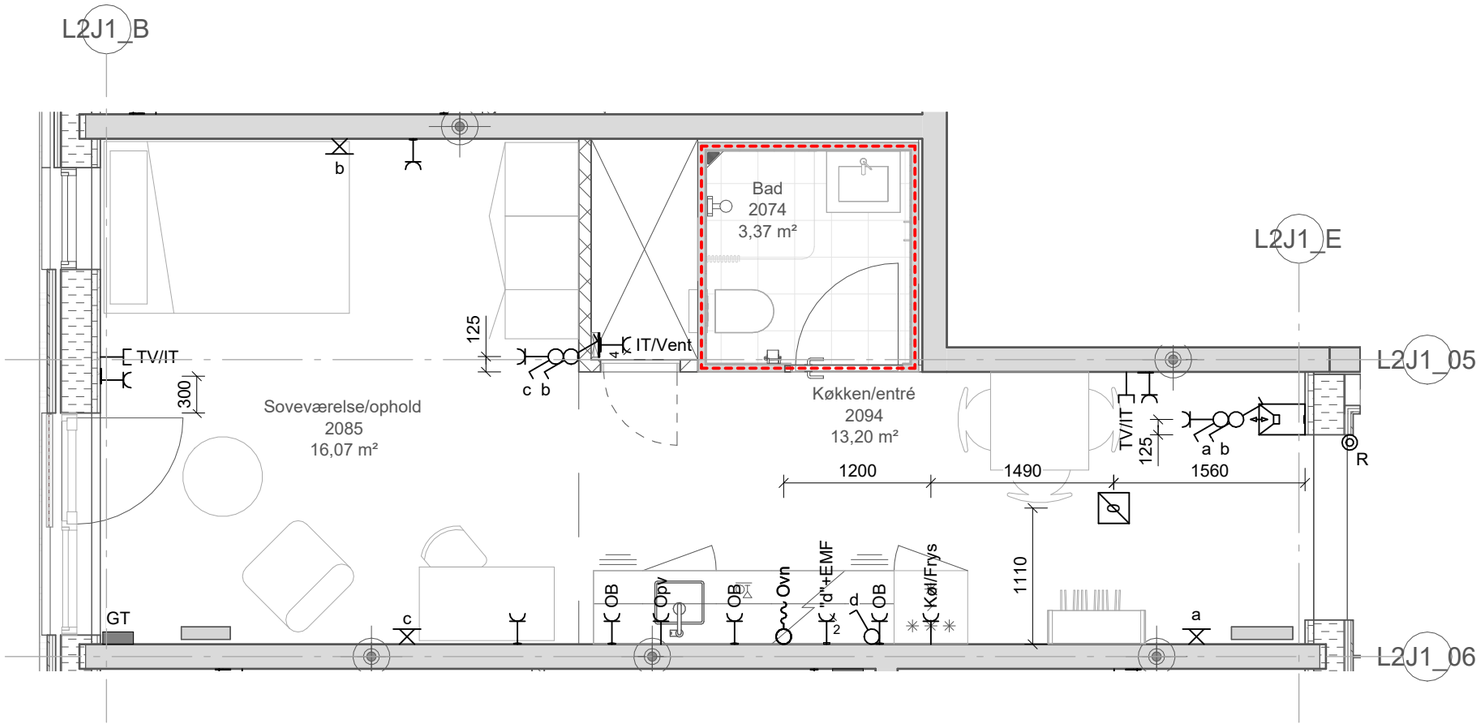

Projekt: Stejlepladsen

ARTELIA


Tekst: Elinstallationer -
Byg J1 - 4. Sal, Byg B
ALT_1V_T30 - Side J1-46

Tegningsnr.: ISP2_K07_L2XX_H04_EXX_N930


Rev.:

Projektnr.: 1019198 | Dato: 2026-02-27 | Rev. Dato: | Mål: 1 : 50 | Side: J1-46

www.arteliagroup.dk | Fil:

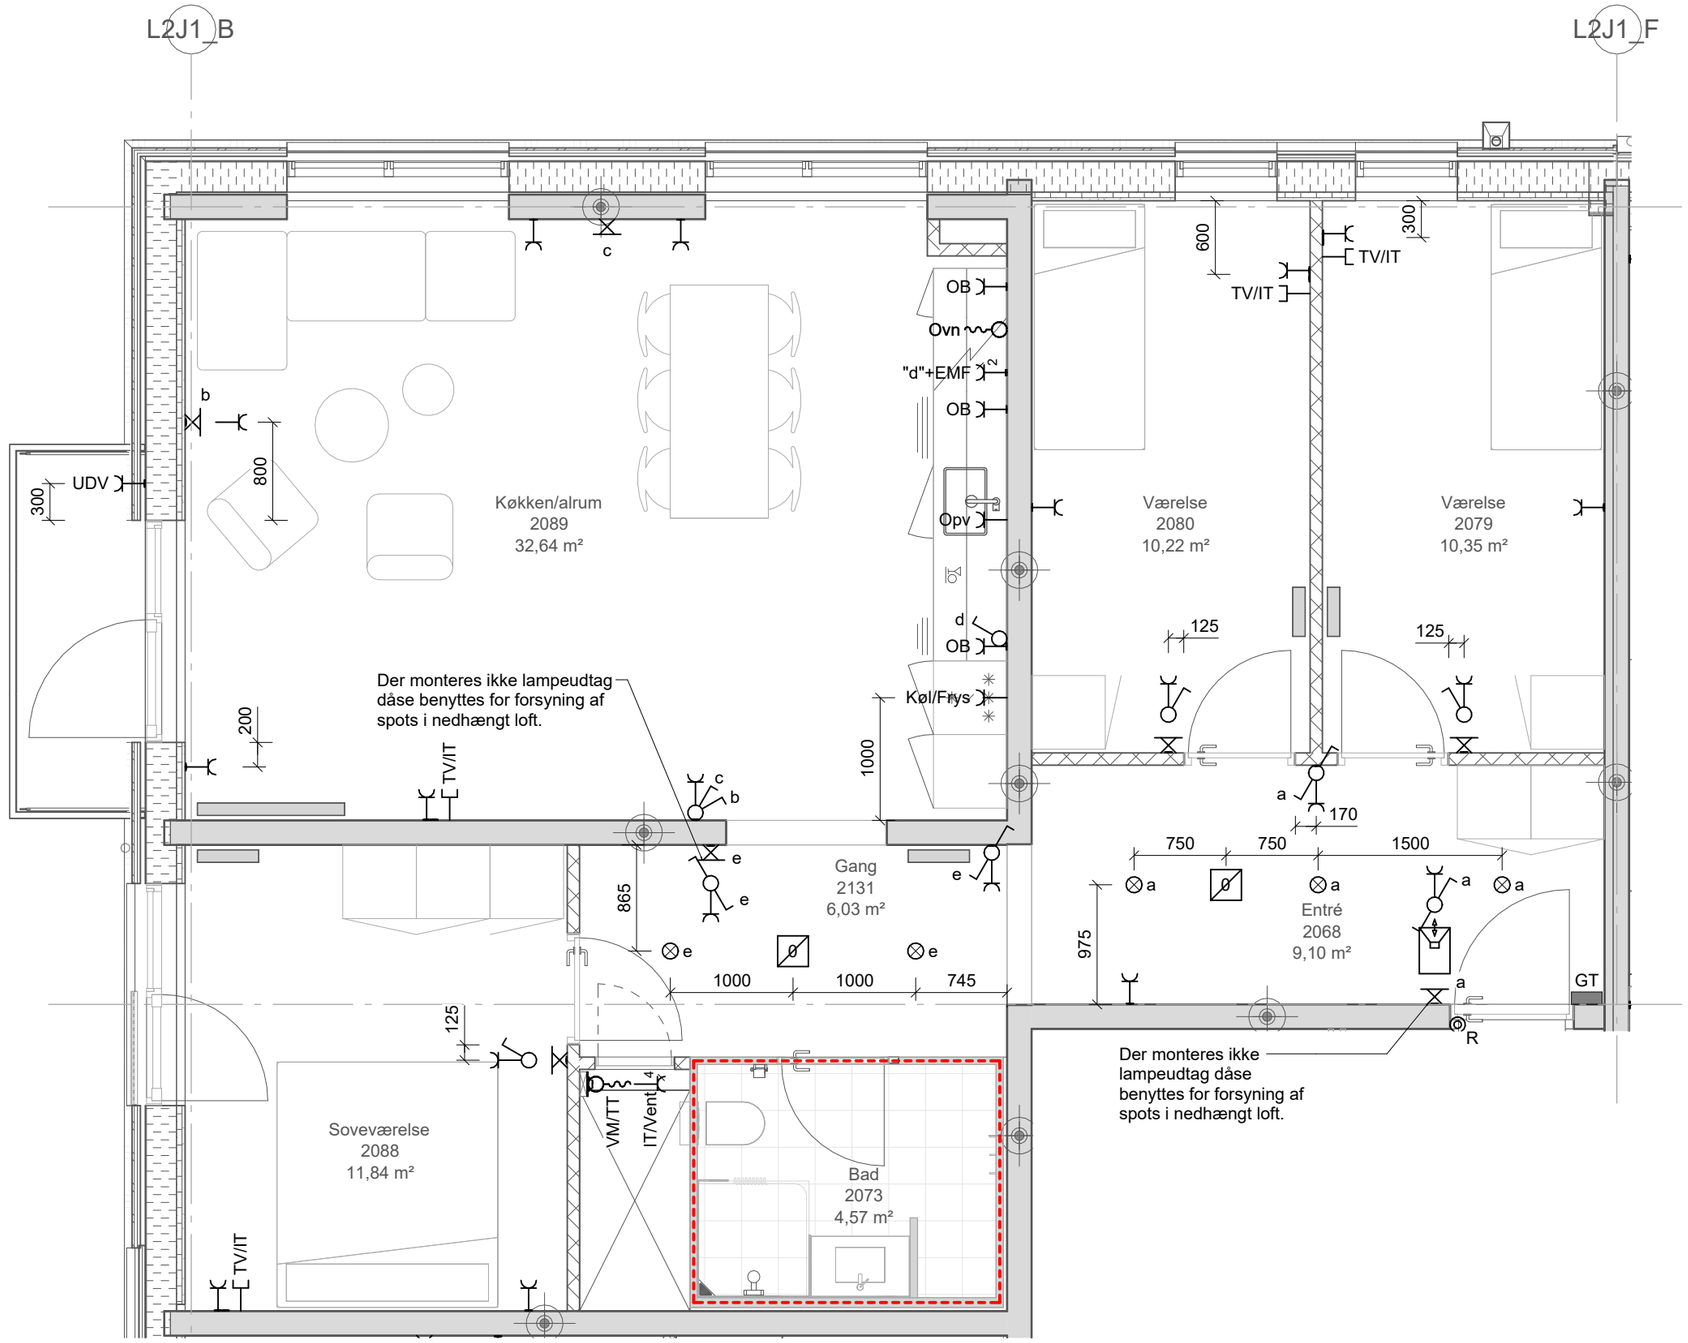

Projekt:	Stejlepladsen				
Tekst:	Elinstallationer - Byg J1 - 4. Sal, Byg B OPG_4V_T31 - Side J1-47			Tegningsnr.:	Rev.:
			ISP2_K07_L2XX_H04_EXX_N930		
Projektnr.: 1019198	Dato: 2026-02-27	Rev. Dato:		Mål: 1 : 50	Side: J1-47
www.arteliagroup.dk	Fil:				

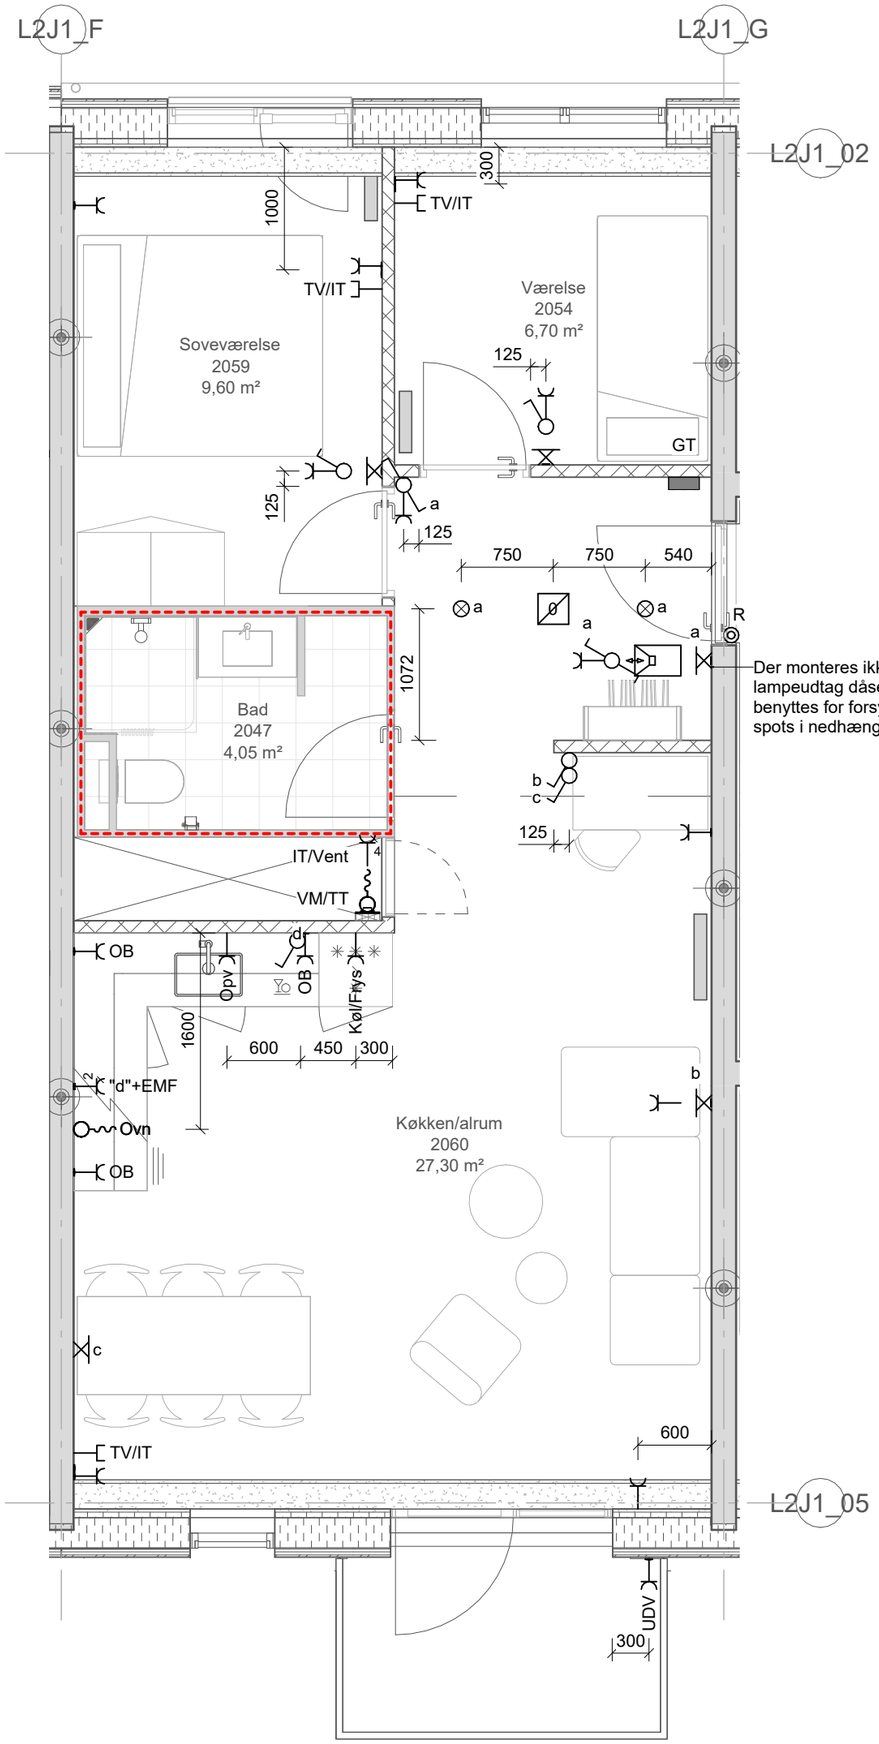

Projekt: Stejlepladsen


Tekst: Elinstallationer -
Byg J1 - 4. Sal, Byg C
OPG_3V_T34 - Side J1-48

Tegningsnr.: ISP2_K07_L2XX_H04_EXX_N930


Rev.:

Projektnr.: 1019198 | Dato: 2026-02-27 | Rev. Dato: | Mål: 1 : 50 | Side: J1-48


www.arteliagroup.dk | Fil:

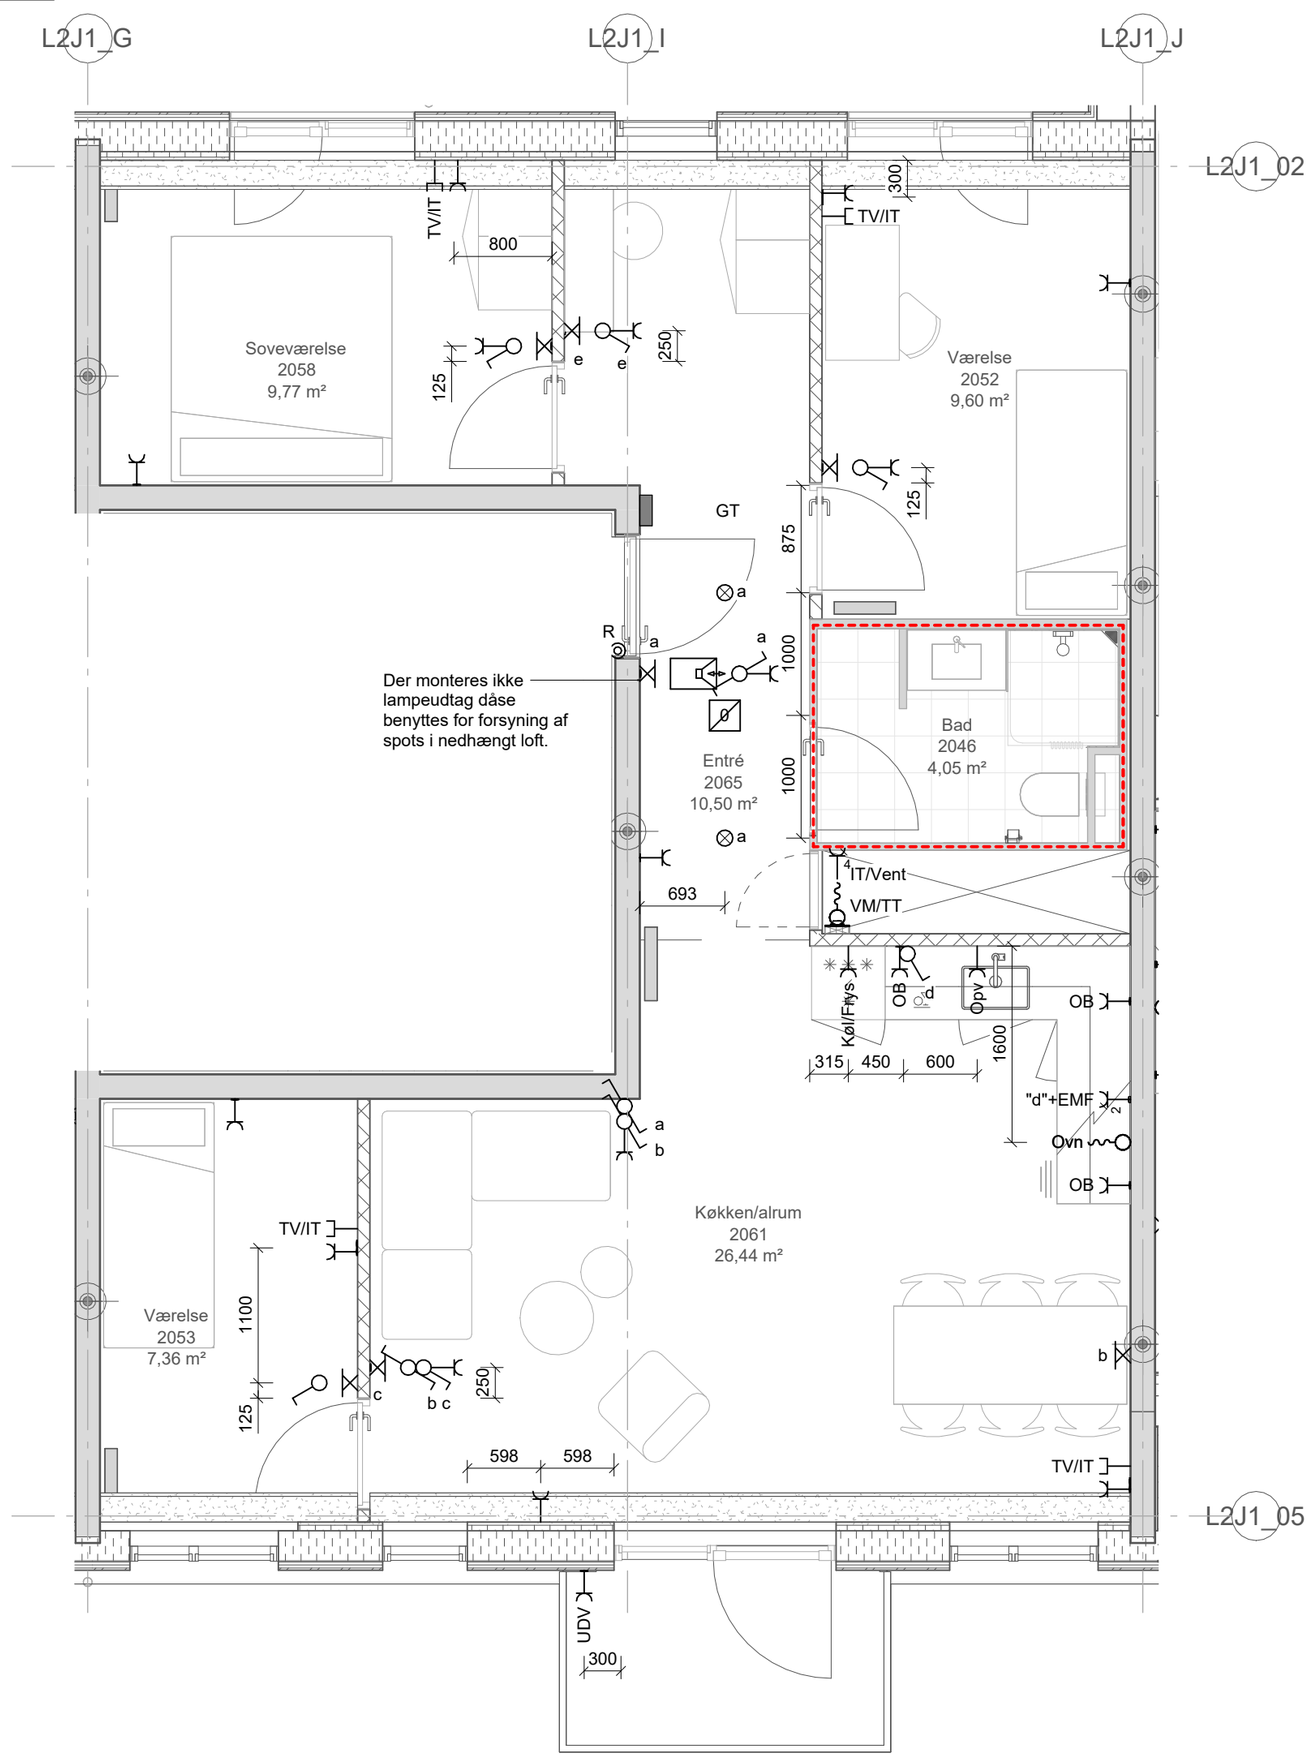


Projekt:	Stejlepladsen				
Tekst:	Elinstallationer - Byg J1 - 4. Sal, Byg C OPG_4V_T32 - Side J1-49			Tegningsnr.:	Rev.:
			ISP2_K07_L2XX_H04_EXX_N930		
Projektnr.: 1019198	Dato: 2026-02-27	Rev. Dato:		Mål: 1 : 50	Side: J1-49
www.arteliagroup.dk	Fil:				

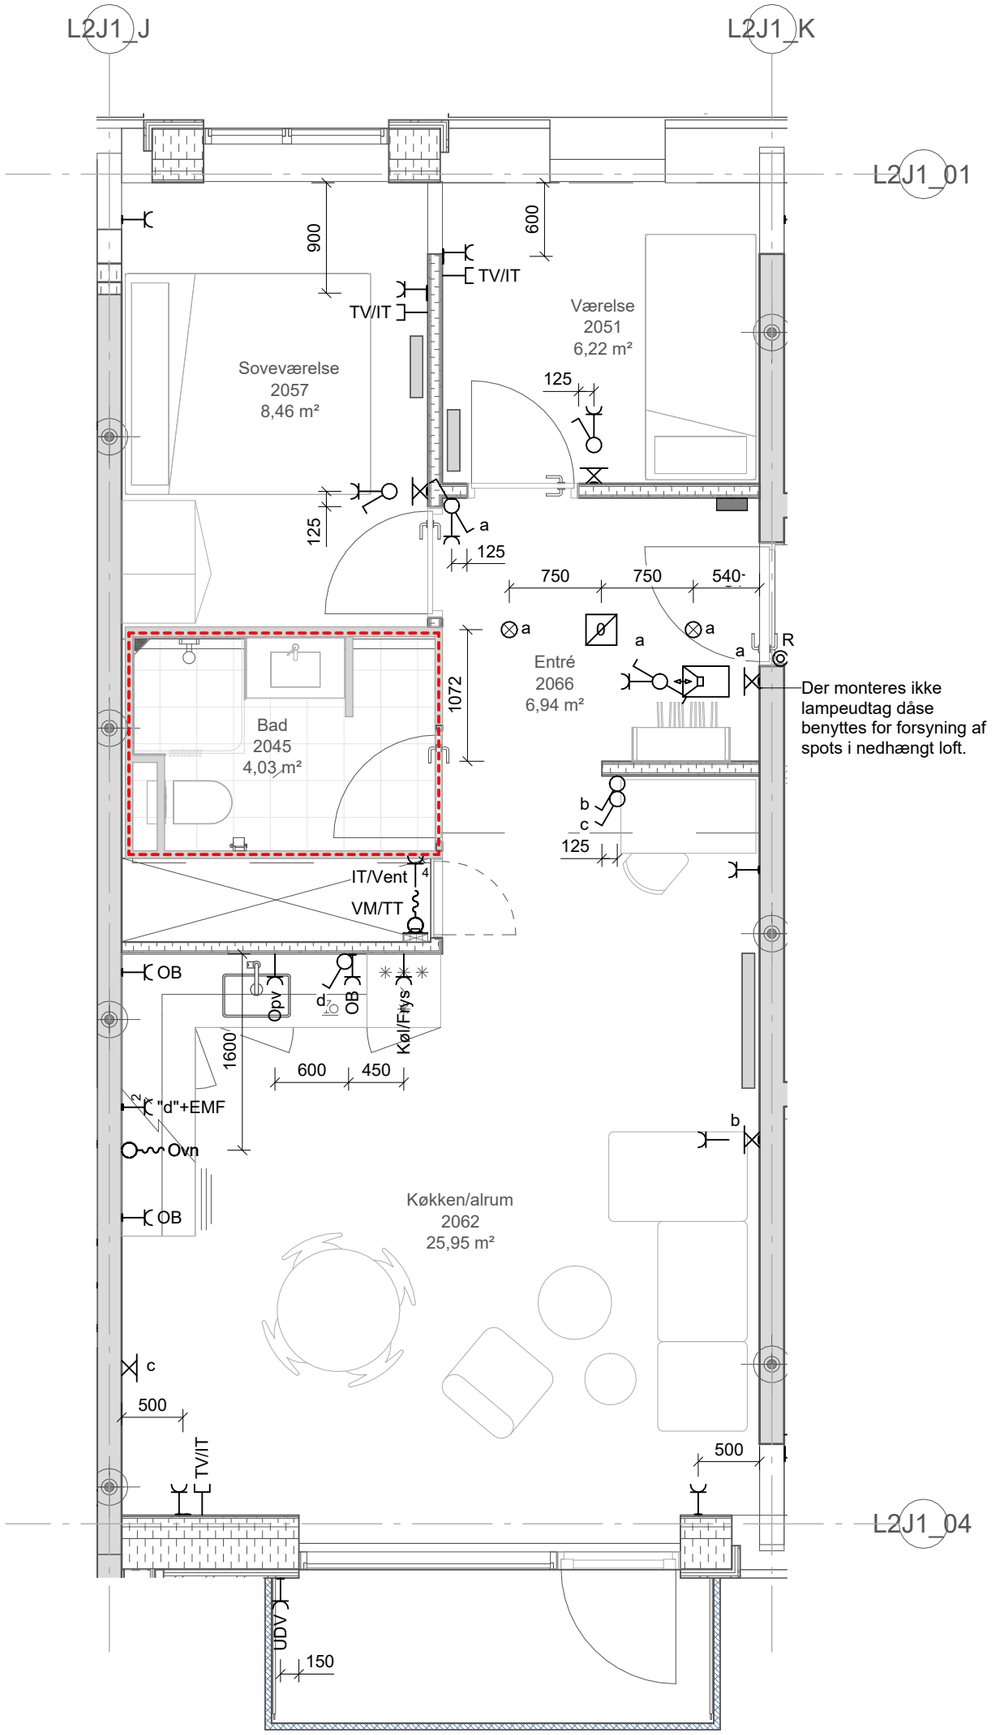

Projekt:	Stejlepladsen				
Tekst:	Elinstallationer - Byg J1 - 4. Sal, Byg D OPG_3V_T34_TA - Side J1-50			Tegningsnr.:	Rev.:
			ISP2_K07_L2XX_H04_EXX_N930		
Projektnr.: 1019198	Dato: 2026-02-27	Rev. Dato:		Mål: 1 : 50	Side: J1-50
www.arteliagroup.dk	Fil:				

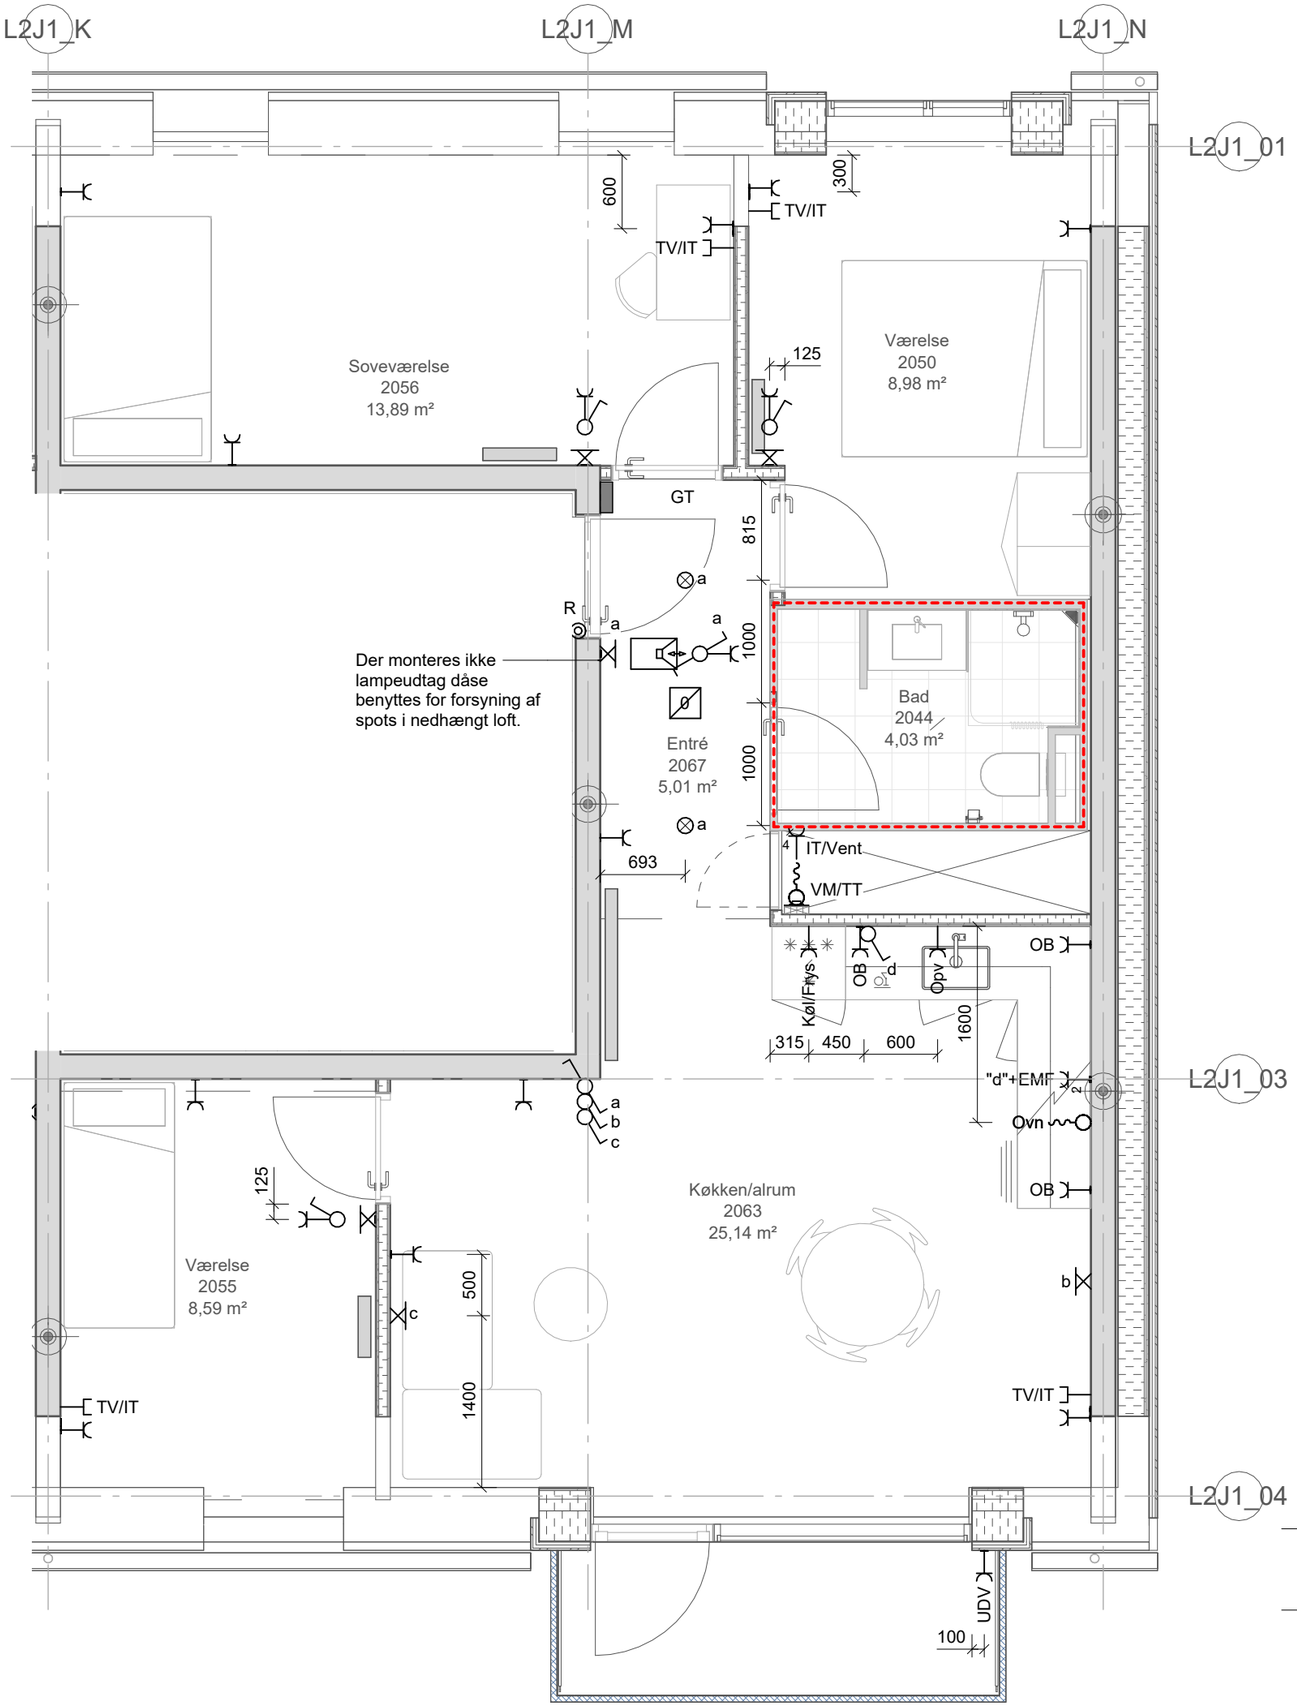

Projekt:	Stejlepladsen				
Tekst:	Elinstallationer - Byg J1 - 4. Sal, Byg D OPG_4V_T33_TA - Side J1-51			Tegningsnr.:	Rev.:
				ISP2_K07_L2XX_H04_EXX_N930	
Projektnr.: 1019198	Dato: 2026-02-27	Rev. Dato:		Mål: 1 : 50	Side: J1-51
www.arteliagroup.dk	Fil:				

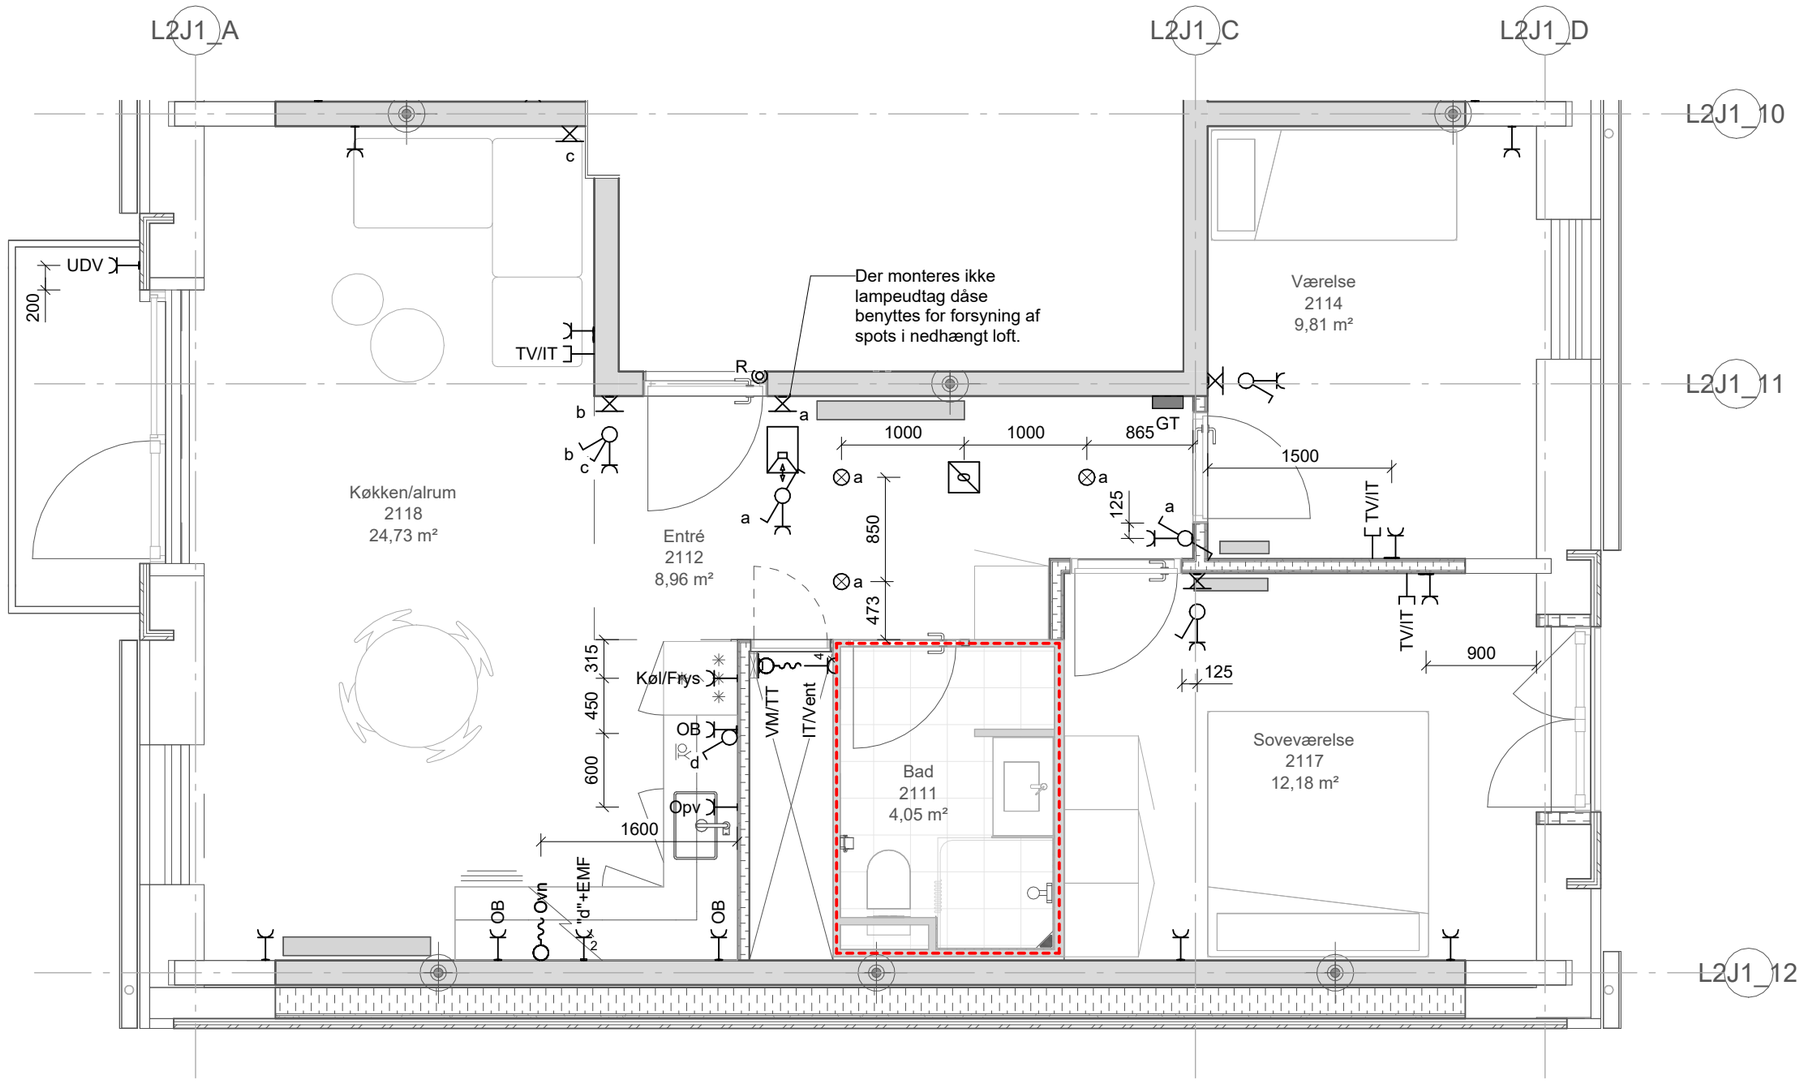

Projekt: Stejlepladsen


Tekst: Elinstallationer -
Byg J1 - 5. Sal, Byg A
OPG_3V_T31_TA_S - Side J1-52

Tegningsnr.: ISP2_K07_L2XX_H04_EXX_N930

Rev.:

Projektnr.: 1019198 | Dato: 2026-02-27 | Rev. Dato: | Mål: 1 : 50 | Side: J1-52

www.arteliagroup.dk | Fil:

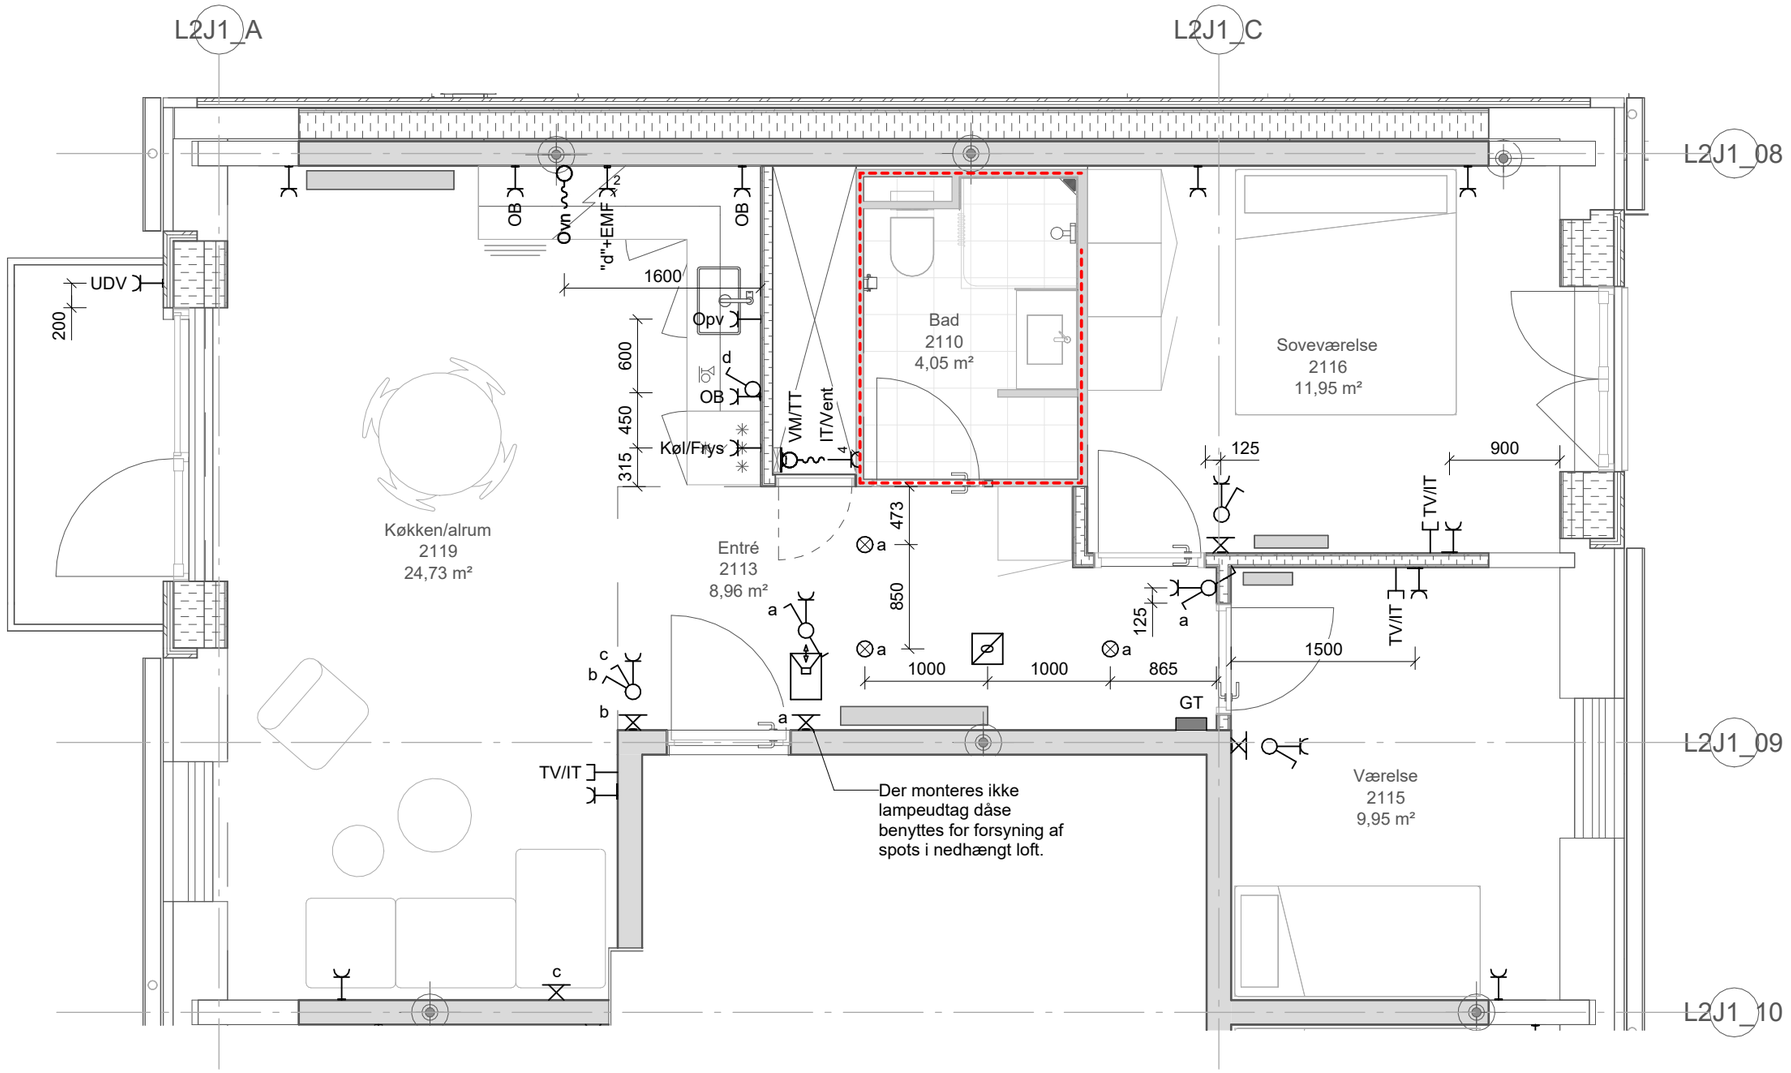

Projekt: Stejlepladsen


Tekst: Elinstallationer -
Byg J1 - 5. Sal, Byg A
OPG_3V_T31_TA - Side J1-53

Tegningsnr.: ISP2_K07_L2XX_H04_EXX_N930

Rev.:

Projektnr.: 1019198 | Dato: 2026-02-27 | Rev. Dato: | Mål: 1 : 50 | Side: J1-53

www.arteliagroup.dk | Fil:

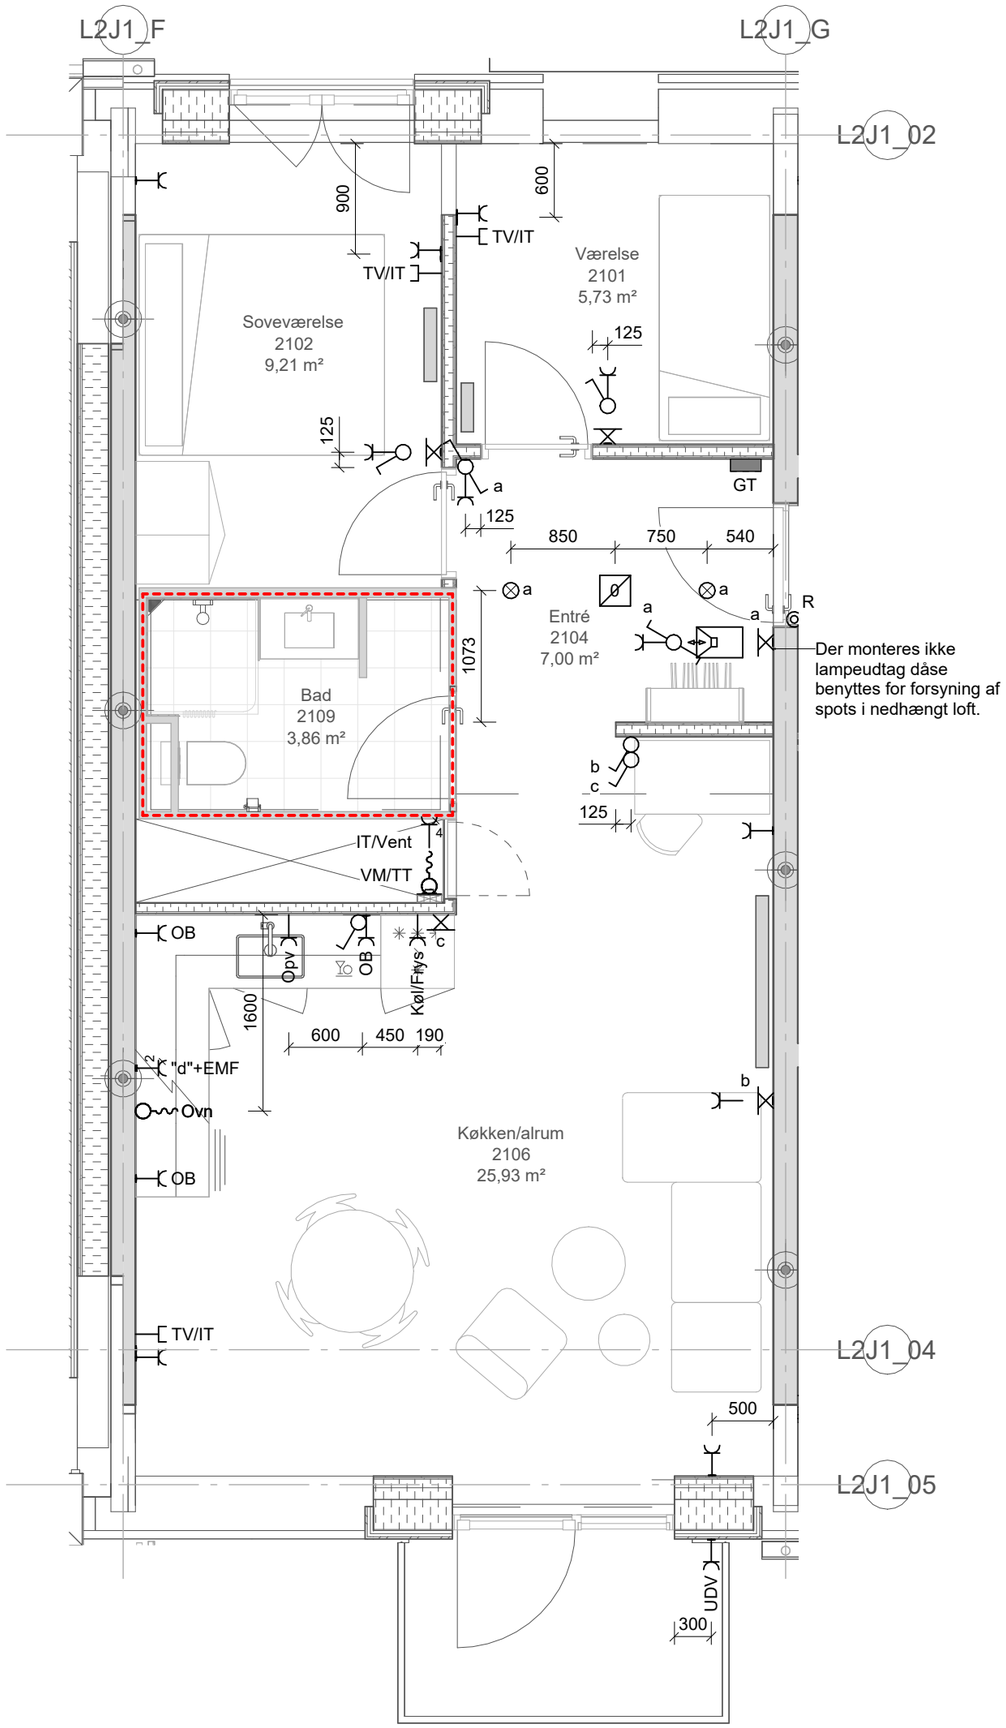

Projekt: Stejlepladsen


Tekst: Elinstallationer -
Byg J1 - 5. Sal, Byg C
OPG_3V_T34_TA - Side J1-54

Tegningsnr.: ISP2_K07_L2XX_H04_EXX_N930

Rev.:

Projektnr.: 1019198 | Dato: 2026-02-27 | Rev. Dato: | Mål: 1 : 50 | Side: J1-54

www.arteliagroup.dk | Fil:

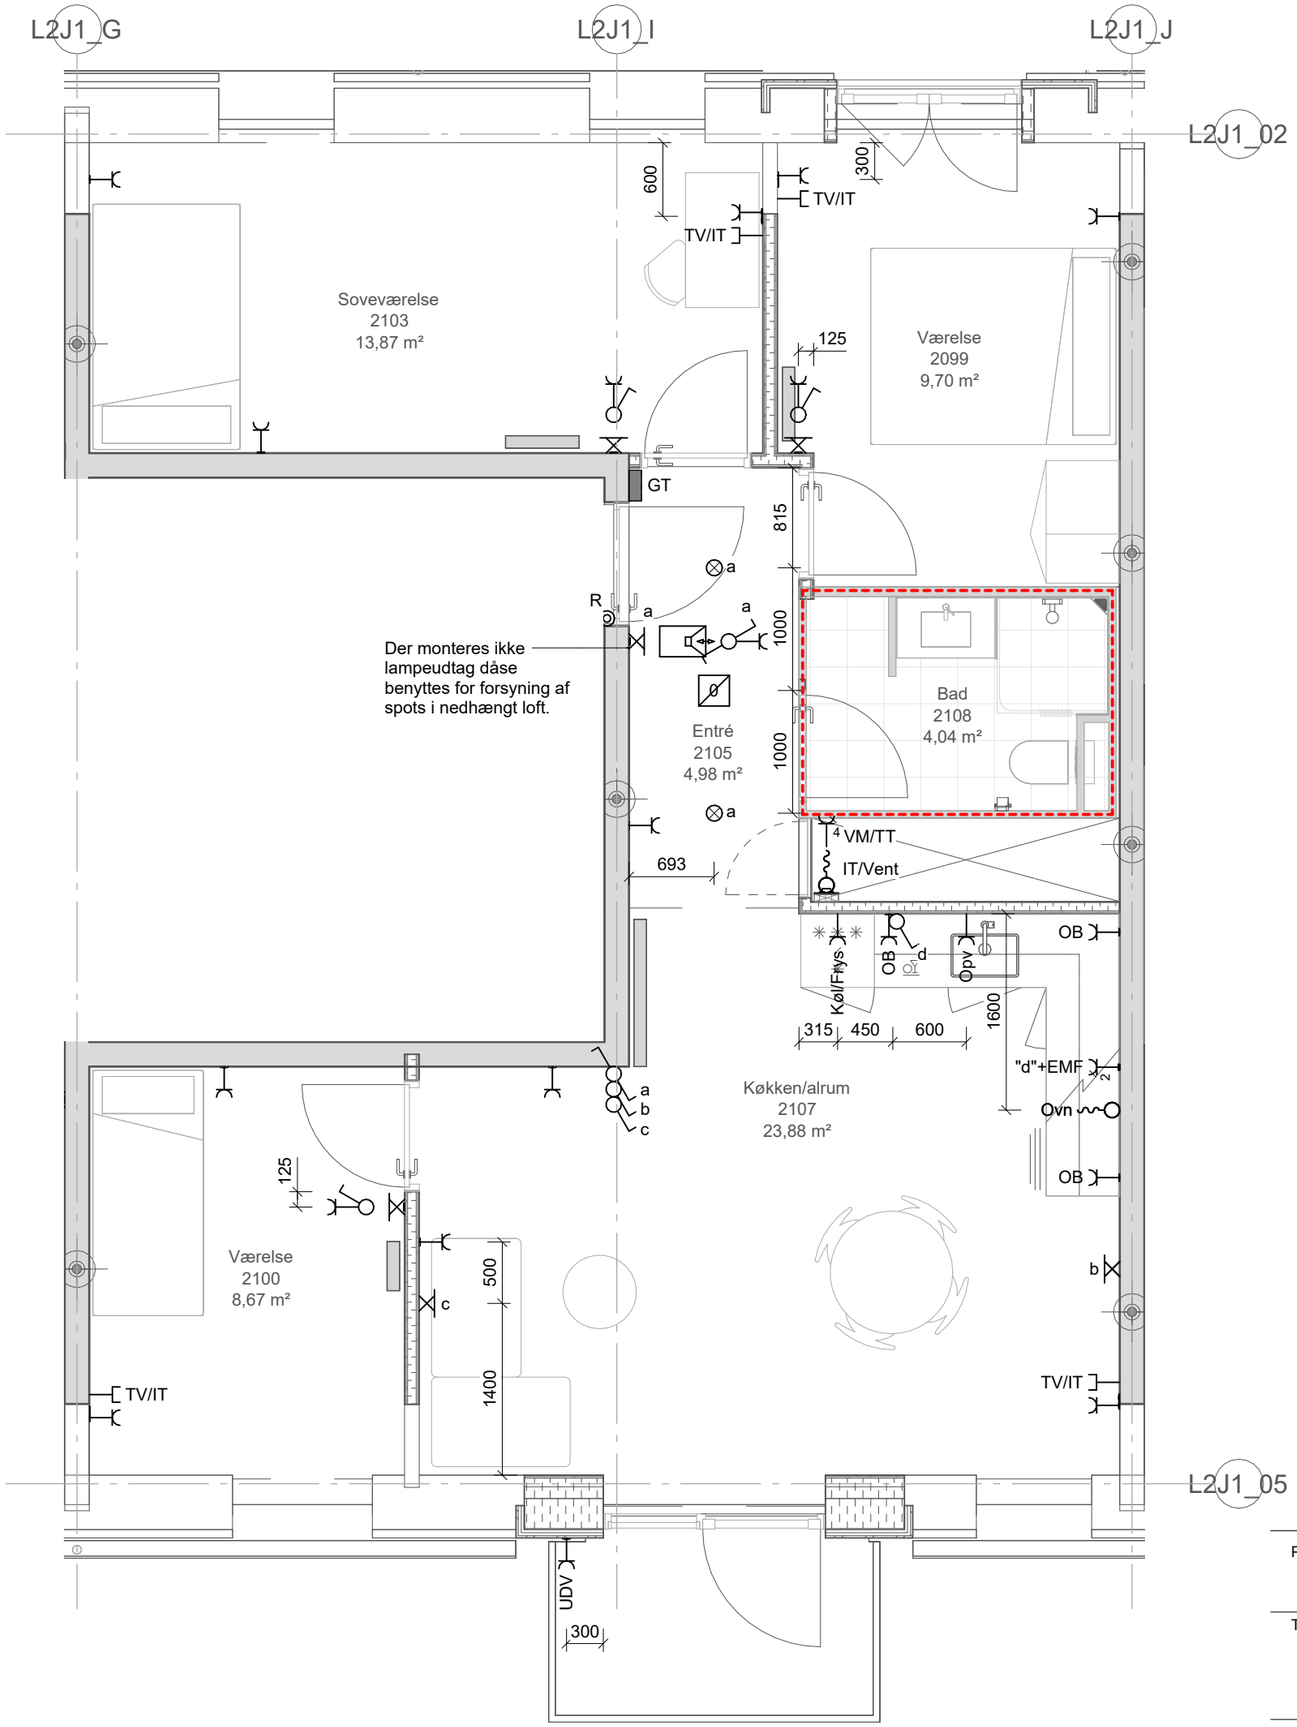

Projekt: Stejlepladsen

Tekst: Elinstallationer -
Byg J1 - 5. Sal, Byg C
OPG_4V_T33_TA - Side J1-55

Tegningsnr.: ISP2_K07_L2XX_H04_EXX_N930

Rev.:

Projektnr.: 1019198 | Dato: 2026-02-27 | Rev. Dato: | Mål: 1 : 50 | Side: J1-55

www.arteliagroup.dk | Fil: