Sheet Number	Tekst:	Dato:	Rev.:	Rev. Dato:
ISP2_K07_L2XX_H04_EXX_N930 - Side J2-1	Byg J2 - Index	2026-02-27		
ISP2_K07_L2XX_H04_EXX_N930 - Side J2-2	Byg J2 - Oversigtsplan	2026-02-27		
ISP2_K07_L2XX_H04_EXX_N930 - Side J2-3	Byg J2 - Stueplan, Byg B	2026-02-27		
ISP2_K07_L2XX_H04_EXX_N930 - Side J2-4	Byg J2 - Stueplan, Byg B	2026-02-27		
ISP2_K07_L2XX_H04_EXX_N930 - Side J2-5	Byg J2 - Stueplan, Byg B	2026-02-27		
ISP2_K07_L2XX_H04_EXX_N930 - Side J2-6	Byg J2 - 1. Sal, Byg A	2026-02-27		
ISP2_K07_L2XX_H04_EXX_N930 - Side J2-7	Byg J2 - 1. Sal, Byg A	2026-02-27		
ISP2_K07_L2XX_H04_EXX_N930 - Side J2-8	Byg J2 - 1. Sal, Byg B	2026-02-27		
ISP2_K07_L2XX_H04_EXX_N930 - Side J2-9	Byg J2 - 1. Sal, Byg B	2026-02-27		
ISP2_K07_L2XX_H04_EXX_N930 - Side J2-10	Byg J2 - 1. Sal, Byg B	2026-02-27		
ISP2_K07_L2XX_H04_EXX_N930 - Side J2-11	Byg J2 - 1. Sal, Byg B	2026-02-27		
ISP2_K07_L2XX_H04_EXX_N930 - Side J2-12	Byg J2 - 1. Sal, Byg B	2026-02-27		
ISP2_K07_L2XX_H04_EXX_N930 - Side J2-13	Byg J2 - 1. Sal, Byg B	2026-02-27		
ISP2_K07_L2XX_H04_EXX_N930 - Side J2-14	Byg J2 - 2. Sal, Byg A	2026-02-27		
ISP2_K07_L2XX_H04_EXX_N930 - Side J2-15	Byg J2 - 2. Sal, Byg A	2026-02-27		
ISP2_K07_L2XX_H04_EXX_N930 - Side J2-16	Byg J2 - 2. Sal, Byg B	2026-02-27		
ISP2_K07_L2XX_H04_EXX_N930 - Side J2-17	Byg J2 - 2. Sal, Byg B	2026-02-27		
ISP2_K07_L2XX_H04_EXX_N930 - Side J2-18	Byg J2 - 2. Sal, Byg B	2026-02-27		
ISP2_K07_L2XX_H04_EXX_N930 - Side J2-19	Byg J2 - 2. Sal, Byg B	2026-02-27		
ISP2_K07_L2XX_H04_EXX_N930 - Side J2-20	Byg J2 - 2. Sal, Byg B	2026-02-27		
ISP2_K07_L2XX_H04_EXX_N930 - Side J2-21	Byg J2 - 2. Sal, Byg B	2026-02-27		
ISP2_K07_L2XX_H04_EXX_N930 - Side J2-22	Byg J2 - 3. Sal, Byg A	2026-02-27		
ISP2_K07_L2XX_H04_EXX_N930 - Side J2-23	Byg J2 - 3. Sal, Byg A	2026-02-27		
ISP2_K07_L2XX_H04_EXX_N930 - Side J2-24	Byg J2 - 3. Sal, Byg B	2026-02-27		
ISP2_K07_L2XX_H04_EXX_N930 - Side J2-25	Byg J2 - 3. Sal, Byg B	2026-02-27		
ISP2_K07_L2XX_H04_EXX_N930 - Side J2-26	Byg J2 - 3. Sal, Byg B	2026-02-27		
ISP2_K07_L2XX_H04_EXX_N930 - Side J2-27	Byg J2 - 4. Sal, Byg A	2026-02-27		
ISP2_K07_L2XX_H04_EXX_N930 - Side J2-28	Byg J2 - 4. Sal, Byg A	2026-02-27		
ISP2_K07_L2XX_H04_EXX_N930 - Side J2-29	Byg J2 - 4. Sal, Byg B	2026-02-27		
ISP2_K07_L2XX_H04_EXX_N930 - Side J2-30	Byg J2 - 4. Sal, Byg B	2026-02-27		
ISP2_K07_L2XX_H04_EXX_N930 - Side J2-31	Byg J2 - 4. Sal, Byg B	2026-02-27		

Projekt: Stejlepladsen


Tekst: Elinstallationer - Byg J2 - Index


Tegningsnr.: ISP2_K07_L2XX_H04_EXX_N930


Rev.:


Projektnr.: 1019198 | Dato: 2026-02-27 | Rev. Dato: | Mål: | Side: J2-1

www.arteliagroup.dk | Fil:

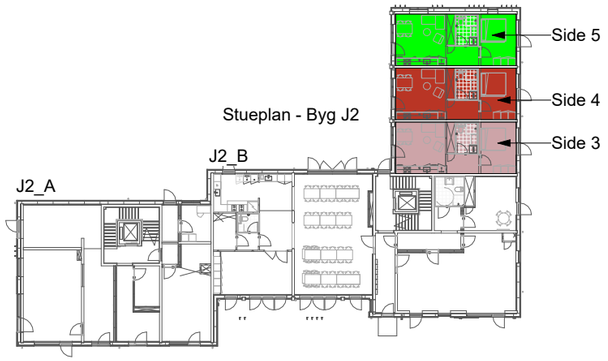

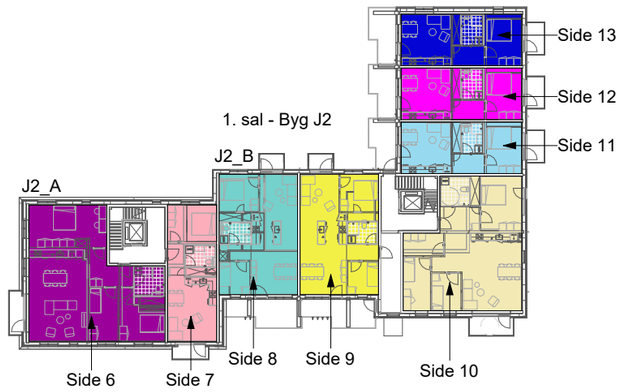

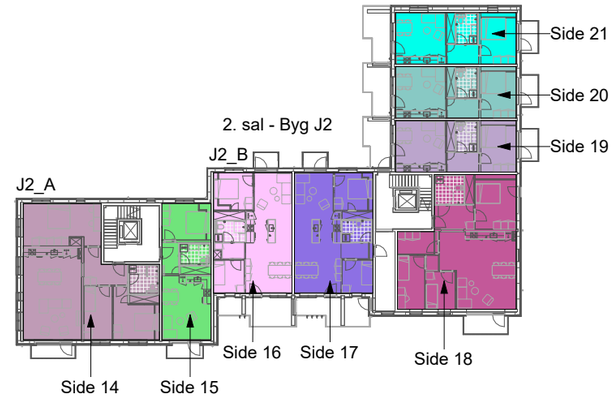

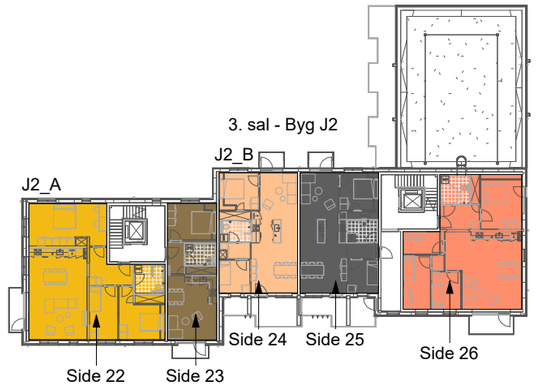



Oversigt, bygning J2:

Side 3: Altangangsbolig, Byg B, st, 2V

Side 4: Altangangsbolig, Byg B, st, 2V

Side 5: Altangangsbolig, Byg B, st, 2V

Side 6: Opgangsbolig, Byg A, 1.sal, 4V

Side 7: Opgangsbolig, Byg A, 1.sal, 2V

Side 8: Altangangsbolig, Byg B, 1.sal, 3V

Side 9: Altangangsbolig, Byg B, 1.sal, 3V

Side 10: Bofælleskab, Byg B, 1.sal, 4V

Side 11: Altangangsbolig, Byg B, 1.sal, 2V

Side 12: Altangangsbolig, Byg B, 1 sal, 2V

Side 13: Altangangsbolig, Byg B, 1 sal, 2V

Side 14: Opgangsbolig, Byg A, 2.sal, 4V

Side 15: Opgangsbolig, Byg A, 2.sal, 2V

Side 16: Altangangsbolig, Byg B, 2.sal, 3V

Side 17: Altangangsbolig, Byg B, 2.sal, 3V

Side 18: Bofælleskab, Byg B, 2.sal, 4V

Side 19: Altangangsbolig, Byg B, 2 sal, 2V

Side 20: Altangangsbolig, Byg B, 2 sal, 2V

Side 21: Altangangsbolig, Byg B, 2 sal, 2V

Side 22: Opgangsbolig, Byg A, 3.sal, 4V

Side 23: Opgangsbolig, Byg A, 3.sal, 2V

Side 24: Altangangsbolig, Byg B, 3.sal, 3V

Side 25: Altangangsbolig, Byg B, 3 sal, 3V

Side 26: Bofælleskab, Byg B, 3 sal, 4V

Side 27: Opgangsbolig, Byg A, 4.sal, 4V

Side 28: Opgangsbolig, Byg A, 4.sal, 2V

Side 29: Altangangsbolig, Byg B, 4.sal, 3V

Side 30: Altangangsbolig, Byg B, 4.sal, 3V

Side 31: Bofælleskab, Byg B, 4 sal, 4V

Projekt: Stejlepladsen


Tekst: Elinstallationer - Byg J2 - Oversigtsplan

Tegningsnr.: ISP2_K07_L2XX_H04_EXX_N930

Rev.:

Projektnr.: 1019198 | Dato: 2026-02-27 | Rev. Dato: | Mål: 1 : 500 | Side: J2-2

www.arteliagroup.dk | Fil:

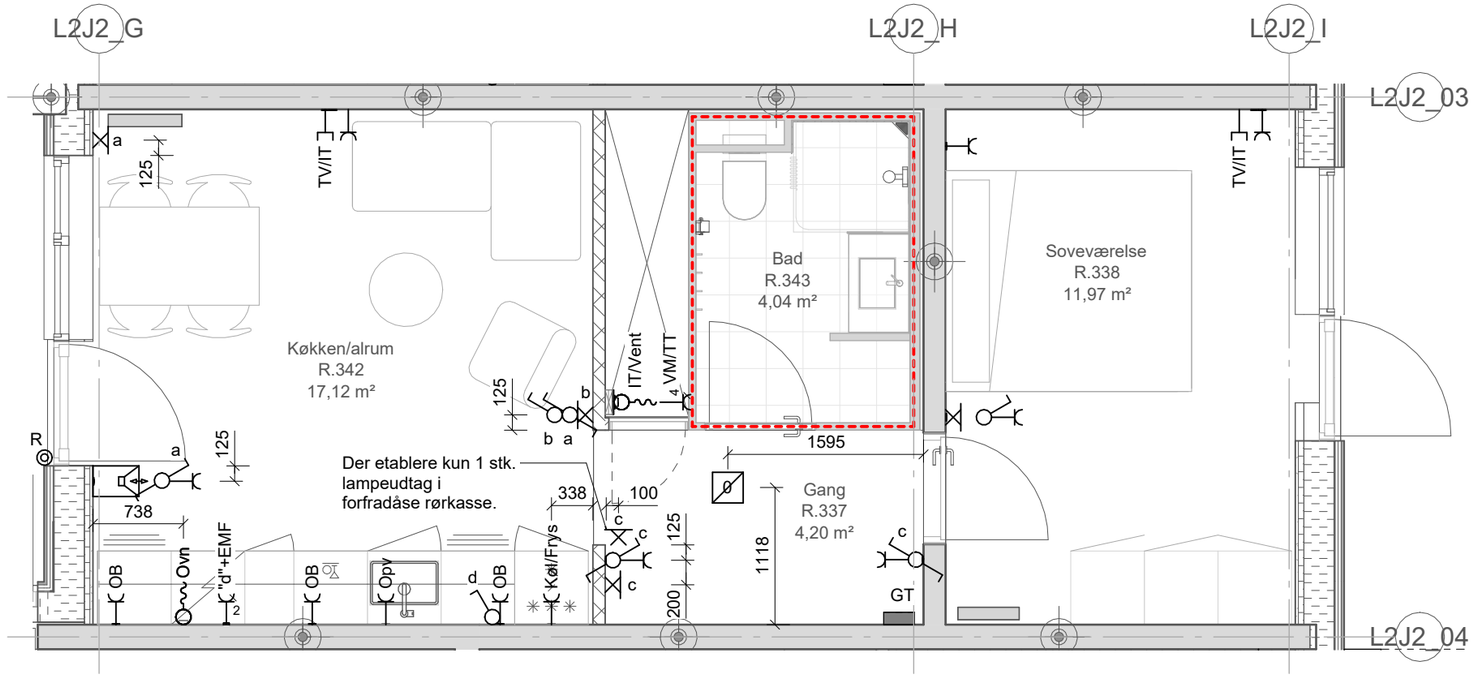

Projekt: Stejlepladsen


Tekst: Elinstallationer -
Byg J2 - Stueplan, Byg B
ALT_2V_T01_ST - Side J2-3

Tegningsnr.: ISP2_K07_L2XX_H04_EXX_N930


Rev.:

Projektnr.: 1019198 | Dato: 2026-02-27 | Rev. Dato: | Mål: 1 : 50 | Side: J2-3

www.arteliagroup.dk | Fil:

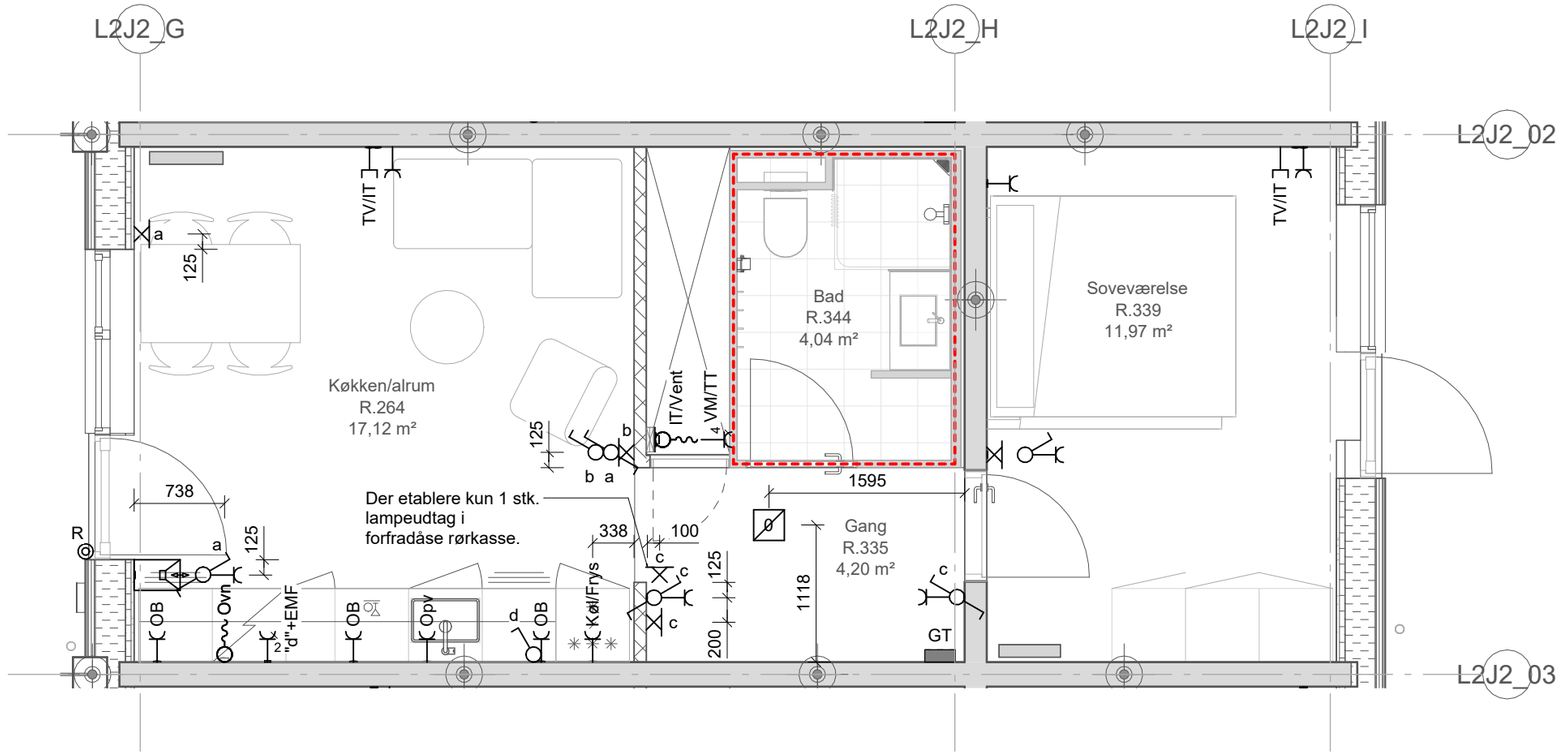

Projekt:	Stejlepladsen				
Tekst:	Elinstallationer - Byg J2 - Stueplan, Byg B ALT_2V_T01_ST - Side J2-4			Tegningsnr.:	Rev.:
				ISP2_K07_L2XX_H04_EXX_N930	
Projektnr.: 1019198	Dato: 2026-02-27	Rev. Dato:		Mål: 1 : 50	Side: J2-4
www.arteliagroup.dk	Fil:				

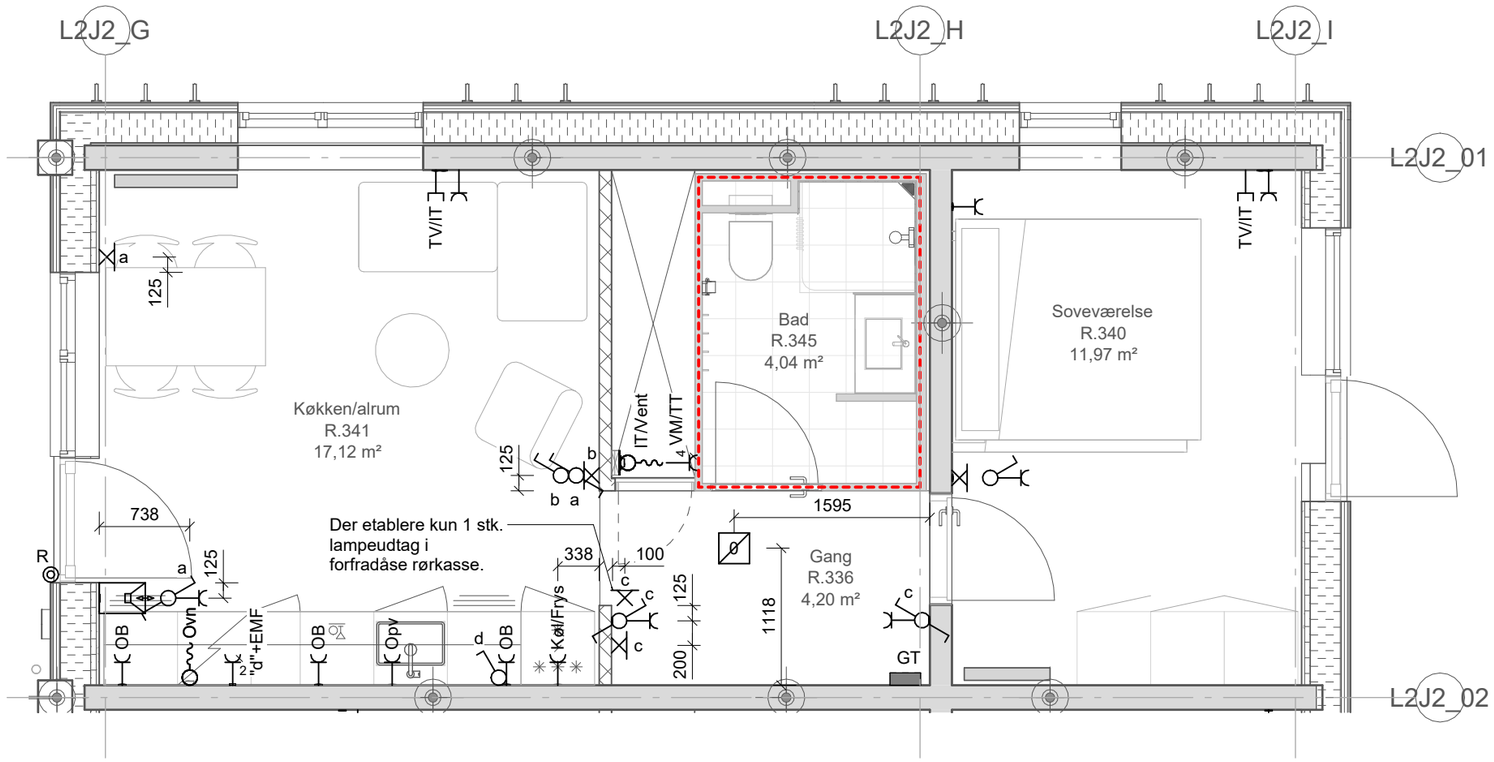

Projekt: Stejlepladsen


Tekst: Elinstallationer -
Byg J2 - Stueplan, Byg B
ALT_2V_T01_ST - Side J2-5

Tegningsnr.: ISP2_K07_L2XX_H04_EXX_N930

Rev.:

Projektnr.: 1019198 | Dato: 2026-02-27 | Rev. Dato: | Mål: 1 : 50 | Side: J2-5

www.arteliagroup.dk | Fil:

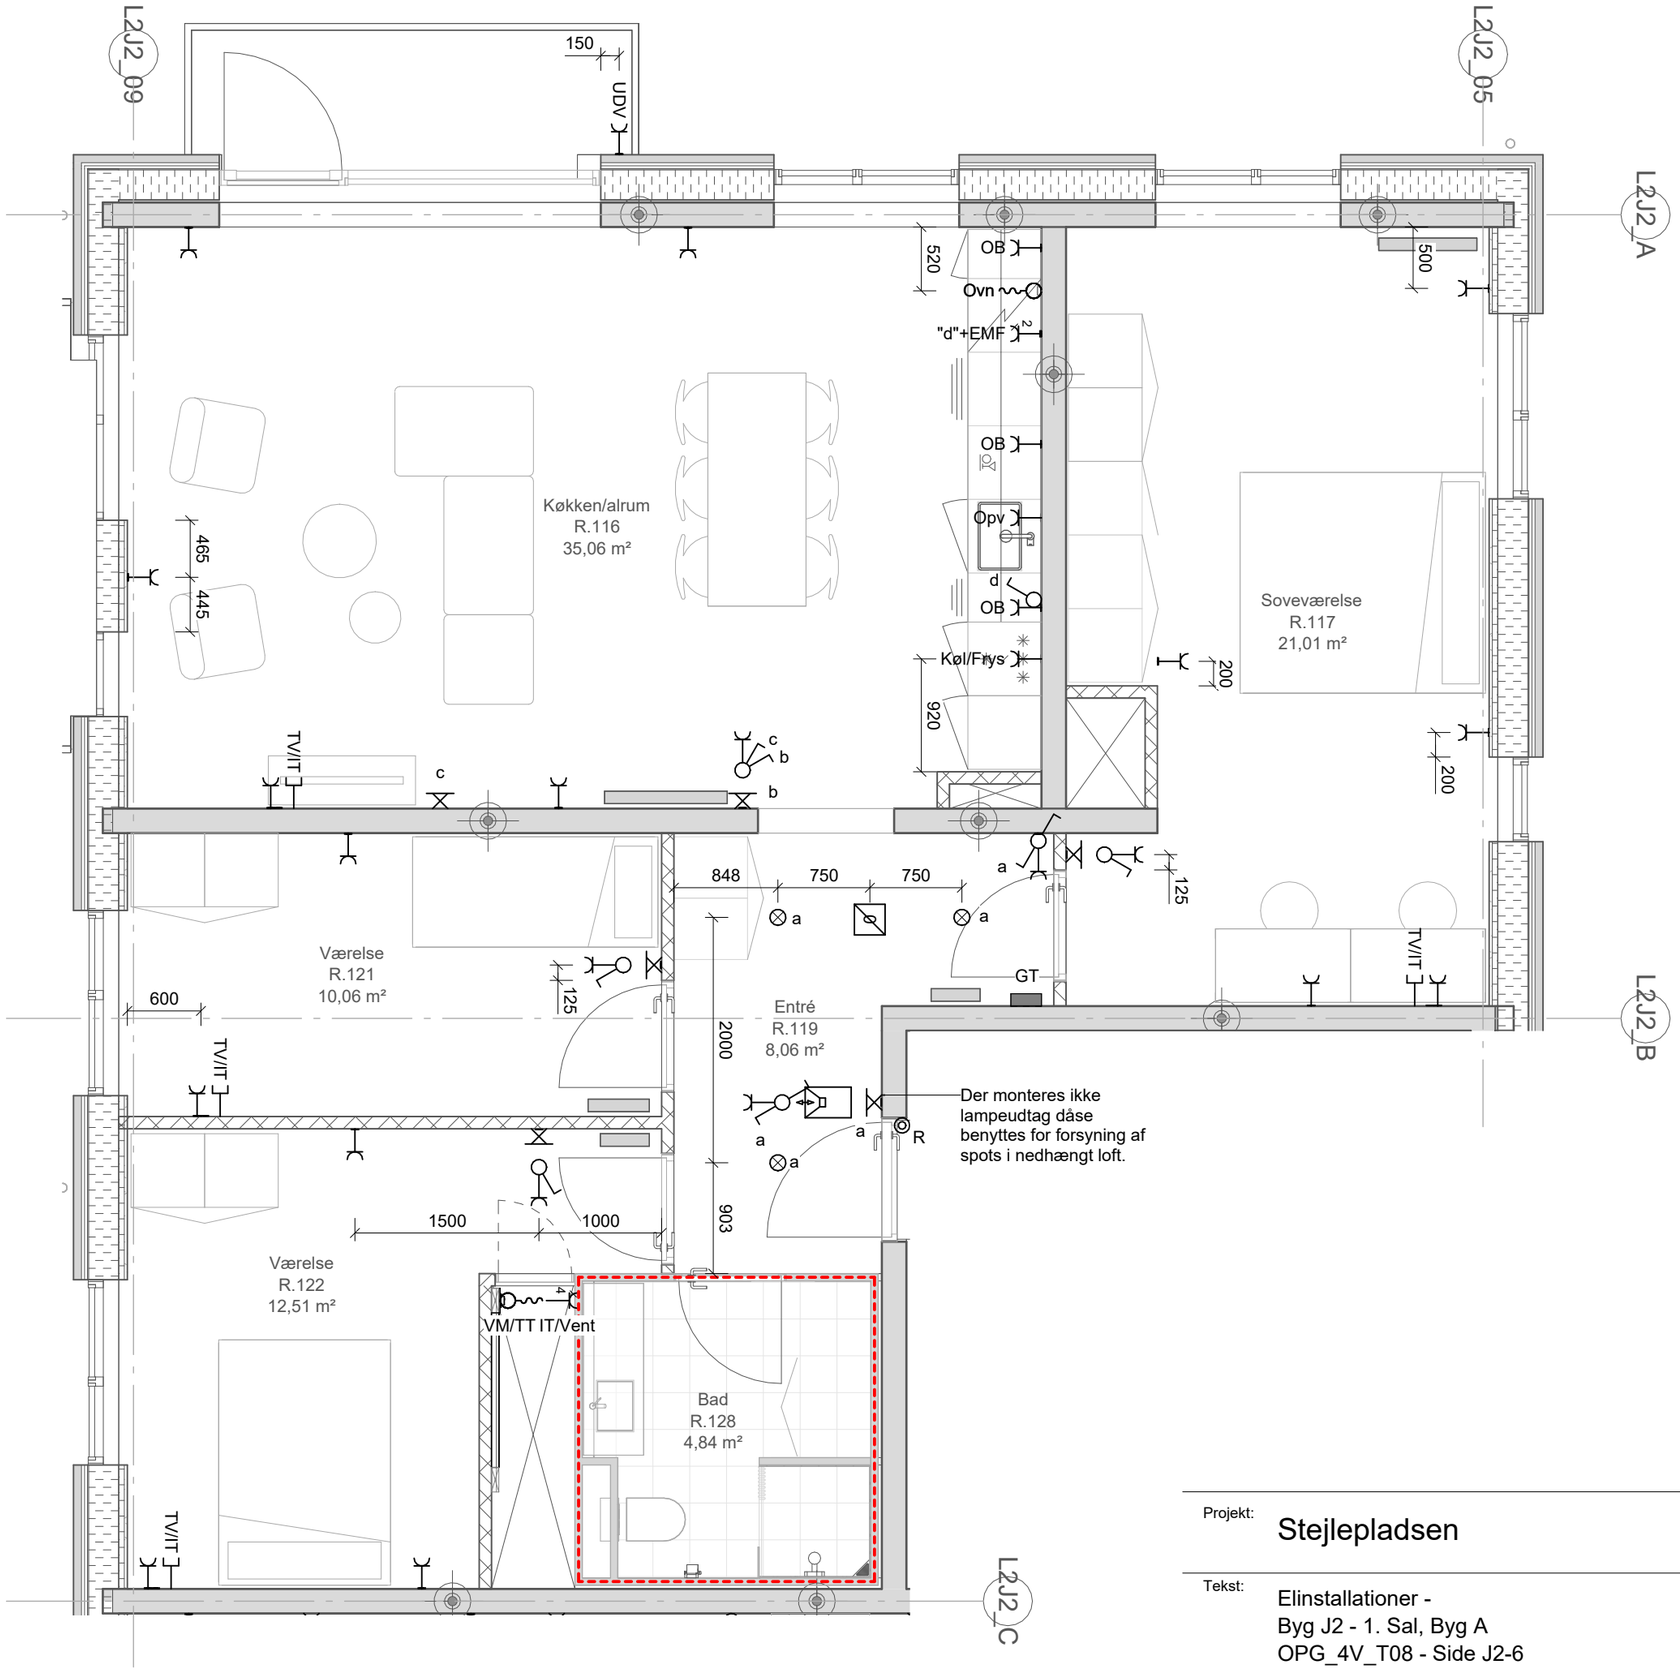

Projekt: Stejlepladsen


Tekst: Elinstallationer -
Byg J2 - 1. Sal, Byg A
OPG_4V_T08 - Side J2-6

Tegningsnr.: ISP2_K07_L2XX_H04_EXX_N930

Rev.:

Projektnr.: 1019198 | Dato: 2026-02-27 | Rev. Dato: | Mål: 1 : 50 | Side: J2-6

www.arteliagroup.dk | Fil:

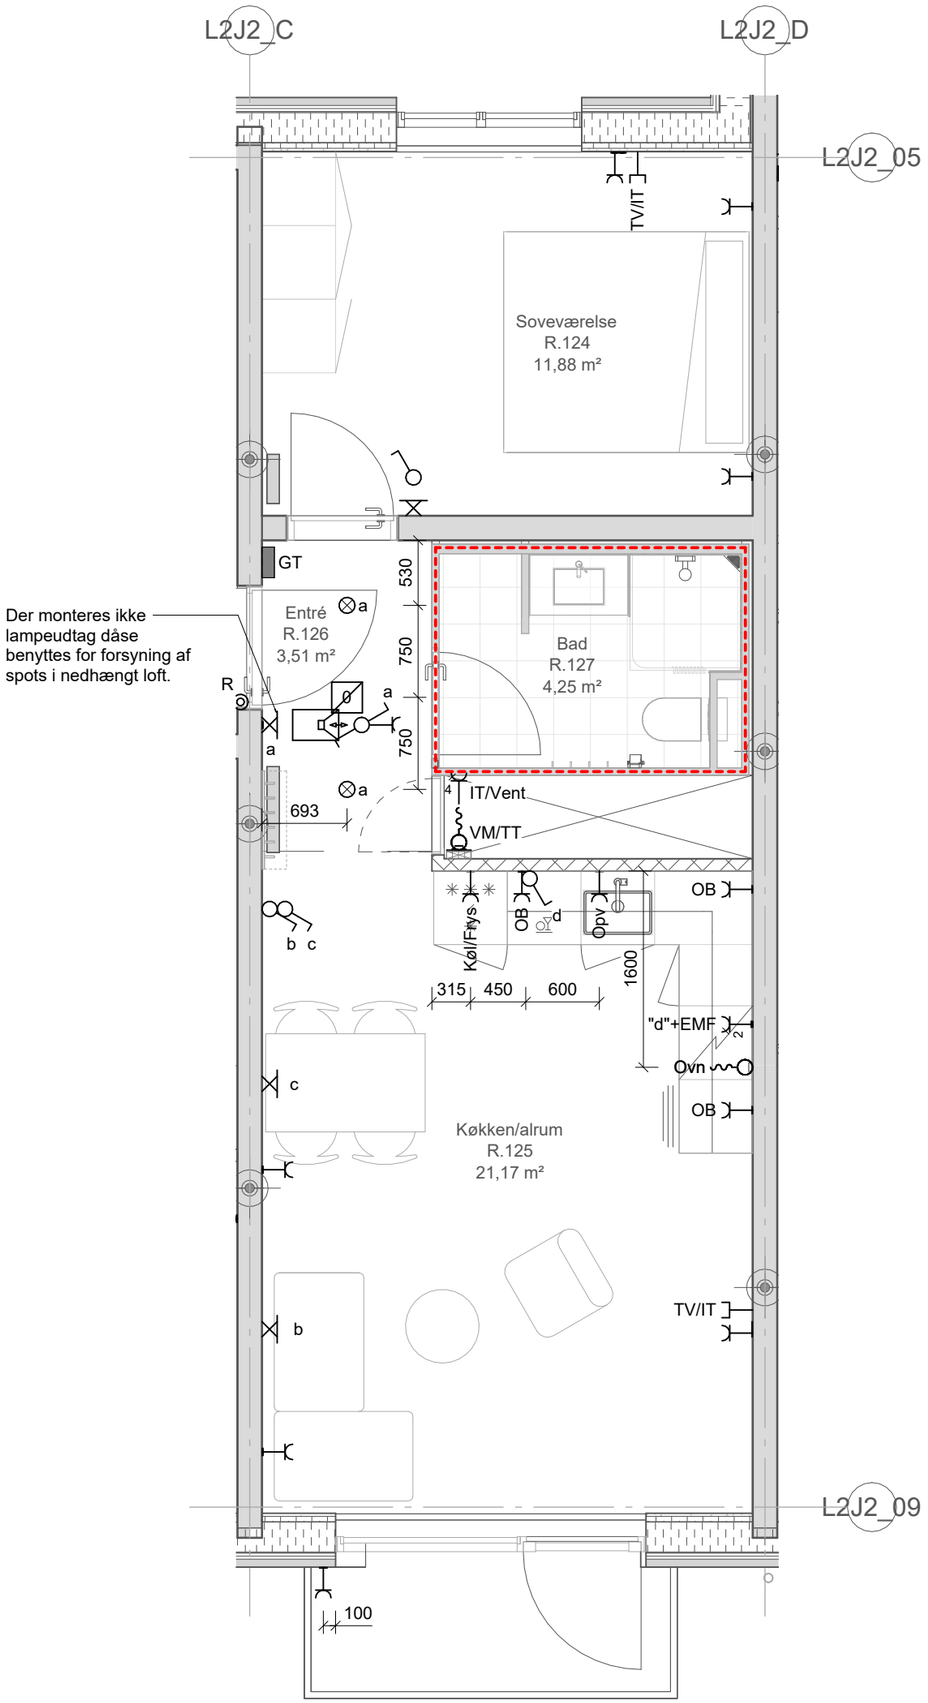

Projekt: Stejlepladsen


Tekst: Elinstallationer -
Byg J2 - 1. Sal, Byg A
OPG_2V_T31 - Side J2-7

Tegningsnr.: ISP2_K07_L2XX_H04_EXX_N930

Rev.:

Projektnr.: 1019198 | Dato: 2026-02-27 | Rev. Dato: | Mål: 1 : 50 | Side: J2-7

www.arteliagroup.dk | Fil:

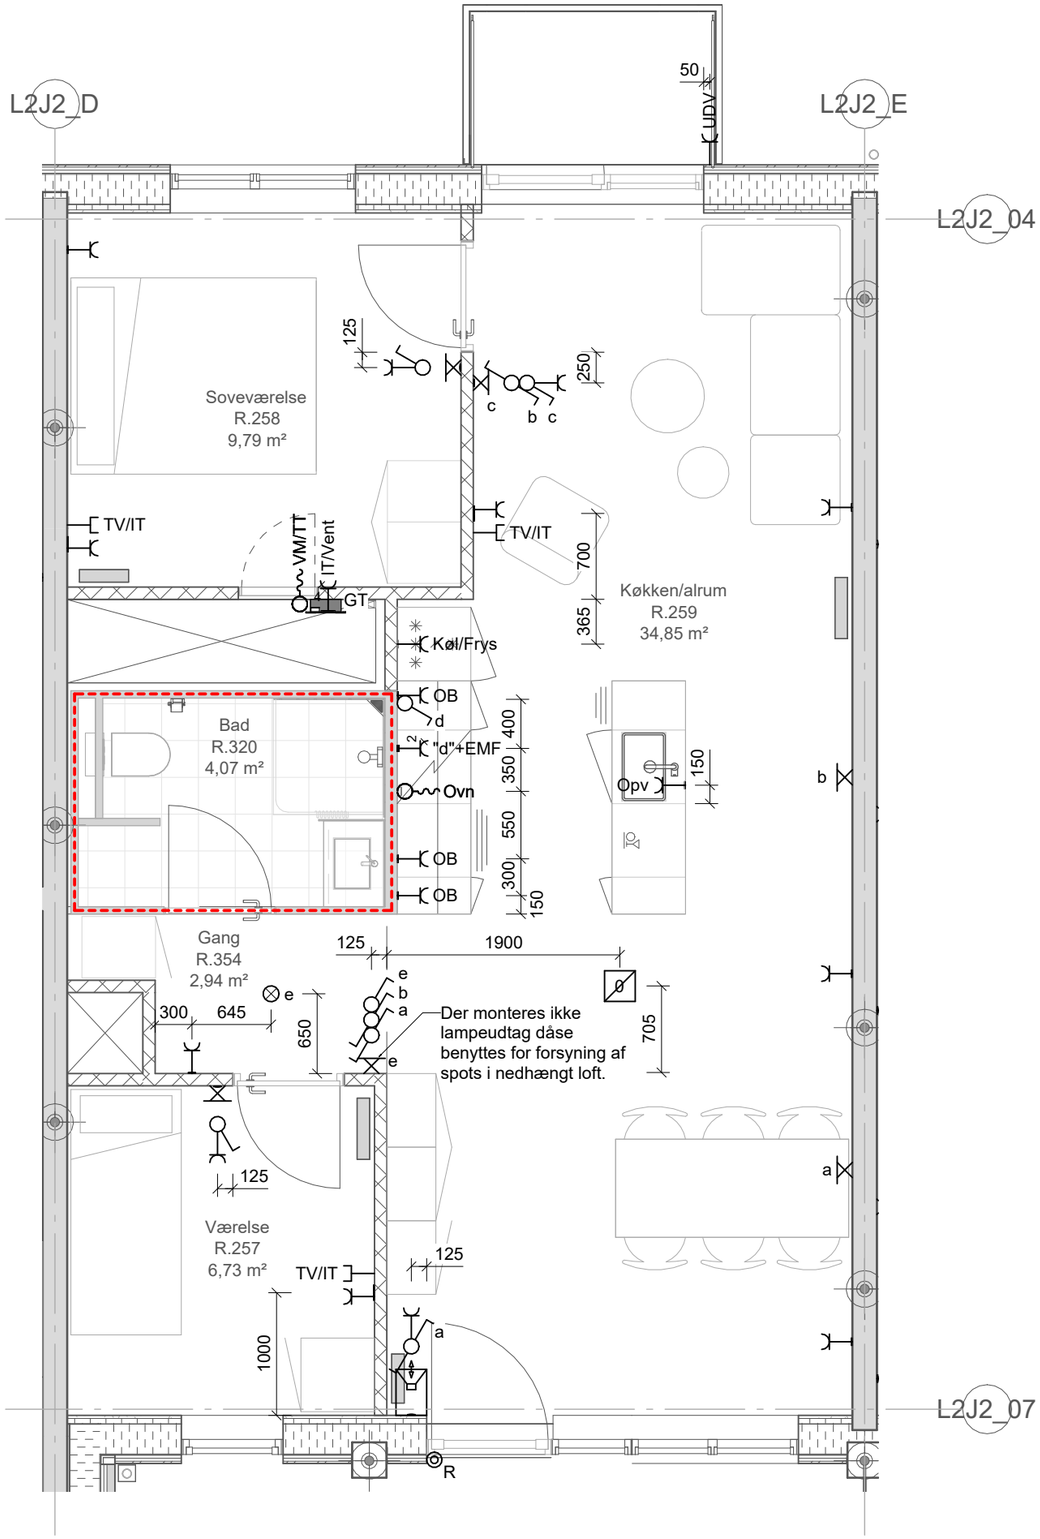

Projekt: Stejlepladsen


Tekst: Elinstallationer -
Byg J2 - 1. Sal, Byg B
ALT_3V_T30 - Side J2-8

Tegningsnr.: ISP2_K07_L2XX_H04_EXX_N930

Rev.:

Projektnr.: 1019198 | Dato: 2026-02-27 | Rev. Dato: | Mål: 1 : 50 | Side: J2-8

www.arteliagroup.dk | Fil:

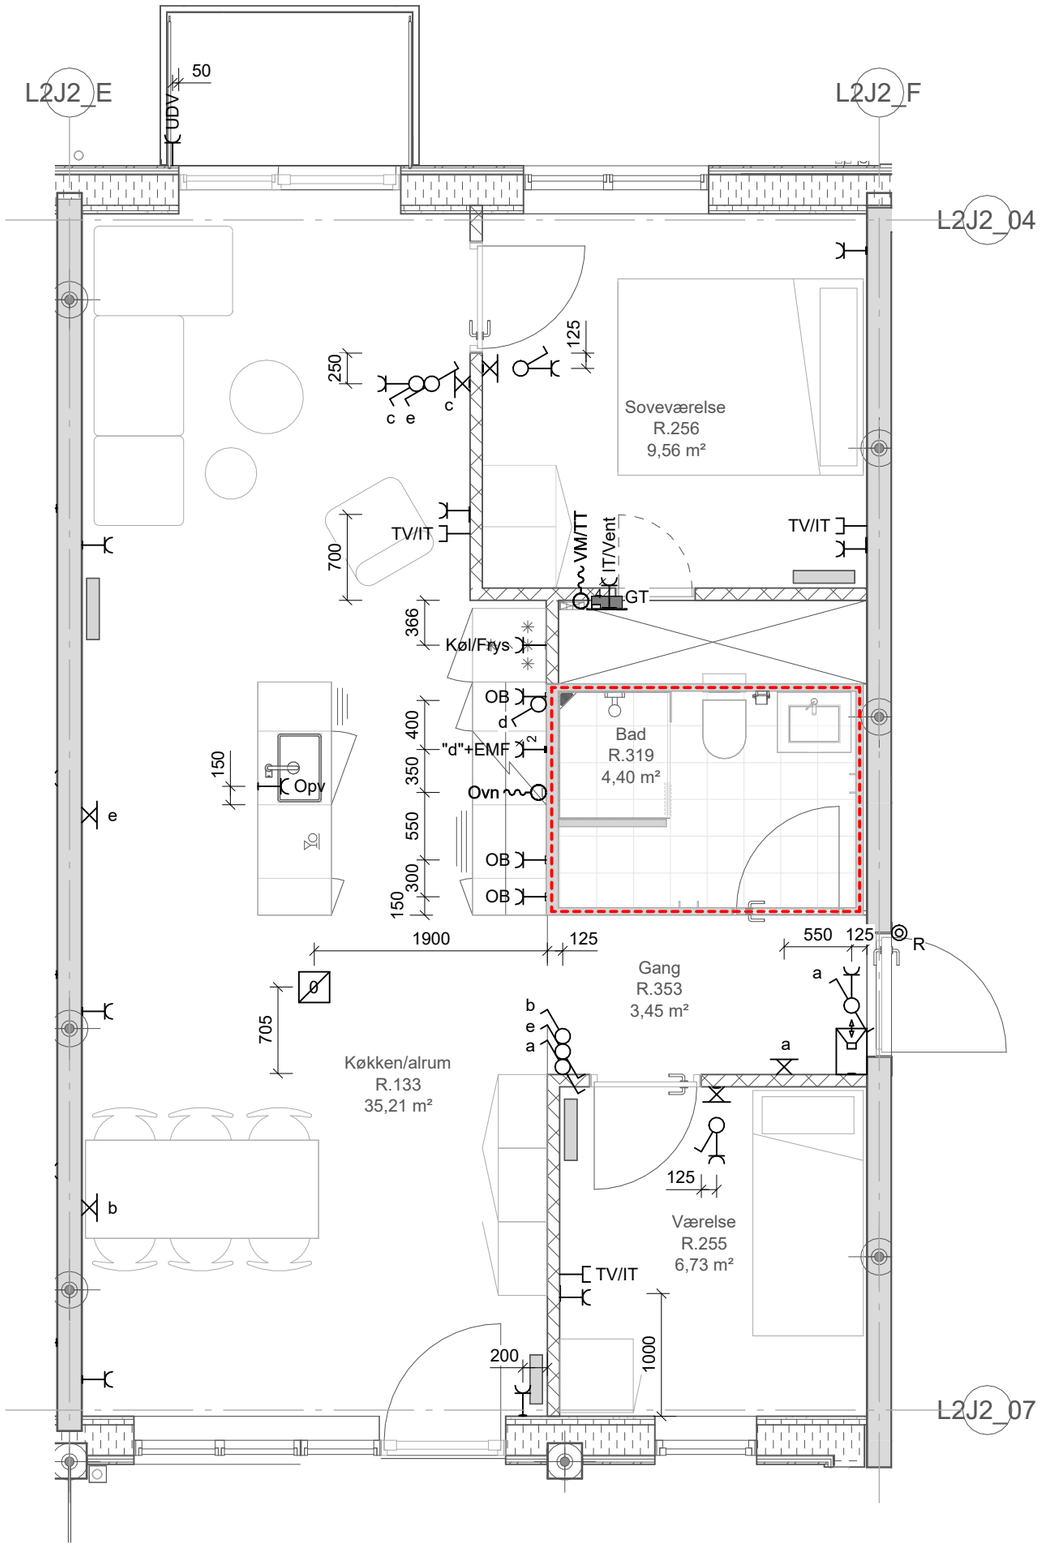

Projekt: Stejlepladsen


Tekst: Elinstallationer -
Byg J2 - 1. Sal, Byg B
ALT_3V_T30_S - Side J2-9

Tegningsnr.: ISP2_K07_L2XX_H04_EXX_N930


Rev.:

Projektnr.: 1019198 | Dato: 2026-02-27 | Rev. Dato: | Mål: 1 : 50 | Side: J2-9

www.arteliagroup.dk | Fil:

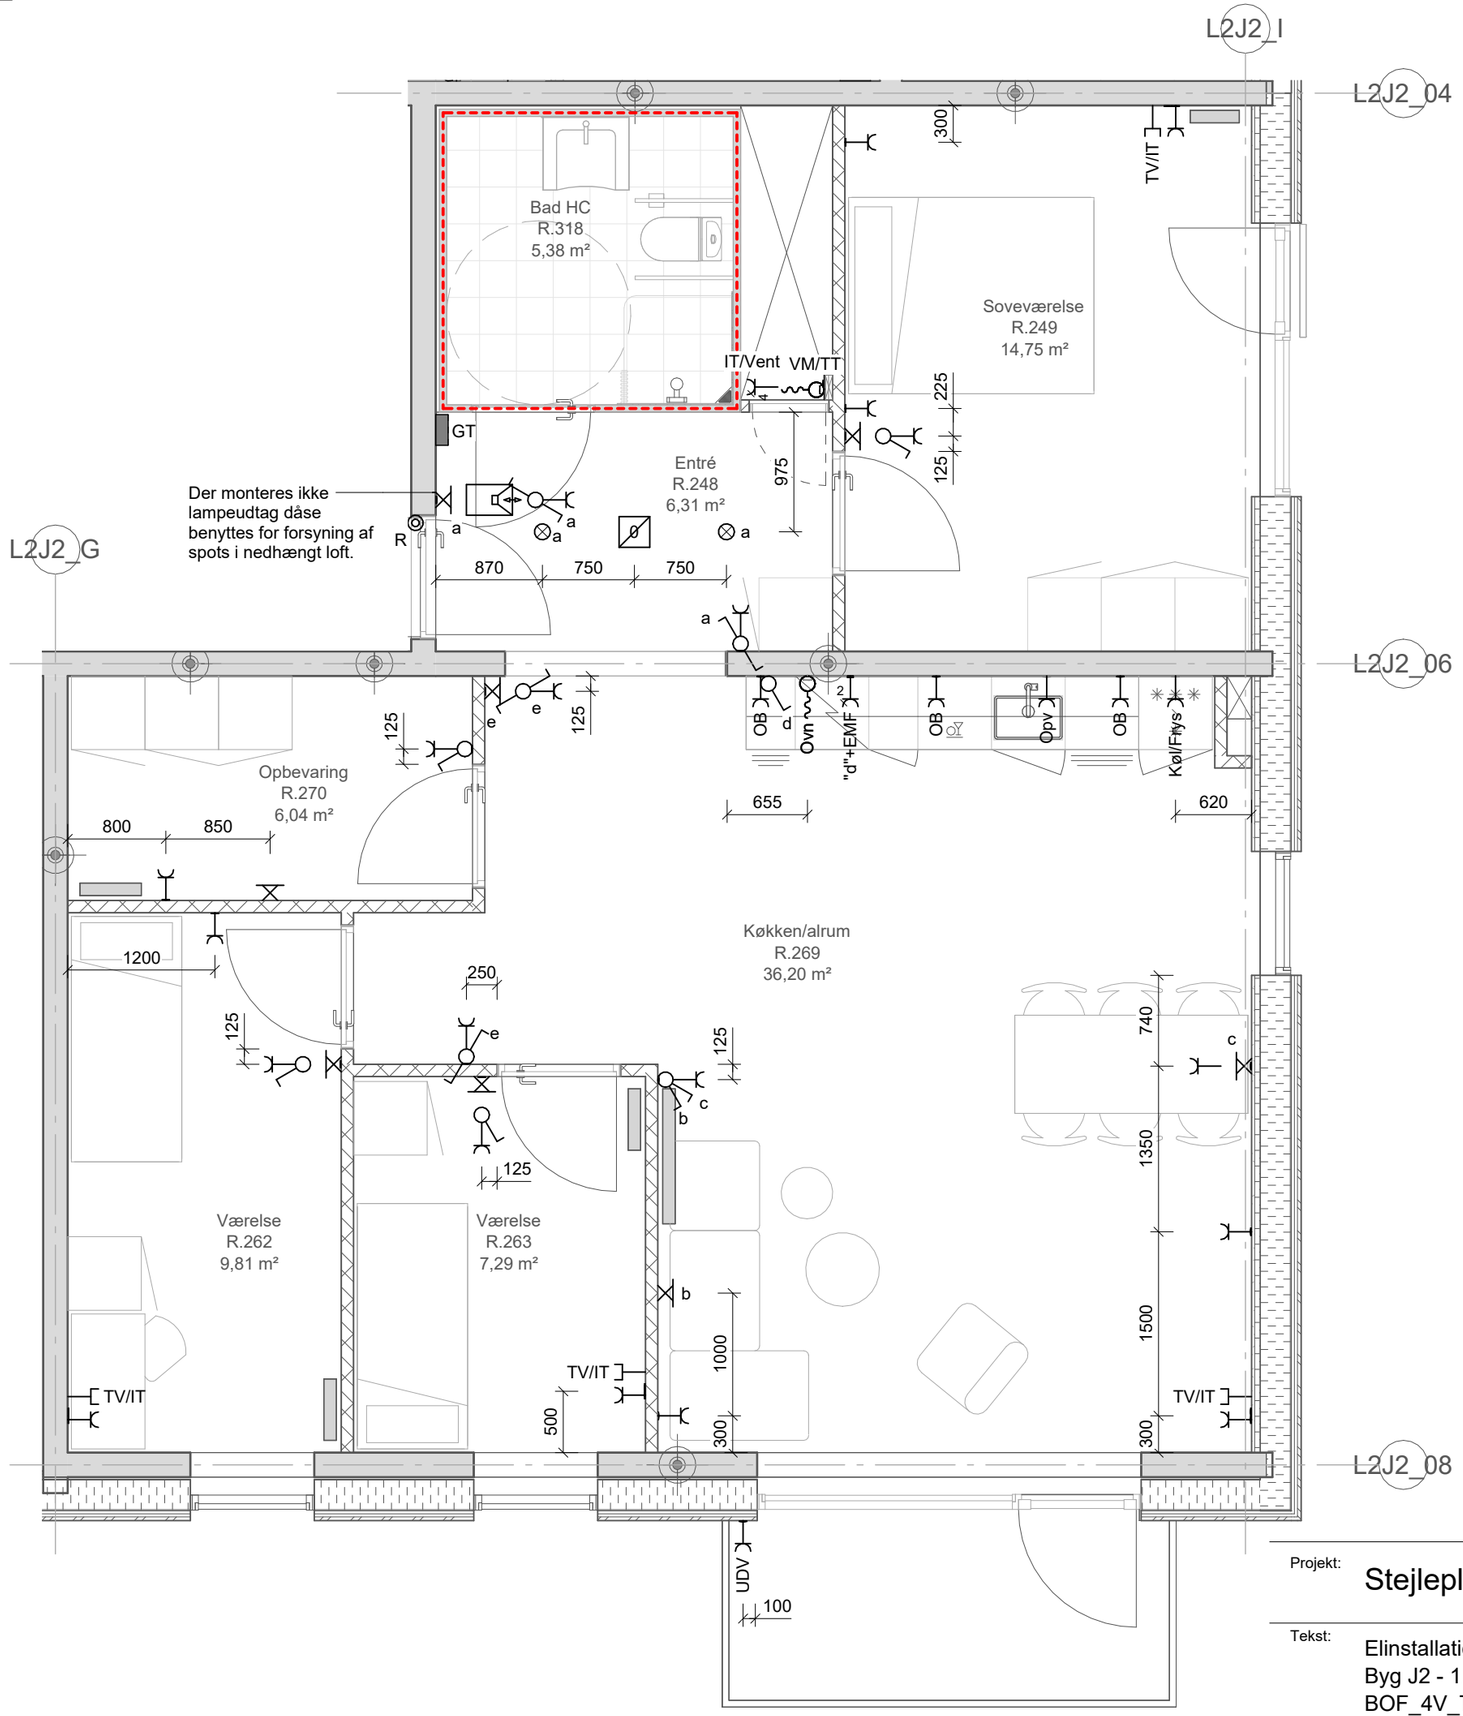

Projekt:	Stejlepladsen			
Tekst:	Elinstallationer - Byg J2 - 1. Sal, Byg B BOF_4V_T31 - Side J2-10	Tegningsnr.:	ISP2_K07_L2XX_H04_EXX_N930	Rev.:
Projektnr.: 1019198	Dato: 2026-02-27	Rev. Dato:	Mål: 1 : 50	Side: J2-10
www.arteliagroup.dk	Fil:			

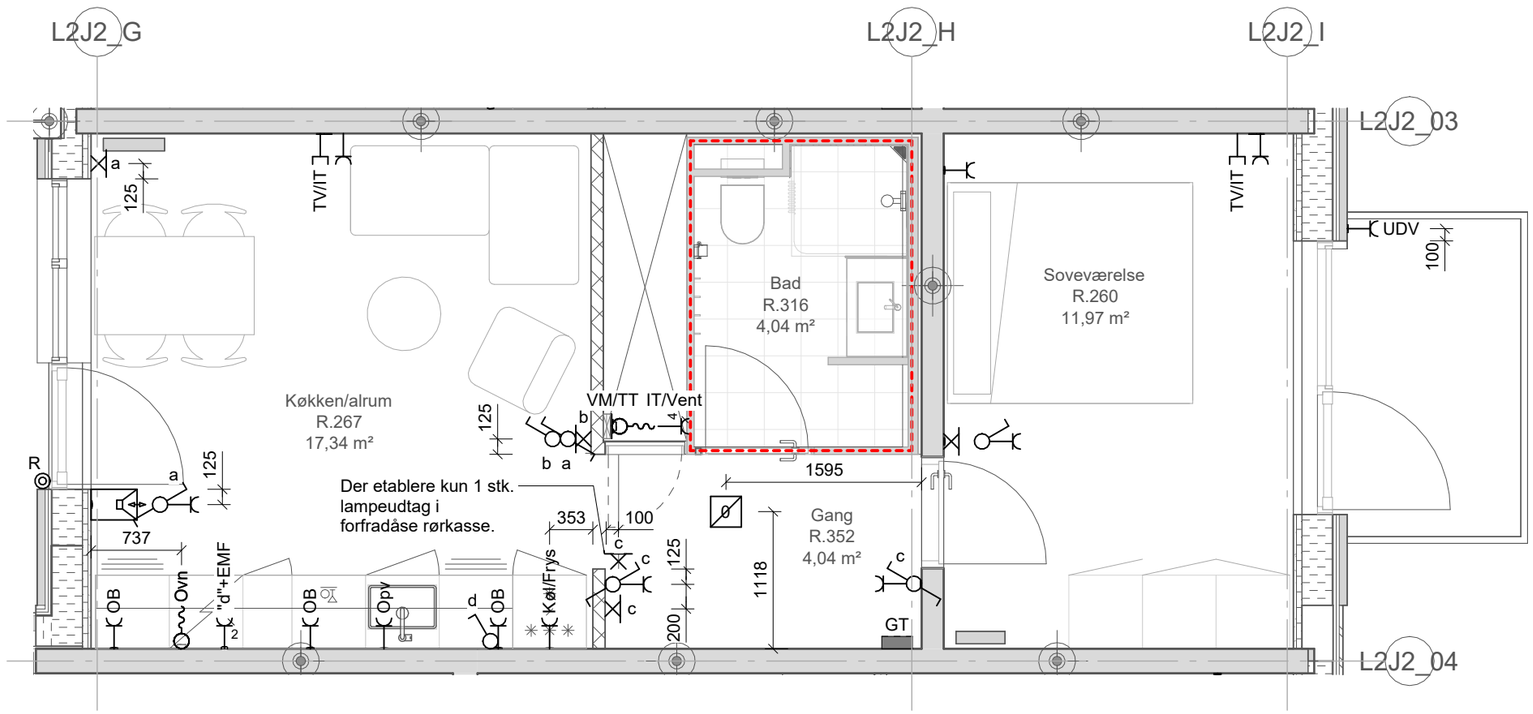

Projekt: Stejlepladsen


Tekst: Elinstallationer -
Byg J2 - 1. Sal, Byg B
ALT_2V_T01 - Side J2-11

Tegningsnr.: ISP2_K07_L2XX_H04_EXX_N930


Rev.:

Projektnr.: 1019198 | Dato: 2026-02-27 | Rev. Dato: | Mål: 1 : 50 | Side: J2-11

www.arteliagroup.dk | Fil:

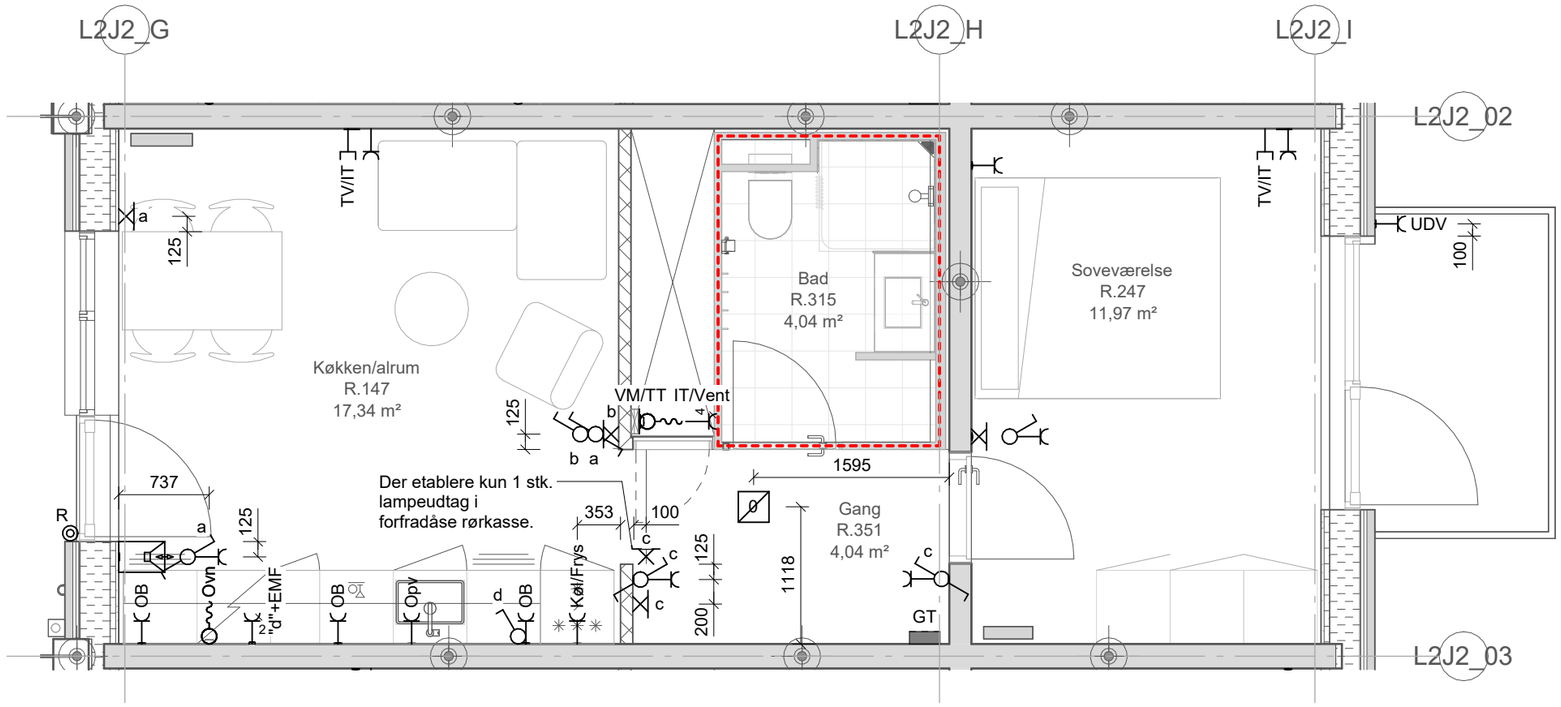

Projekt:	Stejlepladsen				
Tekst:	Elinstallationer - Byg J2 - 1. Sal, Byg B ALT_2V_T01 - Side J2-12			Tegningsnr.:	Rev.:
			ISP2_K07_L2XX_H04_EXX_N930		
Projektnr.: 1019198	Dato: 2026-02-27	Rev. Dato:		Mål: 1 : 50	Side: J2-12
www.arteliagroup.dk	Fil:				

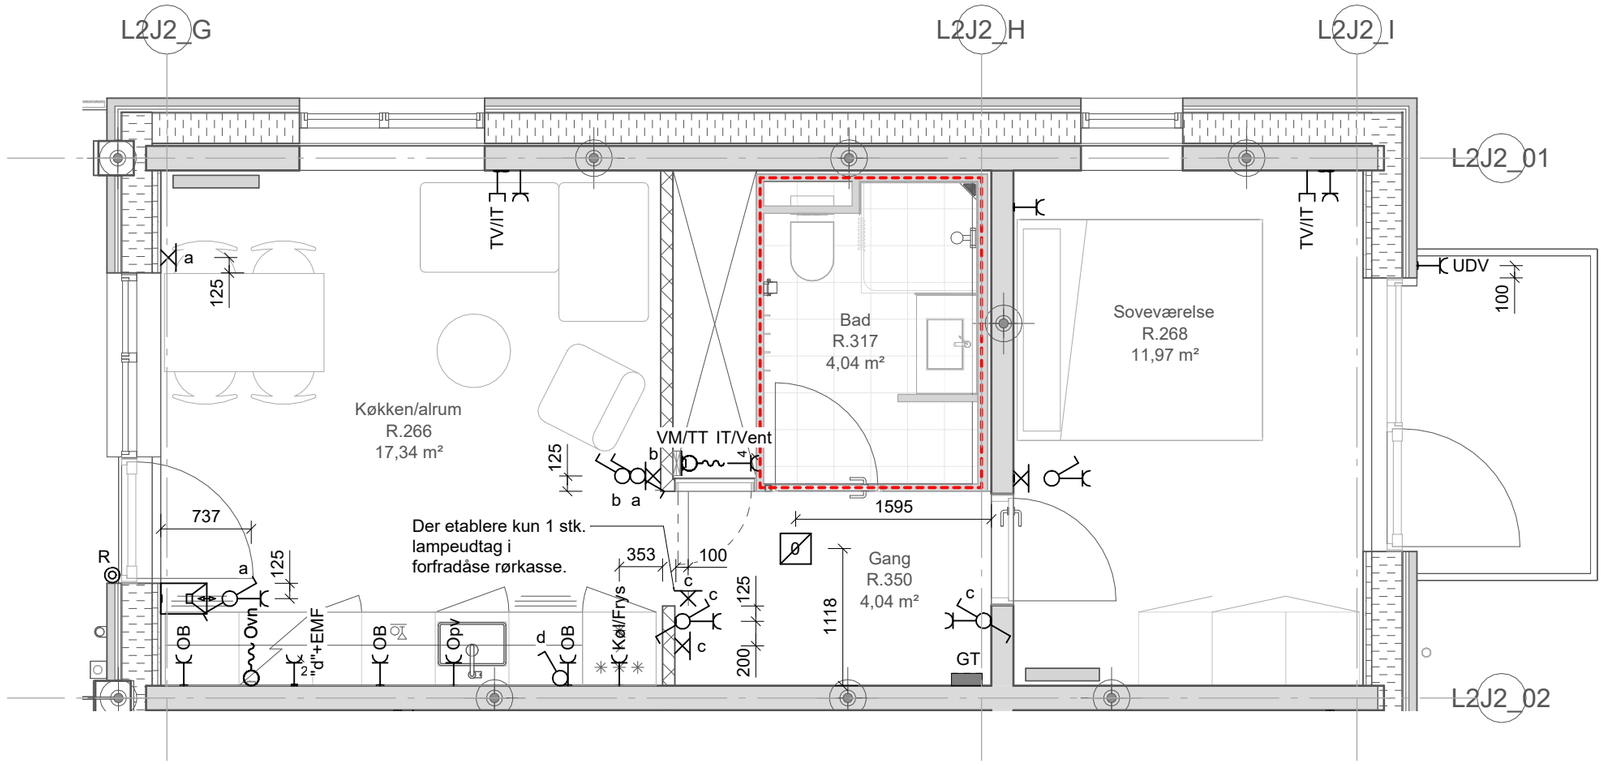

Projekt: Stejlepladsen

Tekst: Elinstallationer -
Byg J2 - 1. Sal, Byg B
ALT_2V_T01 - Side J2-13

Tegningsnr.: ISP2_K07_L2XX_H04_EXX_N930


Rev.:

Projektnr.: 1019198 | Dato: 2026-02-27 | Rev. Dato: | Mål: 1 : 50 | Side: J2-13

www.arteliagroup.dk | Fil:

L2J2_09
L2J2_05
L2J2_A
L2J2_B
L2J2_C
OB
Ovn
"d"+EMF
OB
Opv
d
OB
Køl/Frys
520
500
200
920
200
200
Køkken/alrum
R.73
35,06 m²
Soveværelse
R.74
21,01 m²
TV/IT
c
b
c
b
a
848
750
750
a
a
125
Værelse
R.77
10,06 m²
600
125
Entré
R.76
8,06 m²
GT
2000
TV/IT
TV/IT
a
a
a
R
Der monteres ikke lampeudtag dåse benyttes for forsyning af spots i nedhængt loft.
1500
1000
903
Værelse
R.78
12,51 m²
VM/TT IT/Vent
Bad
R.83
4,66 m²
TV/IT

Projekt:	Stejlepladsen				
Tekst:	Elinstallationer - Byg J2 - 2. Sal, Byg A OPG_4V_T08 - Side J2-14			Tegningsnr.:	Rev.:
				ISP2_K07_L2XX_H04_EXX_N930	
Projektnr.: 1019198	Dato: 2026-02-27	Rev. Dato:		Mål: 1 : 50	Side: J2-14
www.arteliagroup.dk	Fil:				

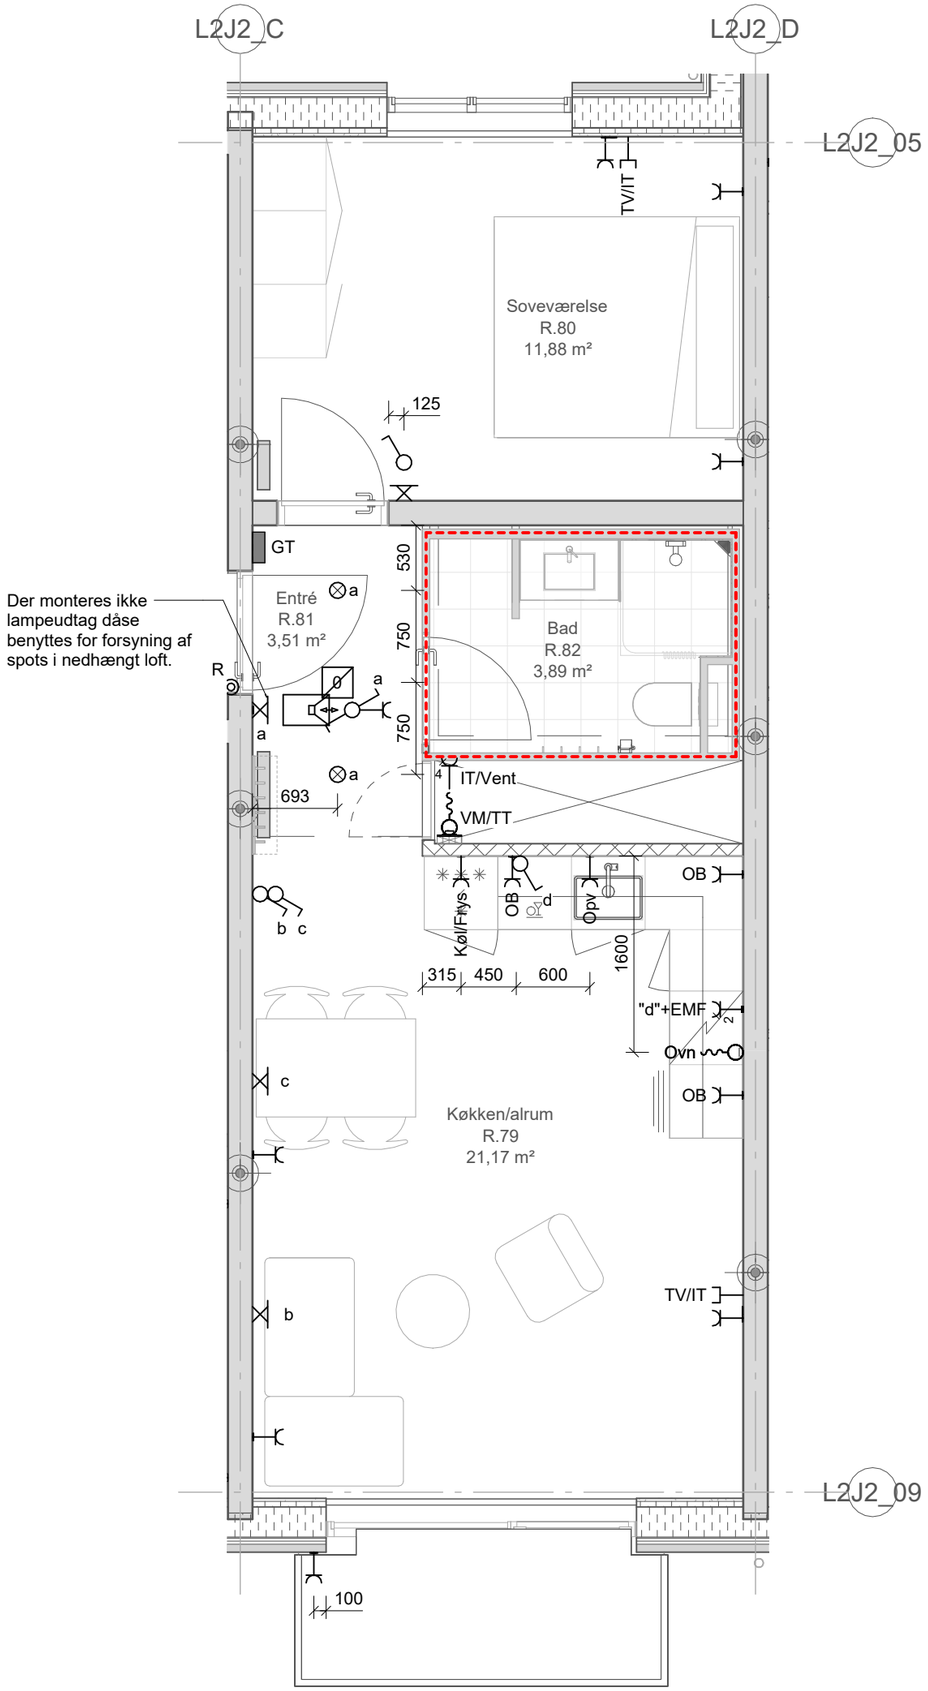

Projekt: Stejlepladsen


Tekst: Elinstallationer -
Byg J2 - 2. Sal, Byg A
OPG_2V_T31 - Side J2-15

Tegningsnr.: ISP2_K07_L2XX_H04_EXX_N930


Rev.:

Projektnr.: 1019198 | Dato: 2026-02-27 | Rev. Dato: | Mål: 1 : 50 | Side: J2-15

www.arteliagroup.dk | Fil:

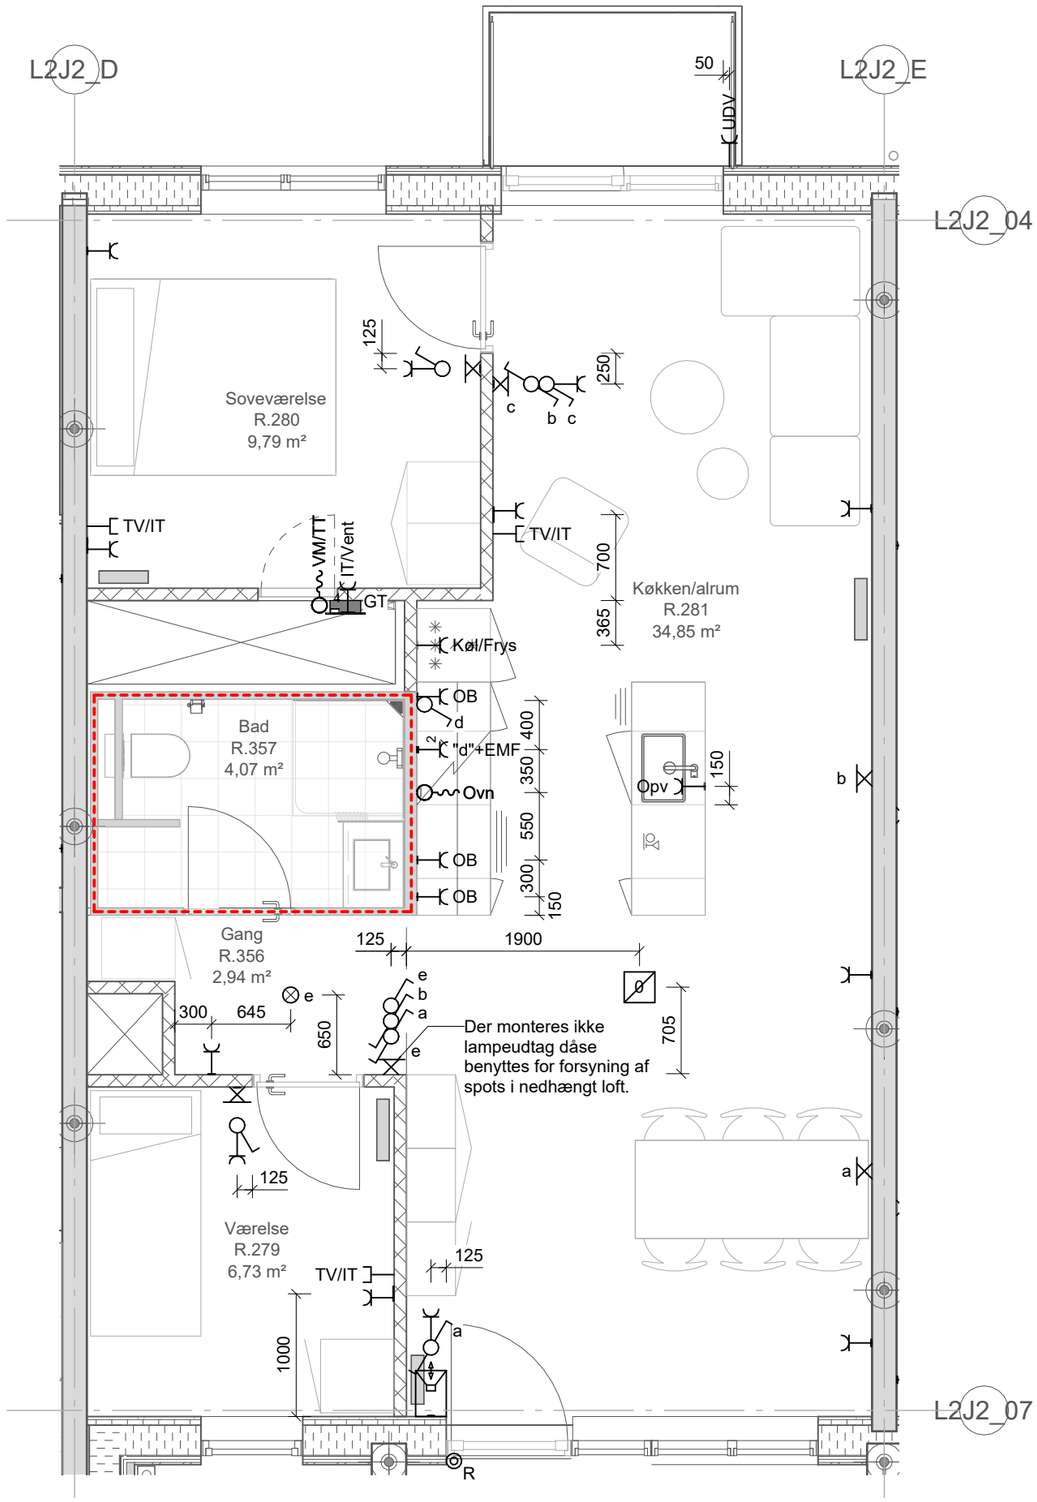

Projekt:	Stejlepladsen				
Tekst:	Elinstallationer - Byg J2 - 2. Sal, Byg B ALT_3V_T30 - Side J2-16			Tegningsnr.:	Rev.:
			ISP2_K07_L2XX_H04_EXX_N930		
Projektnr.: 1019198	Dato: 2026-02-27	Rev. Dato:		Mål: 1 : 50	Side: J2-16
www.arteliagroup.dk	Fil:				

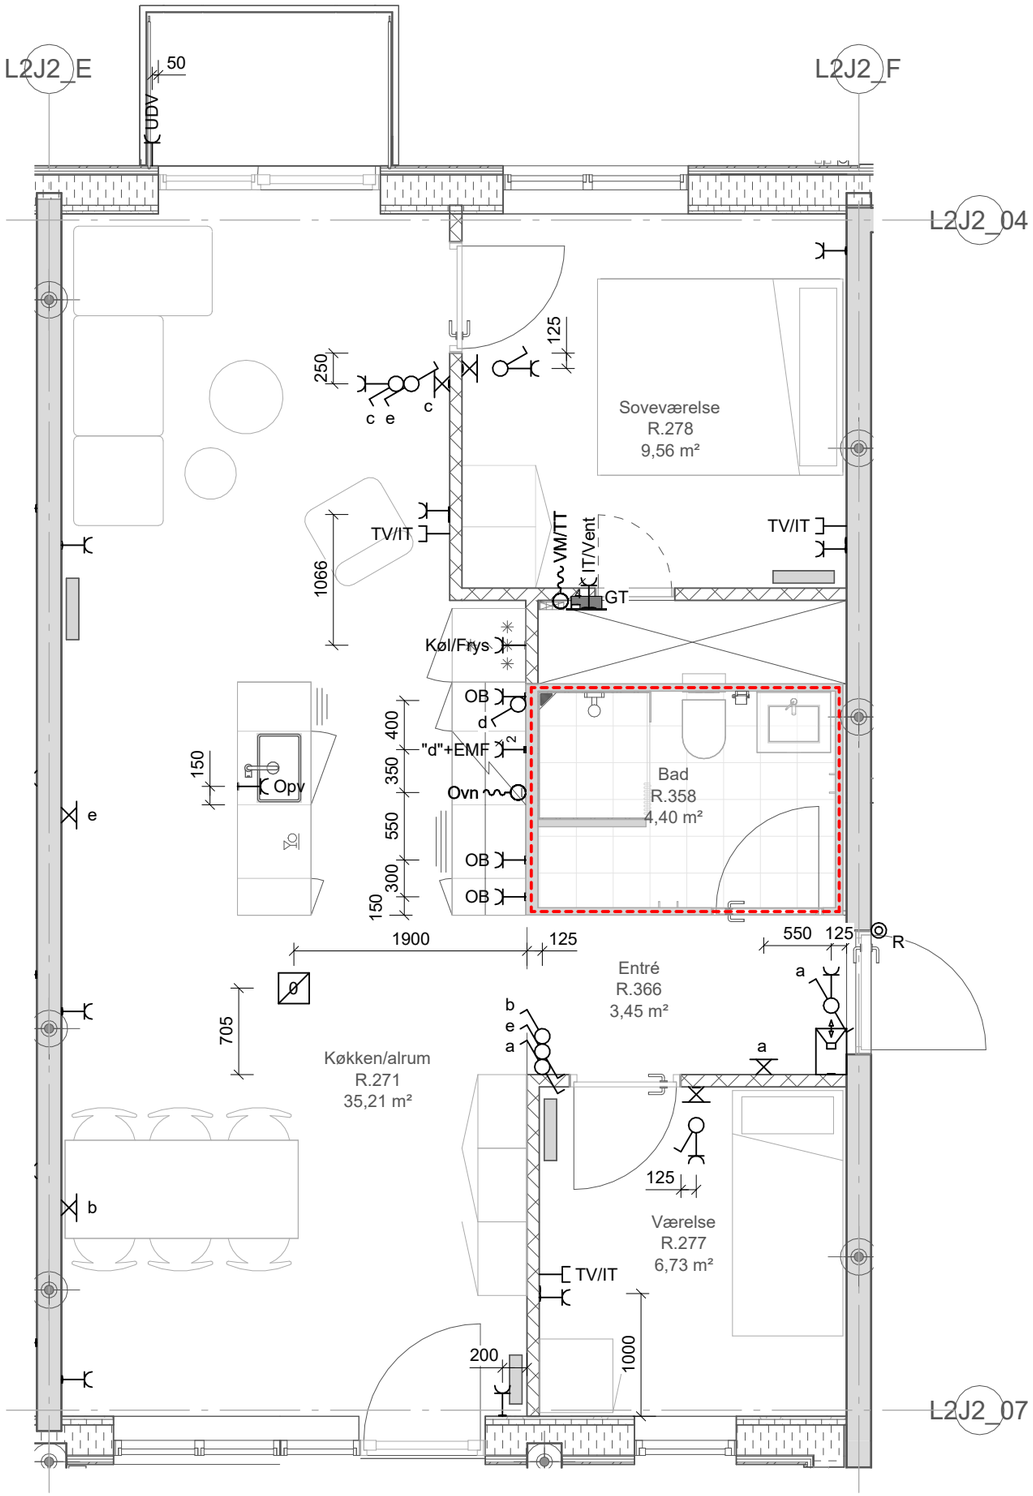

Projekt: Stejlepladsen

ARTELIA

Tekst: Elinstallationer -
Byg J2 - 2. Sal, Byg B
ALT_3V_T30_S - Side J2-17

Tegningsnr.: ISP2_K07_L2XX_H04_EXX_N930

Rev.:

Projektnr.: 1019198 | Dato: 2026-02-27 | Rev. Dato: | Mål: 1 : 50 | Side: J2-17

www.arteliagroup.dk | Fil:

L2J2_I

L2J2_04

L2J2_G

L2J2_06

L2J2_08

Bad HC
R.359
5,38 m²

Soveværelse
R.276
14,75 m²

Entré
R.275
6,31 m²

Opbevaring
R.289
6,04 m²

Køkken/alrum
R.288
36,20 m²

Værelse
R.283
9,81 m²

Værelse
R.284
7,29 m²

Der monteres ikke lampeudtag dåse benyttes for forsyning af spots i nedhængt loft.

GT

IT/Vent

VM/TT

TV/IT

OB

Ovn

"d"+EMF

Opv

Køl/Frys

UDV

300
225
125
975
870
750
750
655
620
800
850
1200
250
740
1350
1500
1000
500
100

Projekt: Stejlepladsen

ARTELIA

Tekst: Elinstallationer -
Byg J2 - 2. Sal, Byg B
BOF_4V_T31 - Side J2-18

Tegningsnr.: ISP2_K07_L2XX_H04_EXX_N930

Rev.:

Projektnr.: 1019198

Dato: 2026-02-27


Rev. Dato:

Mål: 1 : 50


Side: J2-18

www.arteliagroup.dk


Fil:

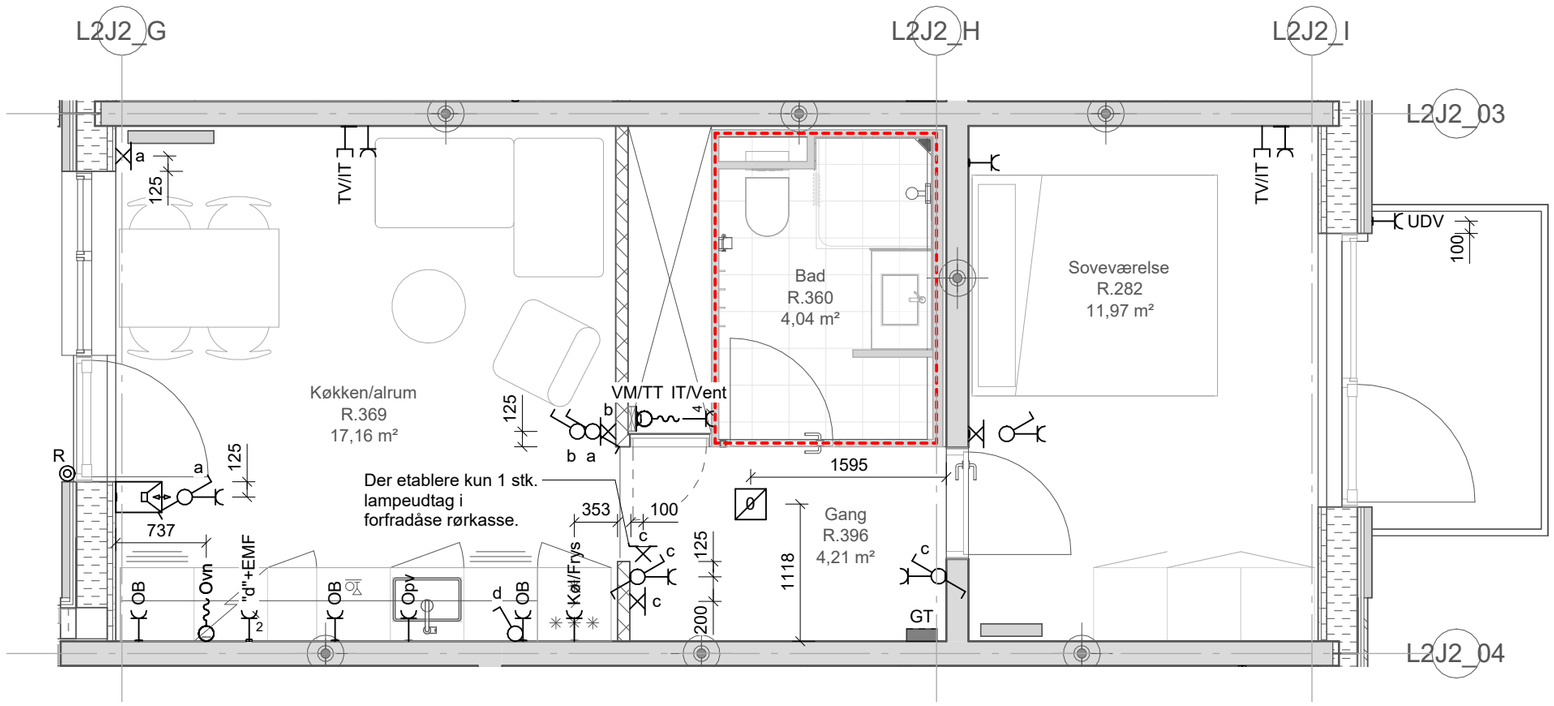

Projekt:	Stejlepladsen				
Tekst:	Elinstallationer - Byg J2 - 2. Sal, Byg B ALT_2V_T01 - Side J2-19			Tegningsnr.:	Rev.:
			ISP2_K07_L2XX_H04_EXX_N930		
Projektnr.: 1019198	Dato: 2026-02-27	Rev. Dato:		Mål: 1 : 50	Side: J2-19
www.arteliagroup.dk	Fil:				

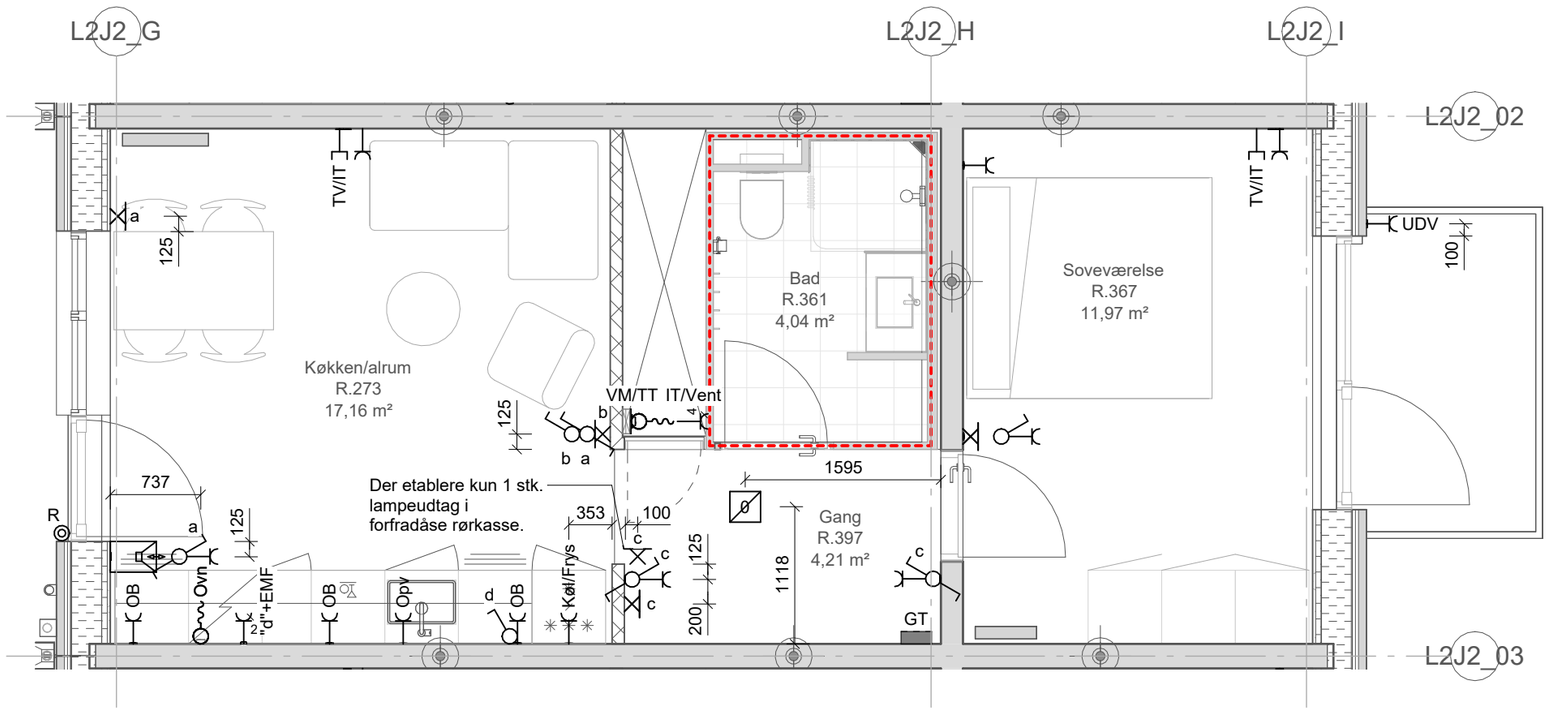

Projekt:	Stejlepladsen				
Tekst:	Elinstallationer - Byg J2 - 2. Sal, Byg B ALT_2V_T01 - Side J2-20			Tegningsnr.:	Rev.:
				ISP2_K07_L2XX_H04_EXX_N930	
Projektnr.: 1019198	Dato: 2026-02-27	Rev. Dato:		Mål: 1 : 50	Side: J2-20
www.arteliagroup.dk	Fil:				

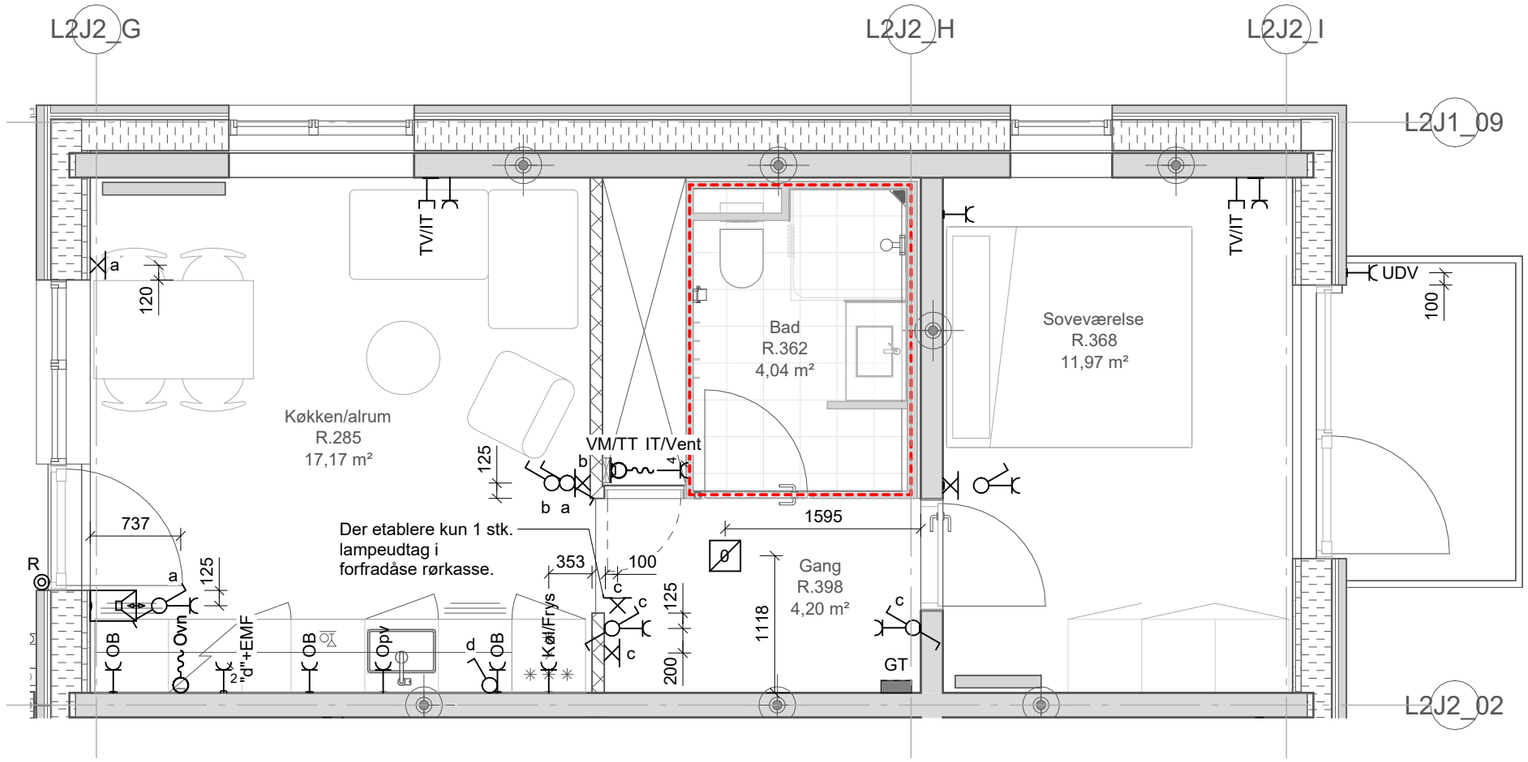

Projekt: Stejlepladsen


Tekst: Elinstallationer -
Byg J2 - 2. Sal, Byg B
ALT_2V_T01 - Side J2-21

Tegningsnr.: ISP2_K07_L2XX_H04_EXX_N930

Rev.:

Projektnr.: 1019198 | Dato: 2026-02-27 | Rev. Dato: | Mål: 1 : 50 | Side: J2-21

www.arteliagroup.dk | Fil:

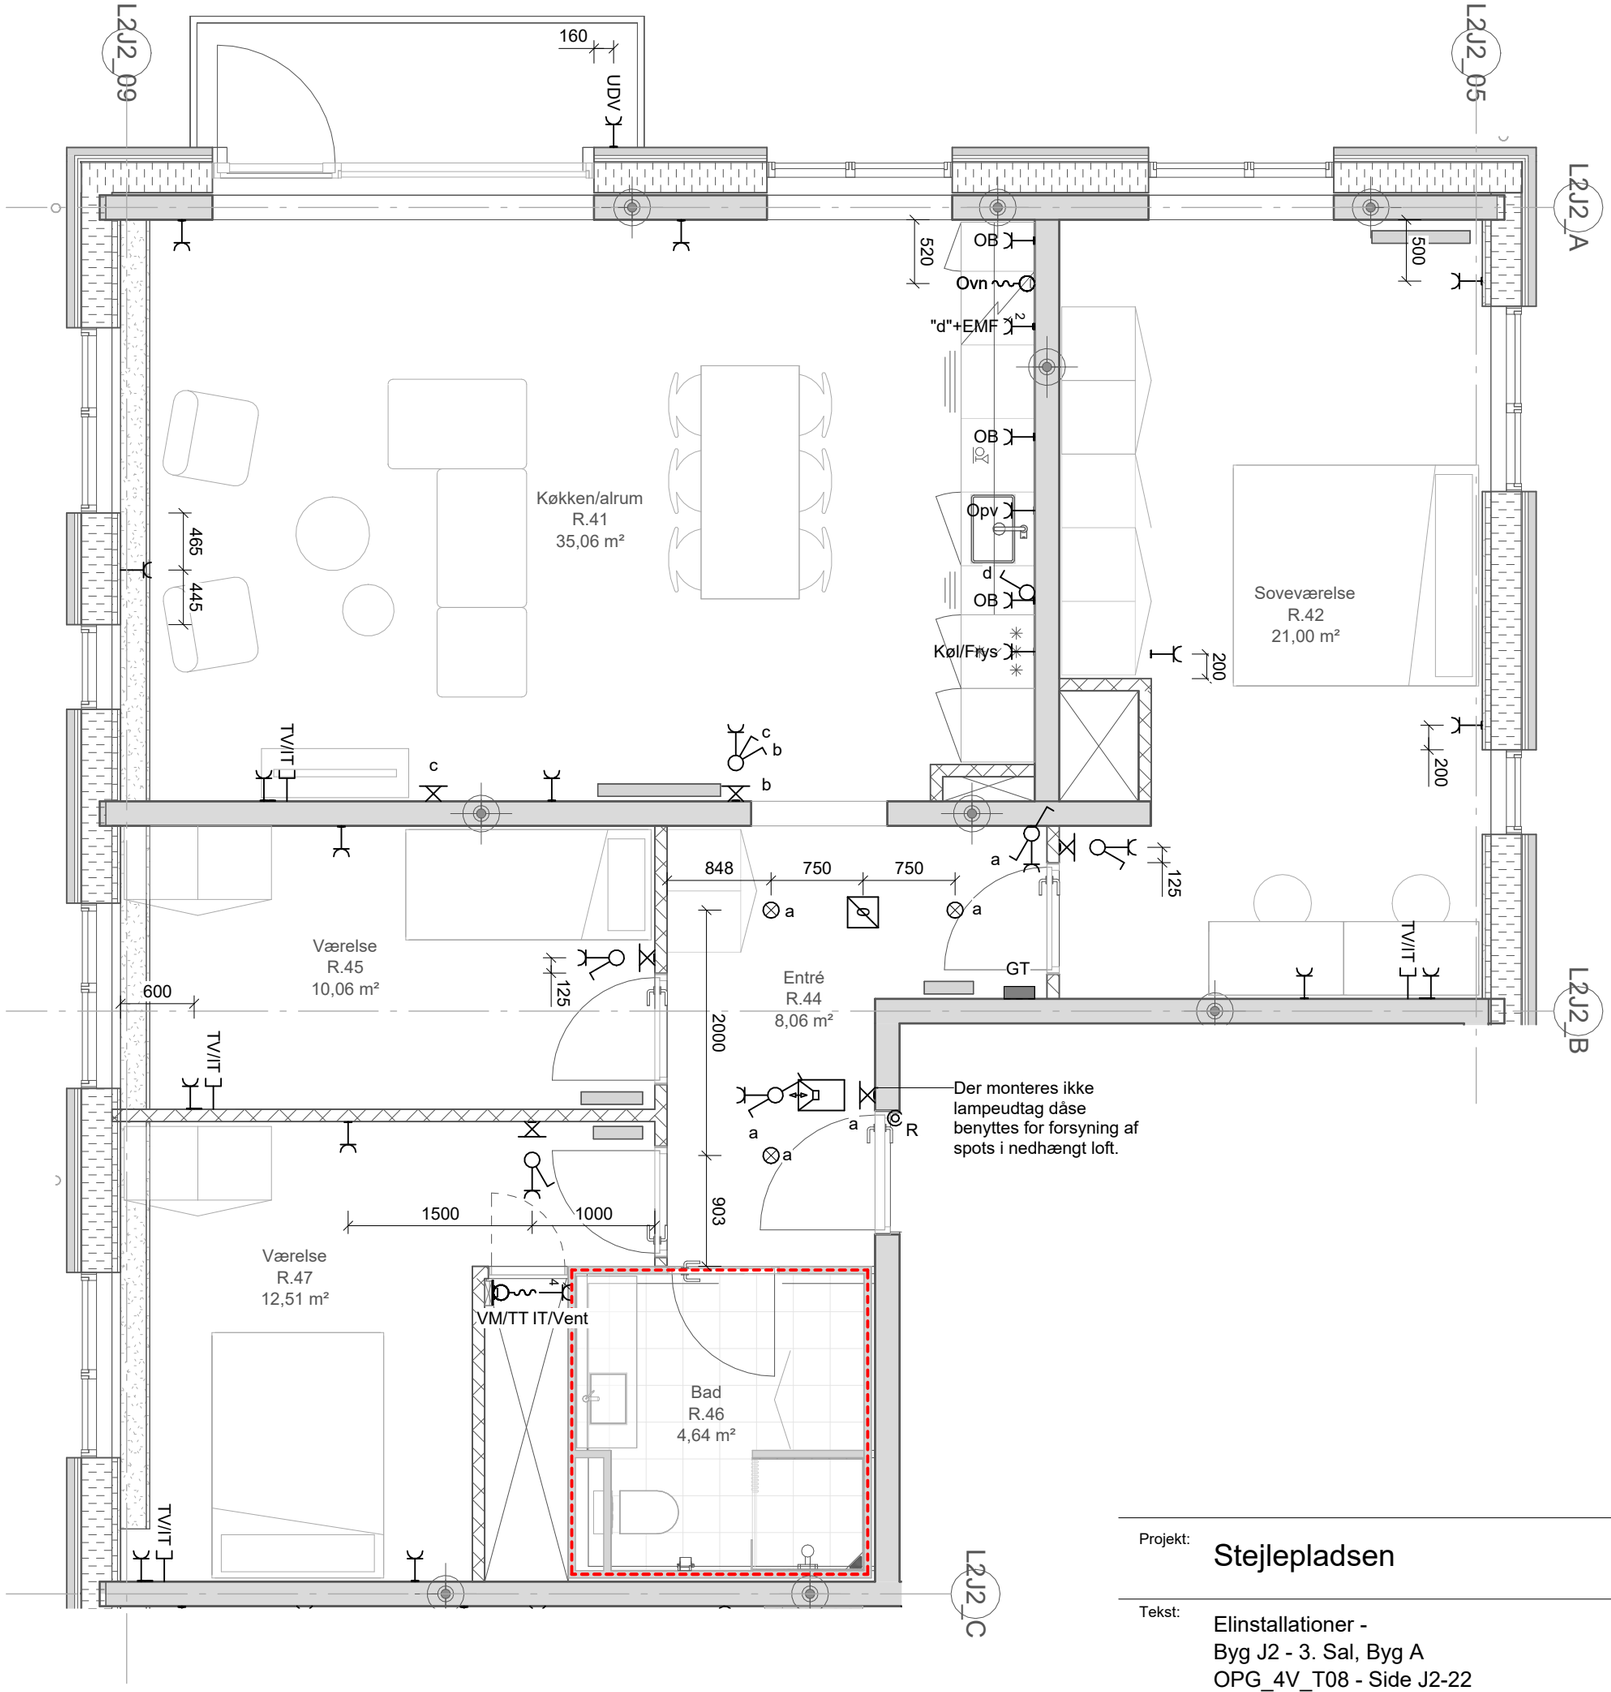

Projekt: Stejlepladsen


Tekst: Elinstallationer -
Byg J2 - 3. Sal, Byg A
OPG_4V_T08 - Side J2-22

Tegningsnr.: ISP2_K07_L2XX_H04_EXX_N930


Rev.:

Projektnr.: 1019198 | Dato: 2026-02-27 | Rev. Dato: | Mål: 1 : 50 | Side: J2-22

www.arteliagroup.dk | Fil:

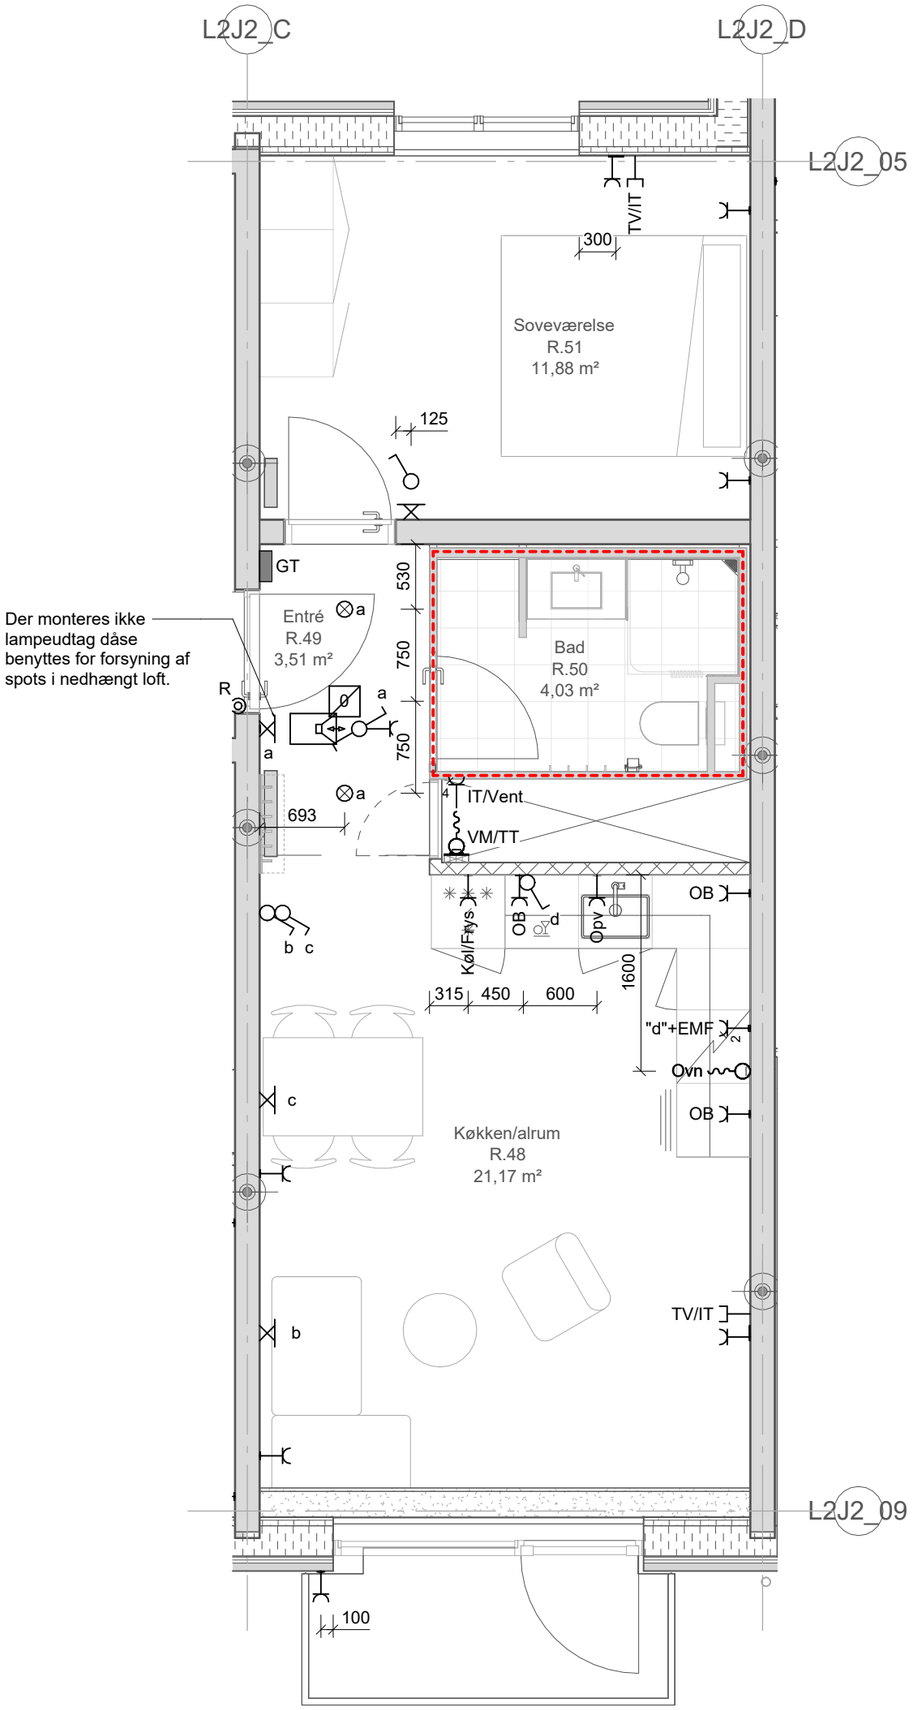

Projekt:	Stejlepladsen				
Tekst:	Elinstallationer - Byg J2 - 3. Sal, Byg A OPG_2V_T31 - Side J2-23			Tegningsnr.:	Rev.:
			ISP2_K07_L2XX_H04_EXX_N930		
Projektnr.: 1019198	Dato: 2026-02-27	Rev. Dato:		Mål: 1 : 50	Side: J2-23
www.arteliagroup.dk	Fil:				

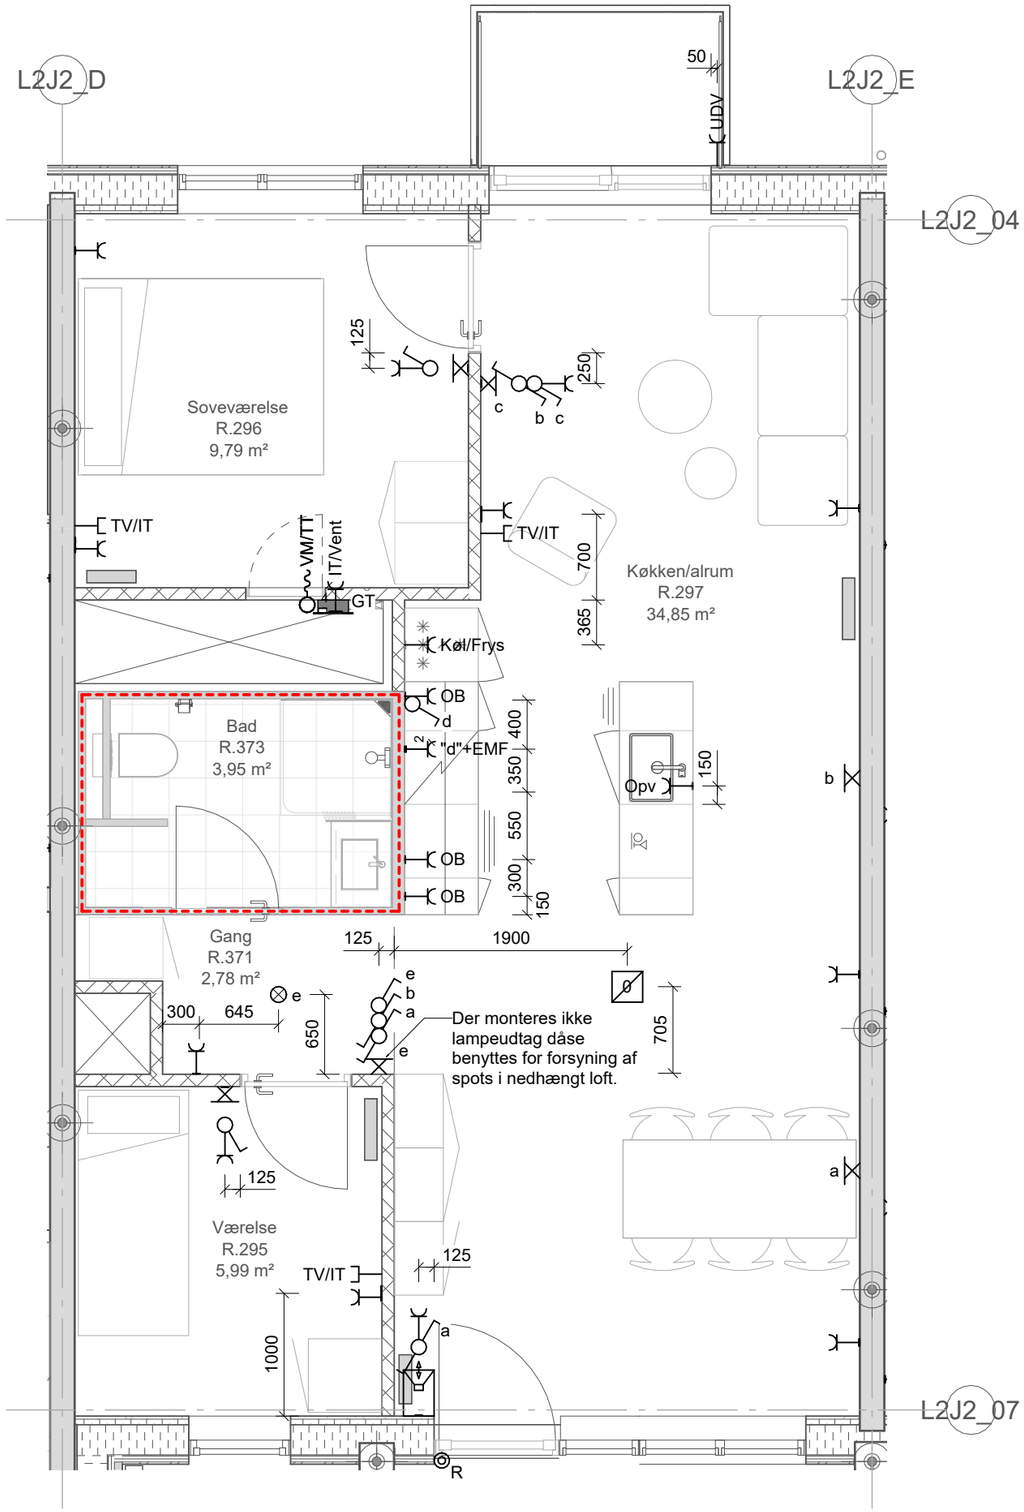

Projekt: Stejlepladsen


Tekst: Elinstallationer -
Byg J2 - 3. Sal, Byg B
ALT_3V_T30 - Side J2-24

Tegningsnr.: ISP2_K07_L2XX_H04_EXX_N930

Rev.:

Projektnr.: 1019198 | Dato: 2026-02-27 | Rev. Dato: | Mål: 1 : 50 | Side: J2-24

www.arteliagroup.dk | Fil:

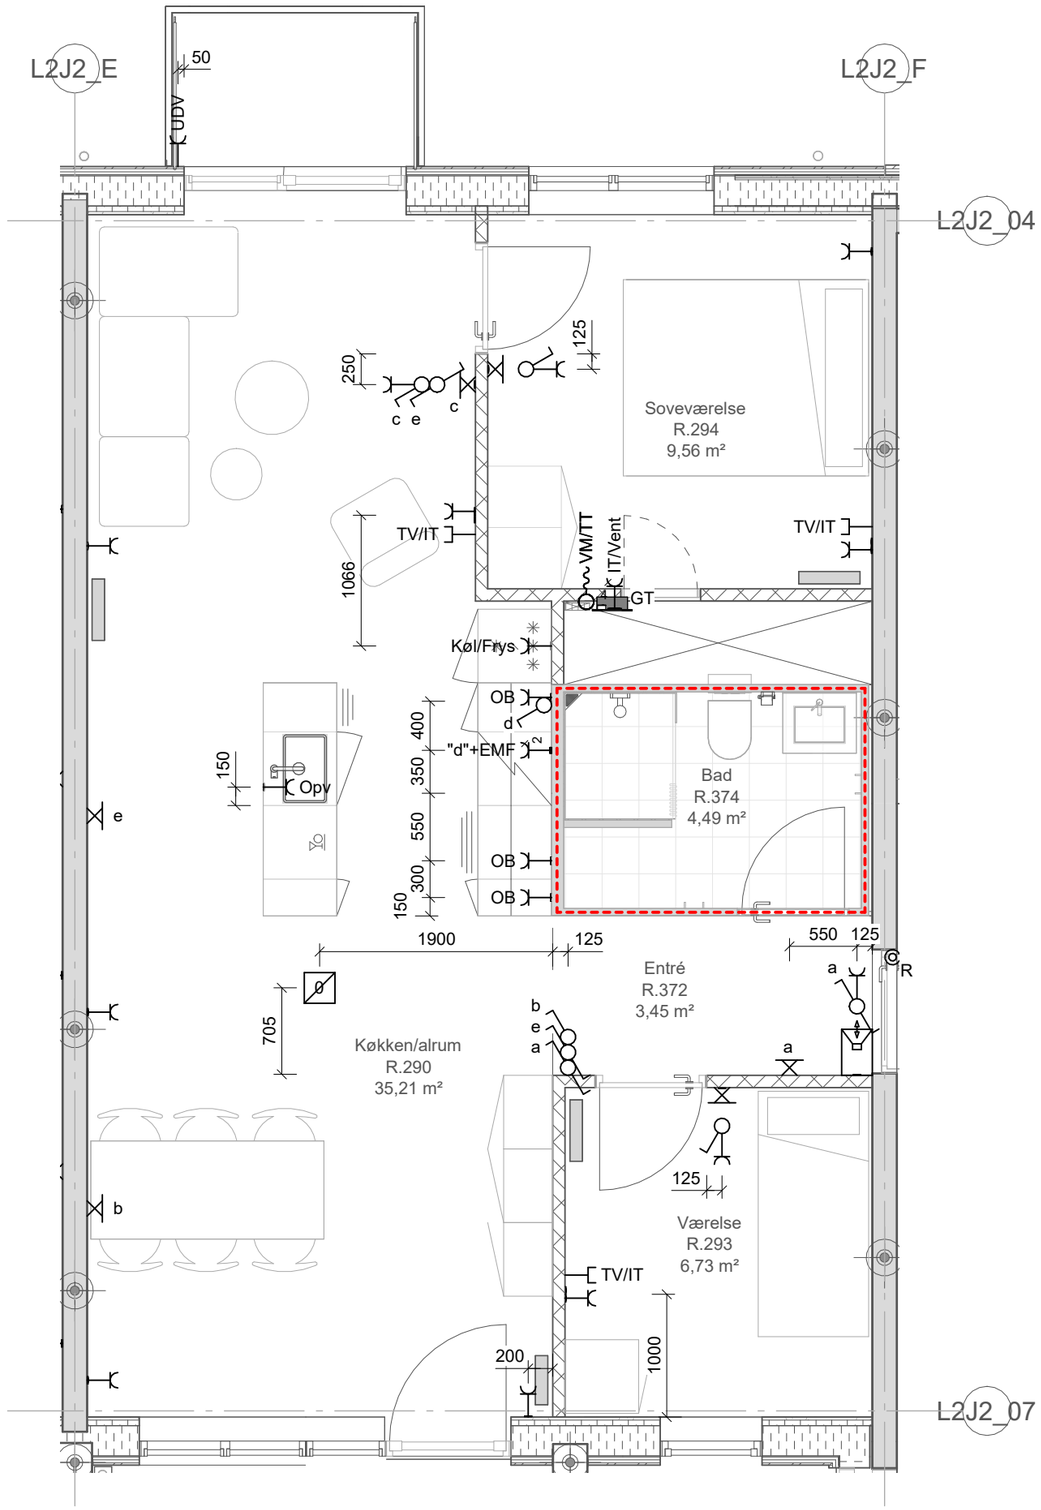

Projekt: Stejlepladsen

ARTELIA


Tekst: Elinstallationer -
Byg J2 - 3. Sal, Byg B
ALT_3V_T30_S - Side J2-25

Tegningsnr.: ISP2_K07_L2XX_H04_EXX_N930

Rev.:

Projektnr.: 1019198 | Dato: 2026-02-27 | Rev. Dato: | Mål: 1 : 50 | Side: J2-25

www.arteliagroup.dk | Fil:

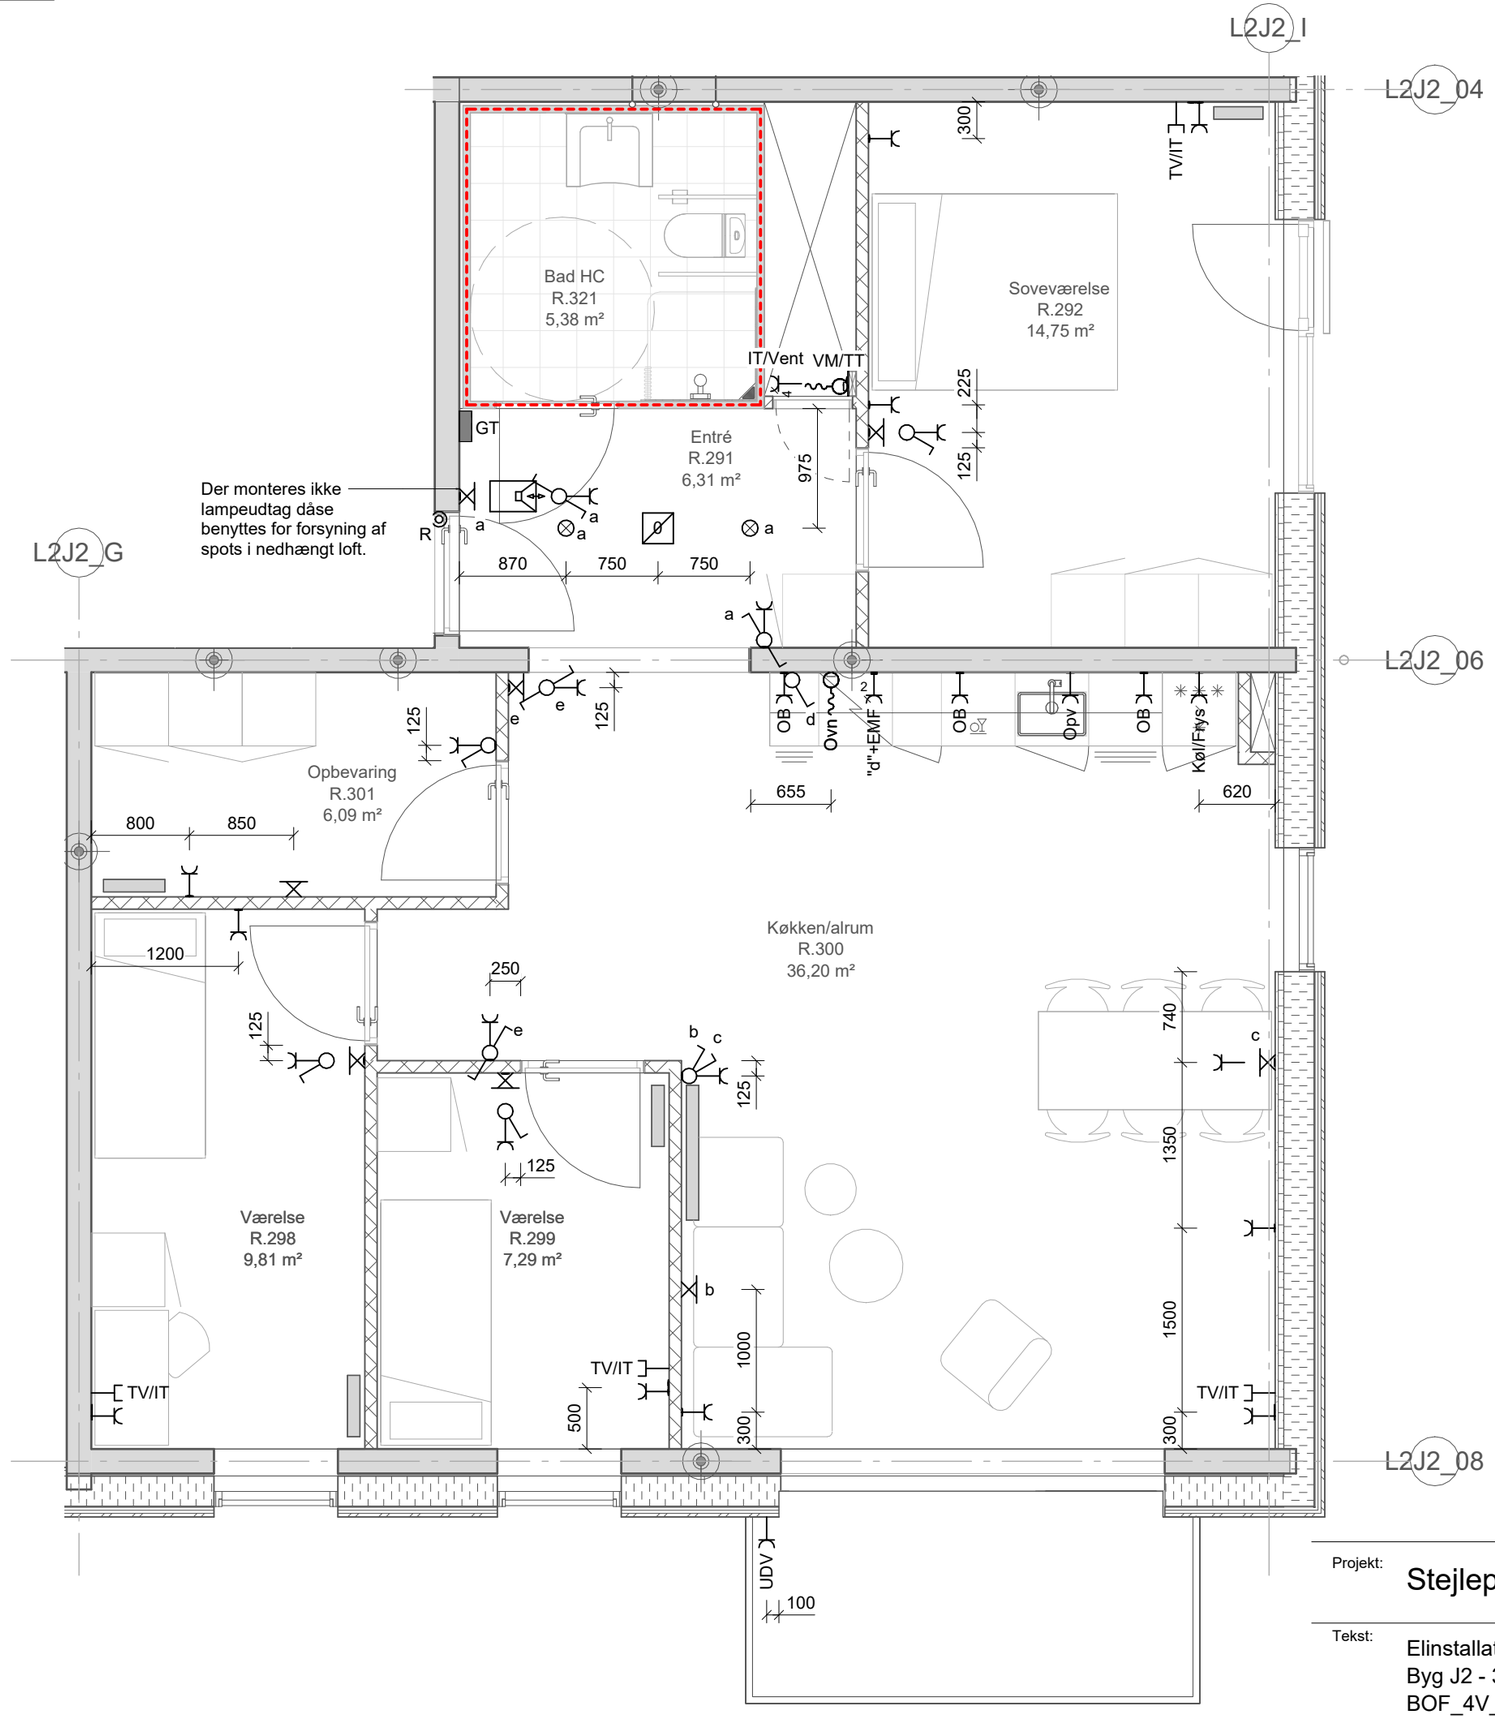

Projekt: Stejlepladsen


Tekst: Elinstallationer -
Byg J2 - 3. Sal, Byg B
BOF_4V_T31 - Side J2-26

Tegningsnr.: ISP2_K07_L2XX_H04_EXX_N930


Rev.:

Projektnr.: 1019198 | Dato: 2026-02-27 | Rev. Dato: | Mål: 1 : 50 | Side: J2-26


www.arteliagroup.dk | Fil:

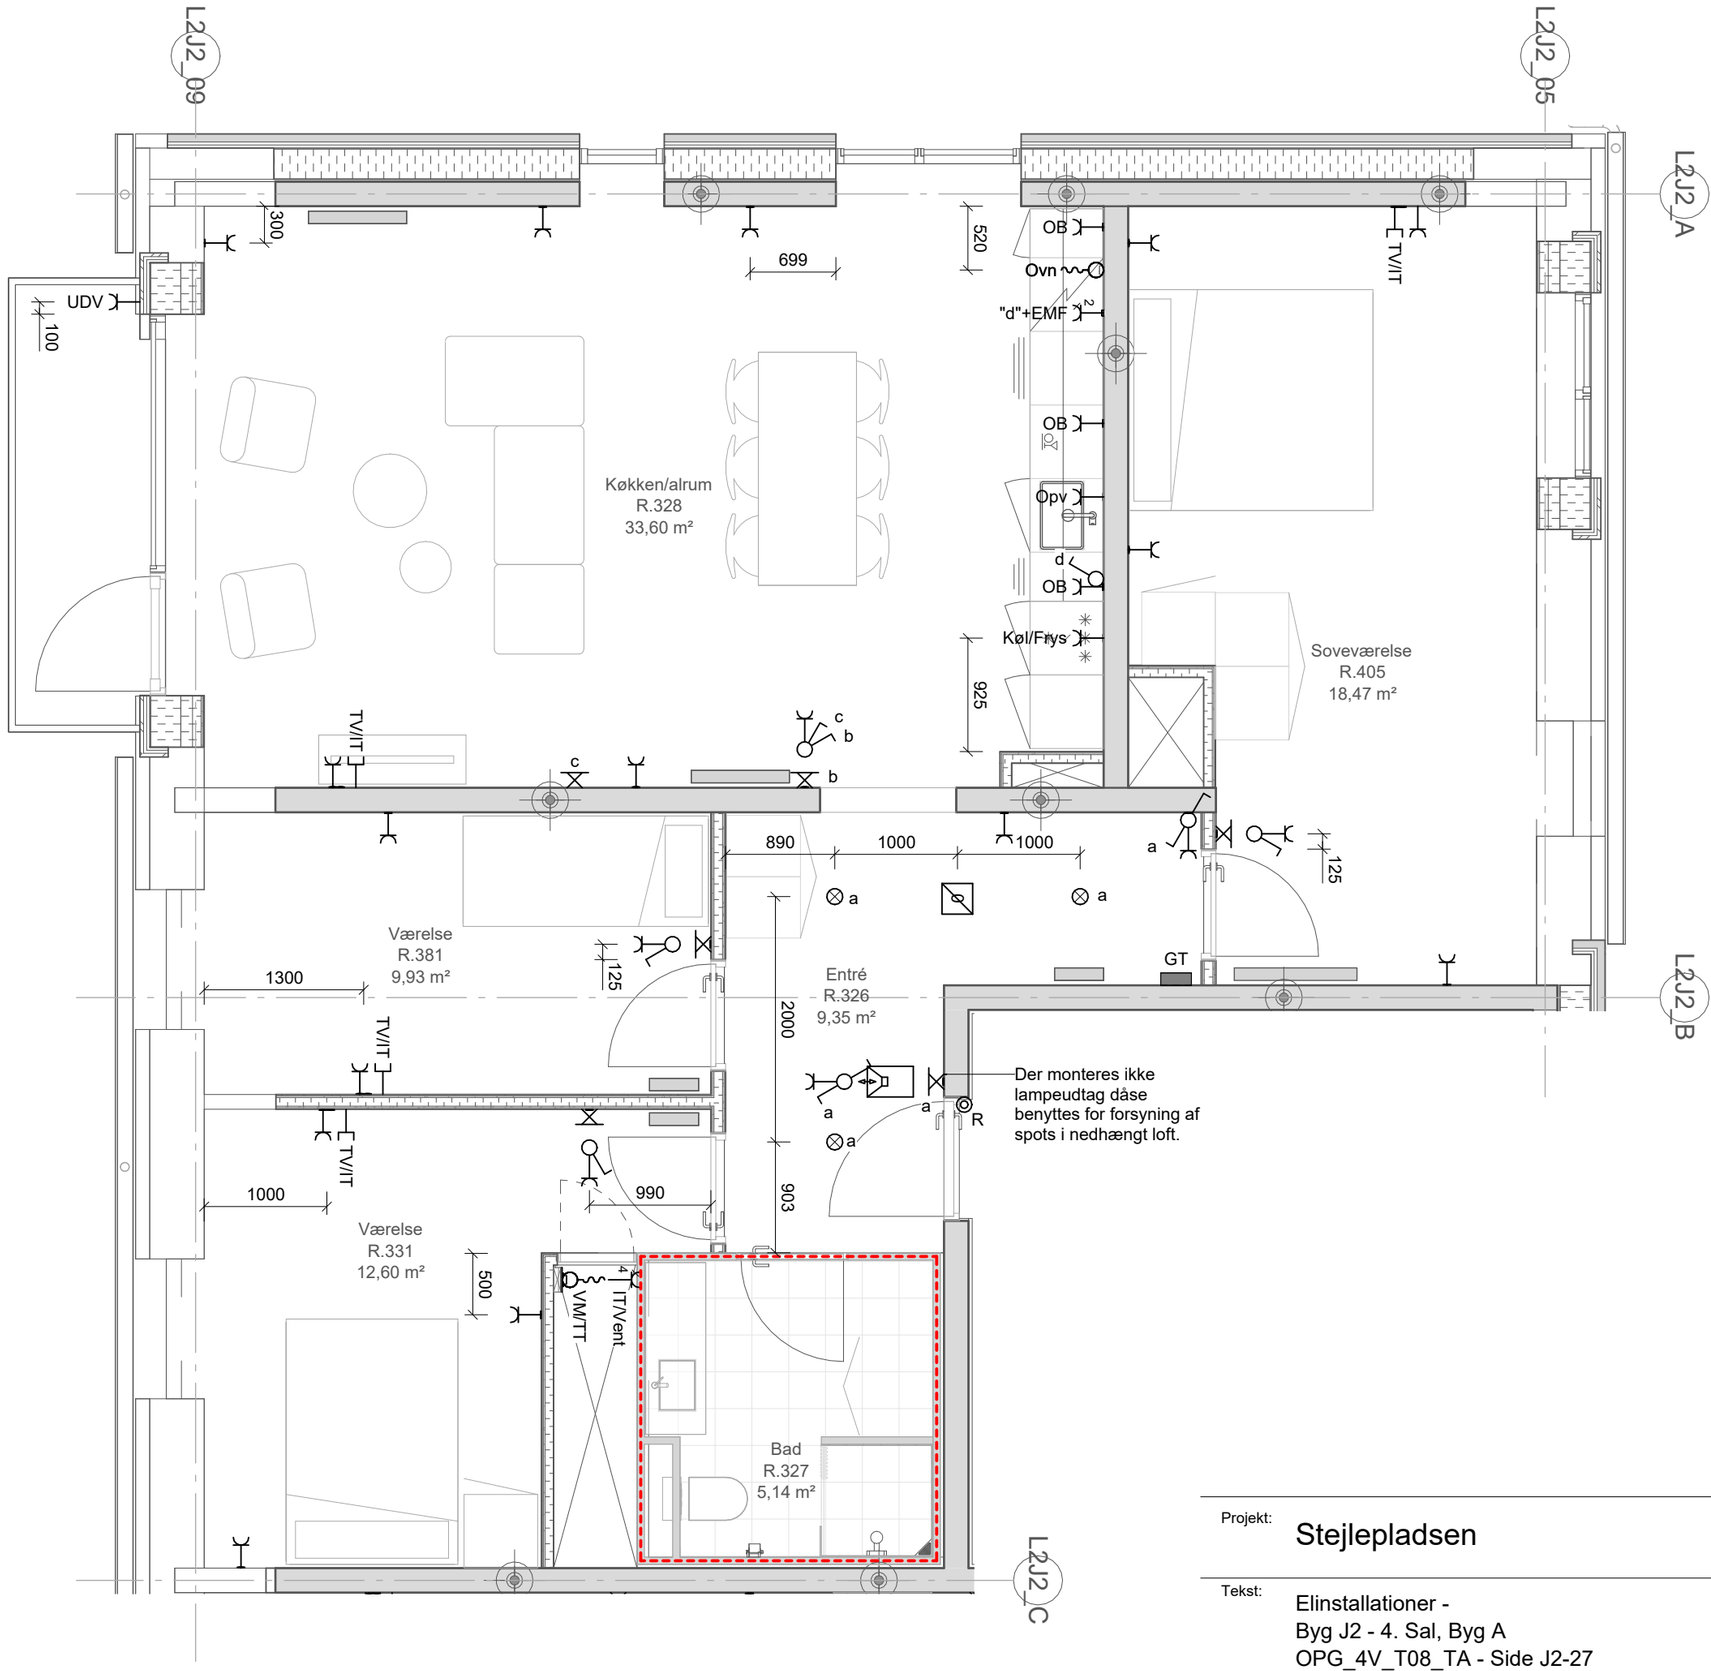

Projekt:	Stejlepladsen		
Tekst:	Elinstallationer - Byg J2 - 4. Sal, Byg A OPG_4V_T08_TA - Side J2-27	Tegningsnr.:	ISP2_K07_L2XX_H04_EXX_N930
Rev.:			
Projektnr.: 1019198	Dato: 2026-02-27	Rev. Dato:	Mål: 1 : 50
Side: J2-27			
www.arteliagroup.dk	Fil:		

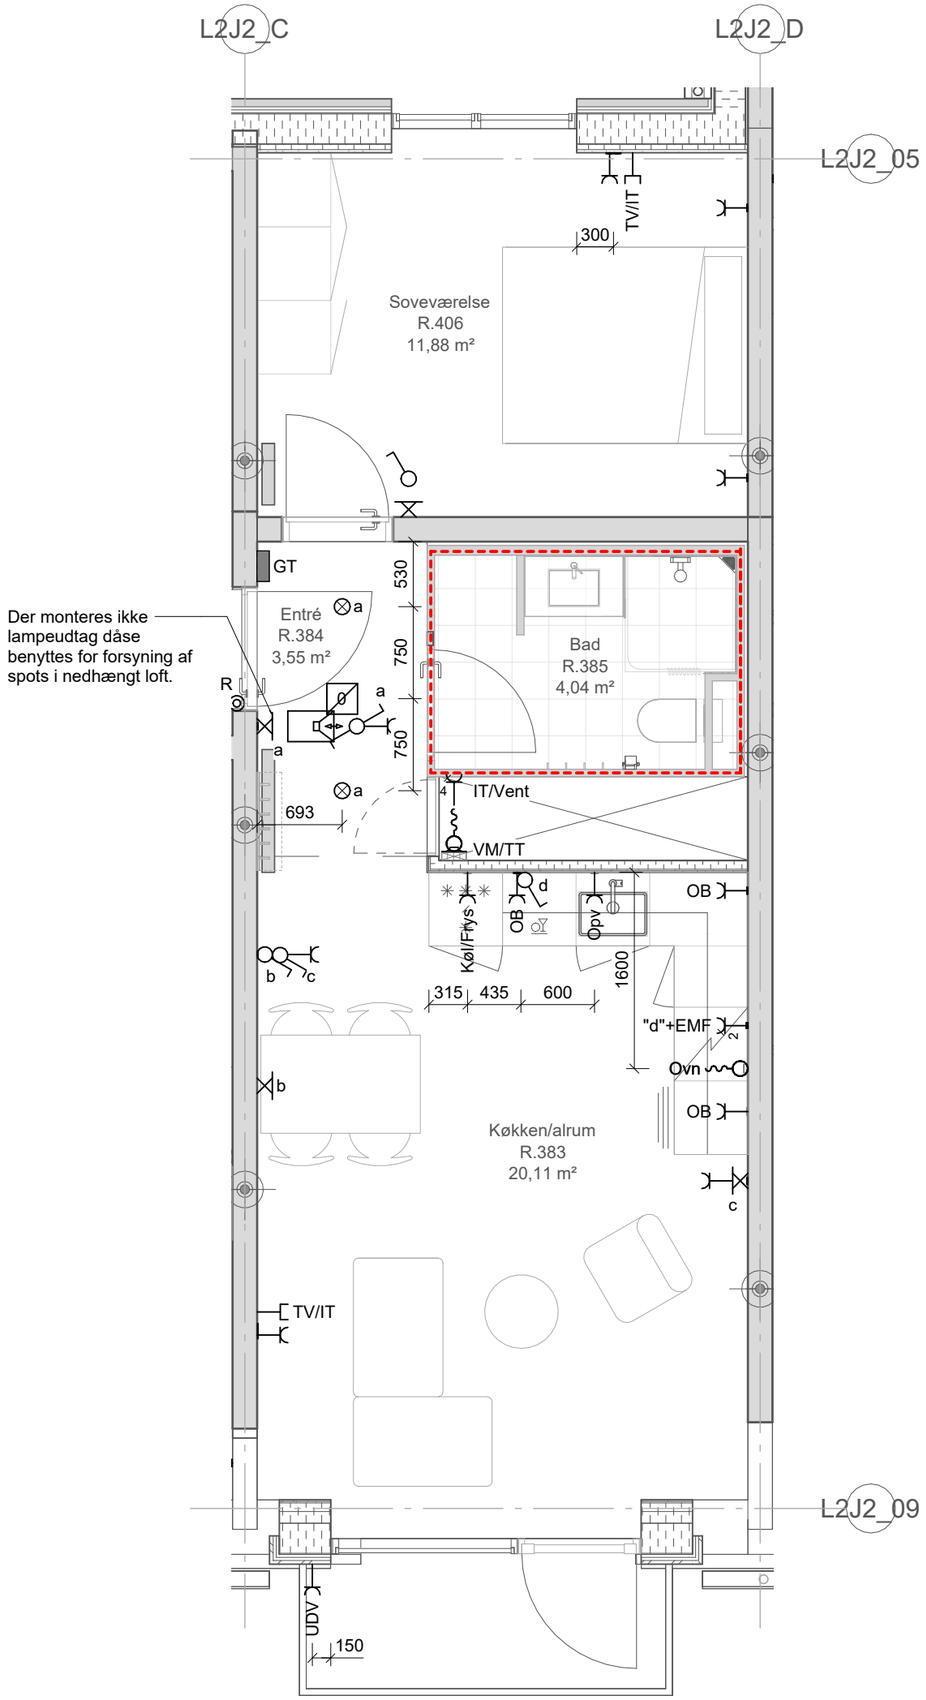

Projekt:	Stejlepladsen				
Tekst:	Elinstallationer - Byg J2 - 4. Sal, Byg A OPG_2V_T31_TA - Side J2-28			Tegningsnr.:	Rev.:
			ISP2_K07_L2XX_H04_EXX_N930		
Projektnr.: 1019198	Dato: 2026-02-27	Rev. Dato:		Mål: 1 : 50	Side: J2-28
www.arteliagroup.dk	Fil:				

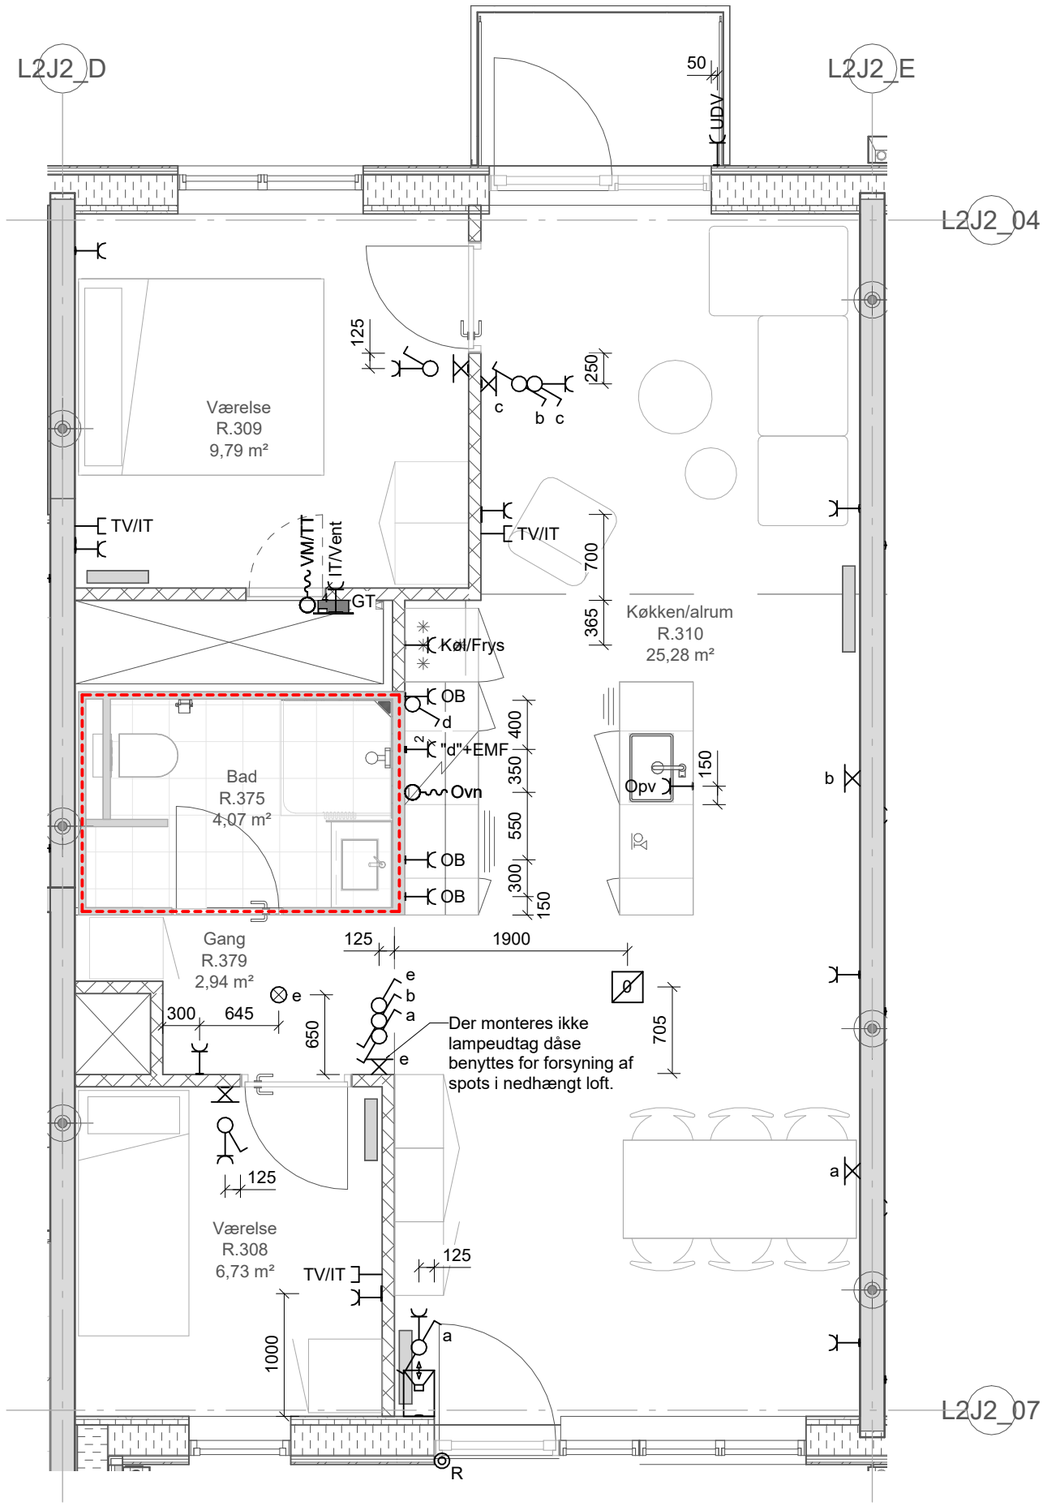

Projekt: Stejlepladsen


Tekst: Elinstallationer -
Byg J2 - 4. Sal, Byg B
ALT_3V_T30 - Side J2-29

Tegningsnr.: ISP2_K07_L2XX_H04_EXX_N930

Rev.:

Projektnr.: 1019198 | Dato: 2026-02-27 | Rev. Dato: | Mål: 1 : 50 | Side: J2-29

www.arteliagroup.dk | Fil:

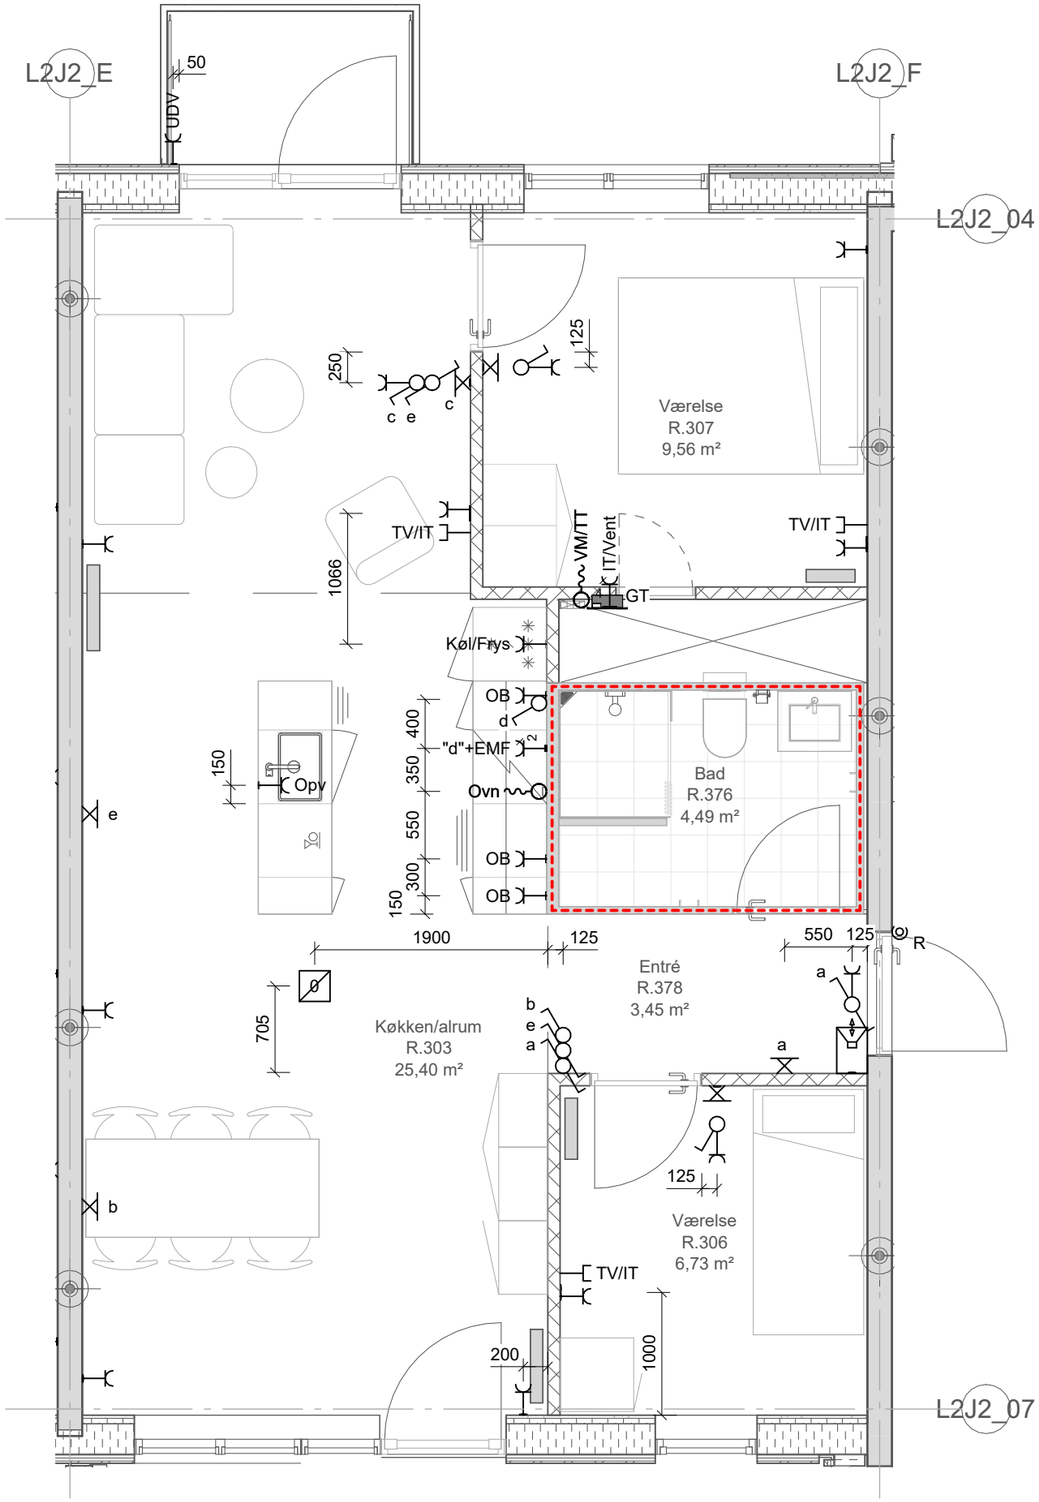

Projekt: Stejlepladsen


Tekst: Elinstallationer -
Byg J2 - 4. Sal, Byg B
ALT_3V_T30_S - Side J2-30

Tegningsnr.: ISP2_K07_L2XX_H04_EXX_N930

Rev.:

Projektnr.: 1019198 | Dato: 2026-02-27 | Rev. Dato: | Mål: 1 : 50 | Side: J2-30

www.arteliagroup.dk | Fil:

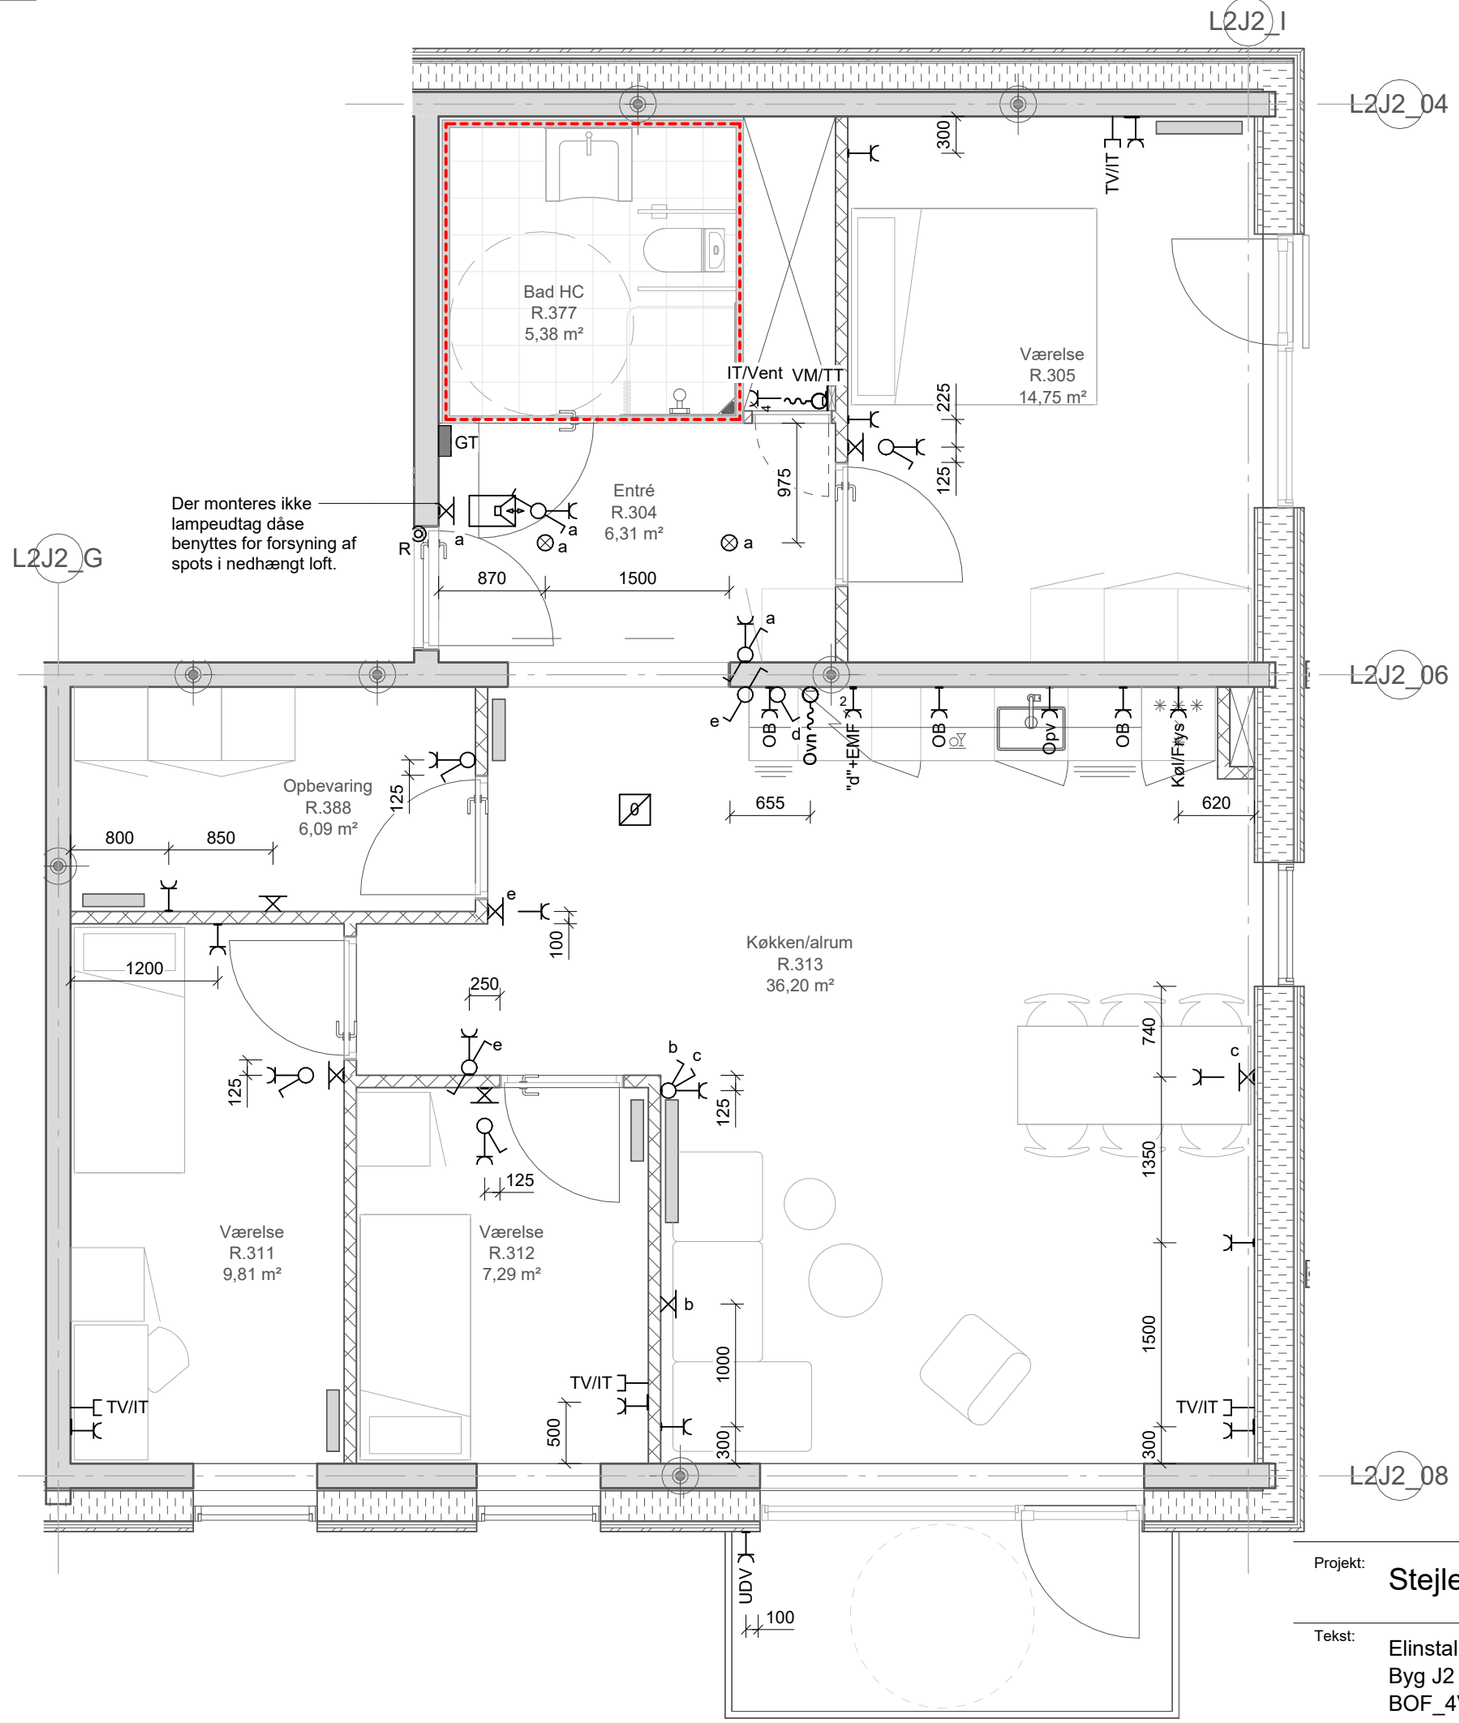

Projekt: Stejlepladsen

Tekst: Elinstallationer -
Byg J2 - 4. Sal, Byg B
BOF_4V_T31 - Side J2-31

Tegningsnr.: ISP2_K07_L2XX_H04_EXX_N930

Rev.:

Projektnr.: 1019198 | Dato: 2026-02-27 | Rev. Dato: | Mål: 1 : 50 | Side: J2-31

www.arteliagroup.dk | Fil: