Sheet Number	Tekst:	Dato:	Rev.:	Rev. Dato:
ISP2_K07_L2XX_H04_EXX_N930 - Side K1-1	Byg K1 - Index	2026-02-27		
ISP2_K07_L2XX_H04_EXX_N930 - Side K1-2	Byg K1 - Oversigtsplan	2026-02-27		
ISP2_K07_L2XX_H04_EXX_N930 - Side K1-3	Byg K1 - Stueplan, Byg A	2026-02-27		
ISP2_K07_L2XX_H04_EXX_N930 - Side K1-4	Byg K1 - Stueplan, Byg A	2026-02-27		
ISP2_K07_L2XX_H04_EXX_N930 - Side K1-5	Byg K1 - Stueplan, Byg B	2026-02-27		
ISP2_K07_L2XX_H04_EXX_N930 - Side K1-6	Byg K1 - Stueplan, Byg B	2026-02-27		
ISP2_K07_L2XX_H04_EXX_N930 - Side K1-8	Byg K1 - 1. Sal, Byg A	2026-02-27		
ISP2_K07_L2XX_H04_EXX_N930 - Side K1-9	Byg K1 - 1. Sal, Byg B	2026-02-27		
ISP2_K07_L2XX_H04_EXX_N930 - Side K1-10	Byg K1 - 1. Sal, Byg B	2026-02-27		
ISP2_K07_L2XX_H04_EXX_N930 - Side K1-11	Byg K1 - 2. Sal, Byg A	2026-02-27		
ISP2_K07_L2XX_H04_EXX_N930 - Side K1-12	Byg K1 - 2. Sal, Byg A	2026-02-27		
ISP2_K07_L2XX_H04_EXX_N930 - Side K1-13	Byg K1 - 2. Sal, Byg B	2026-02-27		
ISP2_K07_L2XX_H04_EXX_N930 - Side K1-14	Byg K1 - 2. Sal, Byg B	2026-02-27		
ISP2_K07_L2XX_H04_EXX_N930 - Side K1-15	Byg K1 - 3. Sal, Byg A	2026-02-27		
ISP2_K07_L2XX_H04_EXX_N930 - Side K1-16	Byg K1 - 3. Sal, Byg B	2026-02-27		
ISP2_K07_L2XX_H04_EXX_N930 - Side K1-17	Byg K1 - 3. Sal, Byg B	2026-02-27		

Projekt: Stejlepladsen

Tekst: Elinstallationer - Byg K1 - Index

Tegningsnr.: ISP2_K07_L2XX_H04_EXX_N930

Rev.:

Projektnr.: 1019198 | Dato: 2026-02-27 | Rev. Dato: | Mål: | Side: K1-1

www.arteliagroup.dk | Fil:


Stueplan - Byg K1




1. sal - Byg K1



2. sal - Byg K1

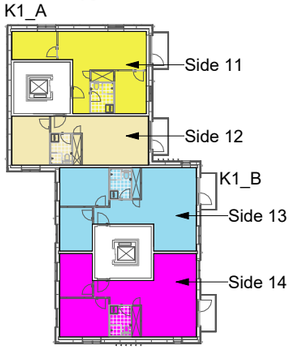

3. sal - Byg K1

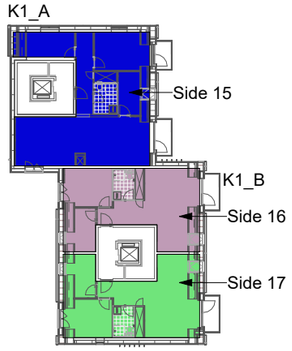

Oversigt, bygning K1:

Side 3:	Opgangsbolig, Byg A, st.,2V
Side 4:	Opgangsbolig, Byg A, st.,2V
Side 5:	Opgangsbolig, Byg B, st.,2V
Side 6:	Opgangsbolig, Byg B, st.,2V
Side 7:	Opgangsbolig, Byg A, 1. sal, 3V
Side 8:	Opgangsbolig, Byg A, 1.sal, 2V
Side 9:	Opgangsbolig, Byg B, 1. sal, 3V
Side 10:	Opgangsbolig, Byg B, 1. sal, 3V
Side 11:	Opgangsbolig, Byg A, 2. sal, 3V
Side 12:	Opgangsbolig, Byg A, 2.sal, 2V
Side 13:	Opgangsbolig, Byg B, 2. sal, 3V
Side 14:	Opgangsbolig, Byg B, 2. sal, 3V
Side 15:	Opgangsbolig, Byg A, 3. sal, 4V
Side 16:	Opgangsbolig, Byg B, 3. sal, 3V
Side 17:	Opgangsbolig, Byg B, 3. sal, 3V

Projekt: Stejlepladsen


Tekst: Elinstallationer -
Byg K1 - Oversigtsplan

Tegningsnr.: ISP2_K07_L2XX_H04_EXX_N930

Rev.:

Projektnr.: 1019198 | Dato: 2026-02-27 | Rev. Dato: | Mål: 1 : 500 | Side: K1-2

www.arteliagroup.dk | Fil:

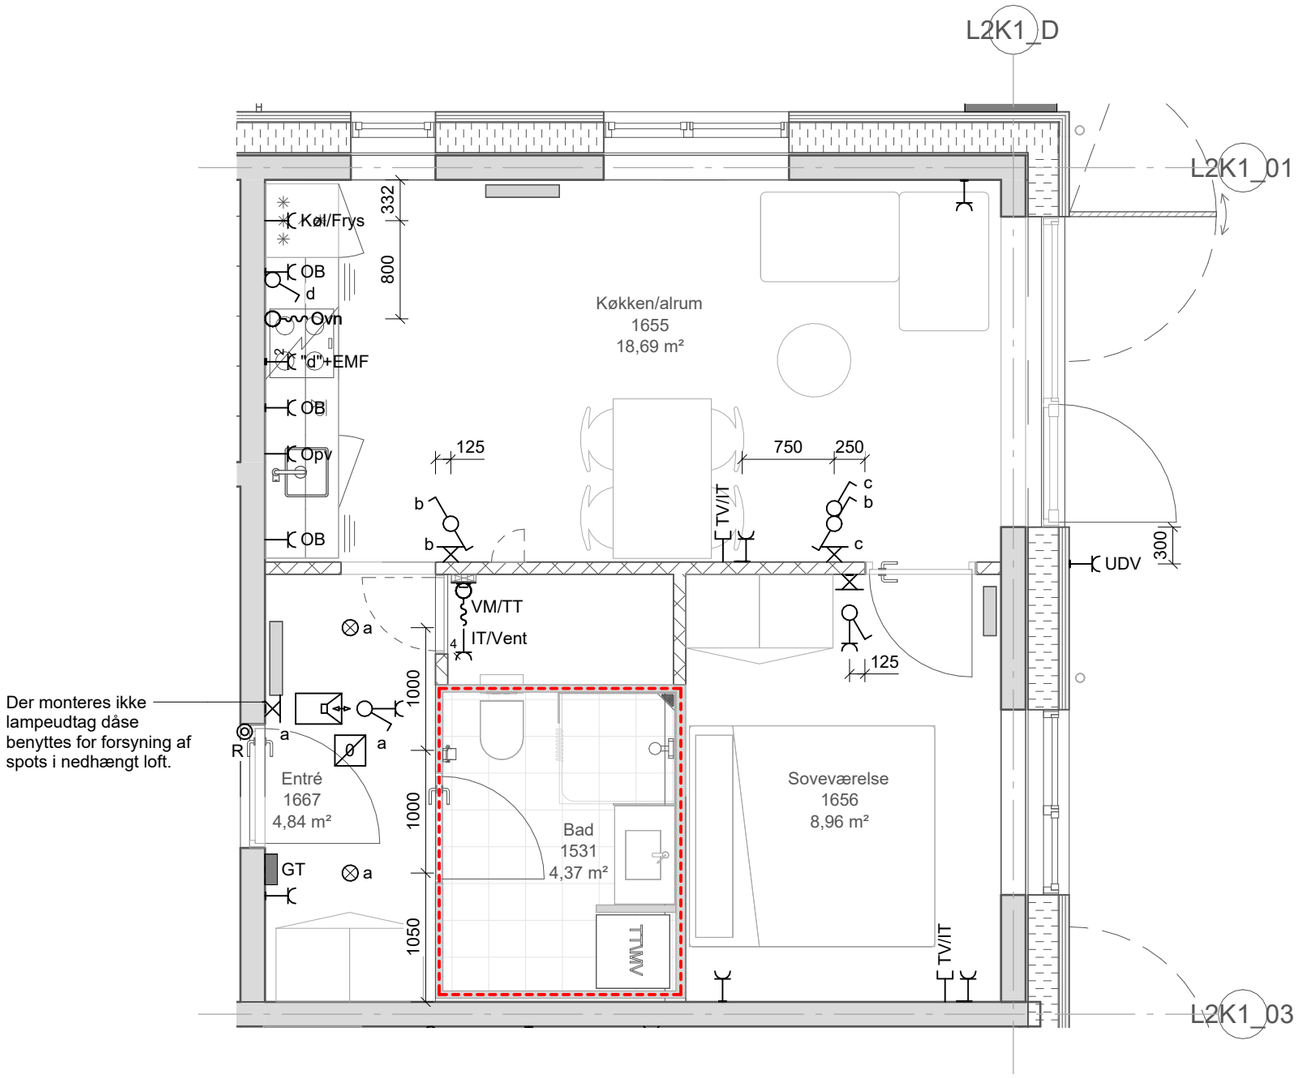

Projekt: Stejlepladsen


Tekst: Elinstallationer -
Byg K1 - Stueplan, Byg A
OPG_2V_T30_ST - Side K1-3

Tegningsnr.: ISP2_K07_L2XX_H04_EXX_N930


Rev.:

Projektnr.: 1019198 | Dato: 2026-02-27 | Rev. Dato: | Mål: 1 : 50 | Side: K1-3


www.arteliagroup.dk | Fil:

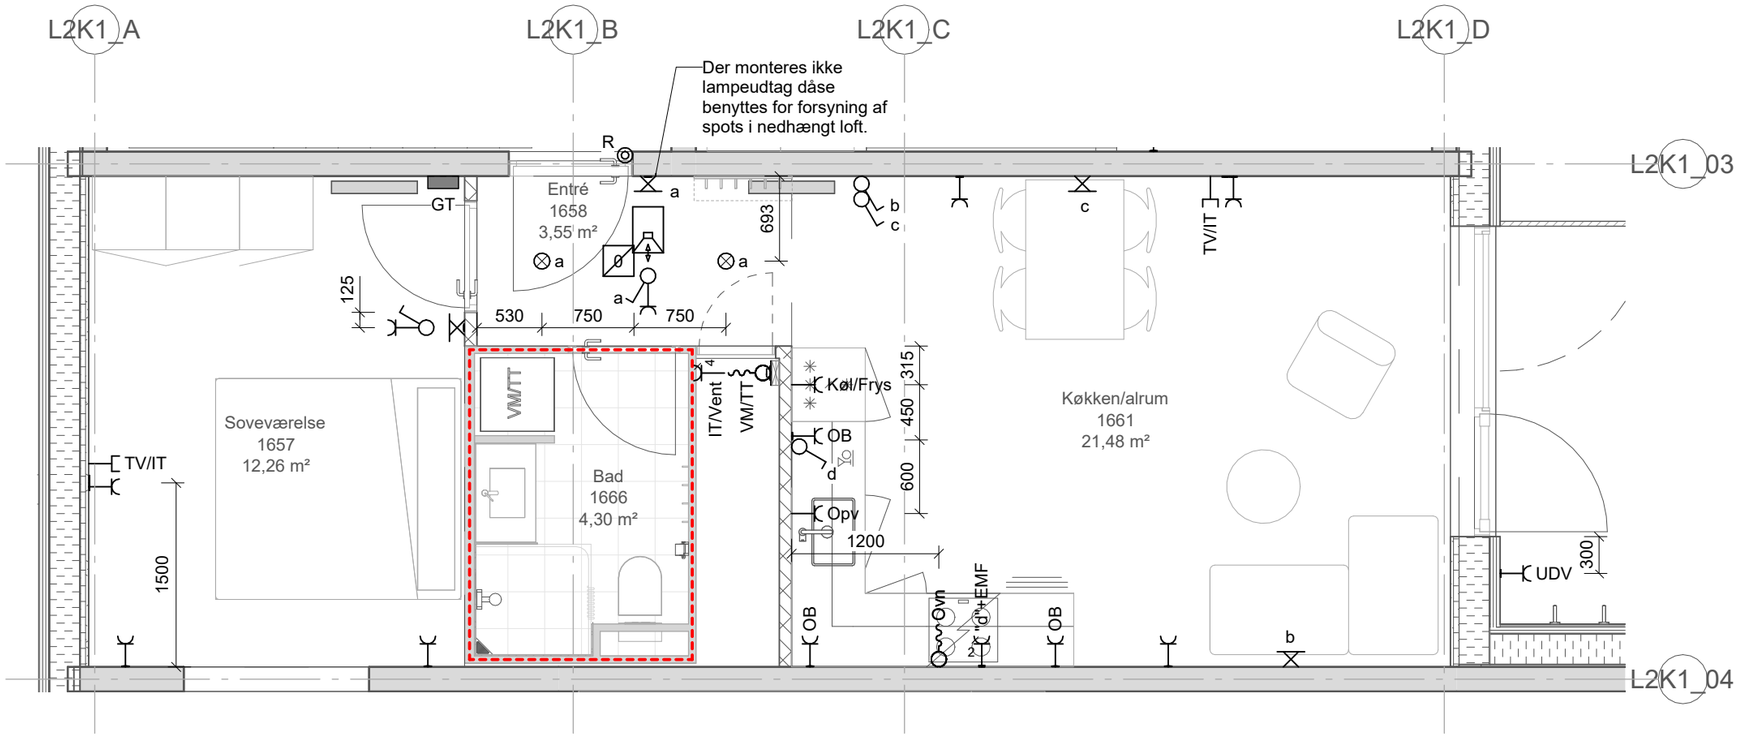


Projekt:	Stejlepladsen				
Tekst:	Elinstallationer - Byg K1 - Stueplan, Byg A OPG_2V_T31_ST_S - Side K1-4			Tegningsnr.:	Rev.:
				ISP2_K07_L2XX_H04_EXX_N930	
Projektnr.: 1019198	Dato: 2026-02-27	Rev. Dato:		Mål: 1 : 50	Side: K1-4
www.arteliagroup.dk	Fil:				

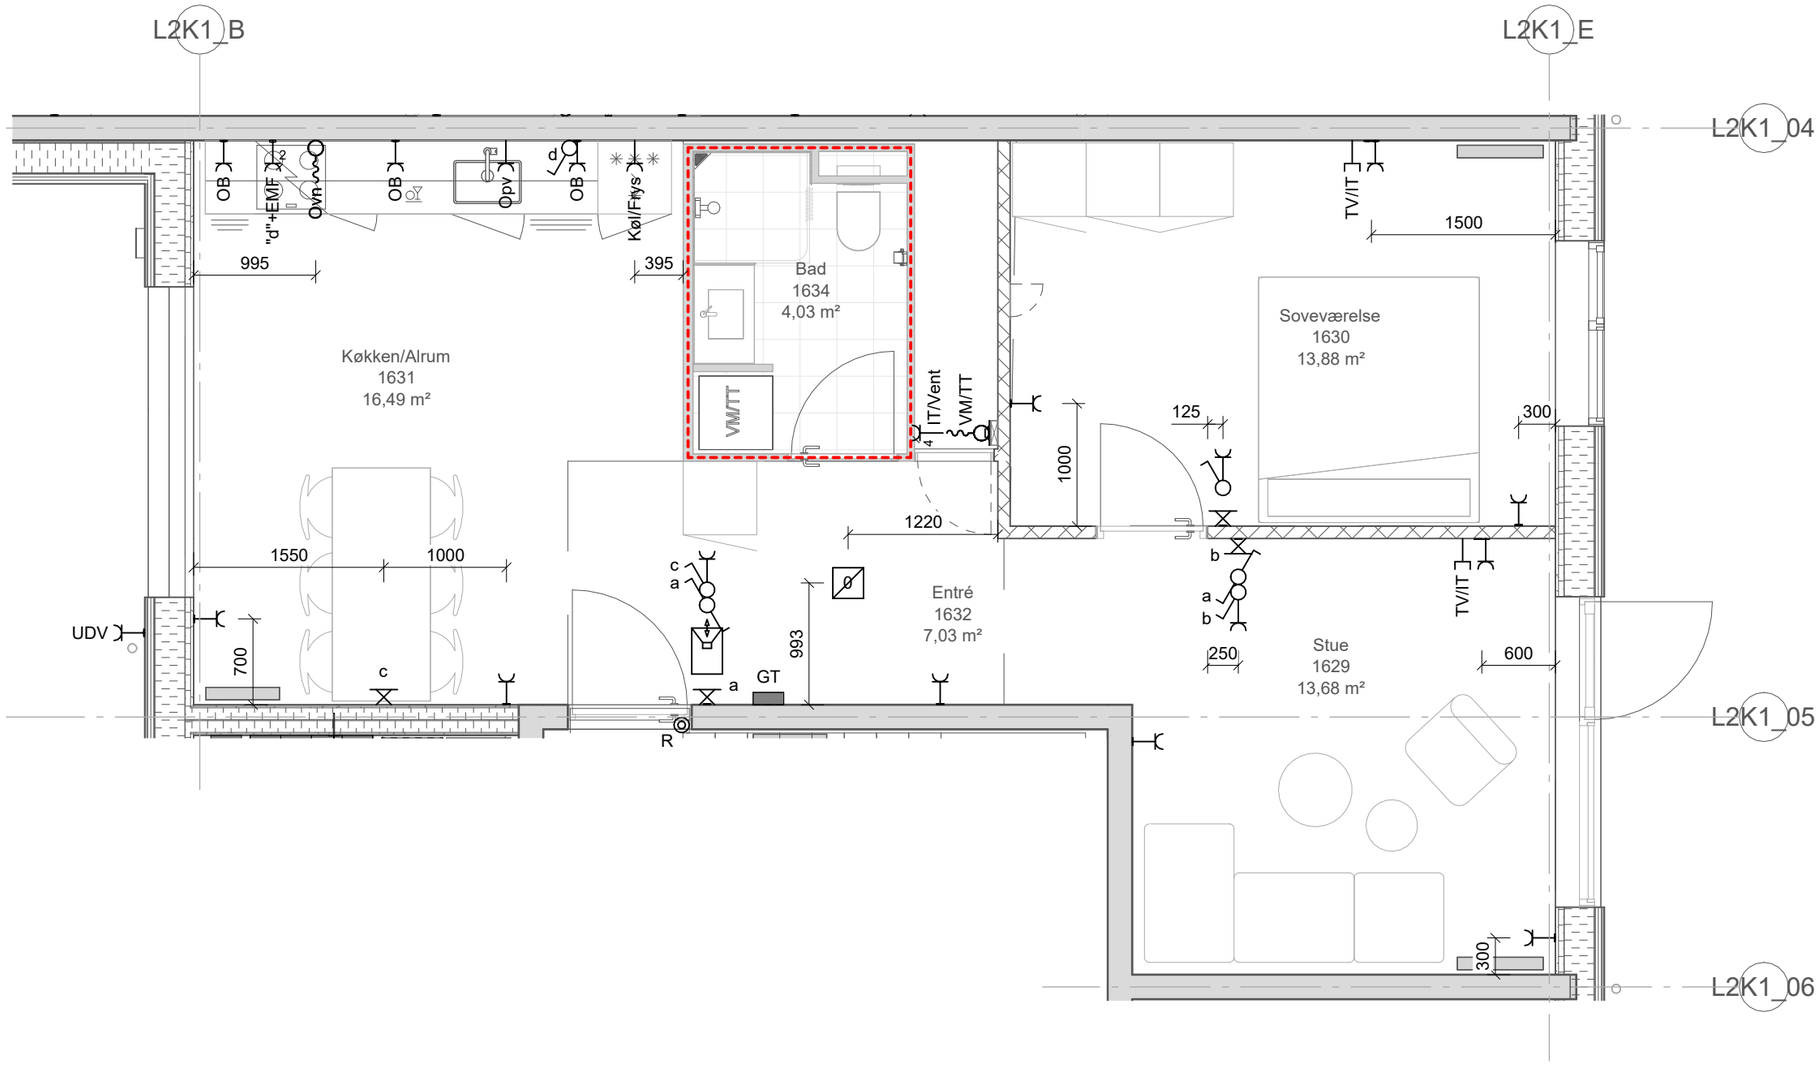


Projekt:	Stejlepladsen				
Tekst:	Elinstallationer - Byg K1 - Stueplan, Byg B OPG_2V_T01_ST_S - Side K1-5			Tegningsnr.:	Rev.:
			ISP2_K07_L2XX_H04_EXX_N930		
Projektnr.: 1019198	Dato: 2026-02-27	Rev. Dato:		Mål: 1 : 50	Side: K1-5
www.arteliagroup.dk	Fil:				

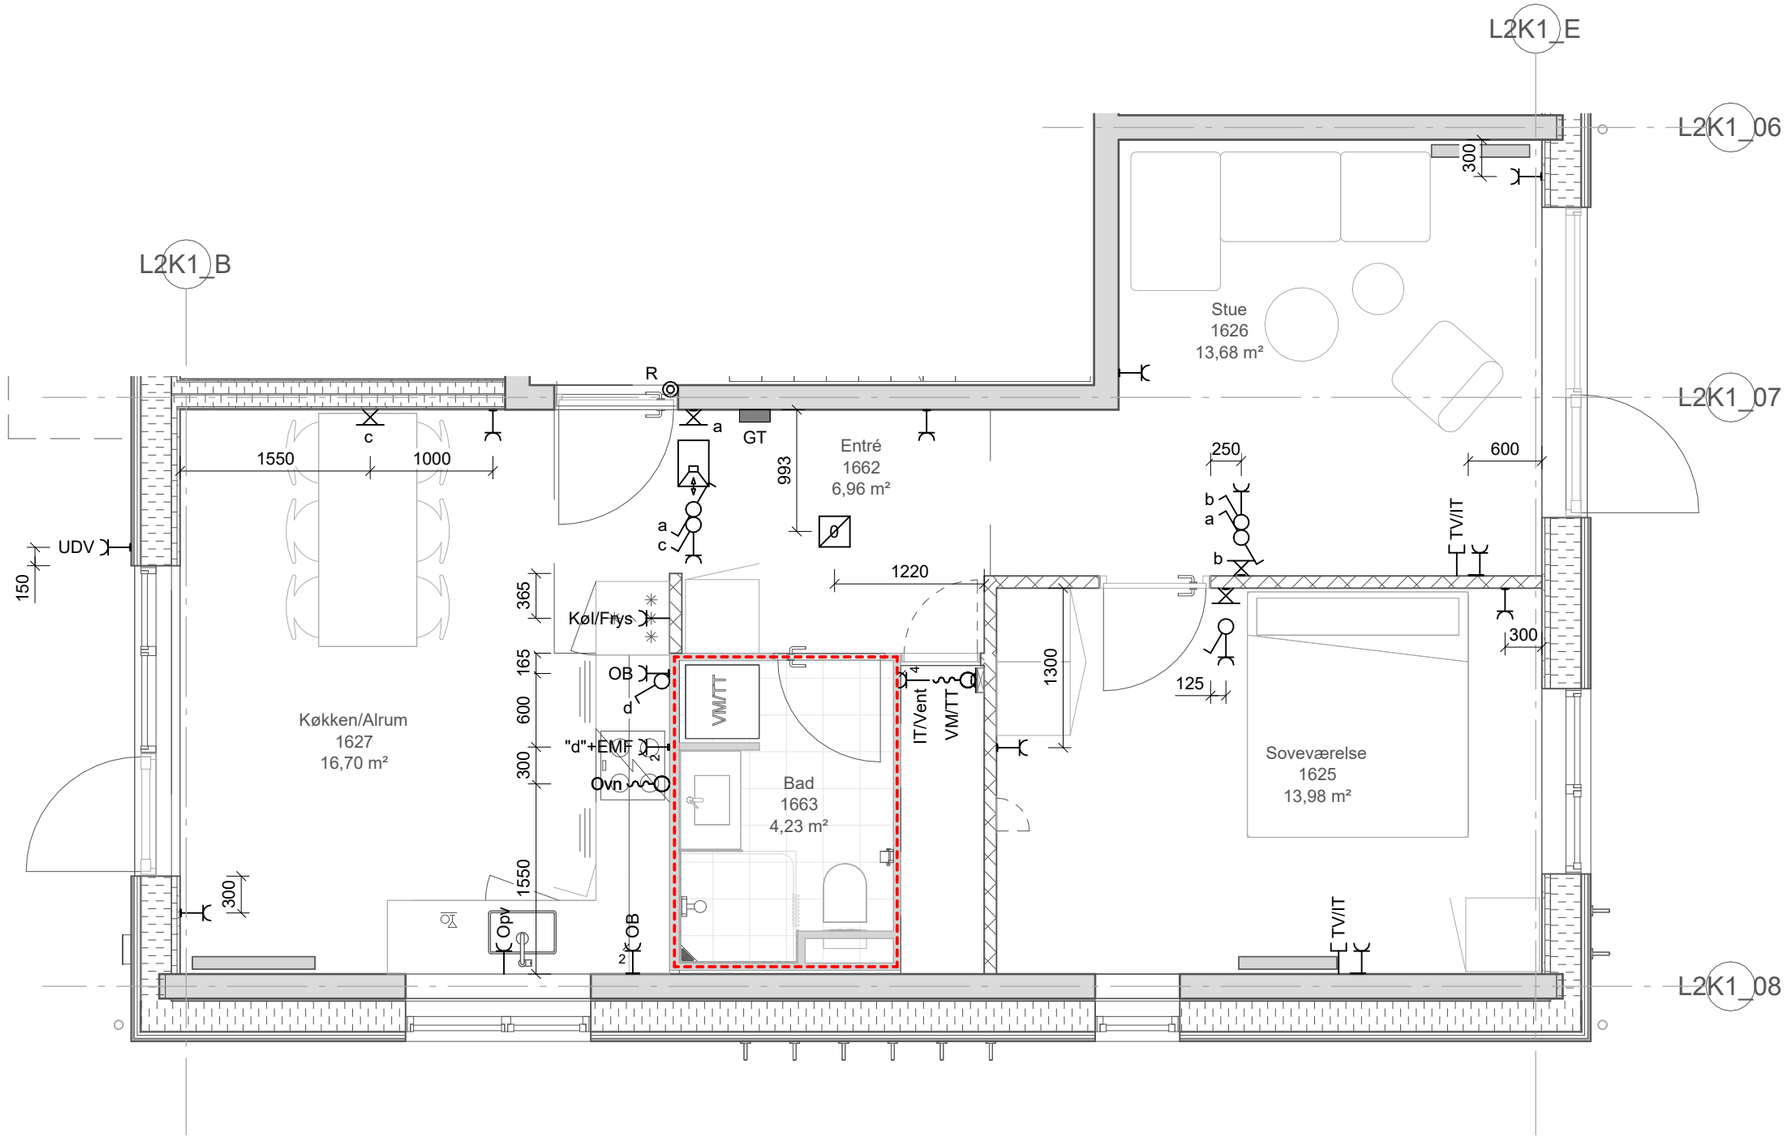


Projekt:	Stejlepladsen				
Tekst:	Elinstallationer - Byg K1 - Stueplan, Byg B OPG_2V_T01_ST - Side K1-6			Tegningsnr.:	Rev.:
			ISP2_K07_L2XX_H04_EXX_N930		
Projektnr.: 1019198	Dato: 2026-02-27	Rev. Dato:		Mål: 1 : 50	Side: K1-6
www.arteliagroup.dk	Fil:				

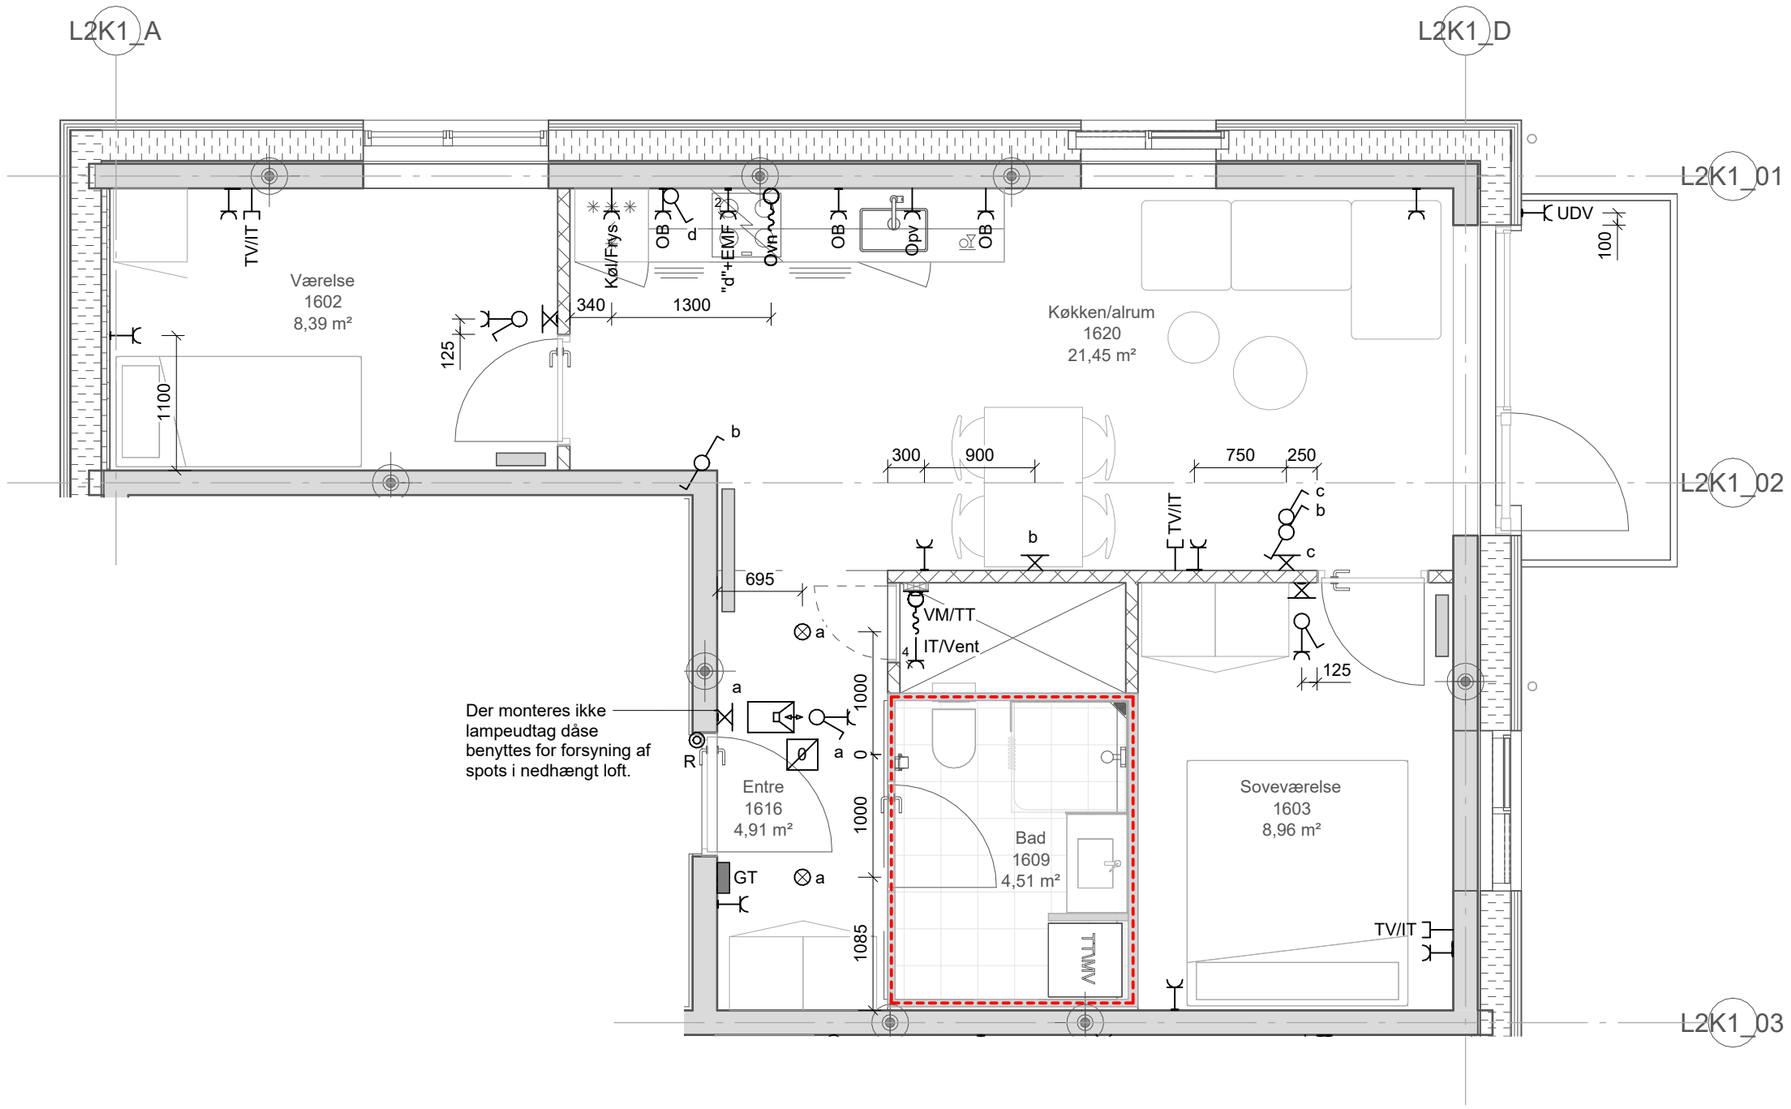


Projekt:	Stejlepladsen				
Tekst:	Elinstallationer - Byg K - 1. Sal, Byg A OPG_3V_T36 - Side K1-7			Tegningsnr.:	Rev.:
				ISP2_K07_L2XX_H04_EXX_N930	
Projektnr.: 1019198	Dato: 2026-02-27	Rev. Dato:		Mål: 1 : 50	Side: K1-7
www.arteliagroup.dk	Fil:				

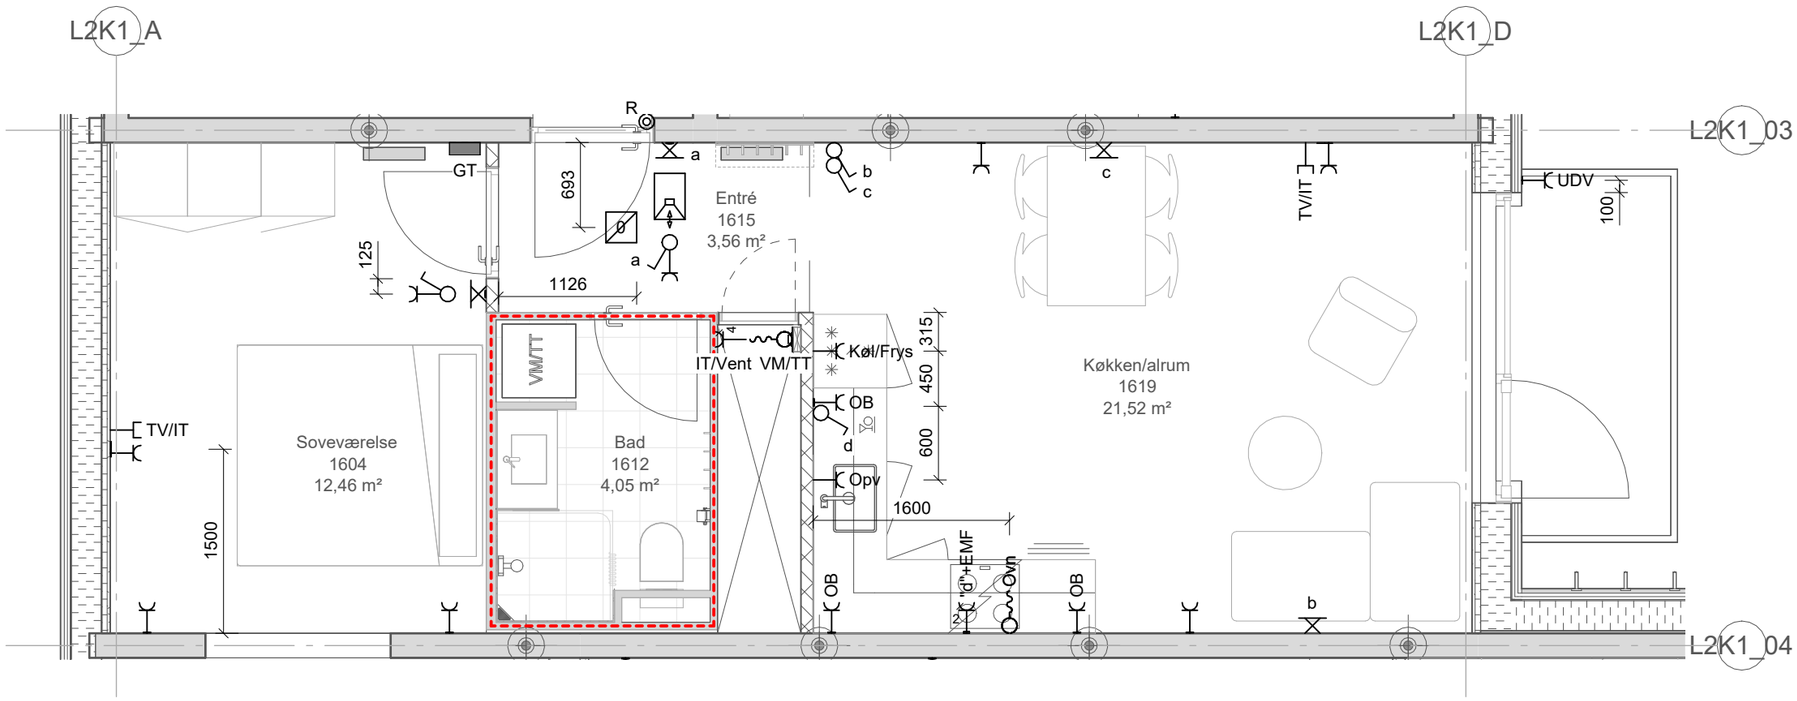

Projekt:	Stejlepladsen				
Tekst:	Elinstallationer - Byg K1 - 1. Sal, Byg A OPG_2V_T31_S - Side K1-8			Tegningsnr.:	Rev.:
			ISP2_K07_L2XX_H04_EXX_N930		
Projektnr.: 1019198	Dato: 2026-02-27	Rev. Dato:		Mål: 1 : 50	Side: K1-8
www.arteliagroup.dk	Fil:				

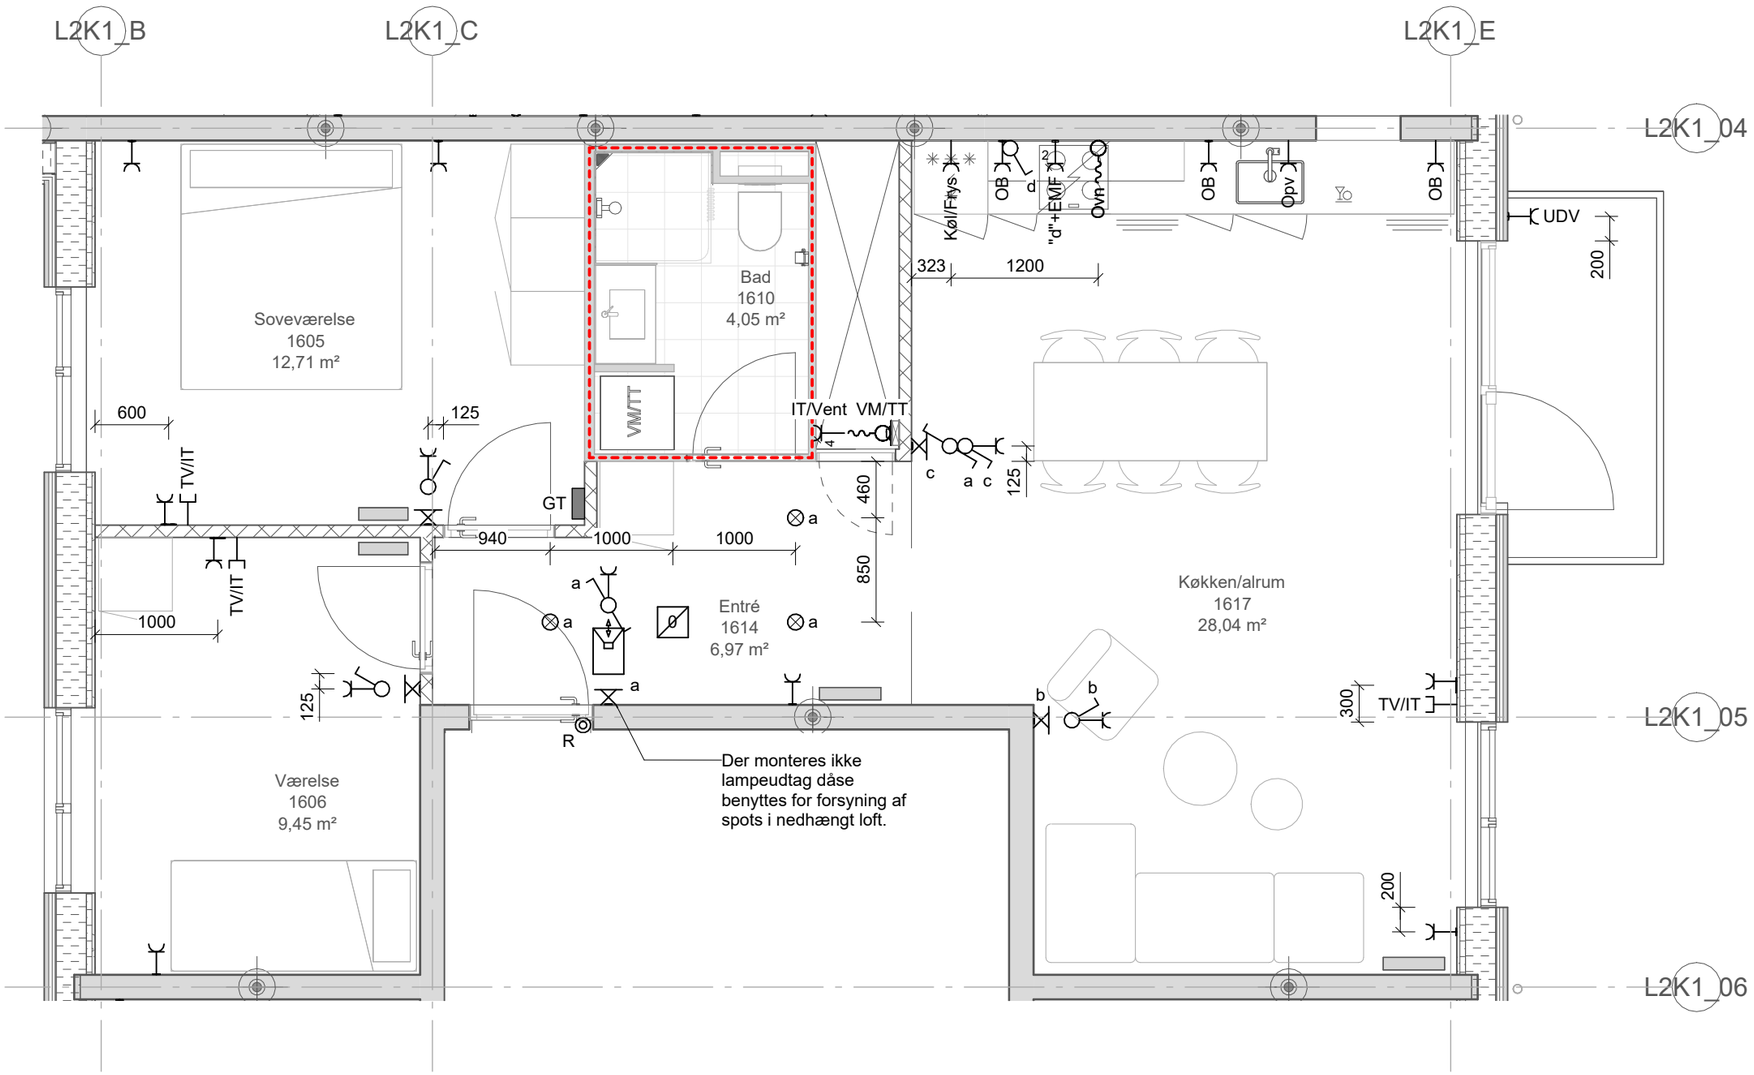

Projekt:	Stejlepladsen				
Tekst:	Elinstallationer - Byg K1 - 1. Sal, Byg B OPG_3V_T02_S - Side K1-9			Tegningsnr.:	Rev.:
			ISP2_K07_L2XX_H04_EXX_N930		
Projektnr.: 1019198	Dato: 2026-02-27	Rev. Dato:		Mål: 1 : 50	Side: K-9
www.arteliagroup.dk	Fil:				

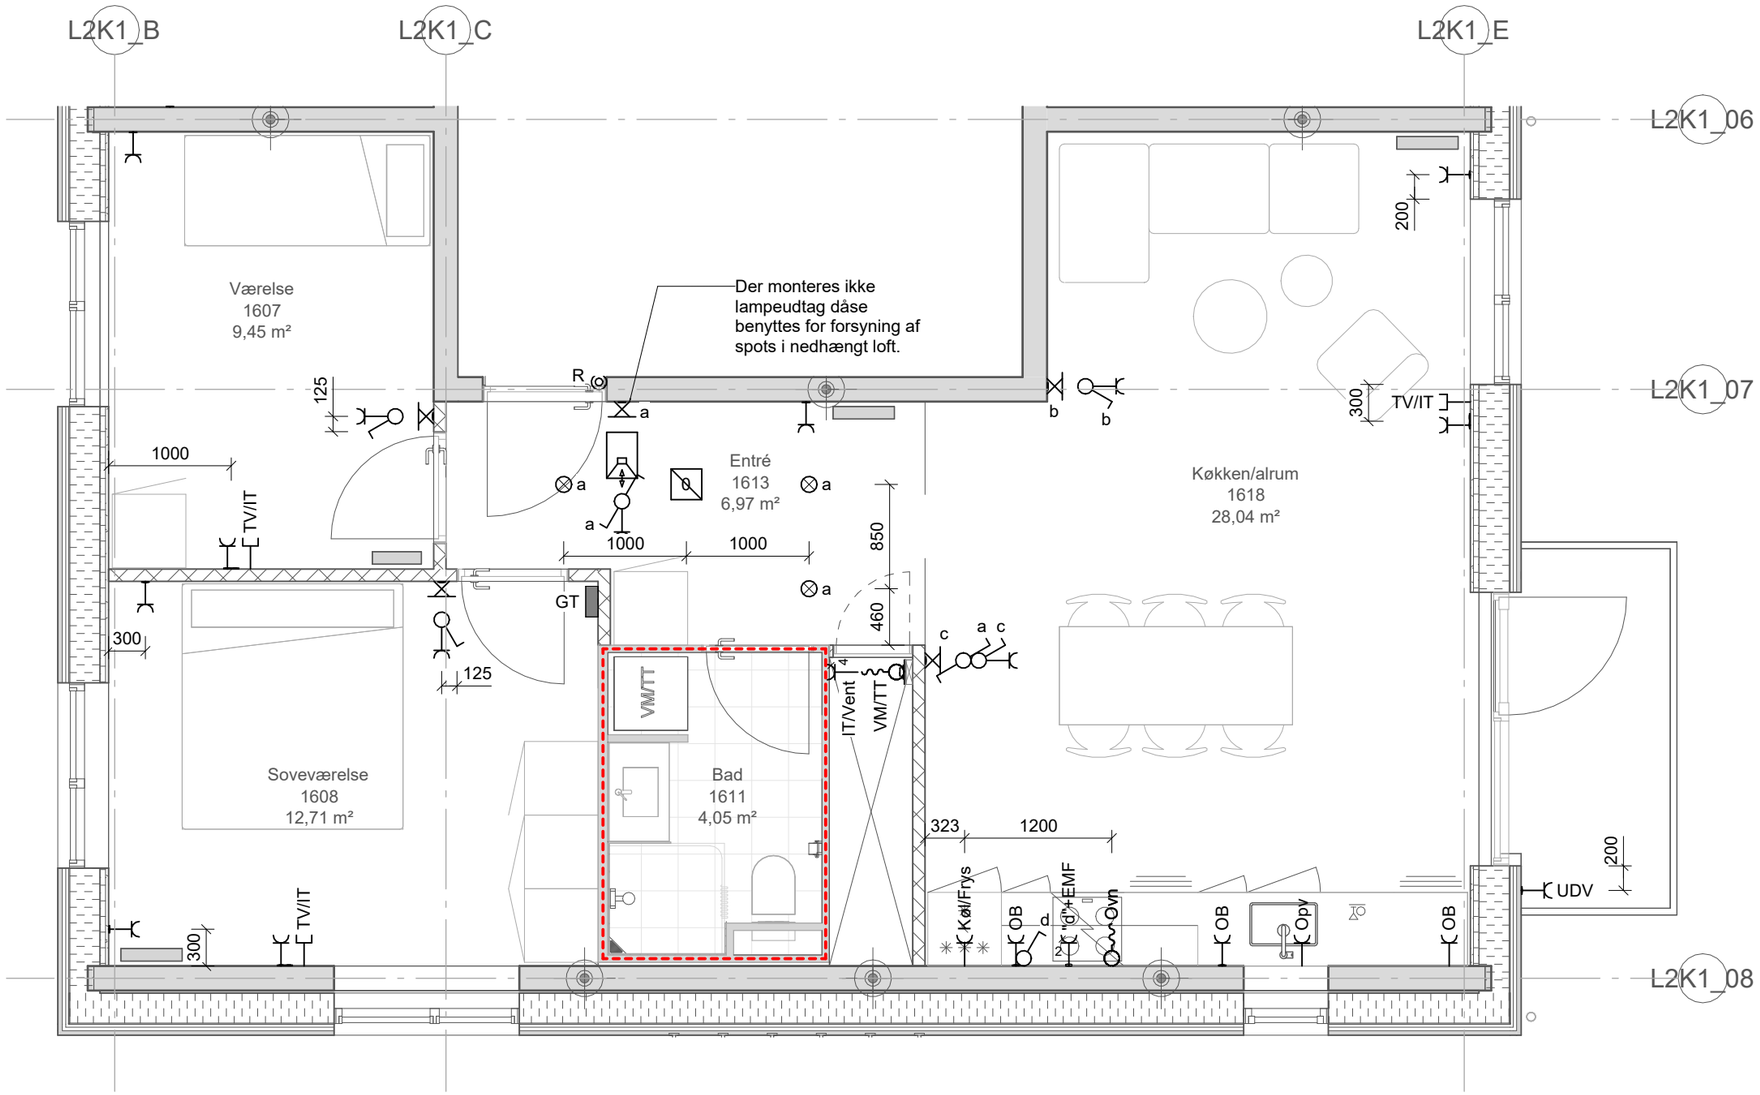

Projekt: Stejlepladsen


Tekst: Elinstallationer -
Byg K1 - 1. Sal, Byg B
OPG_3V_T02 - Side K1-10

Tegningsnr.: ISP2_K07_L2XX_H04_EXX_N930

Rev.:

Projektnr.: 1019198 | Dato: 2026-02-27 | Rev. Dato: | Mål: 1 : 50 | Side: K1-10

www.arteliagroup.dk | Fil:

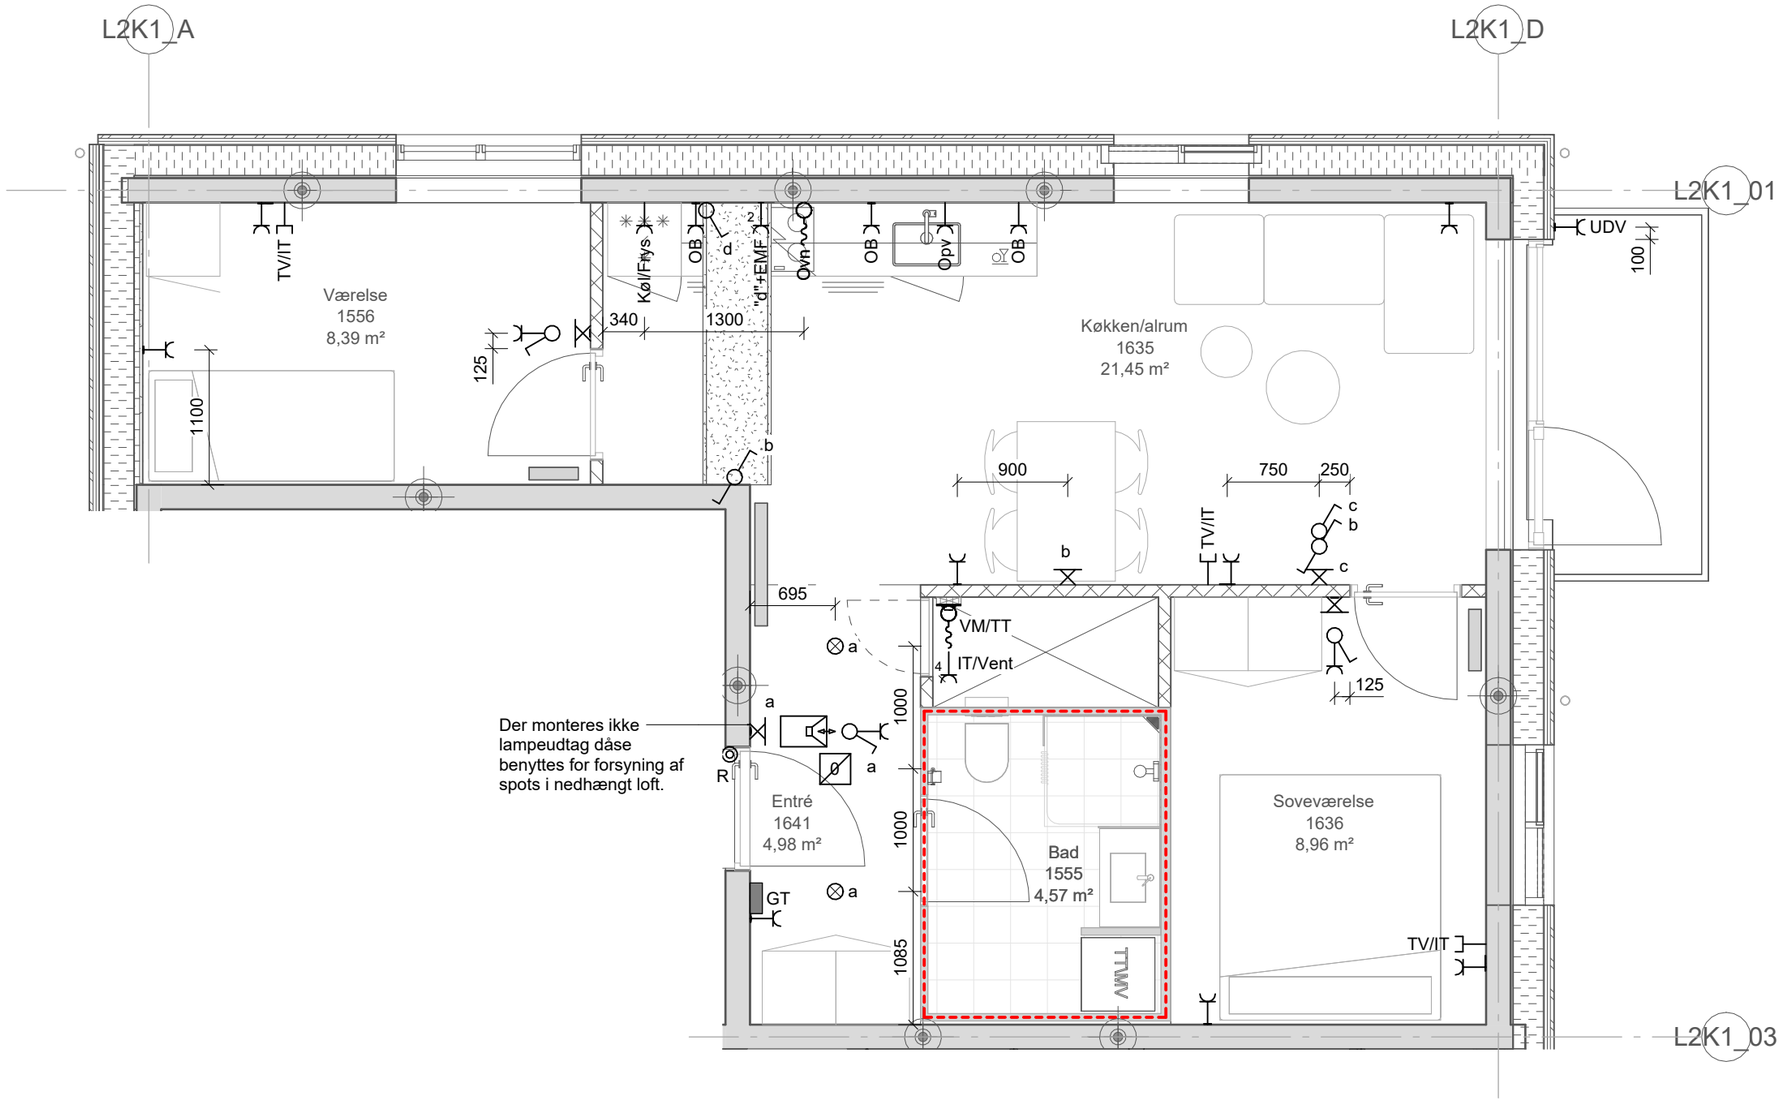

Projekt: Stejlepladsen


Tekst: Elinstallationer -
Byg K1 - 2. Sal, Byg A
OPG_3V_T36 - Side K1-11

Tegningsnr.: ISP2_K07_L2XX_H04_EXX_N930

Rev.:

Projektnr.: 1019198 | Dato: 2026-02-27 | Rev. Dato: | Mål: 1 : 50 | Side: K1-11

www.arteliagroup.dk | Fil:

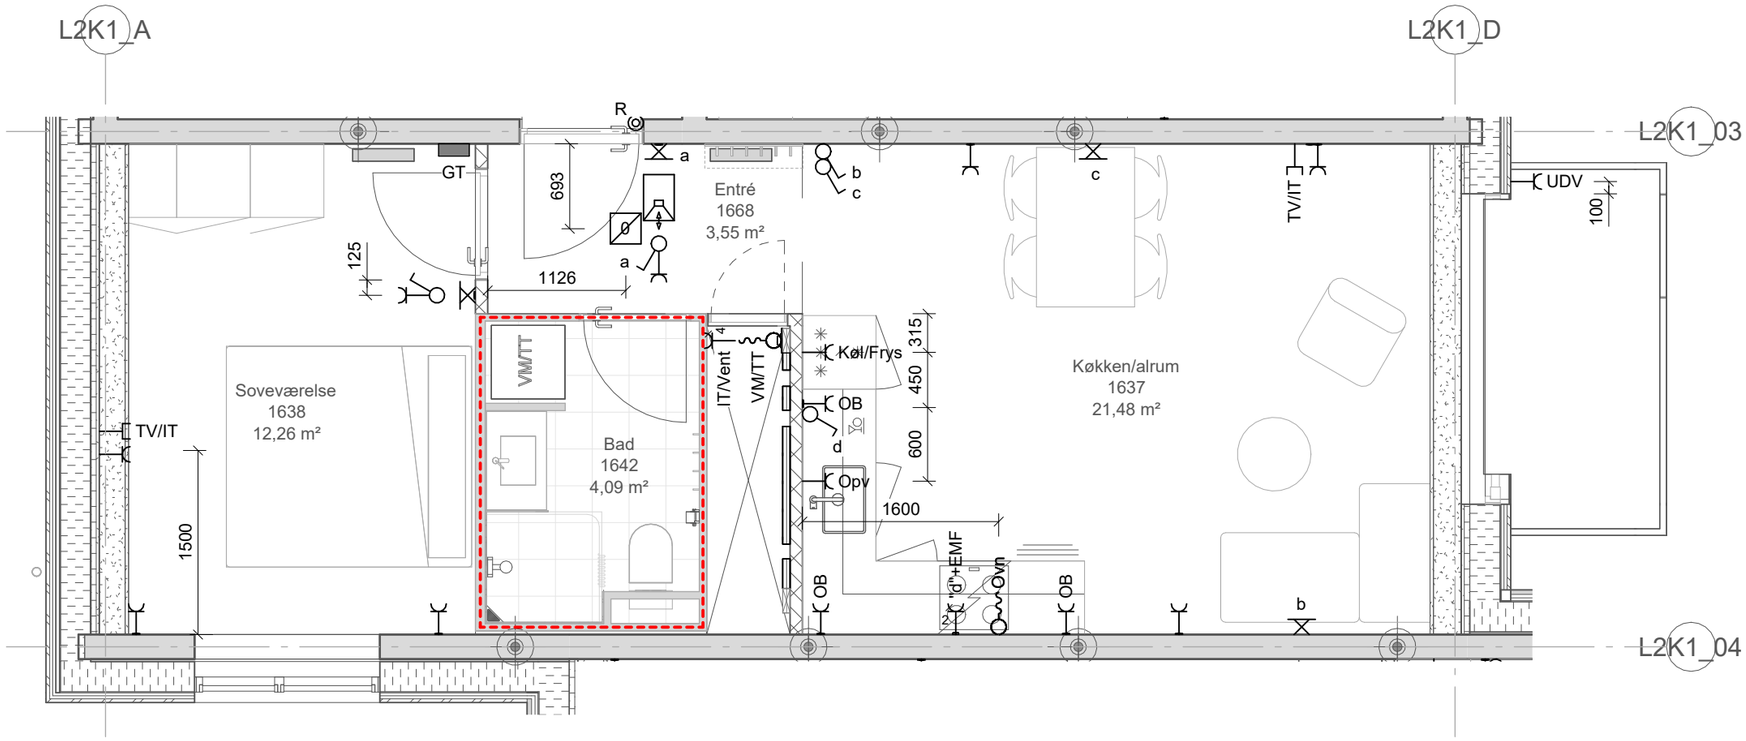

Projekt: Stejlepladsen

ARTELIA


Tekst: Elinstallationer -
Byg K1 - 2. Sal, Byg A
OPG_2V_T31_S - Side K1-12

Tegningsnr.: ISP2_K07_L2XX_H04_EXX_N930


Rev.:

Projektnr.: 1019198 | Dato: 2026-02-27 | Rev. Dato: | Mål: 1 : 50 | Side: K1-12


www.arteliagroup.dk | Fil:

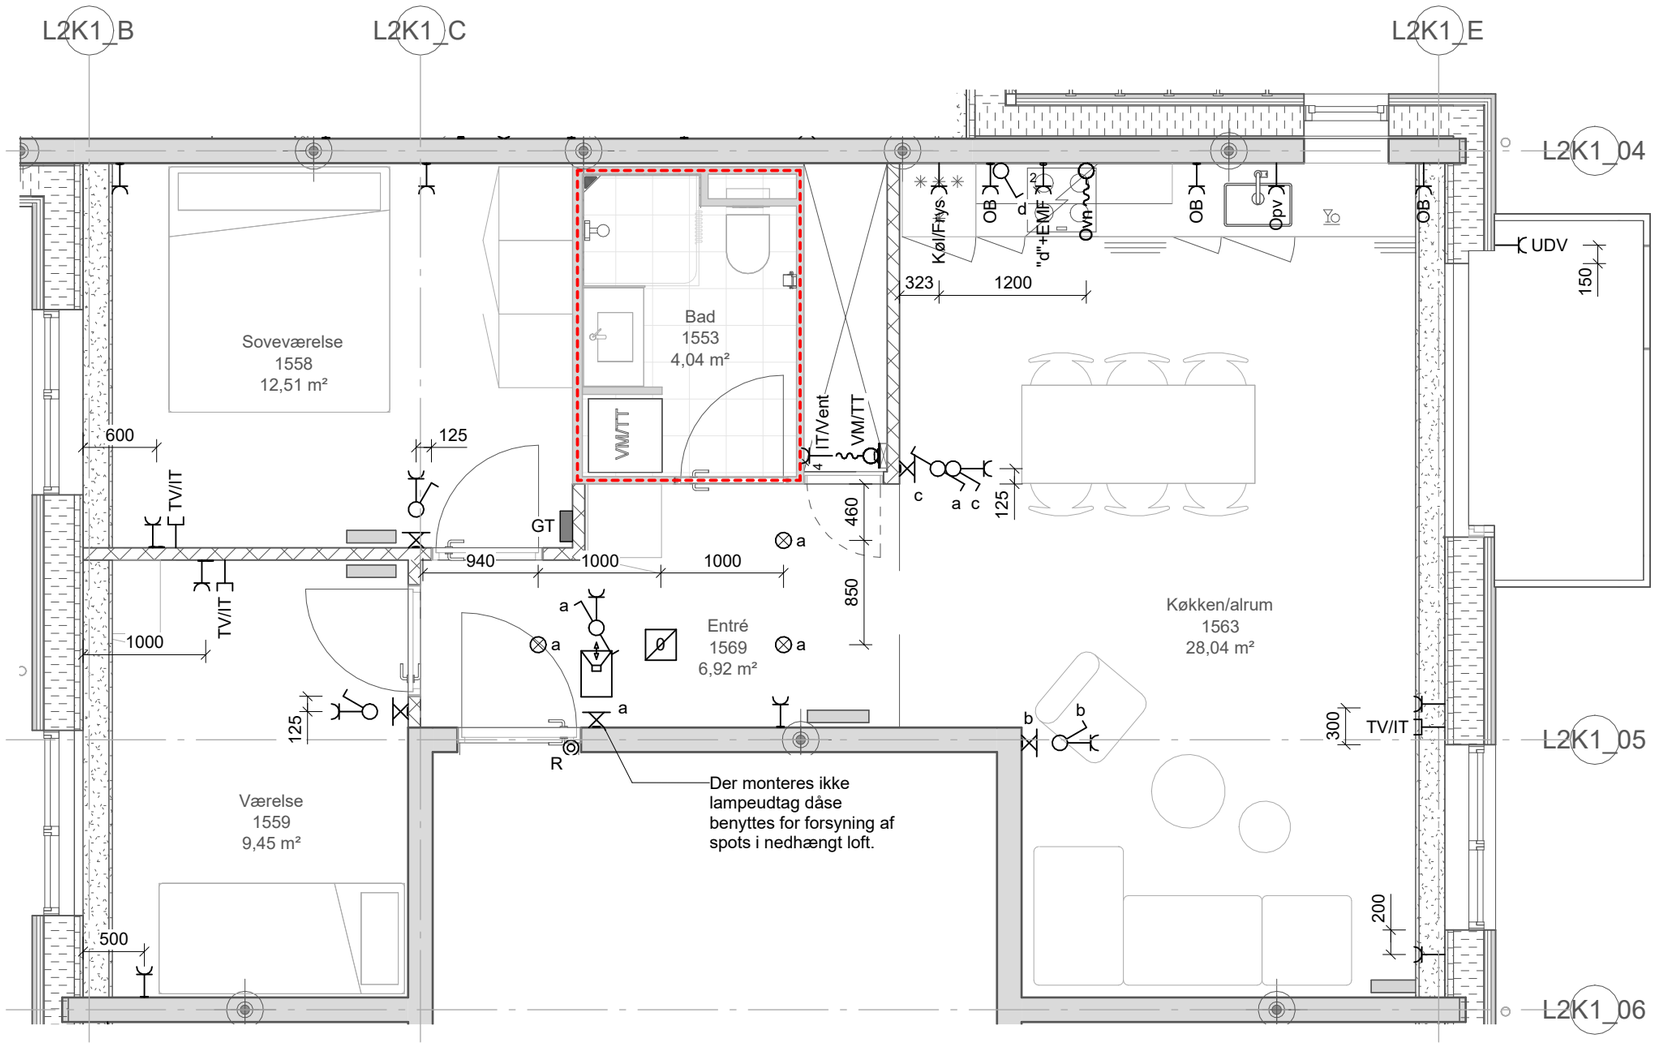

Projekt:	Stejlepladsen				
Tekst:	Elinstallationer - Byg K1 - 2. Sal, Byg B OPG_3V_T02_S - Side K1-13			Tegningsnr.:	Rev.:
				ISP2_K07_L2XX_H04_EXX_N930	
Projektnr.: 1019198	Dato: 2026-02-27	Rev. Dato:		Mål: 1 : 50	Side: K1-13
www.arteliagroup.dk	Fil:				

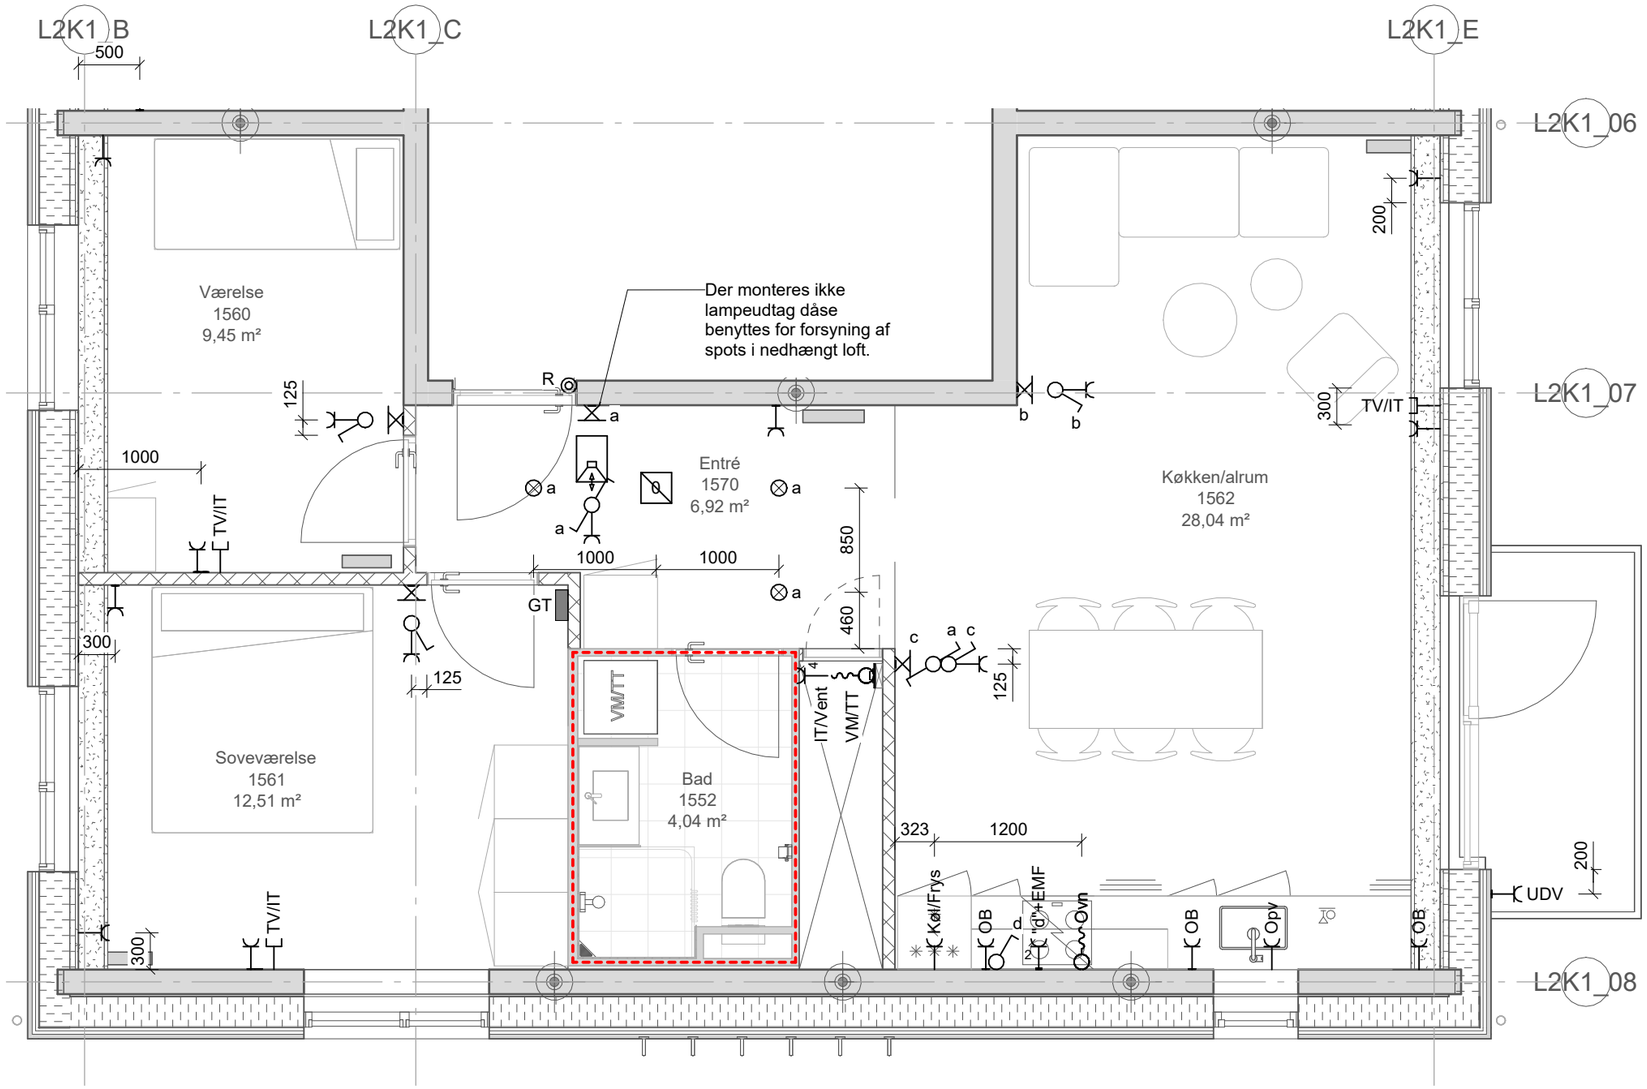

Projekt:	Stejlepladsen				
Tekst:	Elinstallationer - Byg K1 - 2. Sal, Byg B OPG_3V_T02 - Side K1-14			Tegningsnr.:	Rev.:
				ISP2_K07_L2XX_H04_EXX_N930	
Projektnr.: 1019198	Dato: 2026-02-27	Rev. Dato:		Mål: 1 : 50	Side: K1-14
www.arteliagroup.dk	Fil:				

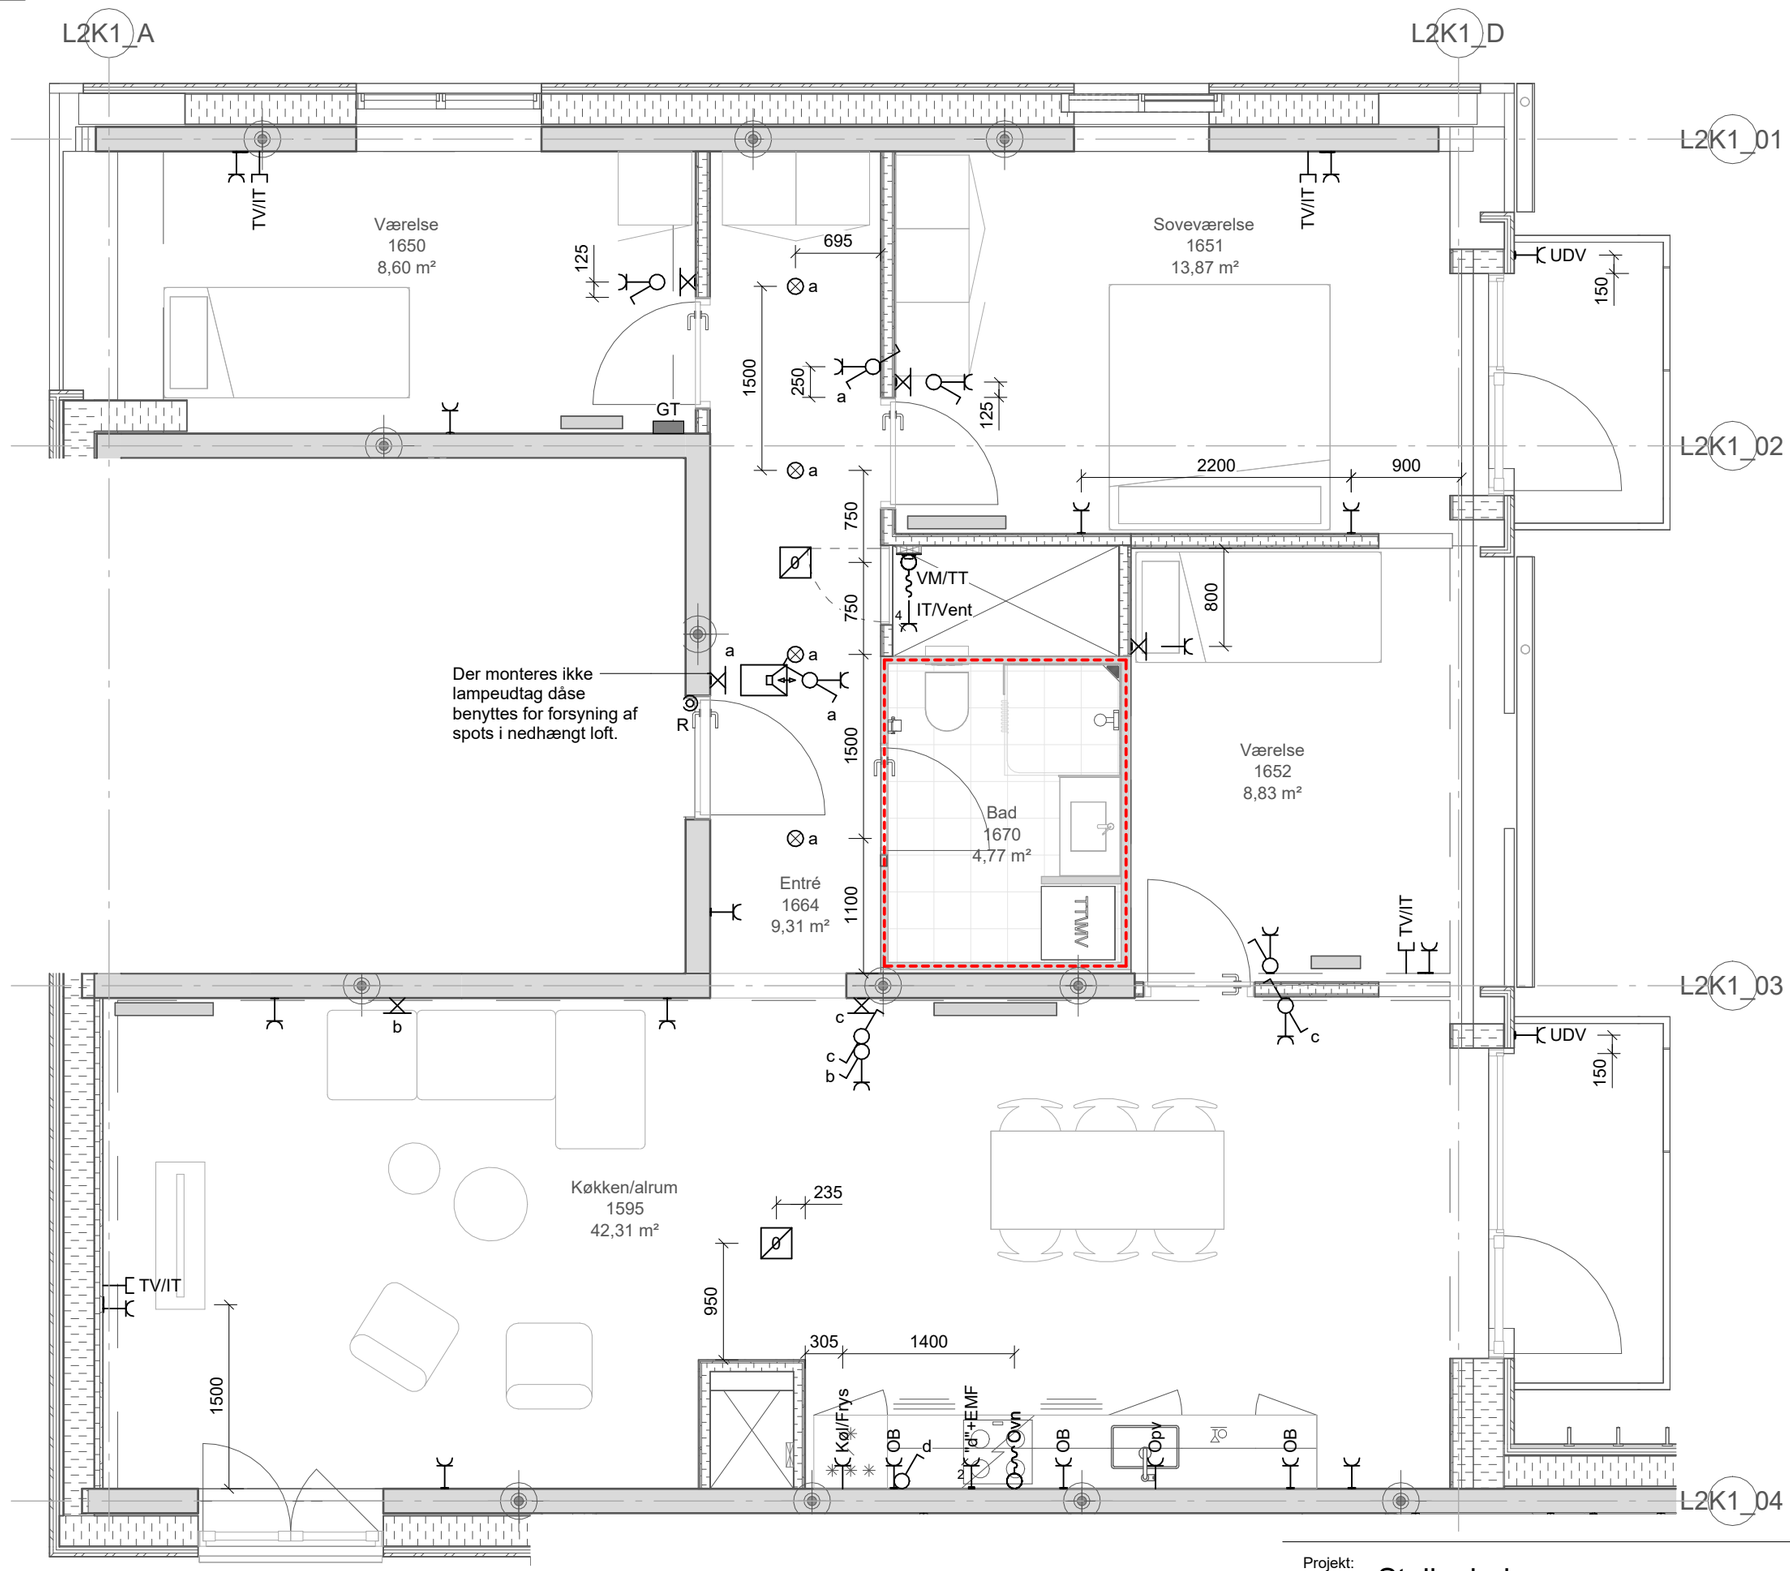

Projekt: Stejlepladsen


Tekst: Elinstallationer -
Byg K1 - 3. Sal, Byg A
OPG_4V_T34_TA - Side K1-15

Tegningsnr.: ISP2_K07_L2XX_H04_EXX_N930

Rev.:

Projektnr.: 1019198 | Dato: 2026-02-27 | Rev. Dato: | Mål: 1 : 50 | Side: K1-15

www.arteliagroup.dk | Fil:

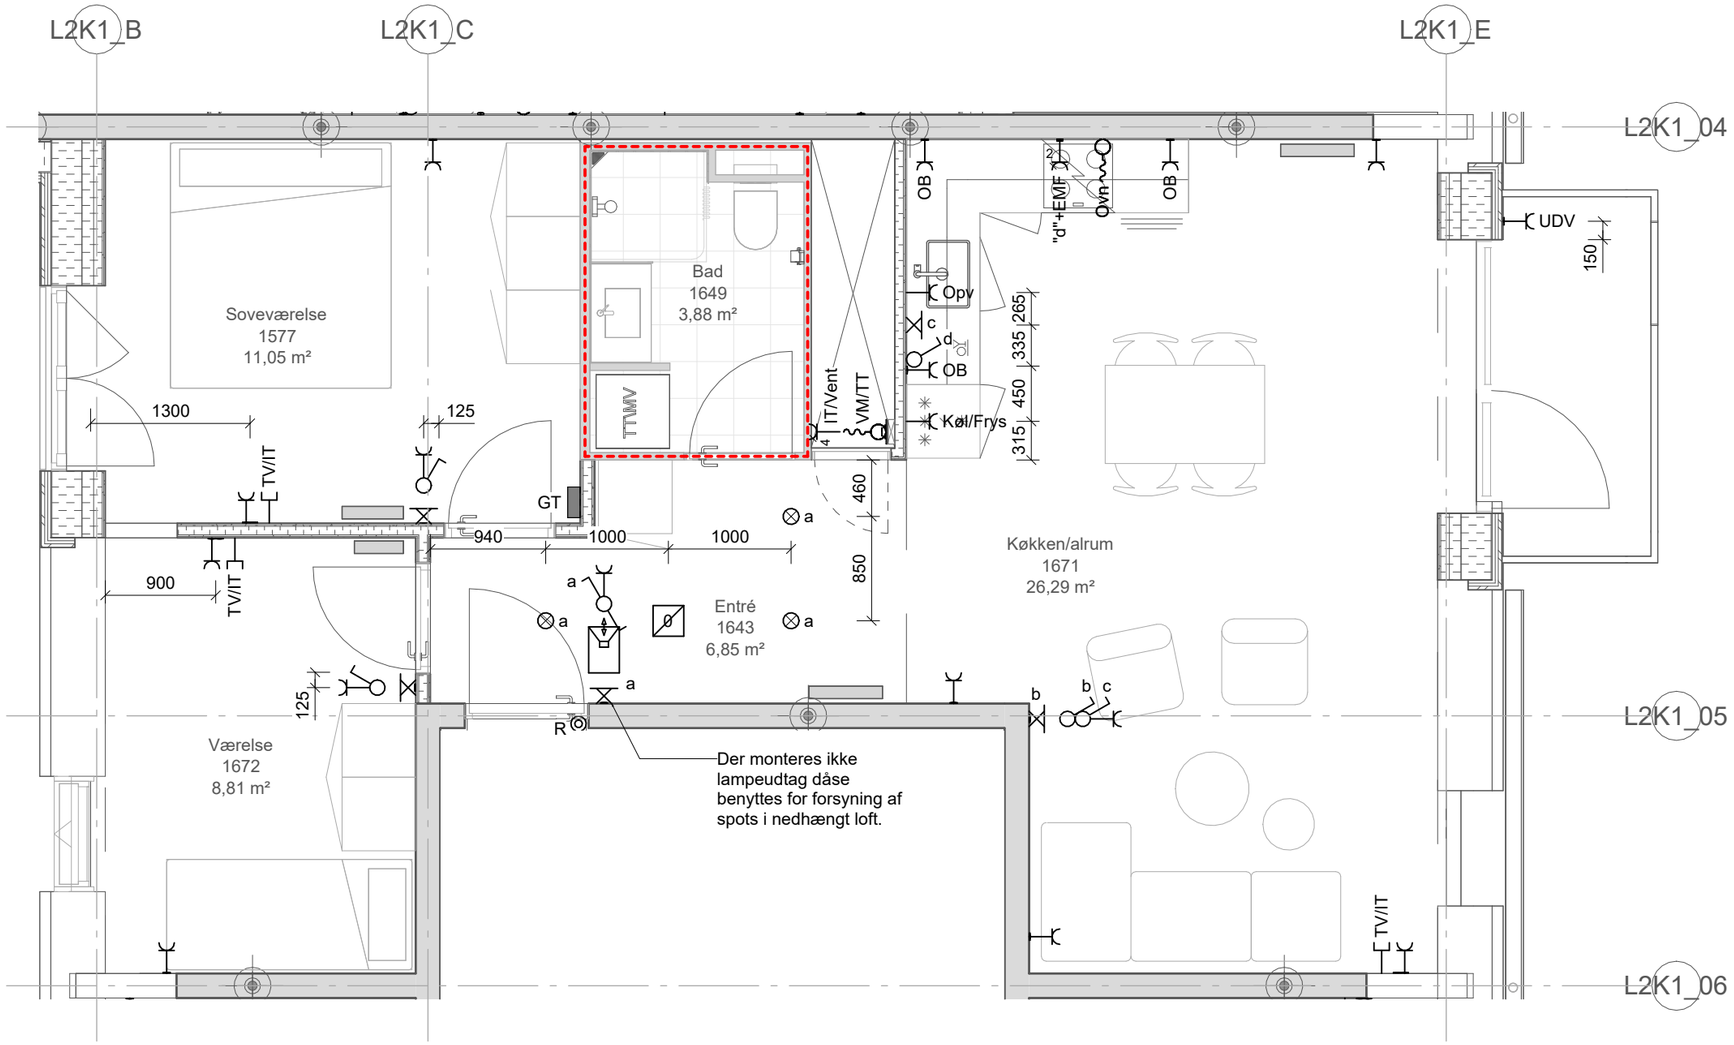

Projekt: Stejlepladsen


Tekst: Elinstallationer -
Byg K1 - 3. Sal, Byg B
OPG_3V_T02_TA_S - Side K1-16

Tegningsnr.: ISP2_K07_L2XX_H04_EXX_N930

Rev.:

Projektnr.: 1019198 | Dato: 2026-02-27 | Rev. Dato: | Mål: 1 : 50 | Side: K1-16

www.arteliagroup.dk | Fil:

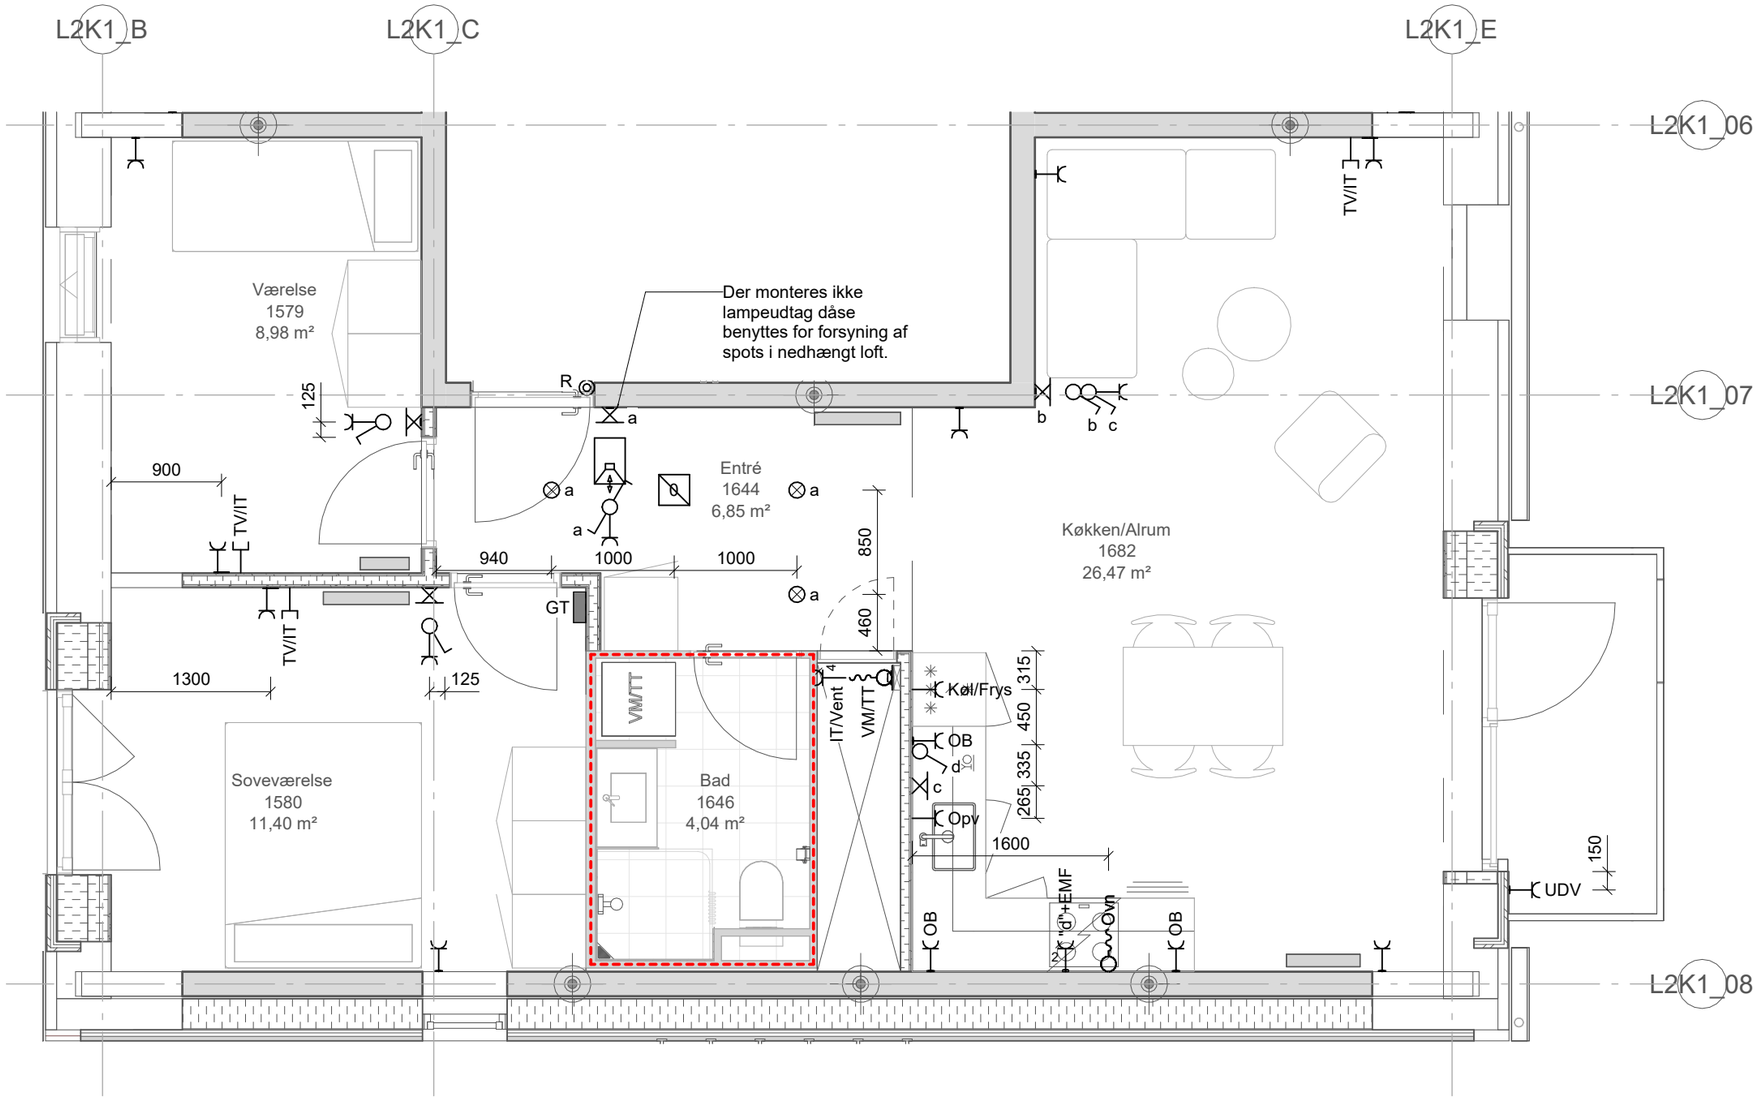

Projekt:	Stejlepladsen				
Tekst:	Elinstallationer - Byg K1 - 3. Sal, Byg B OPG_3V_T02_TA - Side K1-17			Tegningsnr.:	Rev.:
			ISP2_K07_L2XX_H04_EXX_N930		
Projektnr.: 1019198	Dato: 2026-02-27	Rev. Dato:		Mål: 1 : 50	Side: K1-17
www.arteliagroup.dk	Fil:				