Sheet Number	Tekst:	Dato:	Rev.:	Rev. Dato:
ISP2_K07_L2XX_H04_EXX_N930 - Side K3-1	Byg K3 - Index	2026-02-27		
ISP2_K07_L2XX_H04_EXX_N930 - Side K3-2	Byg K3 - Oversigtsplan	2026-02-27		
ISP2_K07_L2XX_H04_EXX_N930 - Side K3-3	Byg K3 - Stueplan	2026-02-27		
ISP2_K07_L2XX_H04_EXX_N930 - Side K3-4	Byg K3 - Stueplan	2026-02-27		
ISP2_K07_L2XX_H04_EXX_N930 - Side K3-5	Byg K3 - Stueplan	2026-02-27		
ISP2_K07_L2XX_H04_EXX_N930 - Side K3-6	Byg K3 - Stueplan	2026-02-27		
ISP2_K07_L2XX_H04_EXX_N930 - Side K3-7	Byg K3 - 1. Sal	2026-02-27		
ISP2_K07_L2XX_H04_EXX_N930 - Side K3-8	Byg K3 - 1. Sal	2026-02-27		
ISP2_K07_L2XX_H04_EXX_N930 - Side K3-9	Byg K3 - 1. Sal	2026-02-27		
ISP2_K07_L2XX_H04_EXX_N930 - Side K3-10	Byg K3 - 1. Sal	2026-02-27		
ISP2_K07_L2XX_H04_EXX_N930 - Side K3-11	Byg K3 - 1. Sal	2026-02-27		
ISP2_K07_L2XX_H04_EXX_N930 - Side K3-12	Byg K3 - 2. Sal	2026-02-27		
ISP2_K07_L2XX_H04_EXX_N930 - Side K3-13	Byg K3 - 2. Sal	2026-02-27		
ISP2_K07_L2XX_H04_EXX_N930 - Side K3-14	Byg K3 - 2. Sal	2026-02-27		
ISP2_K07_L2XX_H04_EXX_N930 - Side K3-15	Byg K3 - 2. Sal	2026-02-27		
ISP2_K07_L2XX_H04_EXX_N930 - Side K3-16	Byg K3 - 2. Sal	2026-02-27		
ISP2_K07_L2XX_H04_EXX_N930 - Side K3-17	Byg K3 - 3. Sal	2026-02-27		
ISP2_K07_L2XX_H04_EXX_N930 - Side K3-18	Byg K3 - 3. Sal	2026-02-27		
ISP2_K07_L2XX_H04_EXX_N930 - Side K3-19	Byg K3 - 3. Sal	2026-02-27		
ISP2_K07_L2XX_H04_EXX_N930 - Side K3-20	Byg K3 - 3. Sal	2026-02-27		
ISP2_K07_L2XX_H04_EXX_N930 - Side K3-21	Byg K3 - 3. Sal	2026-02-27		
ISP2_K07_L2XX_H04_EXX_N930 - Side K3-22	Byg K3 - 4. Sal	2026-02-27		
ISP2_K07_L2XX_H04_EXX_N930 - Side K3-23	Byg K3 - 4. Sal	2026-02-27		
ISP2_K07_L2XX_H04_EXX_N930 - Side K3-24	Byg K3 - 4. Sal	2026-02-27		
ISP2_K07_L2XX_H04_EXX_N930 - Side K3-25	Byg K3 - 4. Sal	2026-02-27		
ISP2_K07_L2XX_H04_EXX_N930 - Side K3-26	Byg K3 - 4. Sal	2026-02-27		

Projekt: Stejlepladsen

Tekst: Elinstallationer - Byg K3 - Index


Tegningsnr.: ISP2_K07_L2XX_H04_EXX_N930

Rev.:

Projektnr.: 1019198 | Dato: 2026-02-27 | Rev. Dato: | Mål: | Side: K3-1

www.arteliagroup.dk | Fil:


Stueplan - Byg K3

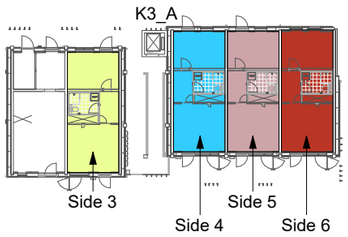


1. sal - Byg K3



2. sal - Byg K3

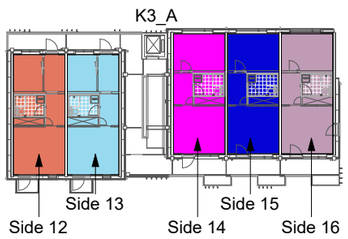

3. sal - Byg K3

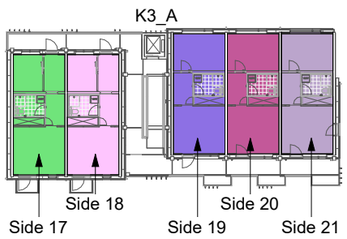

4. sal - Byg K3



Oversigt, bygning K3:

Side 3: Altangangsbolig, st., 2V

Side 4: Altangangsbolig, st., 2V

Side 5: Altangangsbolig, st., 2V

Side 6: Altangangsbolig, st., 2V

Side 7: Altangangsbolig, 1.sal, 2V

Side 8: Altangangsbolig, 1.sal, 2V

Side 9: Altangangsbolig, 1.sal, 2V

Side 10: Altangangsbolig, 1.sal, 2V

Side 11: Altangangsbolig, 1.sal, 2V

Side 12: Altangangsbolig, 2.sal, 2V

Side 13: Altangangsbolig, 2.sal, 2V

Side 14: Altangangsbolig, 2.sal, 2V

Side 15: Altangangsbolig, 2.sal, 2V

Side 16: Altangangsbolig, 2.sal, 2V

Side 17: Altangangsbolig, 3.sal, 2V

Side 18: Altangangsbolig, 3.sal, 2V

Side 19: Altangangsbolig, 3.sal, 2V

Side 20: Altangangsbolig, 3.sal, 2V

Side 21: Altangangsbolig, 3.sal, 2V

Side 22: Altangangsbolig, 4.sal, 2V

Side 23: Altangangsbolig, 4.sal, 2V

Side 24: Altangangsbolig, 4.sal, 2V

Side 25: Altangangsbolig, 4.sal, 2V

Side 26: Altangangsbolig, 4.sal, 2V

Projekt: Stejlepladsen


Tekst: Elinstallationer -
Byg K3 - Oversigtsplan

Tegningsnr.: ISP2_K07_L2XX_H04_EXX_N930

Rev.:

Projektnr.: 1019198 | Dato: 2026-02-27 | Rev. Dato: | Mål: 1 : 500 | Side: K3-2

www.arteliagroup.dk | Fil:

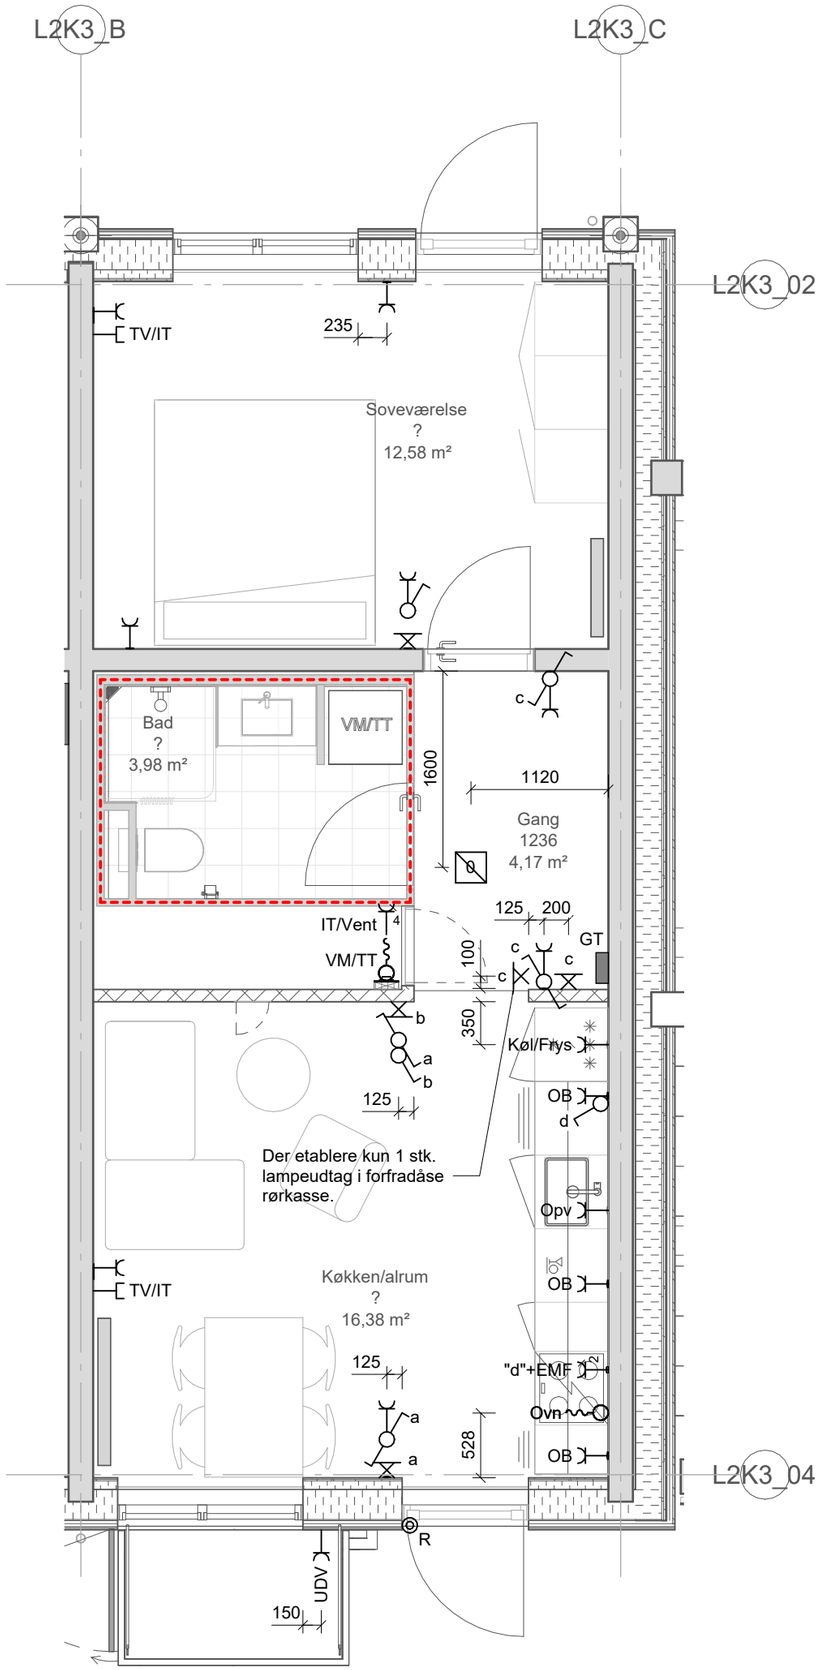

Projekt: Stejlepladsen

ARTELIA


Tekst: Elinstallationer -
Byg K3 - Stueplan
ALT_2V_T01_ST_S - Side K3-3

Tegningsnr.: ISP2_K07_L2XX_H04_EXX_N930

Rev.:

Projektnr.: 1019198 | Dato: 2026-02-27 | Rev. Dato: | Mål: 1 : 50 | Side: K3-3

www.arteliagroup.dk | Fil:

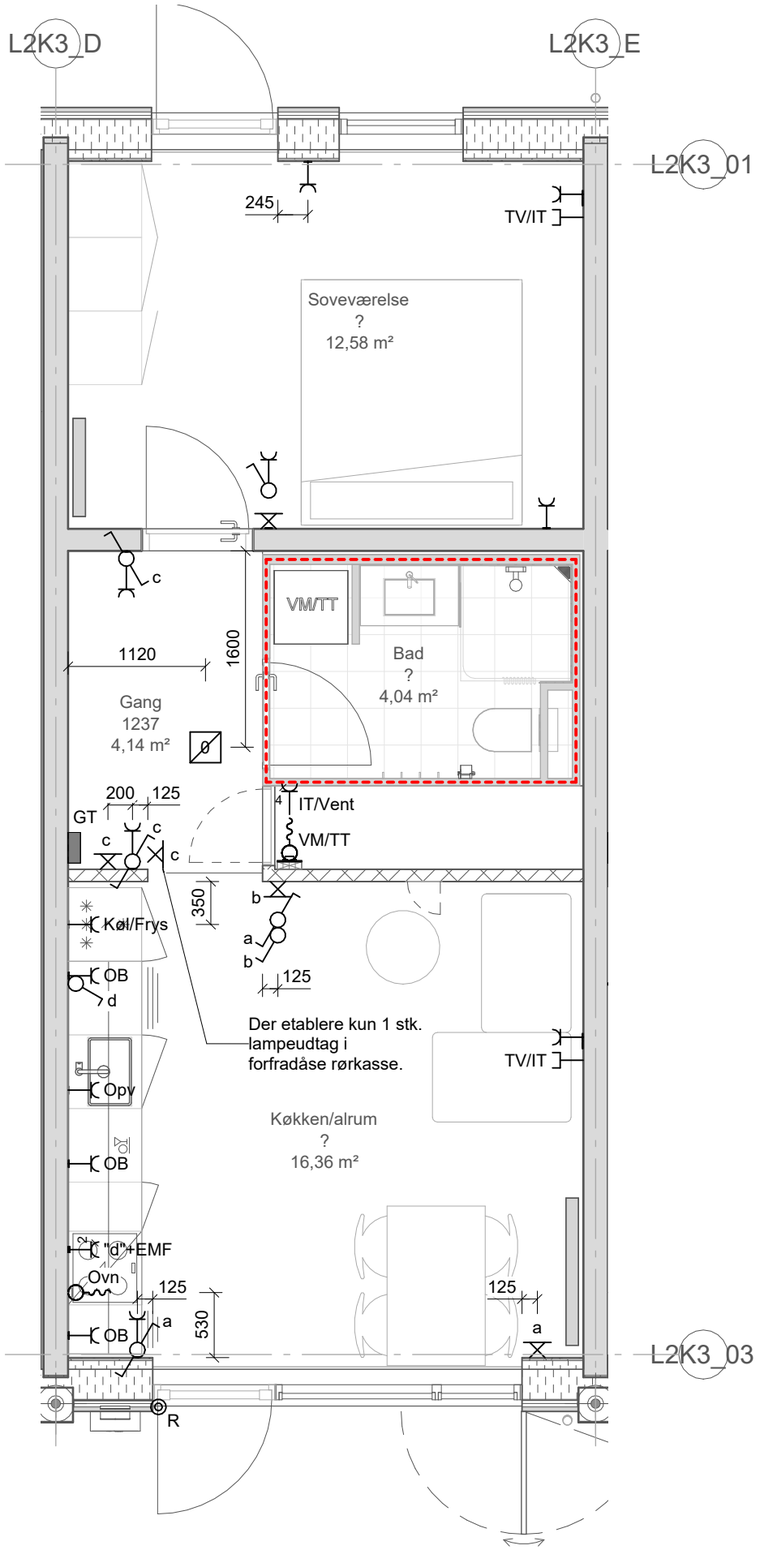

Projekt: Stejlepladsen


Tekst: Elinstallationer -
Byg K3 - Stueplan
ALT_2V_T01_ST - Side K3-4

Tegningsnr.: ISP2_K07_L2XX_H04_EXX_N930

Rev.:

Projektnr.: 1019198 | Dato: 2026-02-27 | Rev. Dato: | Mål: 1 : 50 | Side: K3-4

www.arteliagroup.dk | Fil:

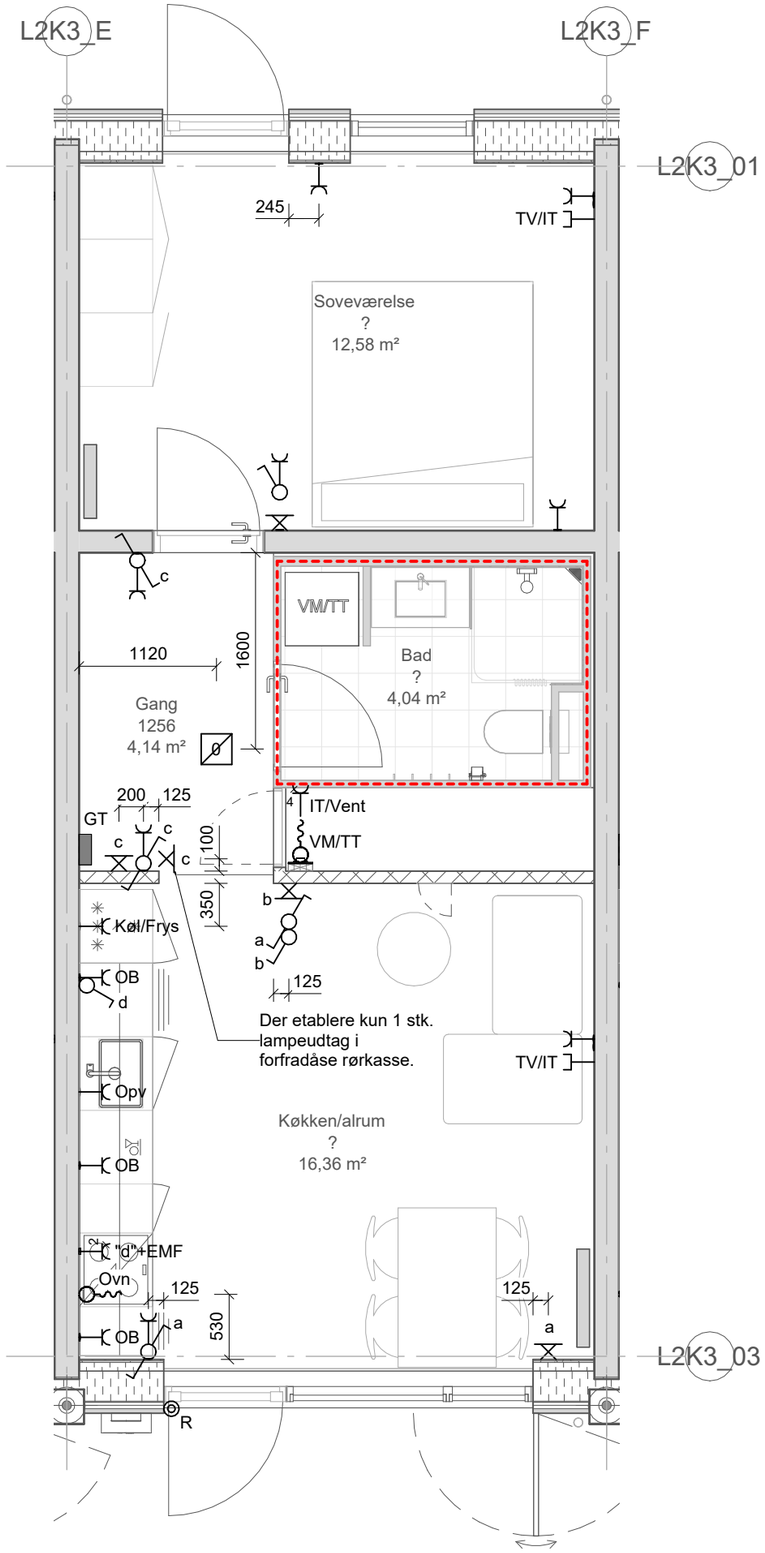

Projekt: Stejlepladsen


Tekst: Elinstallationer -
Byg K3 - Stueplan
ALT_2V_T01_ST - Side K3-5

Tegningsnr.: ISP2_K07_L2XX_H04_EXX_N930

Rev.:

Projektnr.: 1019198 | Dato: 2026-02-27 | Rev. Dato: | Mål: 1 : 50 | Side: K3-5

www.arteliagroup.dk | Fil:

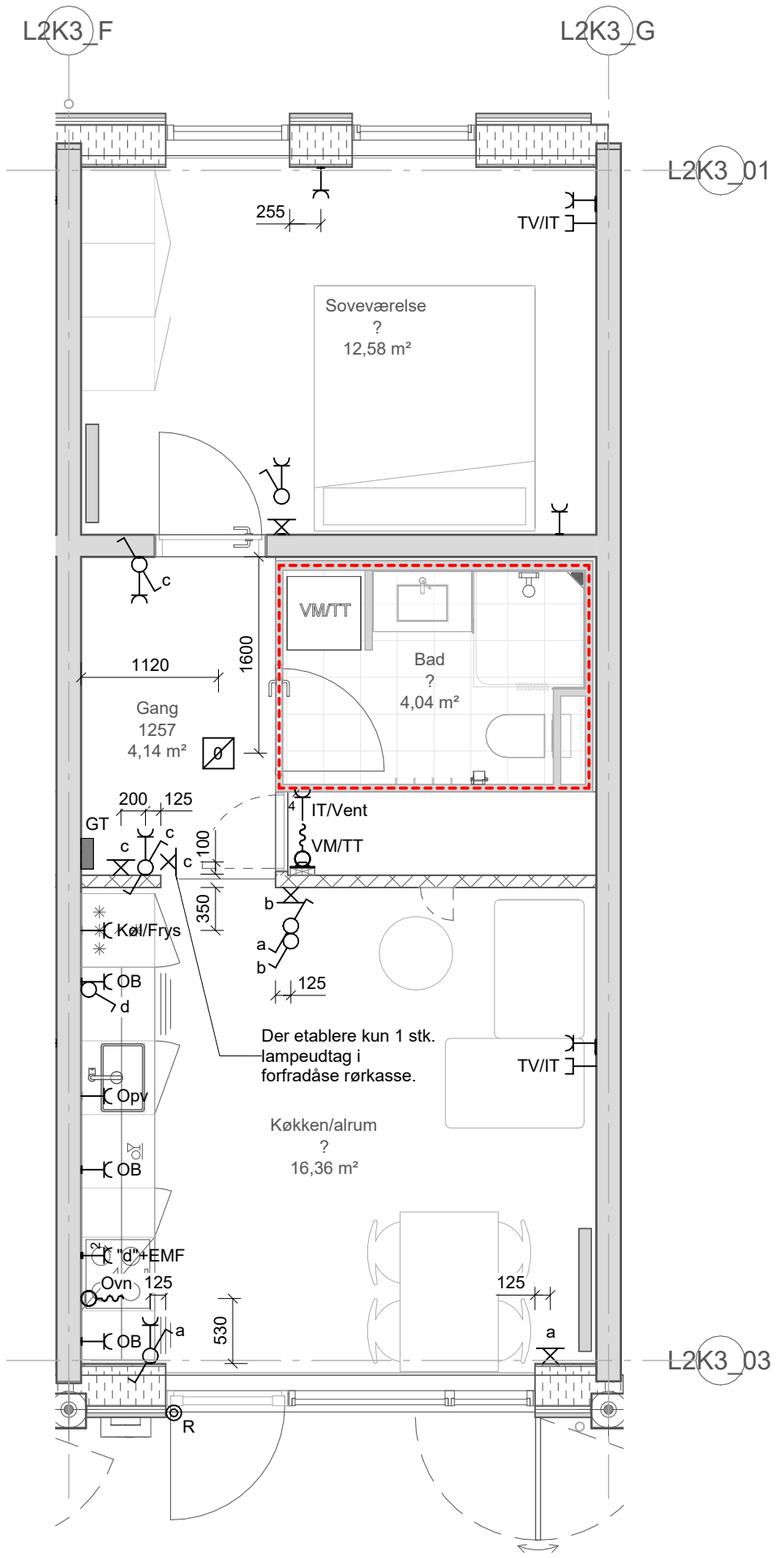

Projekt: Stejlepladsen


Tekst: Elinstallationer -
Byg K3 - Stueplan
ALT_2V_T01_ST - Side K3-6

Tegningsnr.: ISP2_K07_L2XX_H04_EXX_N930

Rev.:

Projektnr.: 1019198 | Dato: 2026-02-27 | Rev. Dato: | Mål: 1 : 50 | Side: K3-6

www.arteliagroup.dk | Fil:

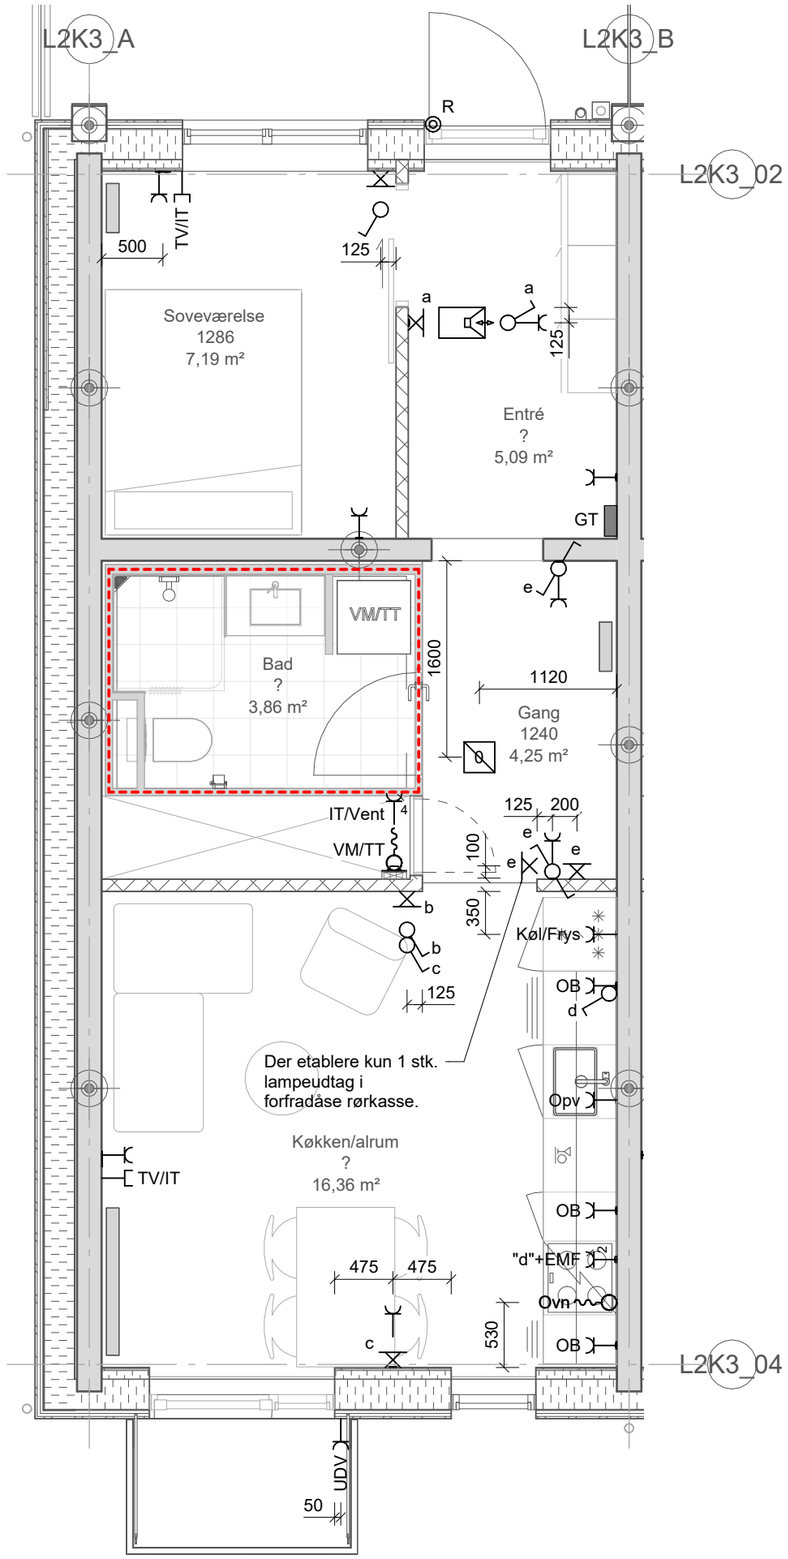

Projekt: Stejlepladsen


Tekst: Elinstallationer -
Byg K3 - 1. Sal
ALT_2V_T01_S - Side K3-7

Tegningsnr.: ISP2_K07_L2XX_H04_EXX_N930

Rev.:

Projektnr.: 1019198 | Dato: 2026-02-27 | Rev. Dato: | Mål: 1 : 50 | Side: K3-7

www.arteliagroup.dk | Fil:

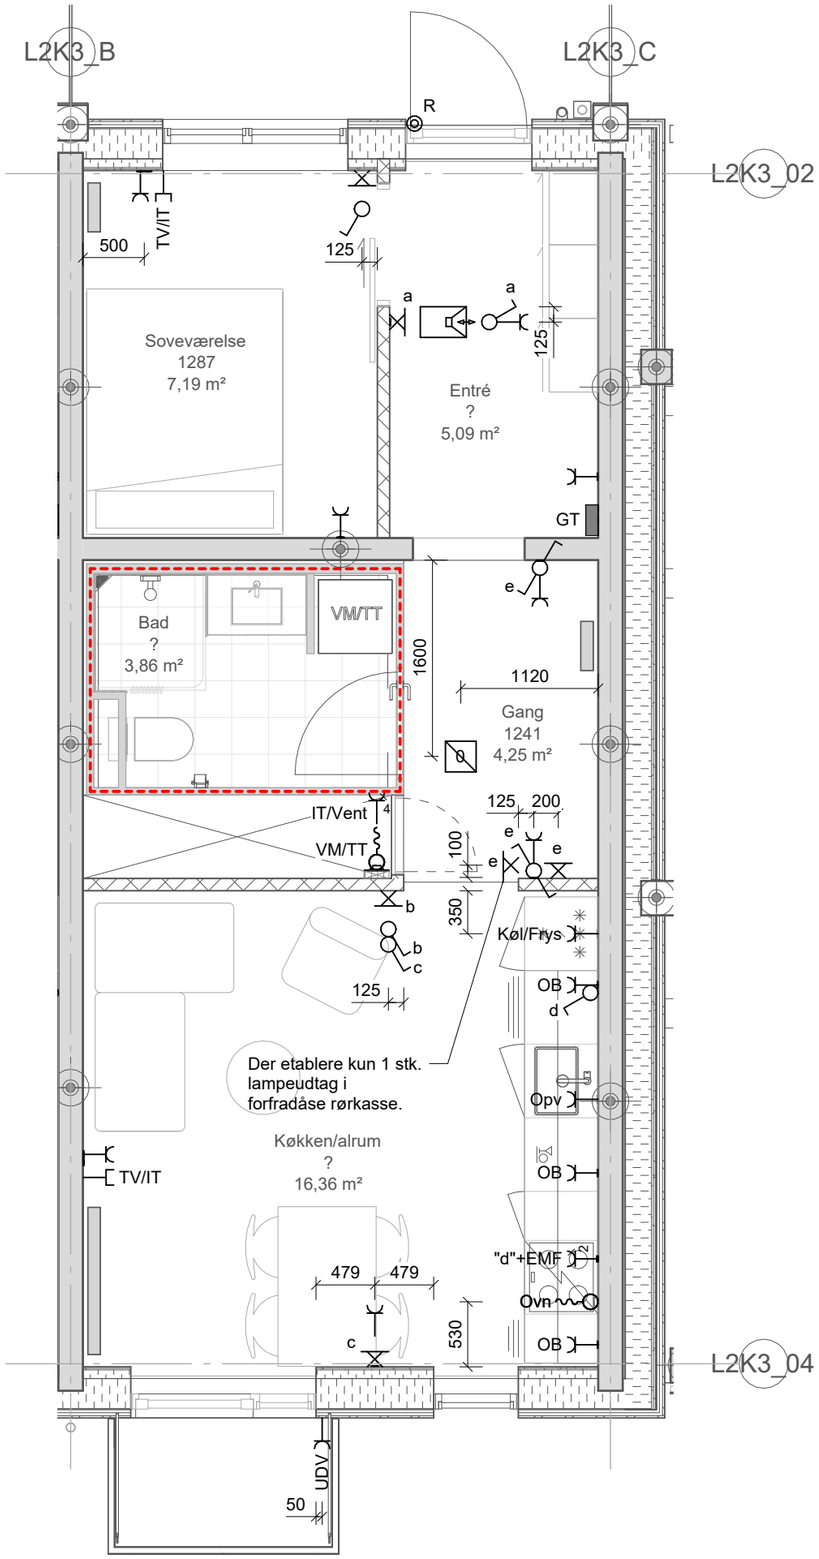

Projekt: Stejlepladsen


Tekst: Elinstallationer -
Byg K3 - 1. Sal
ALT_2V_T01_S - Side K3-8

Tegningsnr.: ISP2_K07_L2XX_H04_EXX_N930

Rev.:

Projektnr.: 1019198 | Dato: 2026-02-27 | Rev. Dato: | Mål: 1 : 50 | Side: K3-8

www.arteliagroup.dk | Fil:

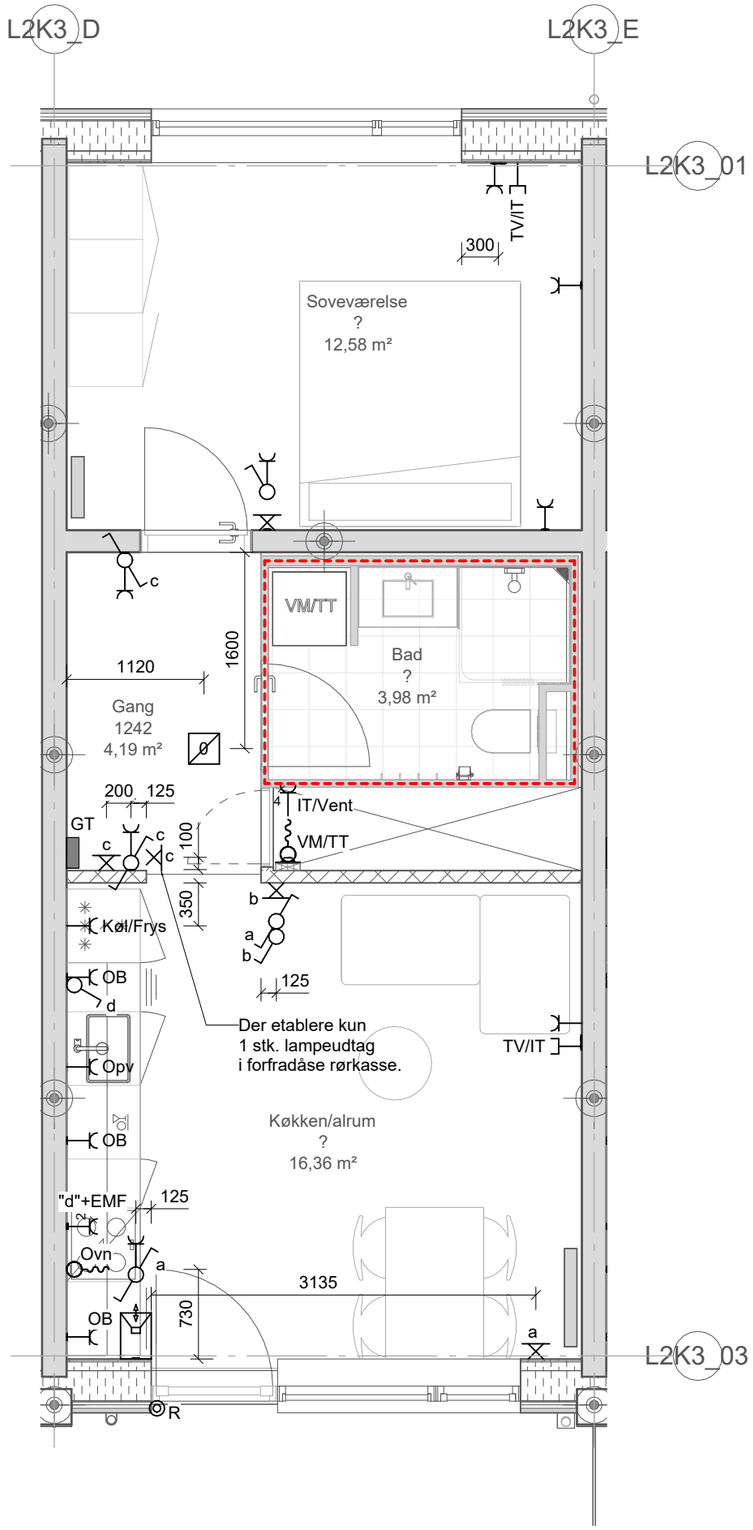

Projekt: Stejlepladsen

ARTELIA


Tekst: Elinstallationer -
Byg K3 - 1. Sal
ALT_2V_T01 - Side K3-9

Tegningsnr.: ISP2_K07_L2XX_H04_EXX_N930

Rev.:

Projektnr.: 1019198 | Dato: 2026-02-27 | Rev. Dato: | Mål: 1 : 50 | Side: K3-9

www.arteliagroup.dk | Fil:

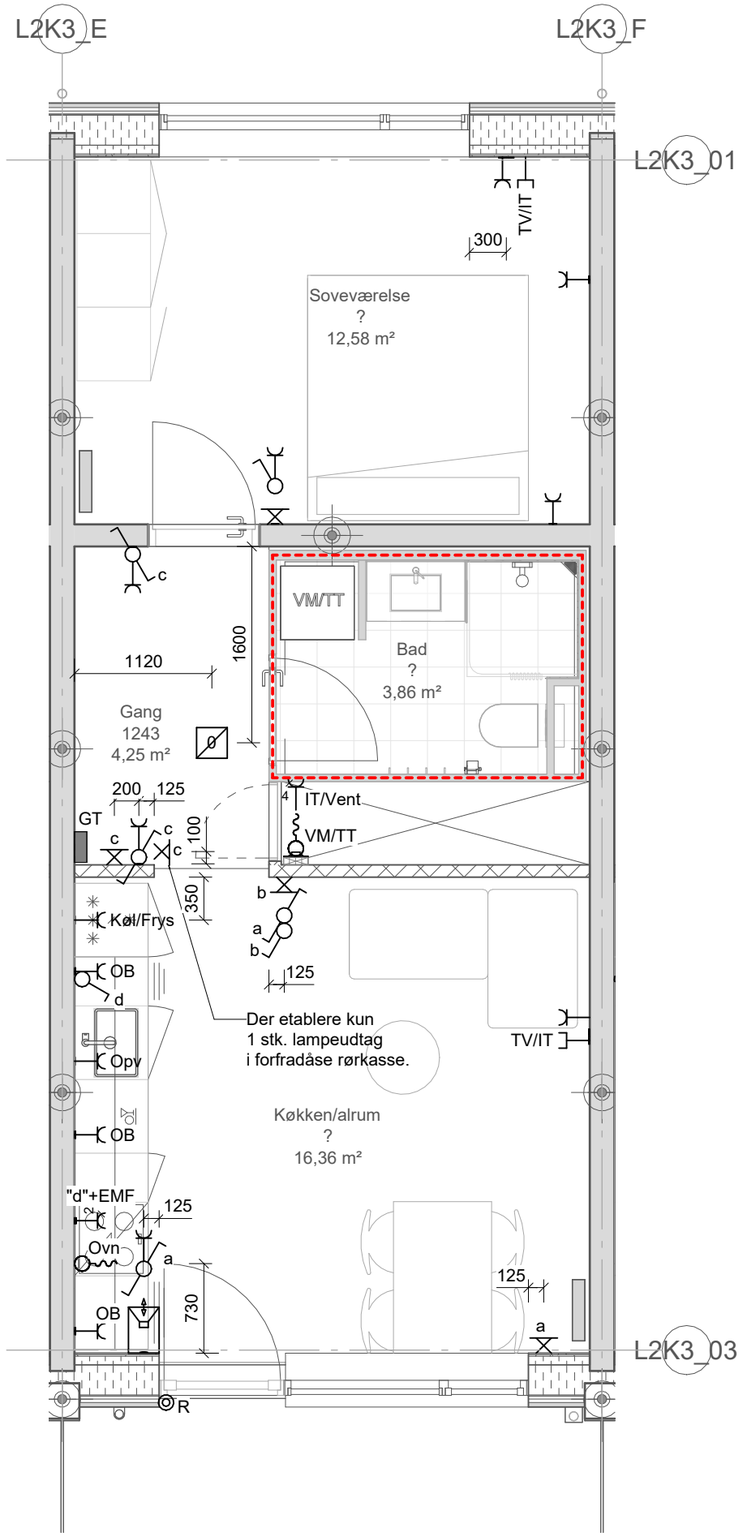

Projekt: Stejlepladsen

ARTELIA


Tekst: Elinstallationer -
Byg K3 - 1. Sal
ALT_2V_T01 - Side K3-10

Tegningsnr.: ISP2_K07_L2XX_H04_EXX_N930

Rev.:

Projektnr.: 1019198 | Dato: 2026-02-27 | Rev. Dato: | Mål: 1 : 50 | Side: K3-10

www.arteliagroup.dk | Fil:

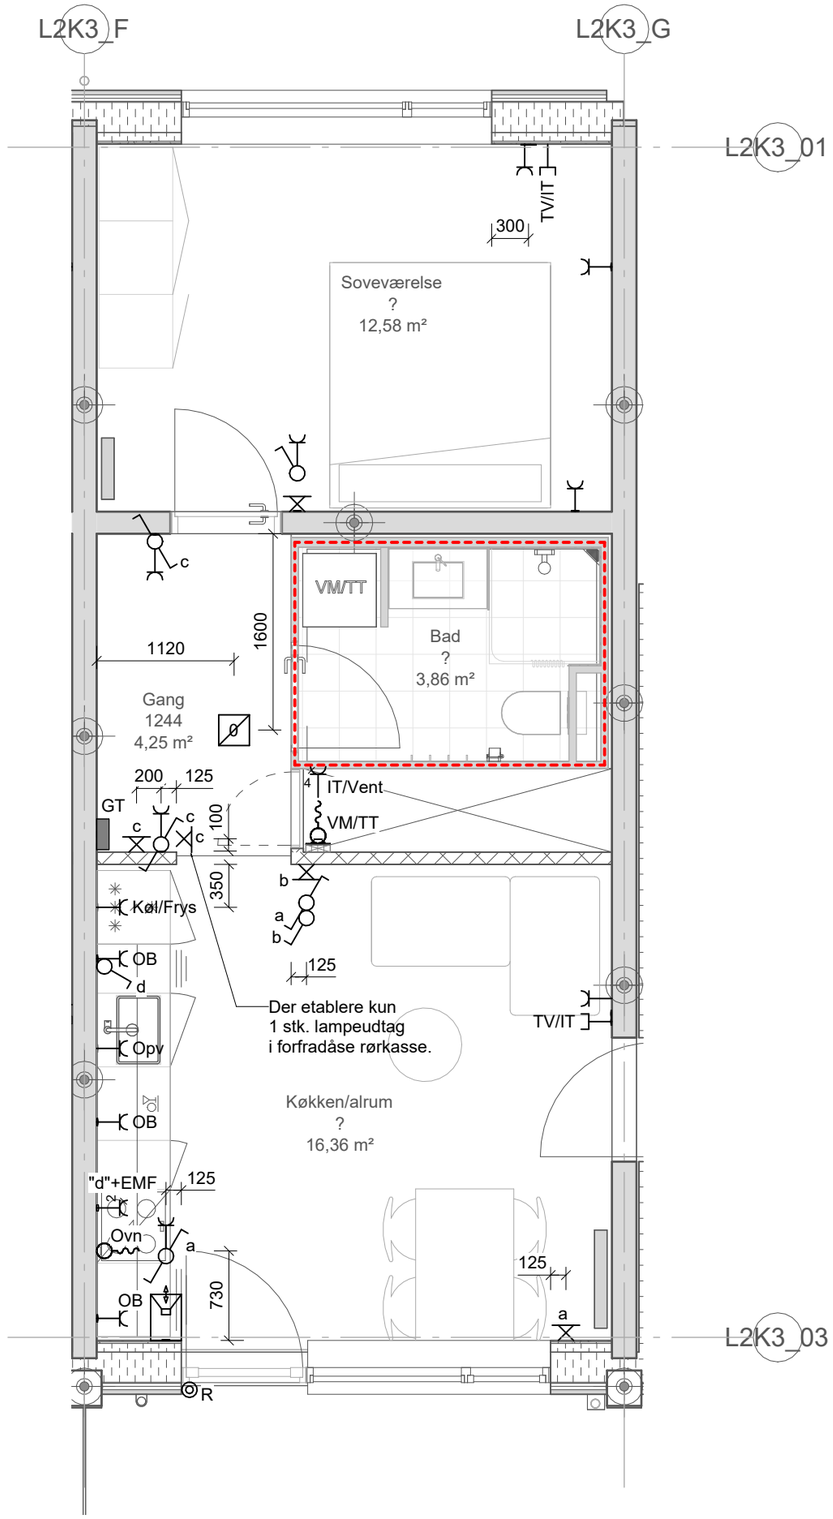

Projekt: Stejlepladsen


Tekst: Elinstallationer -
Byg K3 - 1. Sal
ALT_2V_T01 - Side K3-11

Tegningsnr.: ISP2_K07_L2XX_H04_EXX_N930

Rev.:

Projektnr.: 1019198 | Dato: 2026-02-27 | Rev. Dato: | Mål: 1 : 50 | Side: K3-11

www.arteliagroup.dk | Fil:

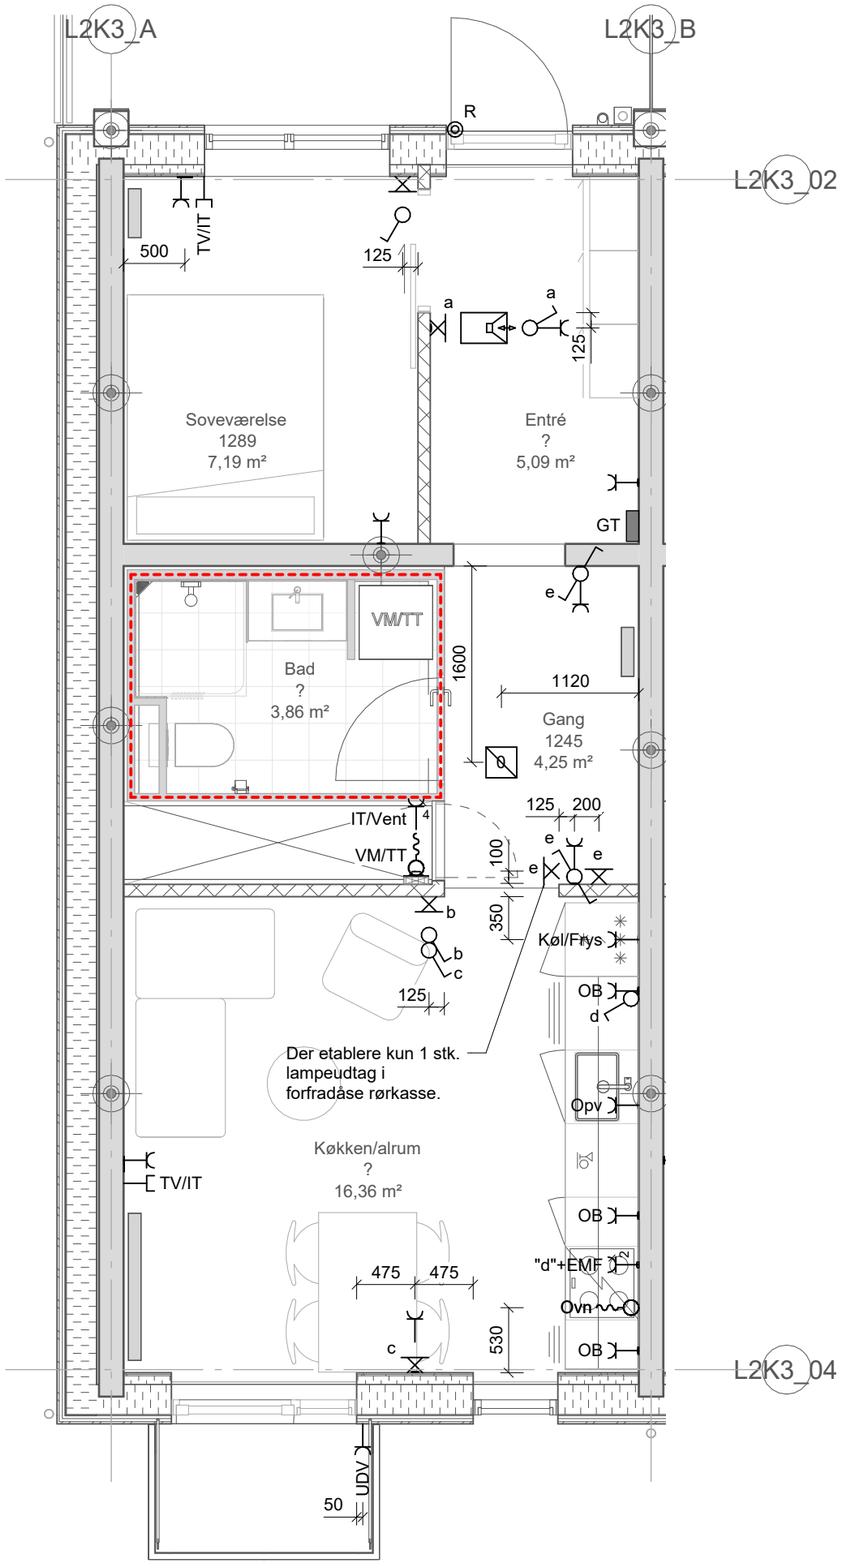

Projekt: Stejlepladsen


Tekst: Elinstallationer -
Byg K3 - 2. Sal
ALT_2V_T01_S - Side K3-12

Tegningsnr.: ISP2_K07_L2XX_H04_EXX_N930

Rev.:

Projektnr.: 1019198 | Dato: 2026-02-27 | Rev. Dato: | Mål: 1 : 50 | Side: K3-12

www.arteliagroup.dk | Fil:

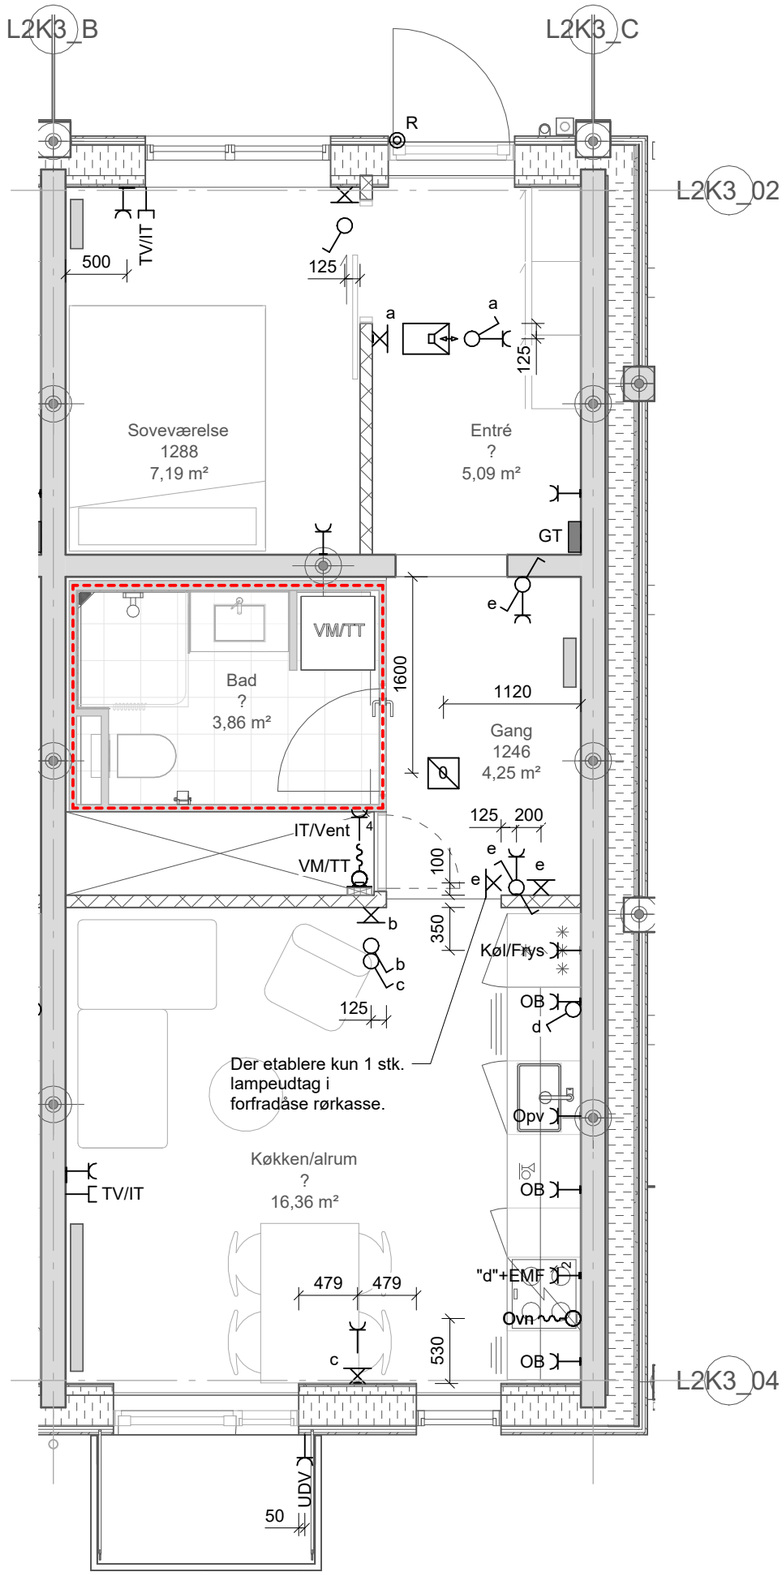

Projekt: Stejlepladsen


Tekst: Elinstallationer -
Byg K3 - 2. Sal
ALT_2V_T01_S - Side K3-13

Tegningsnr.: ISP2_K07_L2XX_H04_EXX_N930

Rev.:

Projektnr.: 1019198 | Dato: 2026-02-27 | Rev. Dato: | Mål: 1 : 50 | Side: K3-13

www.arteliagroup.dk | Fil:

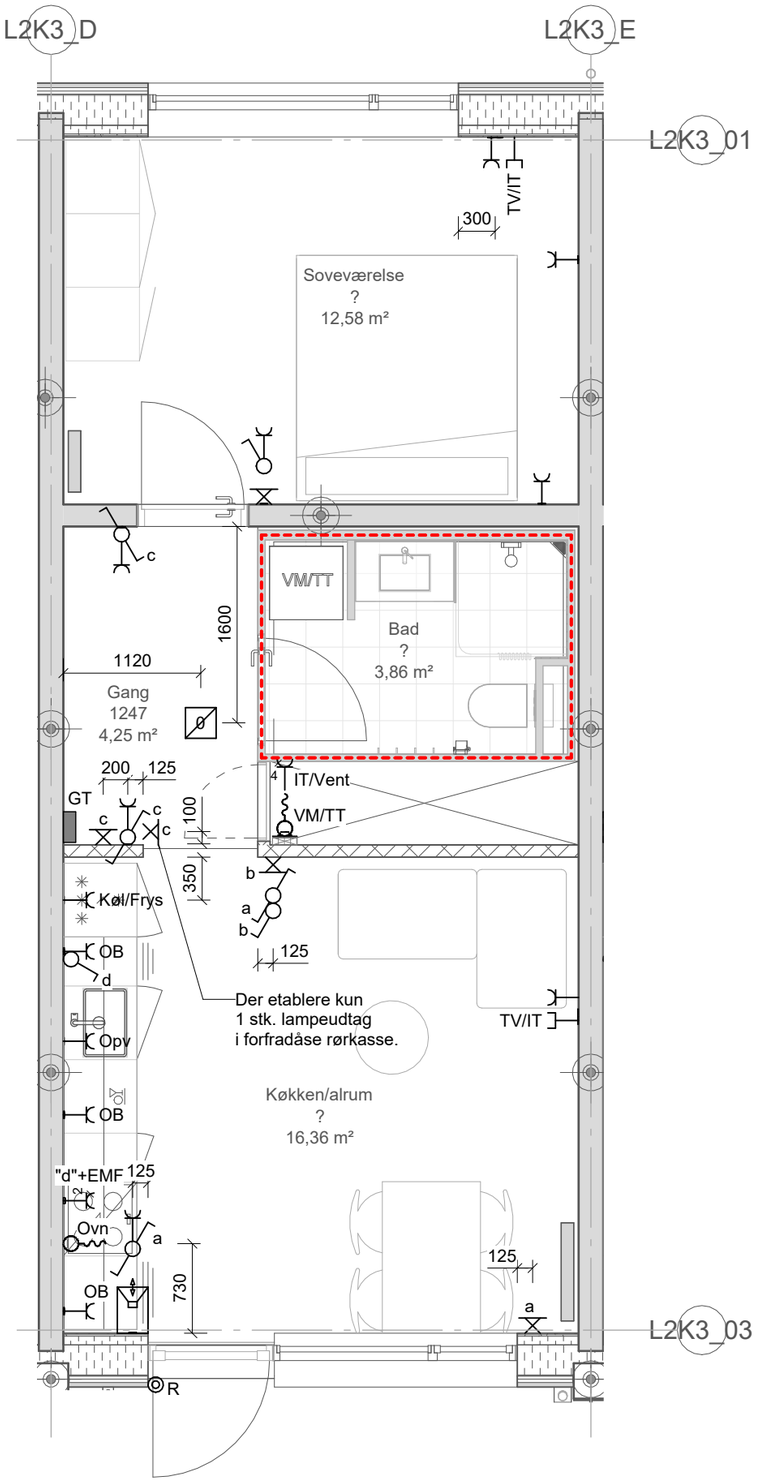

Projekt: Stejlepladsen


Tekst: Elinstallationer -
Byg K3 - 2. Sal
ALT_2V_T01 - Side K3-14

Tegningsnr.: ISP2_K07_L2XX_H04_EXX_N930

Rev.:

Projektnr.: 1019198 | Dato: 2026-02-27 | Rev. Dato: | Mål: 1 : 50 | Side: K3-14

www.arteliagroup.dk | Fil:

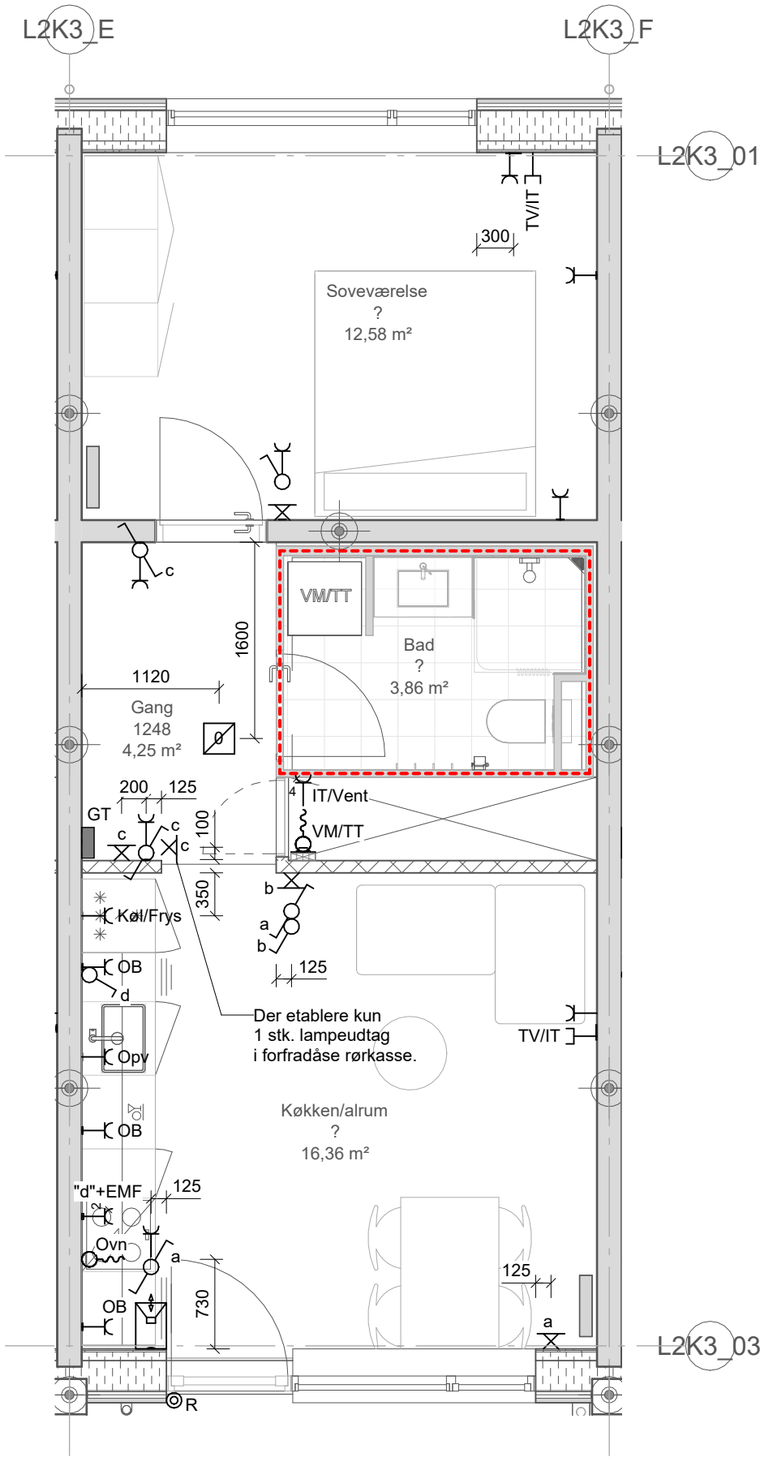

Projekt: Stejlepladsen

ARTELIA


Tekst: Elinstallationer -
Byg K3 - 2. Sal
ALT_2V_T01 - Side K3-15

Tegningsnr.: ISP2_K07_L2XX_H04_EXX_N930

Rev.:

Projektnr.: 1019198 | Dato: 2026-02-27 | Rev. Dato: | Mål: 1 : 50 | Side: K3-15

www.arteliagroup.dk | Fil:

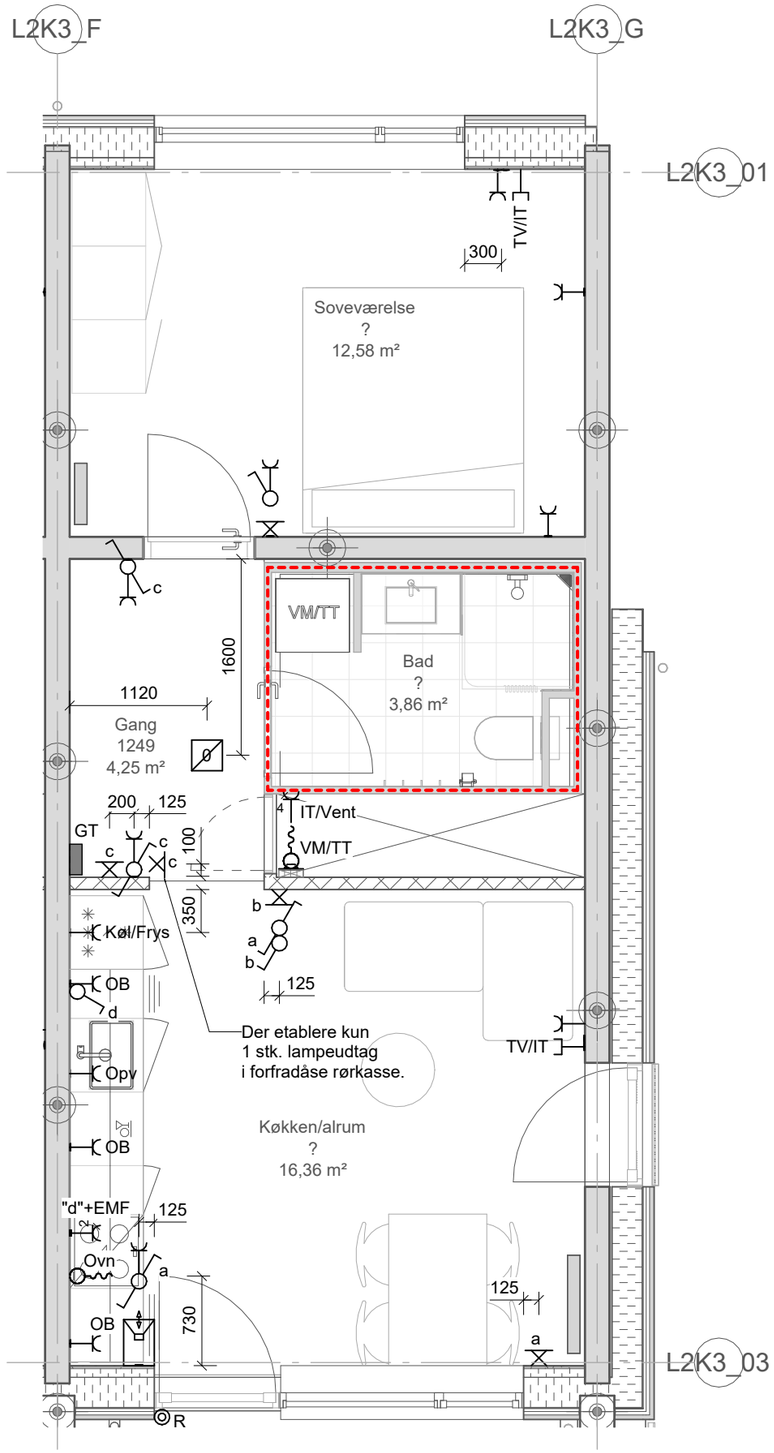

Projekt: Stejlepladsen


Tekst: Elinstallationer -
Byg K3 - 2. Sal
ALT_2V_T01 - Side K3-16

Tegningsnr.: ISP2_K07_L2XX_H04_EXX_N930

Rev.:

Projektnr.: 1019198 | Dato: 2026-02-27 | Rev. Dato: | Mål: 1 : 50 | Side: K3-16

www.arteliagroup.dk | Fil:

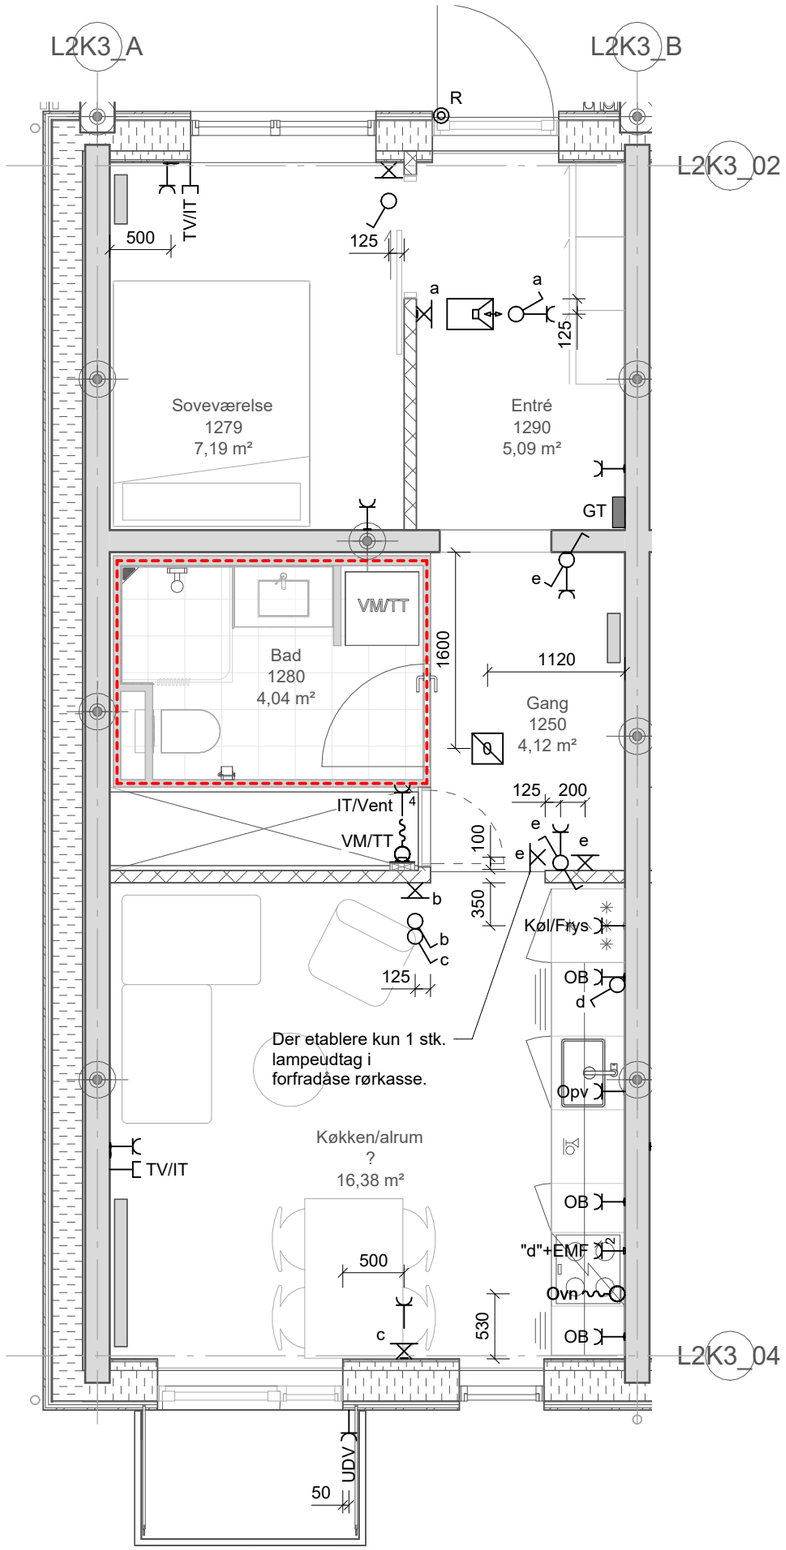

Projekt: Stejlepladsen


Tekst: Elinstallationer -
Byg K3 - 3. Sal
ALT_2V_T01_S - Side K3-17

Tegningsnr.: ISP2_K07_L2XX_H04_EXX_N930

Rev.:

Projektnr.: 1019198 | Dato: 2026-02-27 | Rev. Dato: | Mål: 1 : 50 | Side: K3-17

www.arteliagroup.dk | Fil:

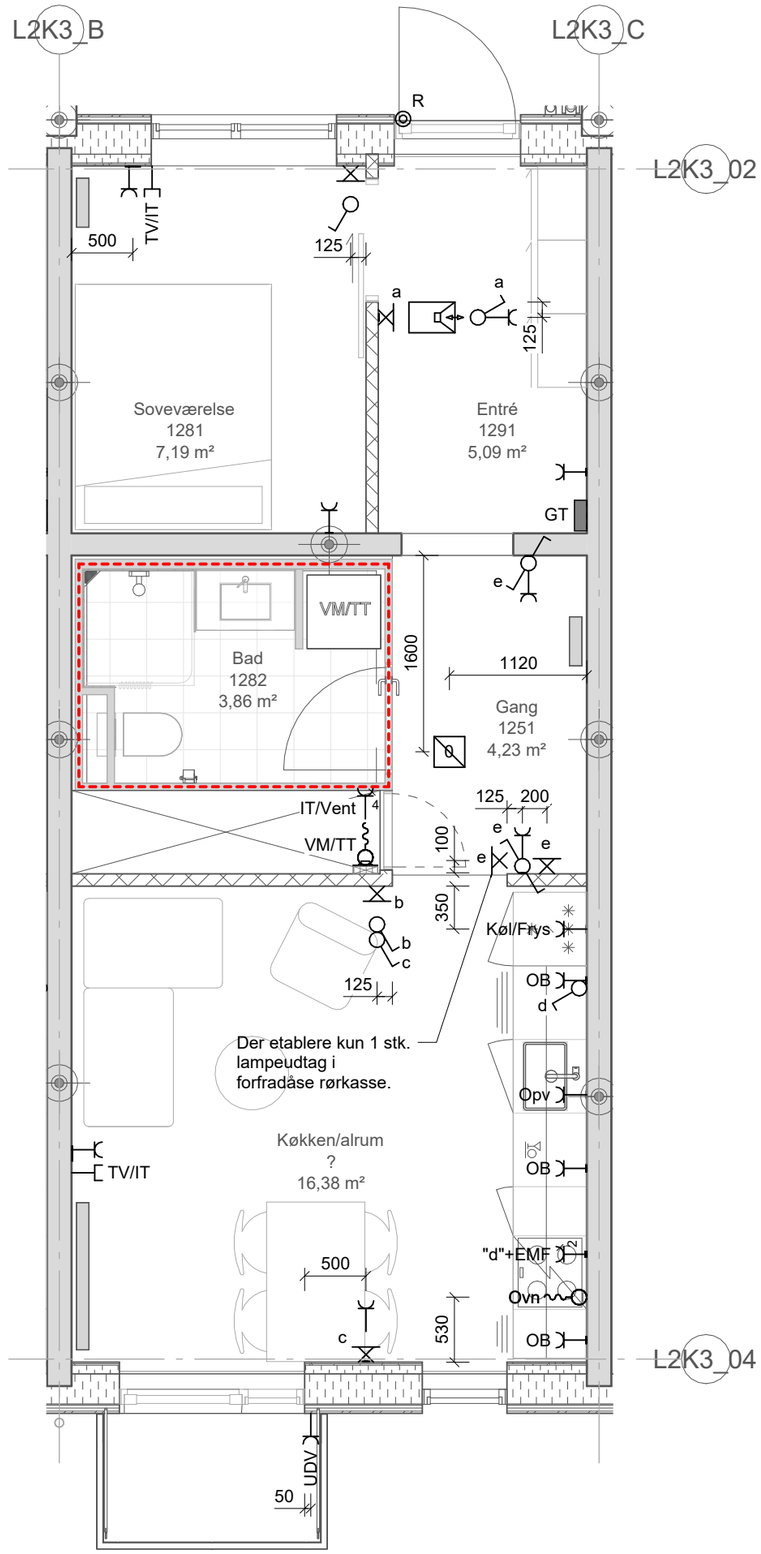

Projekt: Stejlepladsen


Tekst: Elinstallationer -
Byg K3 - 3. Sal
ALT_2V_T01_S - Side K3-18

Tegningsnr.: ISP2_K07_L2XX_H04_EXX_N930

Rev.:

Projektnr.: 1019198 | Dato: 2026-02-27 | Rev. Dato: | Mål: 1 : 50 | Side: K3-18

www.arteliagroup.dk | Fil:

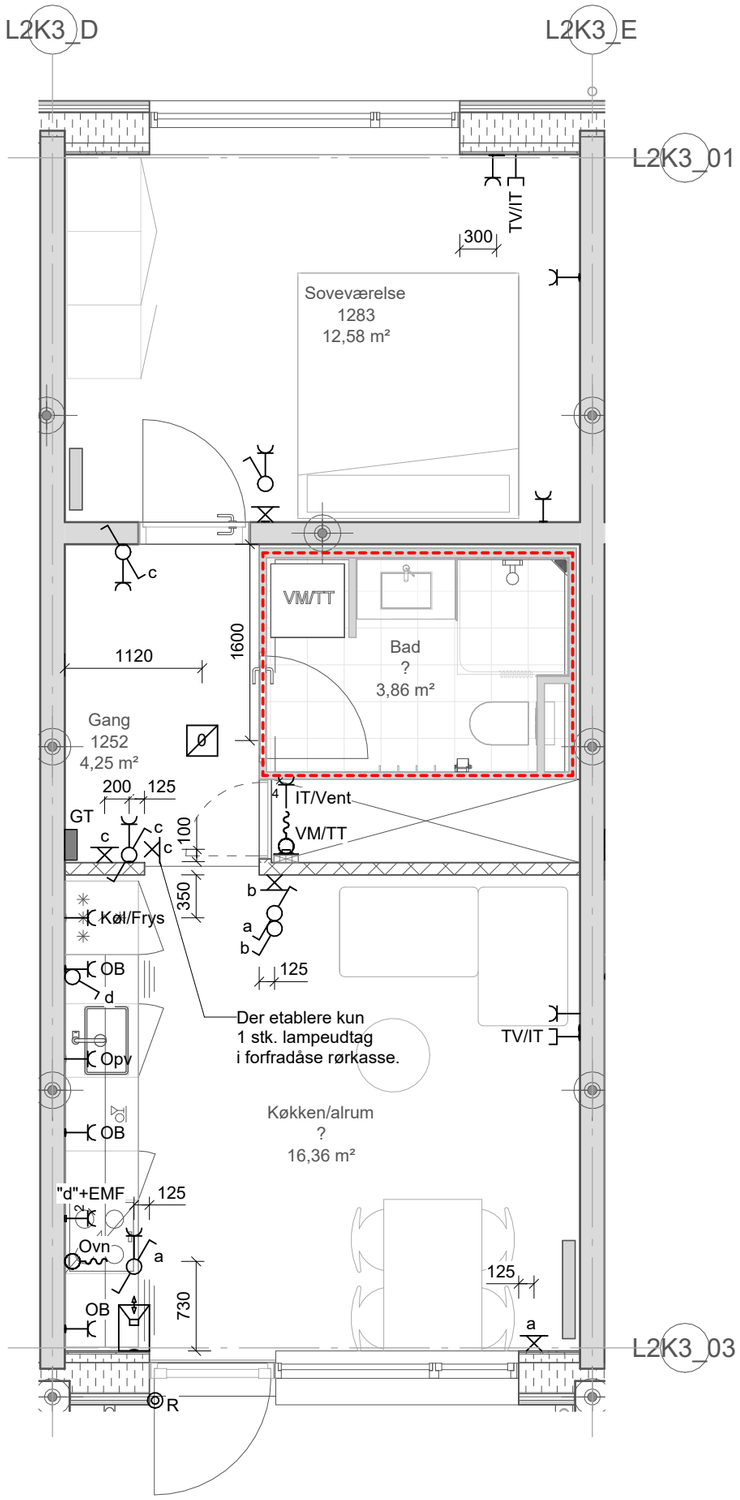

Projekt: Stejlepladsen

ARTELIA


Tekst: Elinstallationer -
Byg K3 - 3. Sal
ALT_2V_T01 - Side K3-19

Tegningsnr.: ISP2_K07_L2XX_H04_EXX_N930

Rev.:

Projektnr.: 1019198 | Dato: 2026-02-27 | Rev. Dato: | Mål: 1 : 50 | Side: K3-19

www.arteliagroup.dk | Fil:

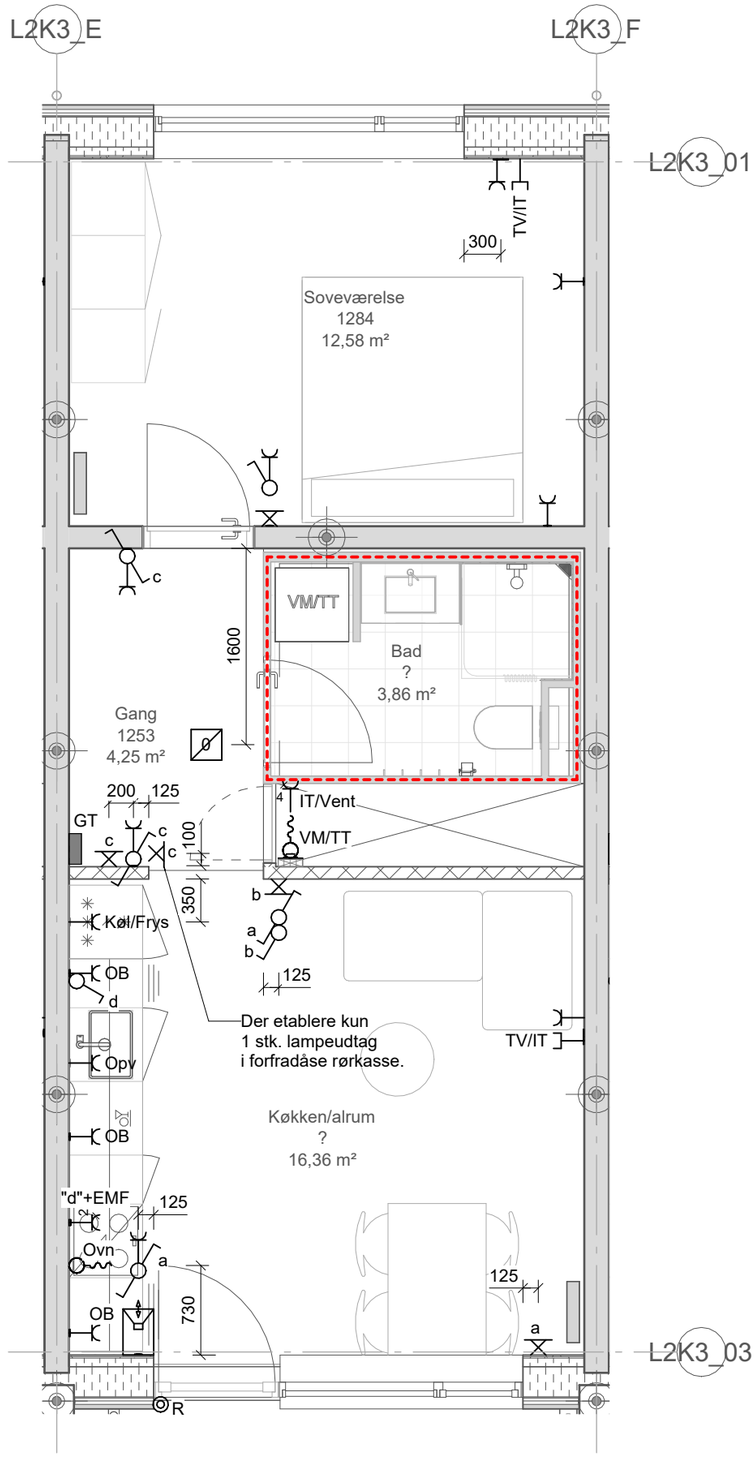

Projekt: Stejlepladsen

ARTELIA


Tekst: Elinstallationer -
Byg K3 - 3. Sal
ALT_2V_T01 - Side K3-20

Tegningsnr.: ISP2_K07_L2XX_H04_EXX_N930

Rev.:

Projektnr.: 1019198 | Dato: 2026-02-27 | Rev. Dato: | Mål: 1 : 50 | Side: K3-20

www.arteliagroup.dk | Fil:

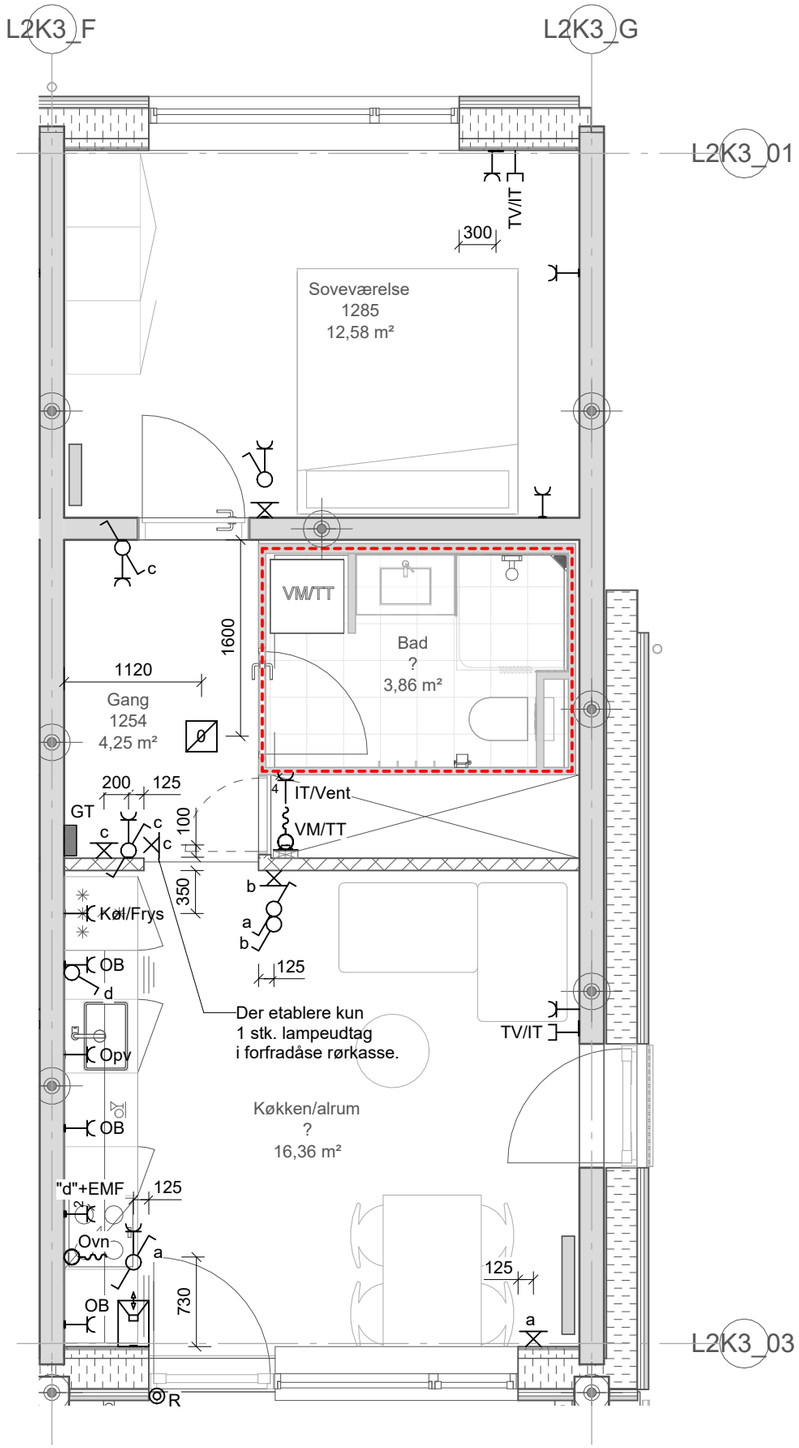

Projekt: Stejlepladsen


Tekst: Elinstallationer -
Byg K3 - 3. Sal
ALT_2V_T01 - Side K3-21

Tegningsnr.: ISP2_K07_L2XX_H04_EXX_N930

Rev.:

Projektnr.: 1019198 | Dato: 2026-02-27 | Rev. Dato: | Mål: 1 : 50 | Side: K3-21

www.arteliagroup.dk | Fil:

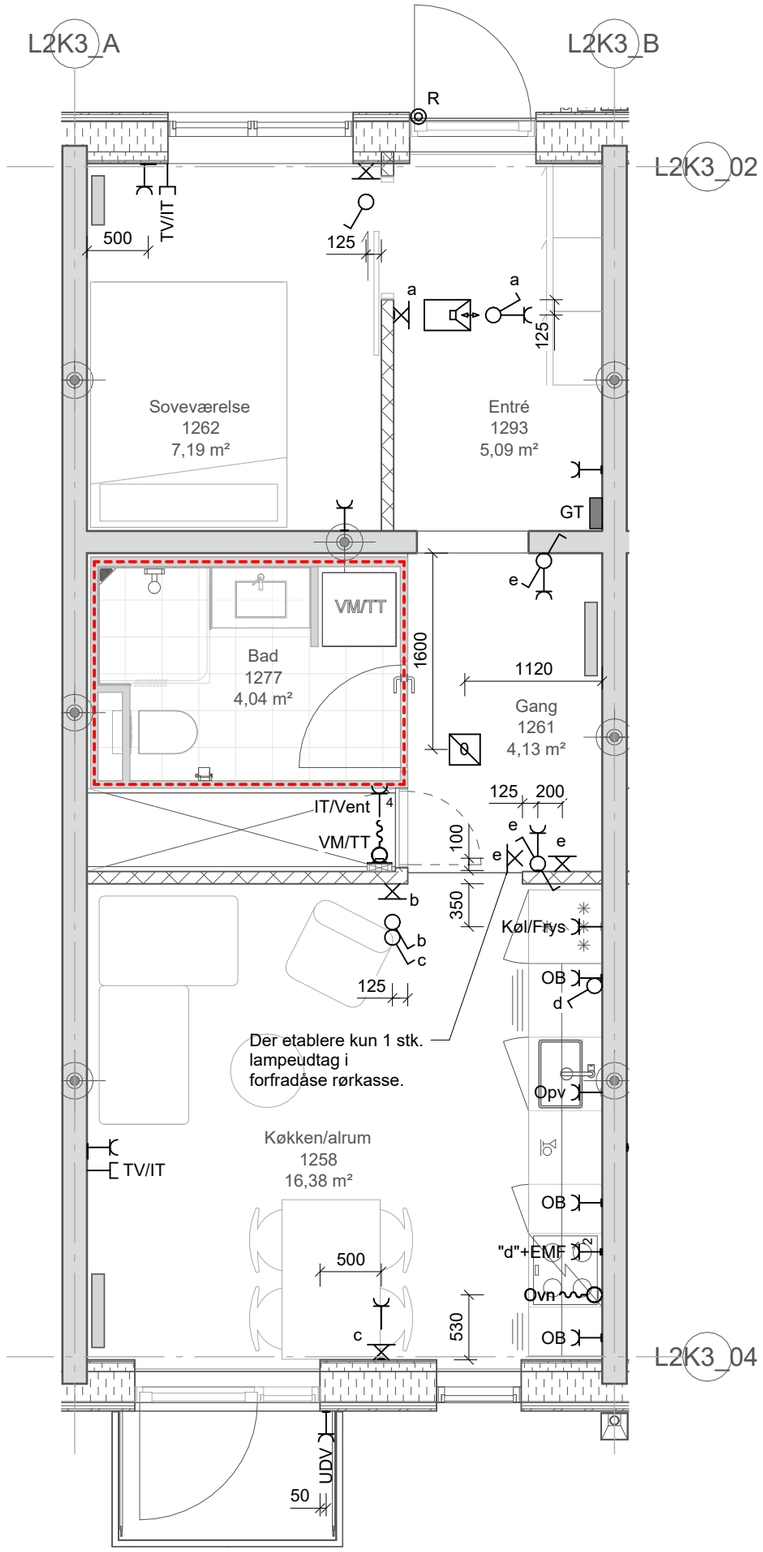

Projekt: Stejlepladsen


Tekst: Elinstallationer -
Byg K3 - 4. Sal
ALT_2V_T01_S - Side K3-22

Tegningsnr.: ISP2_K07_L2XX_H04_EXX_N930

Rev.:

Projektnr.: 1019198 | Dato: 2026-02-27 | Rev. Dato: | Mål: 1 : 50 | Side: K3-22

www.arteliagroup.dk | Fil:

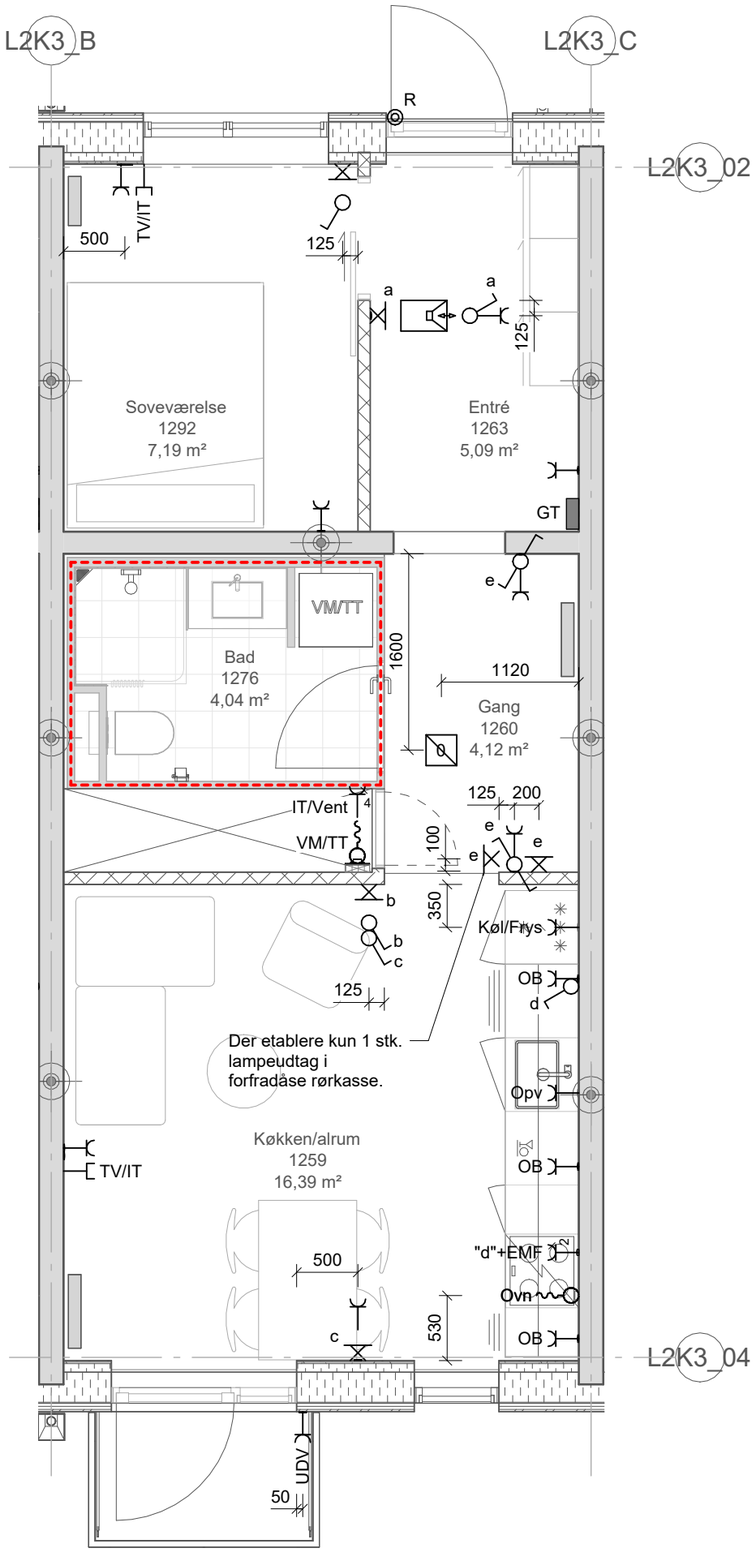

Projekt: Stejlepladsen

ARTELIA


Tekst: Elinstallationer -
Byg K3 - 4. Sal
ALT_2V_T01_S - Side K3-23

Tegningsnr.: ISP2_K07_L2XX_H04_EXX_N930

Rev.:

Projektnr.: 1019198 | Dato: 2026-02-27 | Rev. Dato: | Mål: 1 : 50 | Side: K3-23

www.arteliagroup.dk | Fil:

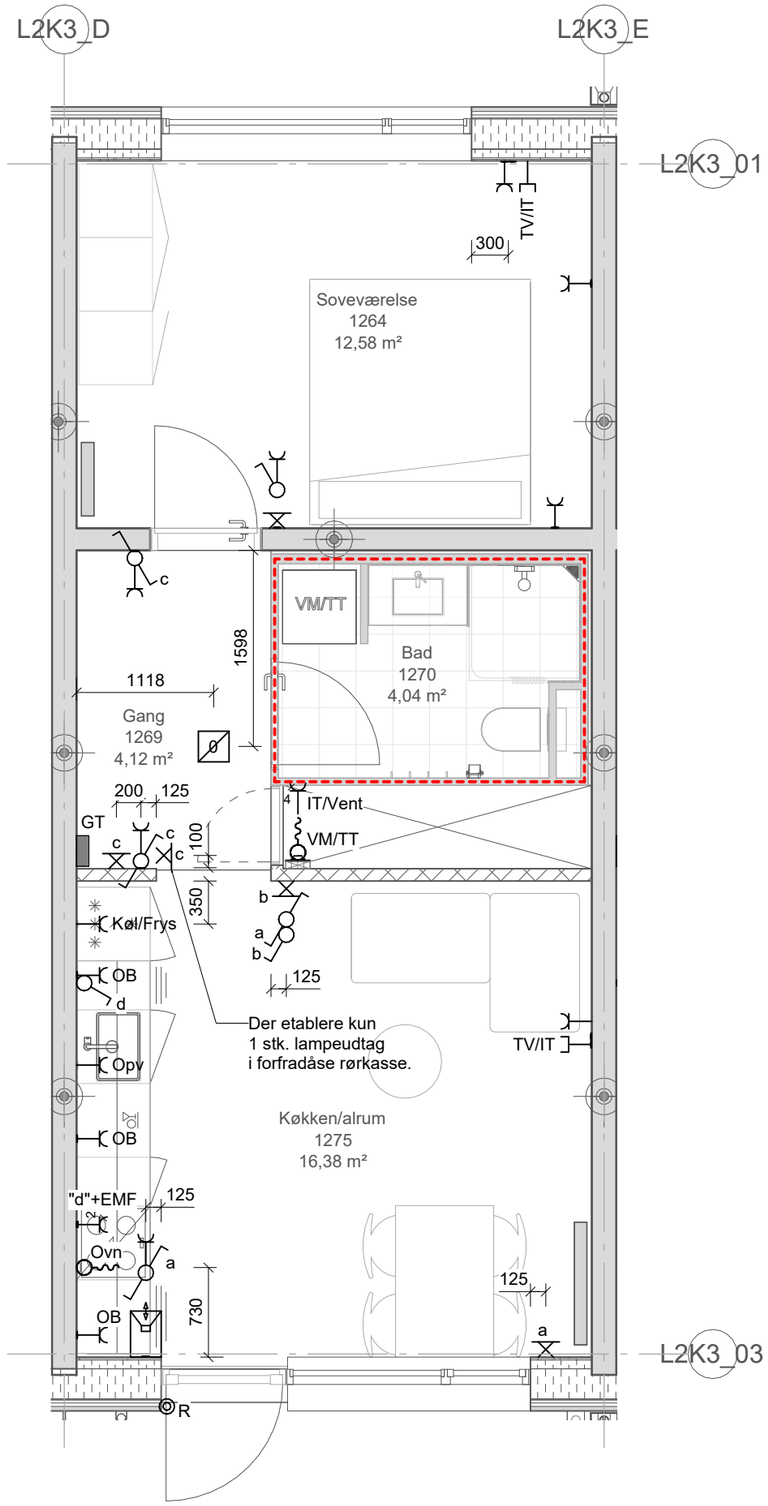

Projekt: Stejlepladsen


Tekst: Elinstallationer -
Byg K3 - 4. Sal
ALT_2V_T01 - Side K3-24

Tegningsnr.: ISP2_K07_L2XX_H04_EXX_N930

Rev.:

Projektnr.: 1019198 | Dato: 2026-02-27 | Rev. Dato: | Mål: 1 : 50 | Side: K3-24

www.arteliagroup.dk | Fil:

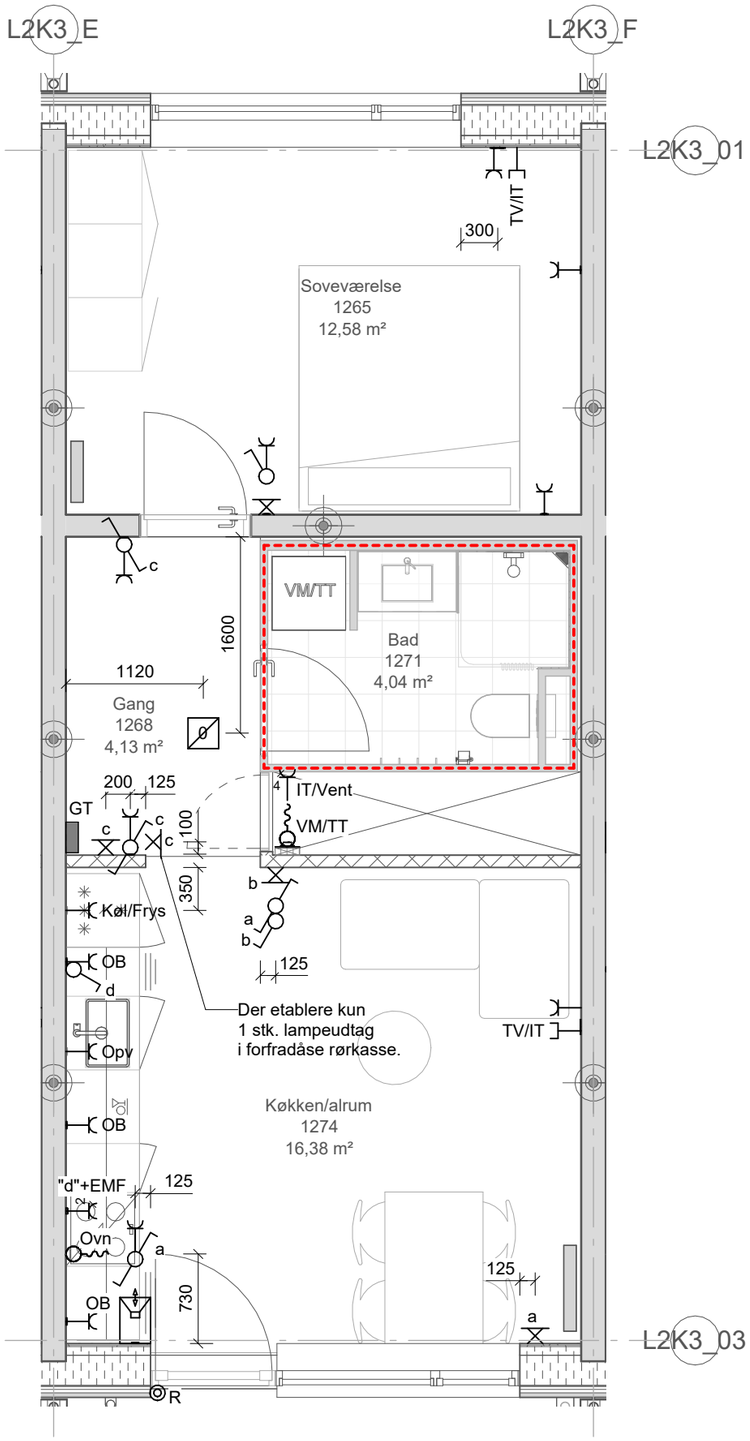

Projekt: Stejlepladsen

ARTELIA


Tekst: Elinstallationer -
Byg K3 - 4. Sal
ALT_2V_T01 - Side K3-25

Tegningsnr.: ISP2_K07_L2XX_H04_EXX_N930

Rev.:

Projektnr.: 1019198 | Dato: 2026-02-27 | Rev. Dato: | Mål: 1 : 50 | Side: K3-25

www.arteliagroup.dk | Fil:

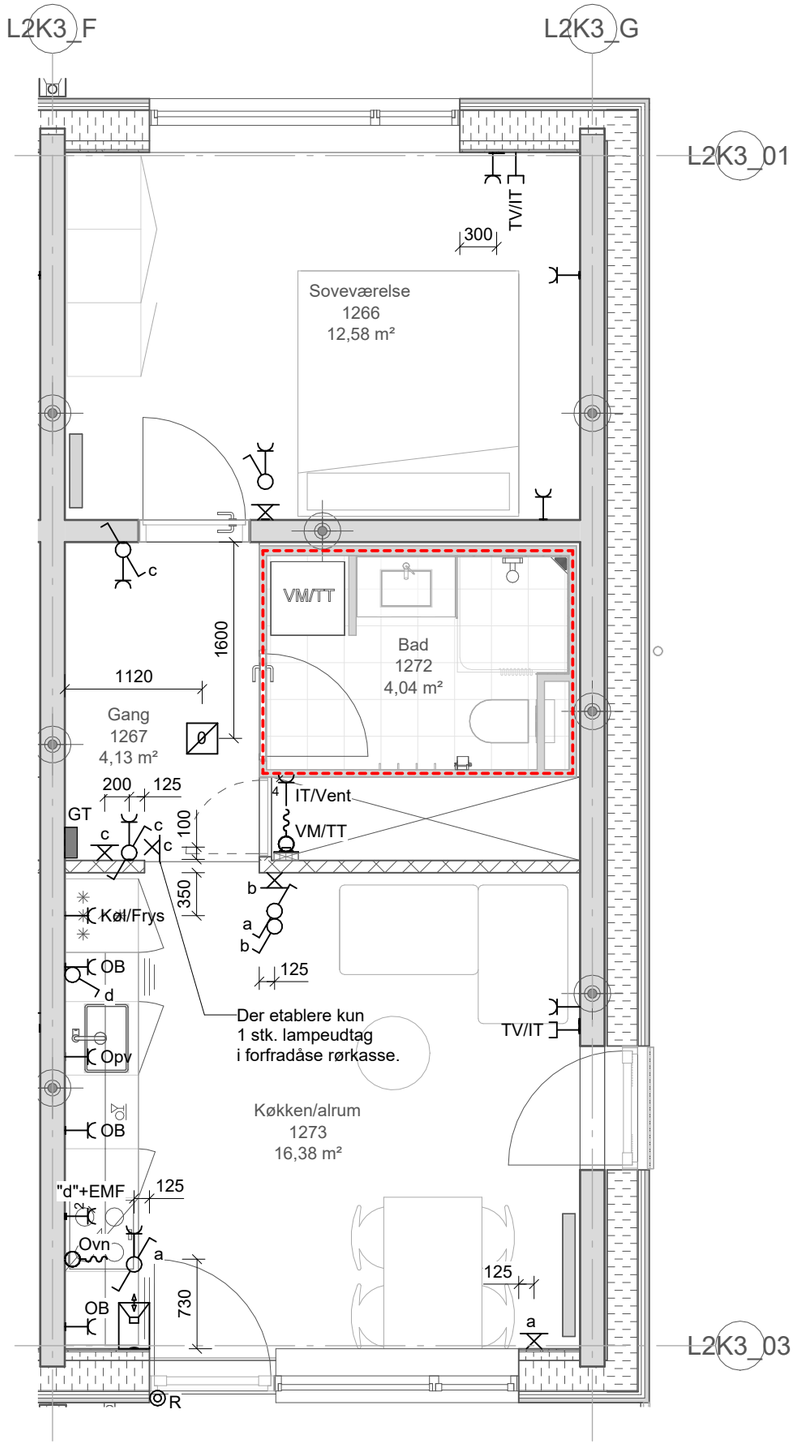

Projekt: Stejlepladsen

ARTELIA

Tekst: Elinstallationer -
Byg K3 - 4. Sal
ALT_2V_T01 - Side K3-26

Tegningsnr.: ISP2_K07_L2XX_H04_EXX_N930

Rev.:

Projektnr.: 1019198 | Dato: 2026-02-27 | Rev. Dato: | Mål: 1 : 50 | Side: K3-26

www.arteliagroup.dk | Fil: