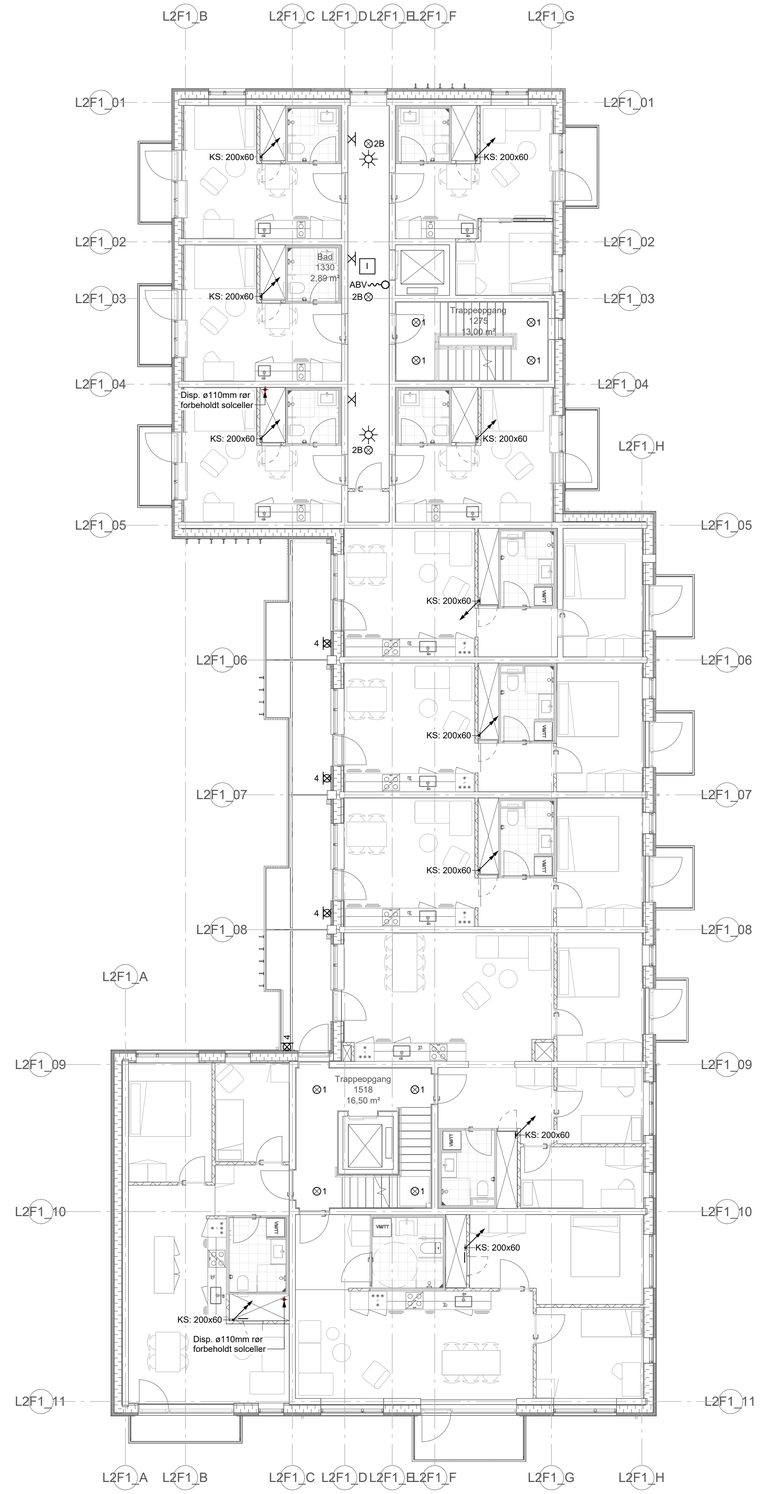


NOTER:

Områder der ikke forsynes fra fællestavler er angivet. Boliger er forsynet fra egen tavle.

HENVISNINGER:

For signatur se hæfte:
ISP2_K07_L2XX_H00_EXX_N100 - Elinstallationer - Signaturforklaring.

For princip og bestykning, fællesarealer se hæfte:
ISP2_K07_L2XX_H04_EXX_N932 - Elinstallationer - Princip og bestykning - Fællesarealer.

For princip og bestykning, lejlighedsplaner se hæfte:
ISP2_K07_L2XX_H04_EXX_N931 - Elinstallationer - Princip og bestykning - Lejlighedsplaner.


For placering af målertavler, se hæfte:
ISP2_K07_L2XX_H04_EXX_N900 - Elinstallationer - Principopstalter for målertavler i kælder / stue.

For armaturtyper se armaturliste:
ISPX_K07_C08.8_ZArmaturliste - Elinstallationer - Armaturliste.

Tegn. nr. :
ISP2_K07_L2F1_H01_E02_N902

Rev. :

Rev.	Rev. dato	Revisionen omfatter

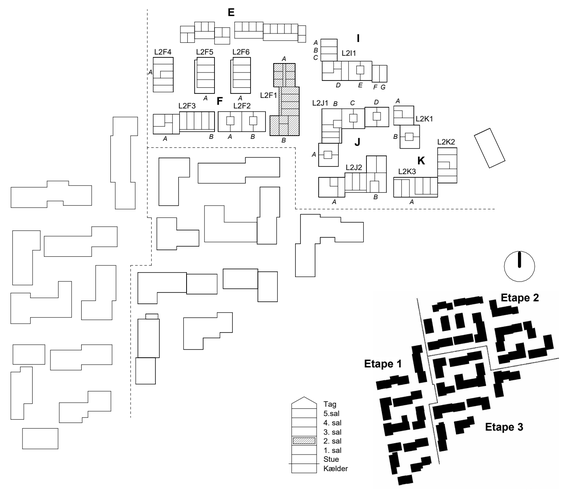

ARTELIA · SJÆLSØ Management · Stejlepladsen

Emne :
Elinstallationer - Føringsveje, lys, kraft og svagstrøm
L2F1 - 2. sal

Tegn. nr. :
ISP2_K07_L2F1_H01_E02_N902

Rev. :

Projektnr.:	1019198	Udf.:	BKR	Dato:	2026-02-27
Fase:	Udførelsesprojekt	Kontr.:	HELG	Rev. dato:	
Mål:	1:100	Godk.:	JSHO	Format:	A1

○ *Byherre: Ejendomsselskabet Stejlepladsen, Nordre Toldbod 7, 1259 København K*
○ *Styringsrådgiver: Sjælsø Management, Masnedøgade 20, 2100 København Ø*
○ *Arkitekt: Arkitema, Ny Carlsbergvej 120, 1799 København V*
● *Ingeniør: Artelia, Buddingevej 272, 2860 Søborg*
○ *Landskabsarkitekt: Kragh-Berglund, Ewaldsgade 3, 1., 2200 København N*
○ *Arkitekt: Lendager, Otto Busses Vej 27, 2450, København SV*