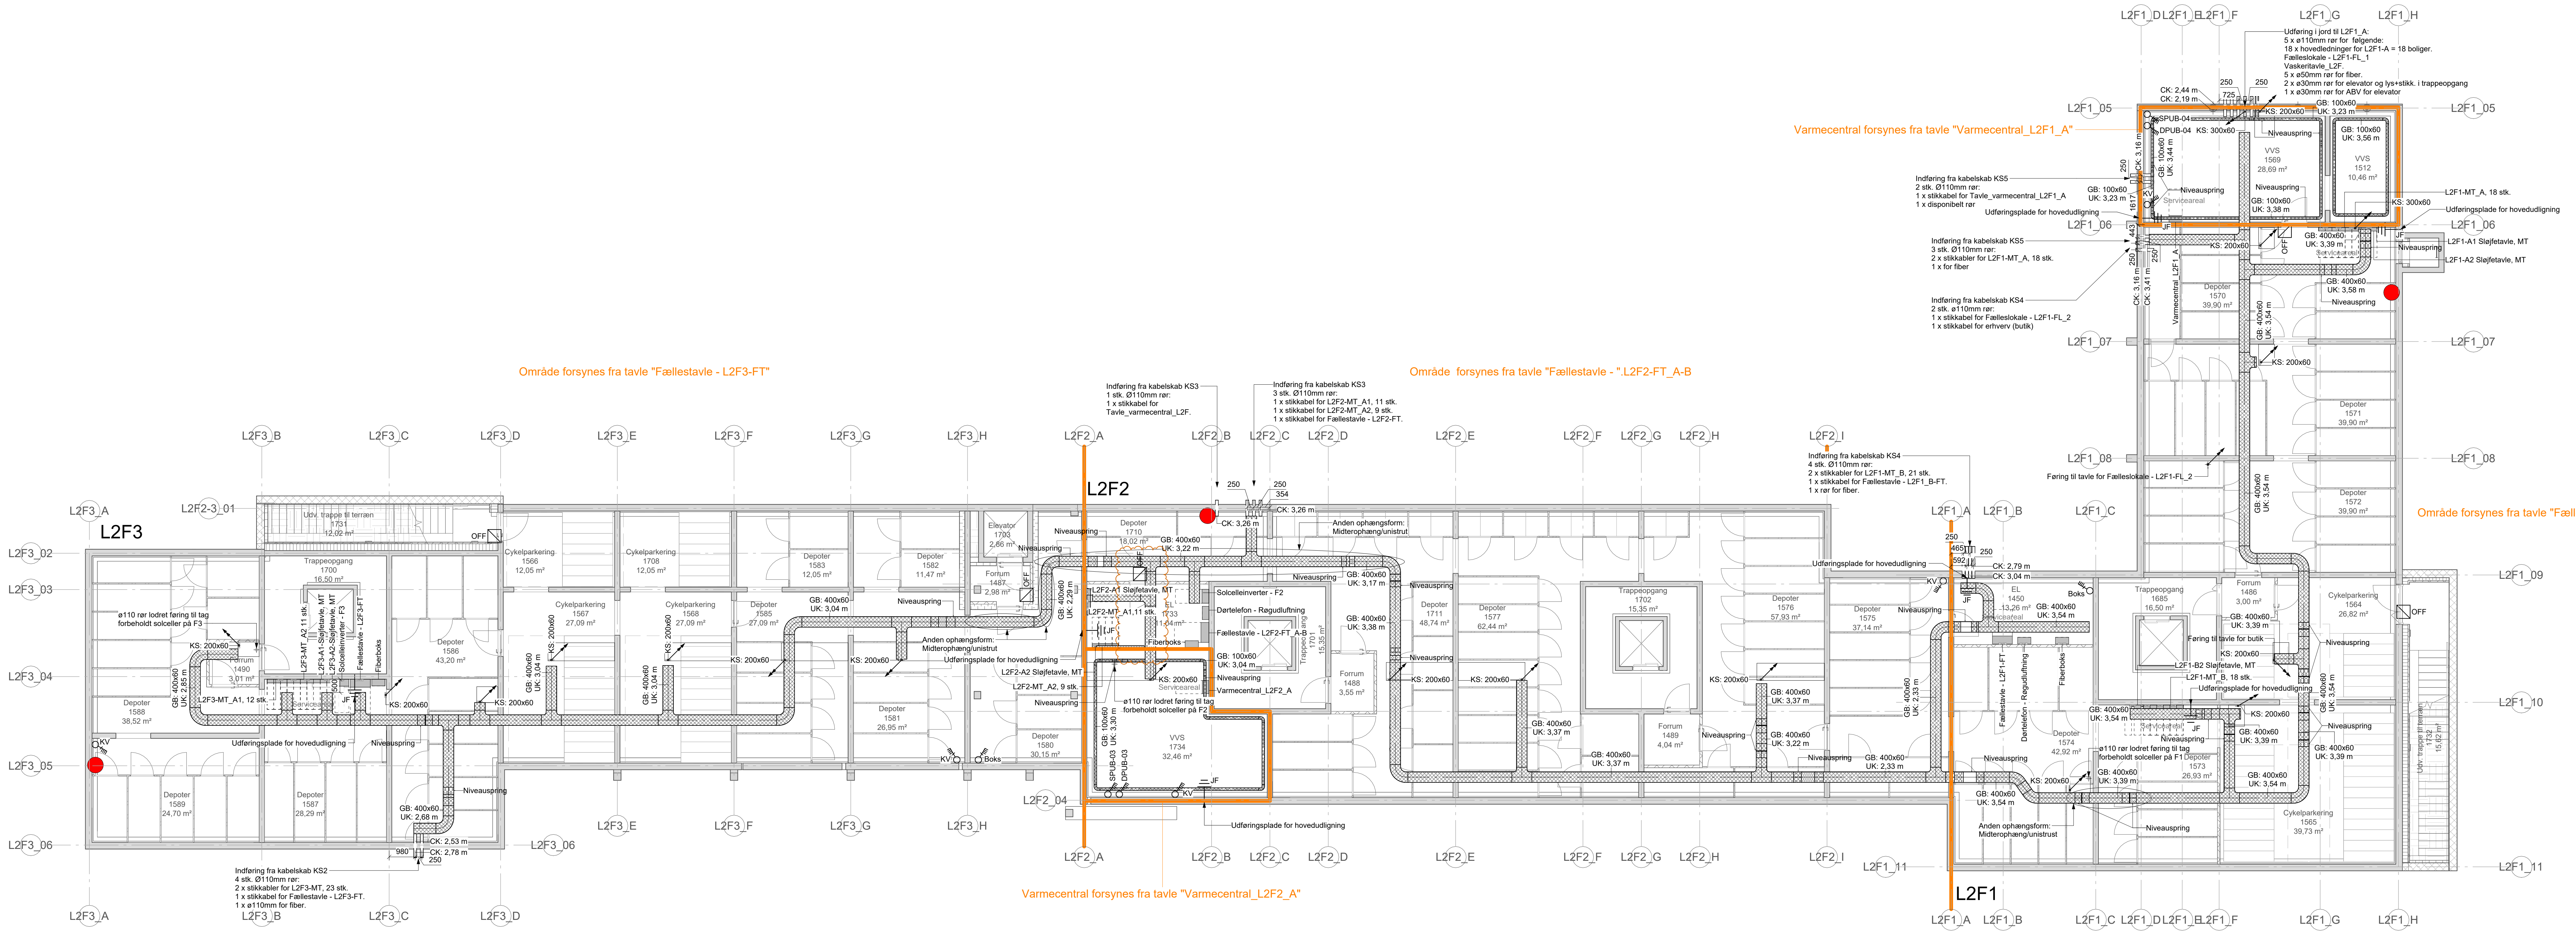

NOTE:

Alle koter er relative, angivet i mm til færdig gulvkote, med mindre andet er angivet.

Huller for ø110mm i kældervægge, med 110mm imellem huller.
Huller bores på stedet.

Områder der ikke forsynes fra fællestavler er angivet. Boliger er forsynet fra egen tavle.

HENVISNINGER:

For placering af målertavler, se hæfte: ISP2_K07_L2XX_H04_EXX_N900 - Principopstalter for målertavler i kælder / stue.

For placering af komponenter i varmecentral, se tegning: ISP2_K08_L2F1_H04_EKL_N900, ISP2_K08_L2F2_H04_EKL_N900, ISP2_K08_L2J1_H04_EKL_N900, ISP2_K08_L2J2_H04_EKL_N900.

For lys i kælder se tegning:
ISP2_K07_L2FX_H01_EKL_N411 - Elinstallationer - Lysinstallationer i kælder.
ISP2_K07_L2JX_H01_EKL_N412 - Elinstallationer - Lysinstallationer i kælder.

For sammenkobling af armering i væg og bundplade, se konstruktion generel note: ISP2_K09_LXX_H0_EXX_N001.

SIGNATURER:

▬	Målertavle / fællestavle / Internetudbyder.
GBXXX ▨	Gitterbakke, GB = Gitterbakke, XXX,XX = Størrelse på Gitterbakke.
KSXXX	Kabelstige, KS = Kabelstige, XXX,XX = Størrelse på Kabelstige.
KSXXX ⊠	Lodret kabelstige, KS = Kabelstige, XXX,XX = Størrelse på Kabelstige.
⊏ ═ ═ ⊐	Rør.
○	Lodret rør, størrelse af rør fremgår af tegningen.
Niveauspring	Niveauspring. Endelig placering koordineres under udførelse.
○──►►	Opadgående ledning.
●──►	Nedadgående ledning.
─‖ JF	Jordingspunkt, Udføringsplade for hovedudligning.
─(	230V stikkontakt.
▬	Forsyningsopdeling fra tavler.
SPUB-XX	Sikkerhedsafbryder 4P/16A, spulepumpebrønd. Koordines med Kloak.
DPUB-XX	Sikkerhedsafbryder 4P/16A, drænpumpebrønd. Koordines med Kloak.
∿○ RØG	Tilslutningssted for røgudluftning. Endelig placering koordineres på stedet.
XXXX	Sikkerhedsafbryder 4P/16A, for ventilation. Endelig placering koordineres på stedet. Forkortelser: Boks = Boksventilator for afværgeforanstaltninger KV = Kanalventilator
⧄ OFF	Dør med adgangskontrol - OFF-line.
🔴	For sammenkobling af armering i væg og bundplade.

SPOROPDELING L2XX:

GB400 Gitterbakke med 3 spor, Stik- og hovedledninger / SV / ST - 100/100/200

GB300 Gitterbakke med 2 spor, SV / ST - 100/200

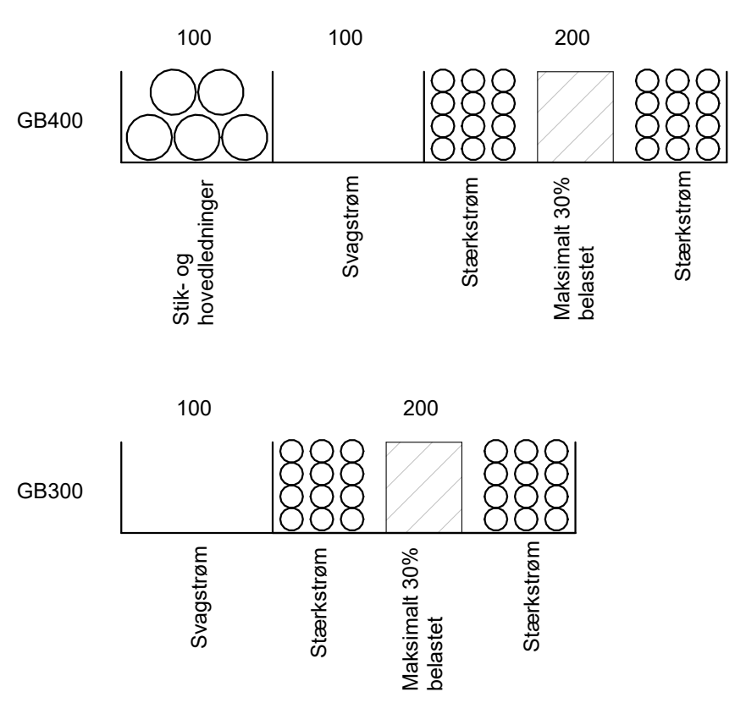

Tegn. nr. :
ISP2_K07_L2FX_H01_EKL_N911
Rev. :
2

Rev.	Rev. dato	Revisonen omfatter
2	2026-08-24	El tilpasset indretning af teknikrum EL 1733 og VVS 1734 i kælder
1	2026-05-19	Føringsvej tilpasset

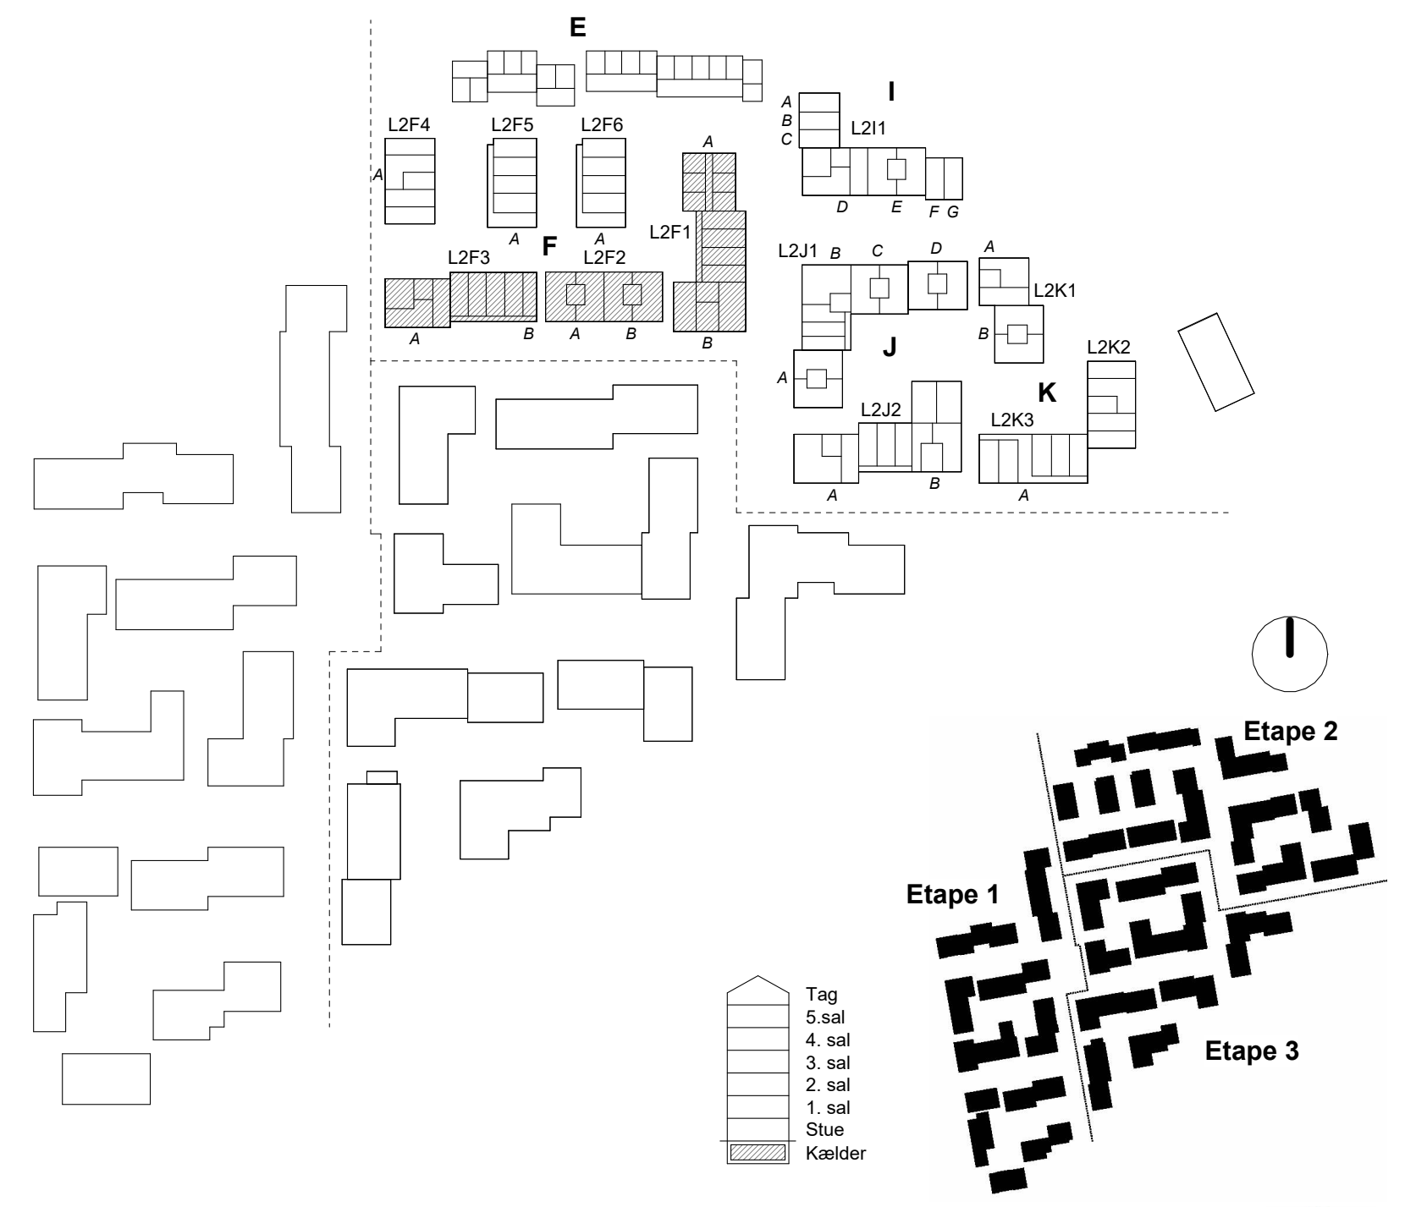

ARTELIA

SJÆLSØ Management

Stejlepladsen

Emne :
Elinstallationer - Føringsveje, kraft og svagstrøm
L2FX - Kælder

Tegn. nr. :
ISP2_K07_L2FX_H01_EKL_N911
Rev. :
2

Projektnr.:	1019198	Udf.:	BKR	Dato:	2026-02-27
Fase:	Udførelsesprojekt	Kontr.:	HELG	Rev. dato:	2026-08-24
Mål:	1 : 100	Godk.:	JSHO	Format:	A0

- ○ *Bygherre: Ejendomsselskabet Stejlepladsen, Nordre Toldbod 7, 1259 København K*
- ○ *Styringsrådgiver: Sjælsø Management, Masnedøgade 20, 2100 København Ø*
- ○ *Arkitekt: Arkitema, Ny Carlsbergvej 120, 1799 København V*
- ● *Ingeniør: Artelia, Buddingevej 272, 2860 Søborg*
- ○ *Landskabsarkitekt: Kragh-Berglund, Ewaldsgade 3, 1., 2200 København N*
- ○ *Arkitekt: Lendager, Otto Busses Vej 27, 2450, København SV*