NOTE:

Alle koter er relative, angivet i mm til færdig gulvkote, med mindre andet er angivet.

Belysning skal være på egne grupper og stikkontakter må ikke sættes på belysningsgrupper.

Belysningsarmaturer samt PIR er alene vejledende for placering og antal.

Belysningsarmaturer iht. armaturliste, endelig placering af lysarmaturer iht. arkitektprojekt.


HENVISNINGER:


For Føringsveje, kraft og svagstrøm i kælder se tegning:
ISP2_K07_L2FX_H01_EKL_N911 - Elinstallationer - Føringsveje, kraft og svagstrøm i kælder.
ISP2_K07_L2JX_H01_EKL_N912 - Elinstallationer - Føringsveje, kraft og svagstrøm i kælder.

Belysningsarmaturer, se armaturliste – tegning nr. ISPX_K07_C08.8_ZX-armaturliste.

SIGNATURER:

6	Armaturtype 6, påbygget, i henhold til armaturliste. Se note.
6	Armaturtype 6, Nedhængt, i henhold til armaturliste. Se note.
3	Facadebelysning, type 3, i henhold til armaturliste. Se note.
1	Belysning, type 1, i henhold til armaturliste. Se note.
	PIR-føler, loft monteret 360°.
	Enpolet afbryder med glimlampe.

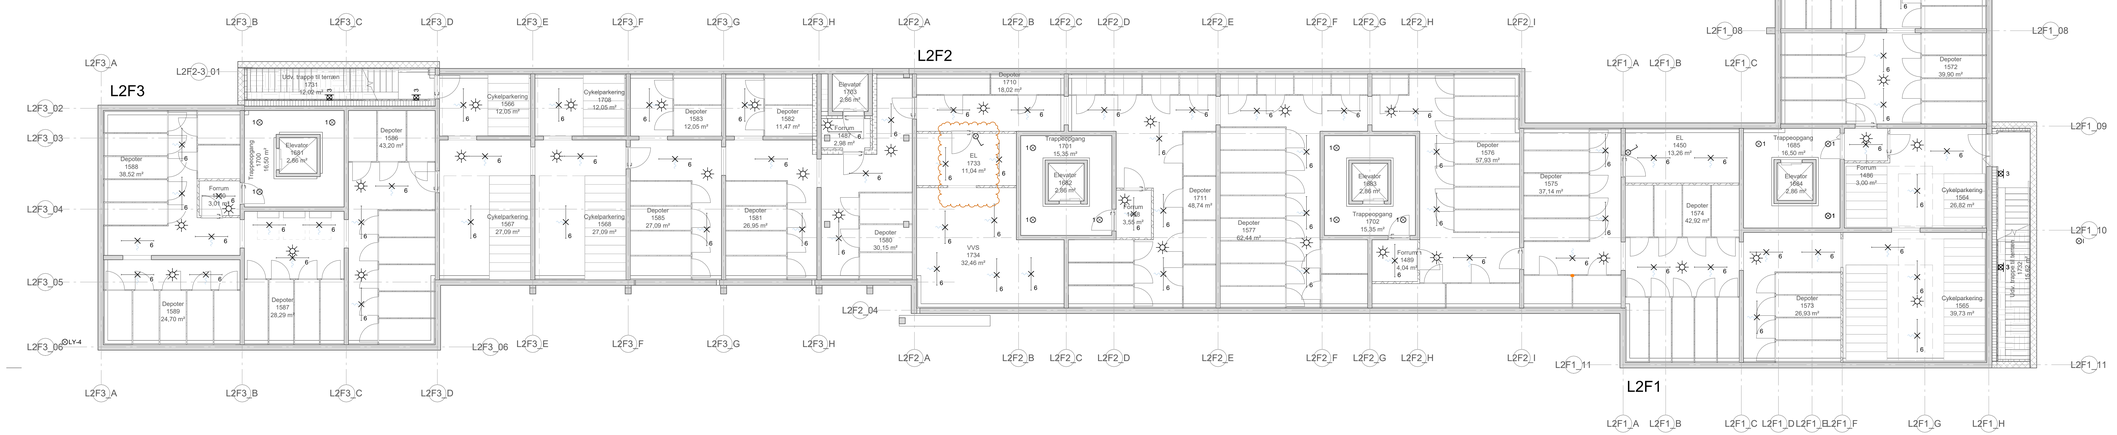

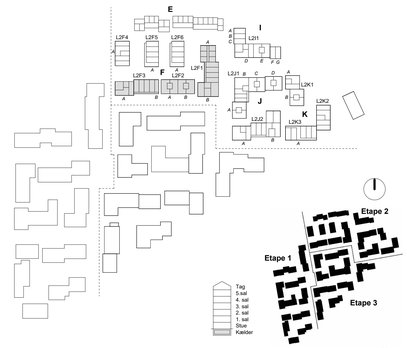

Rev.	Rev. dato	Revisionen omfatter
2	2026-08-24	El tilpasset indretning af teknikrum EL 1733 og VVS 1734 i kælder
1	2026-05-19	Lys tilpasset

Tegn. nr.:
ISP2_K07_L2FX_H01_EKL_N411

Rev.:
2

ARTELIA

SJÆLSØ Management

Stejlepladsen

Emne:
Elinstallationer -
L2FX - Lysinstallationer i kælder

Tegn. nr.:
ISP2_K07_L2FX_H01_EKL_N411

Rev.:
2

Projektnr.:	1019106	Udf.:	BKR
Fase:	Udførelsesprojekt	Kontr.:	HELG
Mål:	1:100	Godk.:	JSHO
		Dato:	2026-02-27
		Rev. dato:	2026-08-24
		Format:	A0

○ *Bygherre: Ejendomsselskabet Stejlepladsen, Nordre Toldbod 7, 1259 København K*
○ *Styringsrådgiver: Sjælsø Management, Mesnedalsgade 20, 2100 København Ø*
○ *Arkitekt: Arkitema, Ny Carlsbergvej 100, 1799 København V*
◆ *Ingeniør: Artelia, Buddingevej 272, 2860 Søborg*
○ *Landskabsarkitekt: Kragh-Berglund, Ewaldsgade 3, 1., 2200 København N*
○ *Arkitekt: Lendager, Otto Busses Vej 27, 2450, København SV*