Sheet Number	Tekst:	Dato:	Rev.:	Rev. Dato:
ISP2_K07_L2XX_H04_EFX_N931 - Side F2-1	Byg F2 - Index	2026-02-27		
ISP2_K07_L2XX_H04_EFX_N931 - Side F2-2	Byg F2 - Oversigtsplan	2026-02-27		
ISP2_K07_L2XX_H04_EFX_N931 - Side F2-3	Byg F2 - Stueplan, Byg A	2026-02-27		
ISP2_K07_L2XX_H04_EFX_N931 - Side F2-4	Byg F2 - Stueplan, Byg A	2026-02-27		
ISP2_K07_L2XX_H04_EFX_N931 - Side F2-5	Byg F2 - Stueplan, Byg B	2026-02-27		
ISP2_K07_L2XX_H04_EFX_N931 - Side F2-6	Byg F2 - Stueplan, Byg B	2026-02-27		
ISP2_K07_L2XX_H04_EFX_N931 - Side F2-7	Byg F2 - 1. Sal, Byg A	2026-02-27		
ISP2_K07_L2XX_H04_EFX_N931 - Side F2-8	Byg F2 - 1. Sal, Byg A	2026-02-27		
ISP2_K07_L2XX_H04_EFX_N931 - Side F2-9	Byg F2 - 1. Sal, Byg B	2026-02-27		
ISP2_K07_L2XX_H04_EFX_N931 - Side F2-10	Byg F2 - 1. Sal, Byg B	2026-02-27		
ISP2_K07_L2XX_H04_EFX_N931 - Side F2-11	Byg F2 - 2. Sal, Byg A	2026-02-27		
ISP2_K07_L2XX_H04_EFX_N931 - Side F2-12	Byg F2 - 2. Sal, Byg A	2026-02-27		
ISP2_K07_L2XX_H04_EFX_N931 - Side F2-13	Byg F2 - 2. Sal, Byg B	2026-02-27		
ISP2_K07_L2XX_H04_EFX_N931 - Side F2-14	Byg F2 - 2. Sal, Byg B	2026-02-27		
ISP2_K07_L2XX_H04_EFX_N931 - Side F2-15	Byg F2 - 3. Sal, Byg A	2026-02-27		
ISP2_K07_L2XX_H04_EFX_N931 - Side F2-16	Byg F2 - 3. Sal, Byg A	2026-02-27		
ISP2_K07_L2XX_H04_EFX_N931 - Side F2-17	Byg F2 - 3. Sal, Byg B	2026-02-27		
ISP2_K07_L2XX_H04_EFX_N931 - Side F2-18	Byg F2 - 3. Sal, Byg B	2026-02-27		
ISP2_K07_L2XX_H04_EFX_N931 - Side F2-19	Byg F2 - 4. Sal, Byg A	2026-02-27		
ISP2_K07_L2XX_H04_EFX_N931 - Side F2-20	Byg F2 - 4. Sal, Byg A	2026-02-27		
ISP2_K07_L2XX_H04_EFX_N931 - Side F2-21	Byg F2 - 4. Sal, Byg B	2026-02-27		
ISP2_K07_L2XX_H04_EFX_N931 - Side F2-22	Byg F2 - 4. Sal, Byg B	2026-02-27		

Projekt: Stejlepladsen

Tekst: Elinstallationer - Byg F2 - Index


Tegningsnr.: ISP2_K07_L2XX_H04_EFX_N931

Rev.:


Projektnr.: 1019198 | Dato: 2026-02-27 | Rev. Dato: | Mål: | Side: F2-1

www.arteliagroup.dk | Fil:


Stueplan - Byg F2

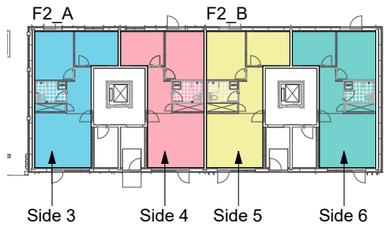


1. sal - Byg F2

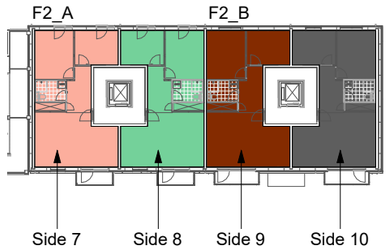


2. sal - Byg F2

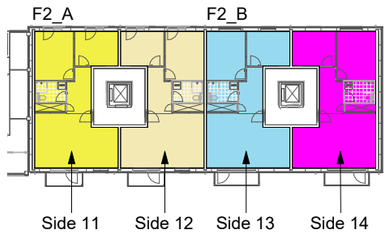

3. sal - Byg F2

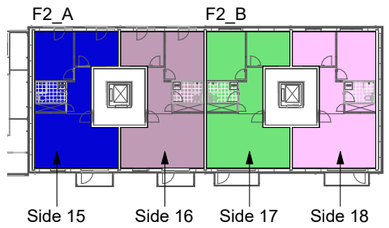

4. sal - Byg F2

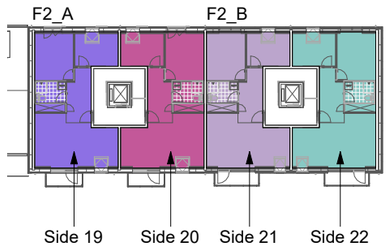

Oversigt, bygning F2:

Side 3:		Opgangsbolig, Byg A, st., 3V
Side 4:		Opgangsbolig, Byg A, st., 3V
Side 5:		Opgangsbolig, Byg B, st., 3V
Side 6:		Opgangsbolig, Byg B, st., 3V
Side 7:		Opgangsbolig, Byg A, 1.sal, 3V
Side 8:		Opgangsbolig, Byg A, 1.sal, 3V
Side 9:		Opgangsbolig, Byg B, 1.sal, 3V
Side 10:		Opgangsbolig, Byg B, 1.sal, 3V
Side 11:		Opgangsbolig, Byg A, 2.sal, 3V
Side 12:		Opgangsbolig, Byg A, 2.sal, 3V
Side 13:		Opgangsbolig, Byg B, 2.sal, 3V
Side 14:		Opgangsbolig, Byg B, 2.sal, 3V
Side 15:		Opgangsbolig, Byg A, 3.sal, 3V
Side 16:		Opgangsbolig, Byg A, 3.sal, 3V
Side 17:		Opgangsbolig, Byg B, 3.sal, 3V
Side 18:		Opgangsbolig, Byg B, 3.sal, 3V
Side 19:		Opgangsbolig, Byg A, 4.sal, 3V
Side 20:		Opgangsbolig, Byg A, 4.sal, 3V
Side 21:		Opgangsbolig, Byg B, 4.sal, 3V
Side 22:		Opgangsbolig, Byg B, 4.sal, 3V

Projekt: Stejlepladsen


Tekst: Elinstallationer -
Byg F2 - Oversigtsplan

Tegningsnr.: ISP2_K07_L2XX_H04_EFX_N931

Rev.:

Projektnr.: 1019198 | Dato: 2026-02-27 | Rev. Dato: | Mål: 1 : 500 | Side: F2-2

www.arteliagroup.dk | Fil:

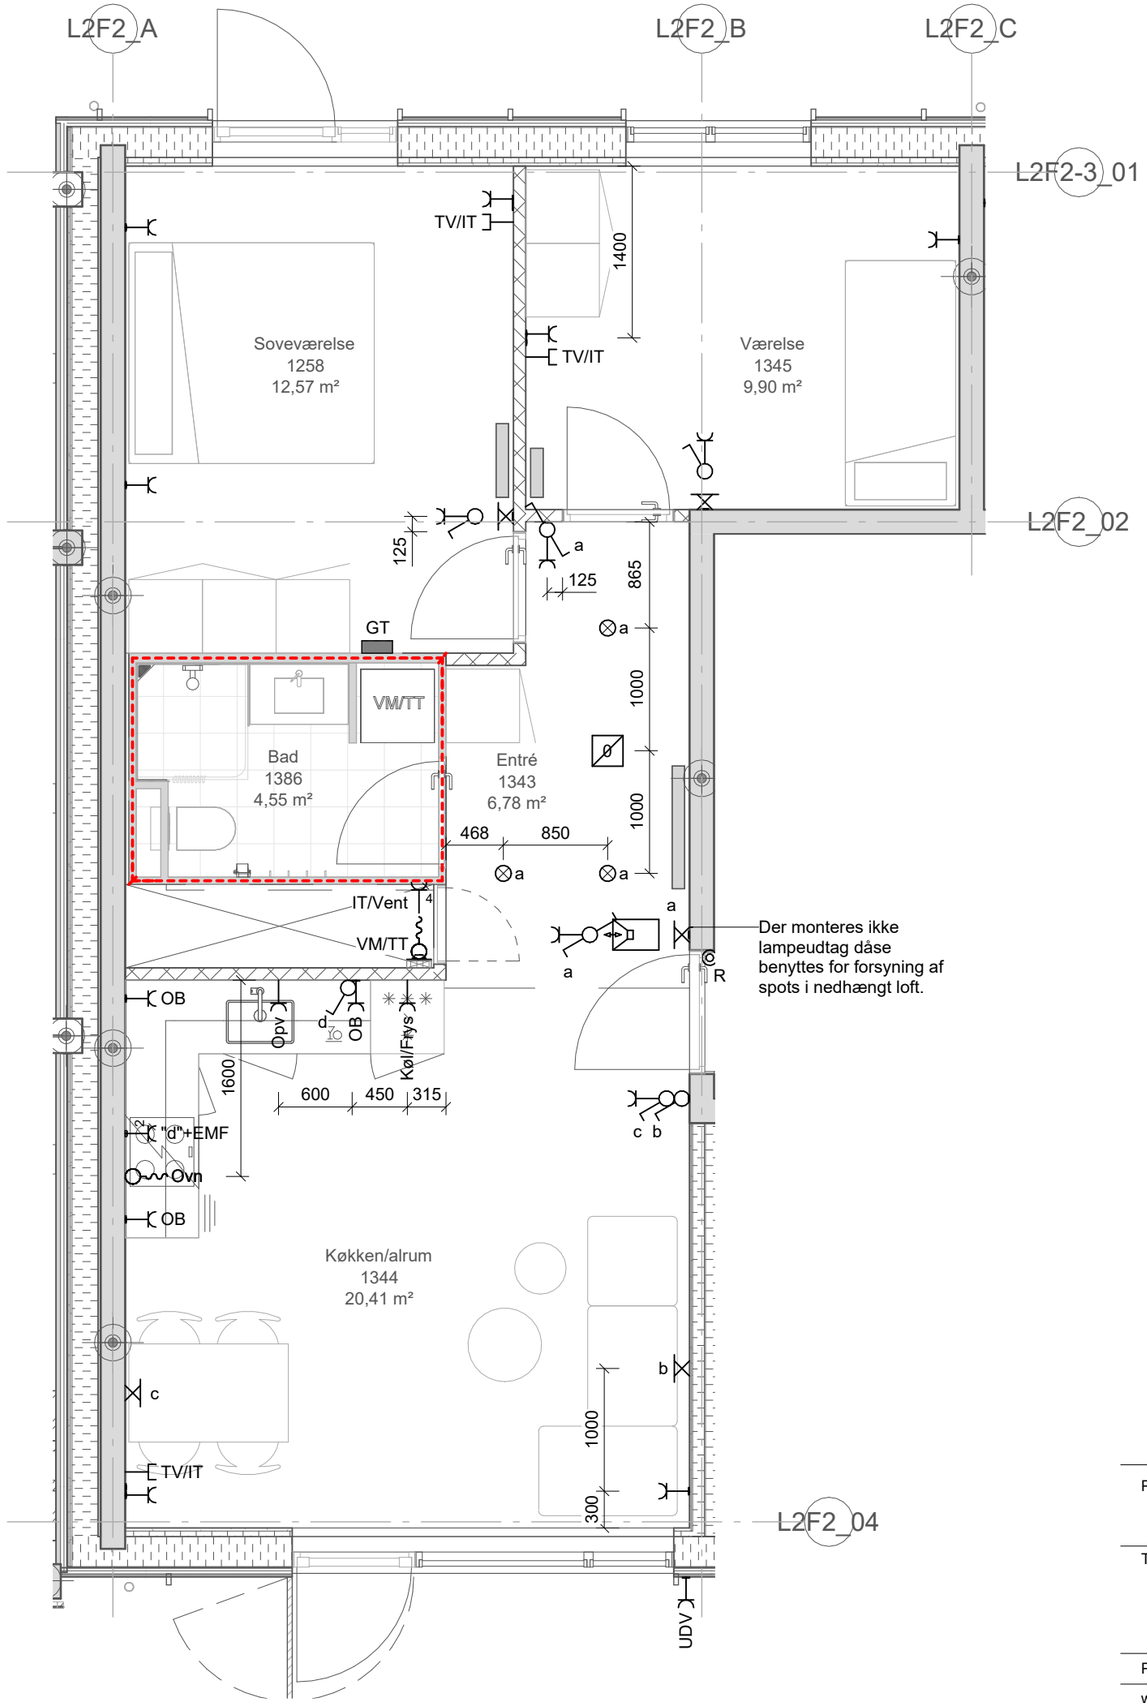

Projekt: Stejlepladsen


Tekst: Elinstallationer -
Byg F2 - Stueplan, Byg A
OPG_3V_T32_ST - Side F2-3

Tegningsnr.: ISP2_K07_L2XX_H04_EXX_N931


Rev.:

Projektnr.: 1019198 | Dato: 2026-02-27 | Rev. Dato: | Mål: 1 : 50 | Side: F2-3

www.arteliagroup.dk | Fil:

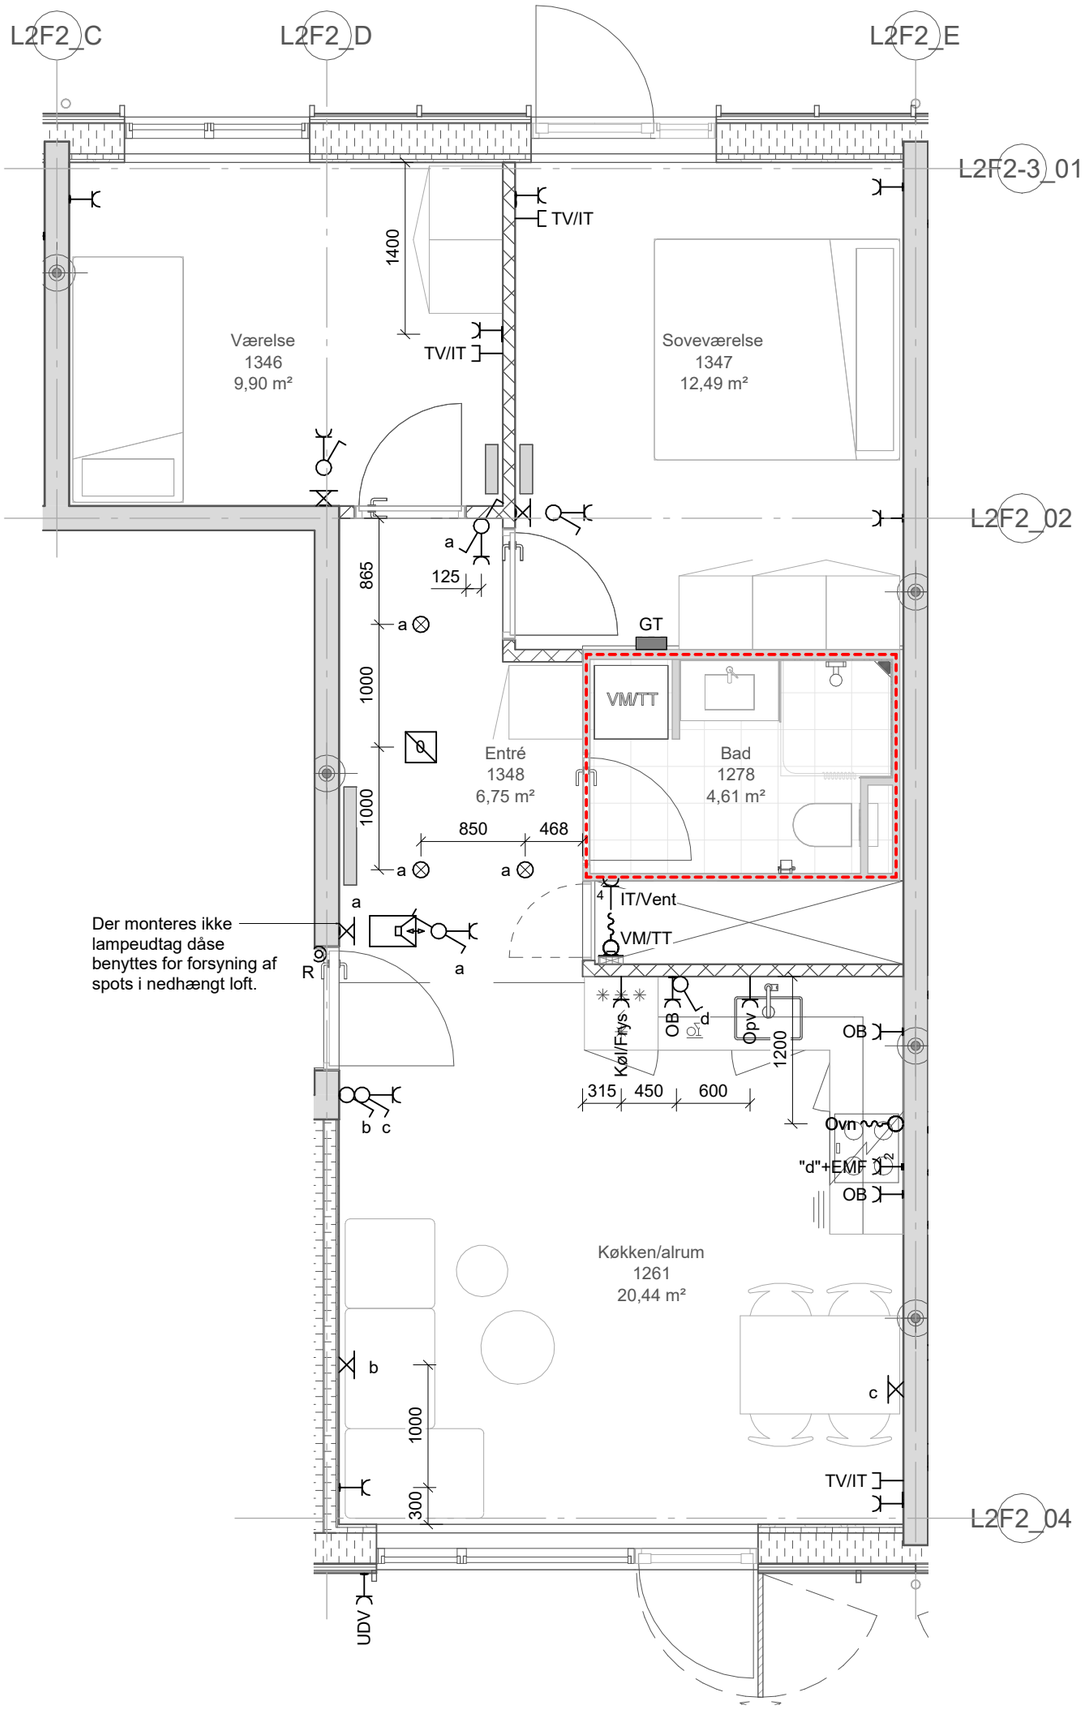

Projekt:	Stejlepladsen				
Tekst:	Elinstallationer - Byg F2 - Stueplan, Byg A OPG_3V_T32_ST_S - Side F2-4			Tegningsnr.:	Rev.:
				ISP2_K07_L2XX_H04_EXX_N931	
Projektnr.: 1019198	Dato: 2026-02-27	Rev. Dato:		Mål: 1 : 50	Side: F2-4
www.arteliagroup.dk	Fil:				

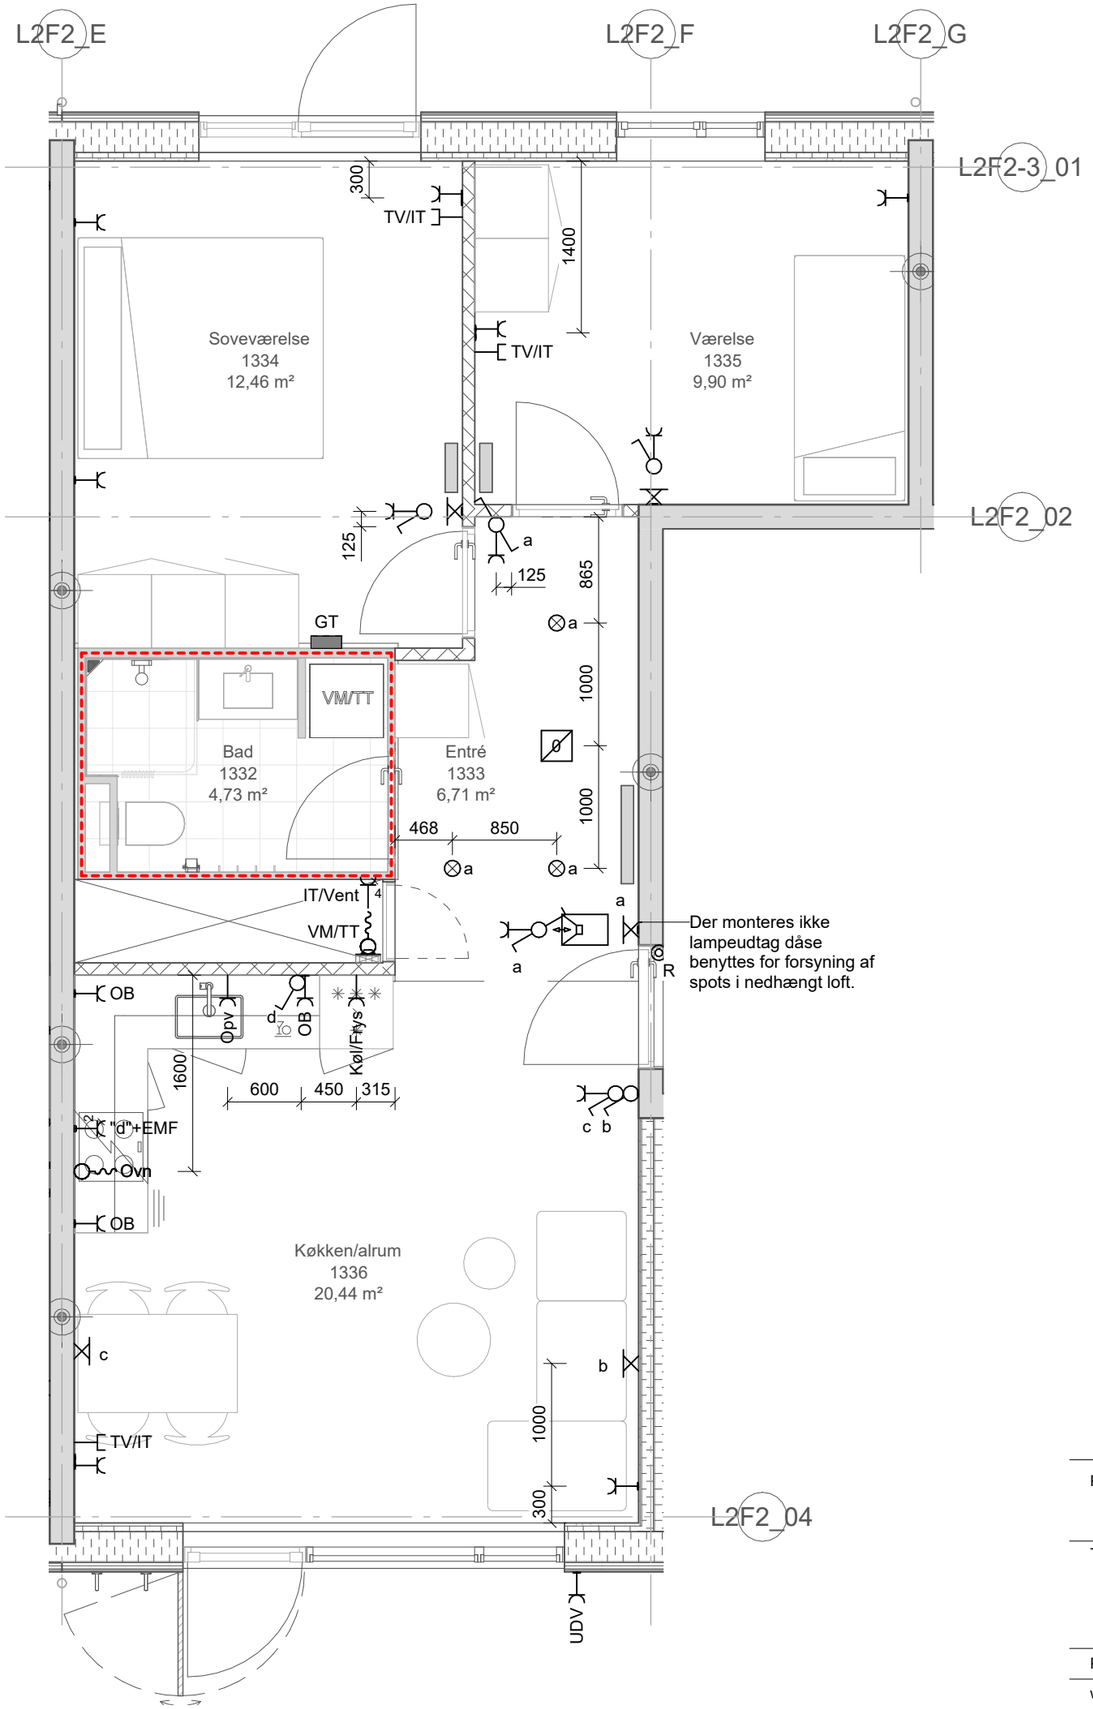

Projekt: Stejlepladsen


Tekst: Elinstallationer -
Byg F2 - Stueplan, Byg B
OPG_3V_T32_ST - Side F2-5

Tegningsnr.: ISP2_K07_L2XX_H04_EXX_N931

Rev.:

Projektnr.: 1019198 | Dato: 2026-02-27 | Rev. Dato: | Mål: 1 : 50 | Side: F2-5

www.arteliagroup.dk | Fil:

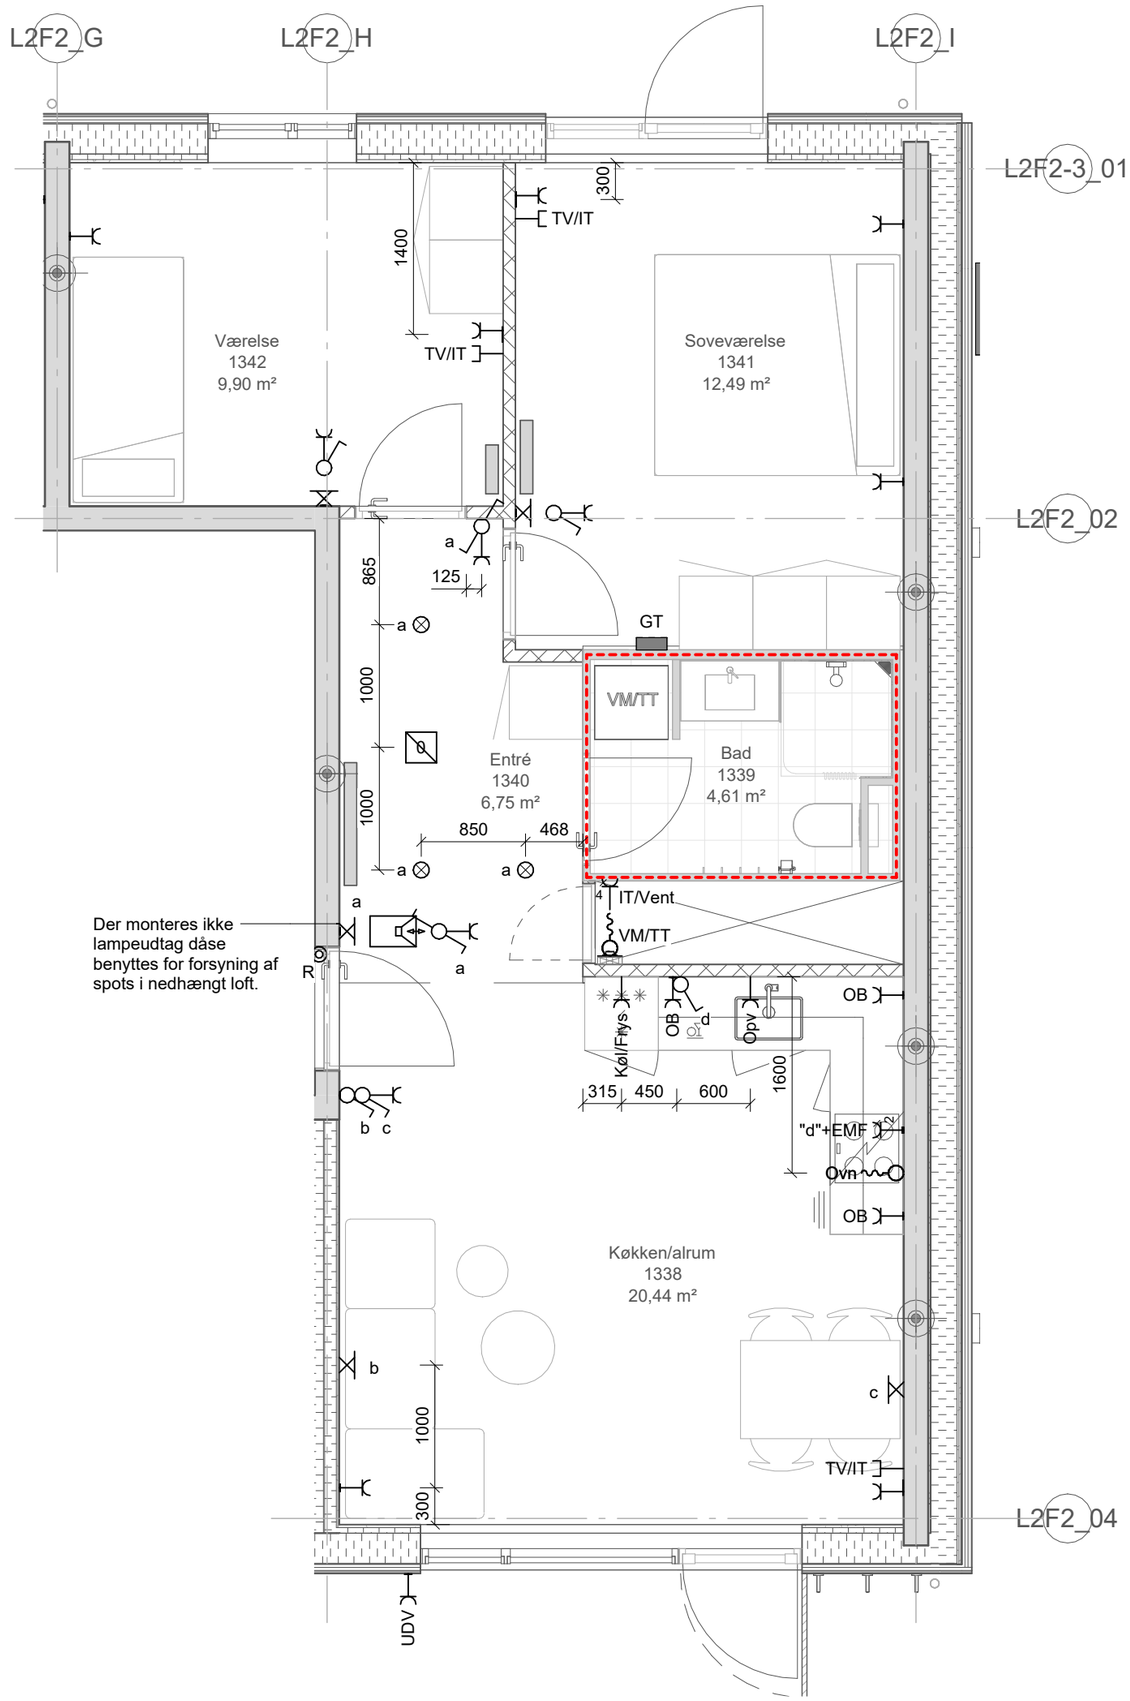

Projekt: Stejlepladsen


Tekst: Elinstallationer -
Byg F2 - Stueplan, Byg B
OPG_3V_T32_ST_S - Side F2-6

Tegningsnr.: ISP2_K07_L2XX_H04_EXX_N931

Rev.:

Projektnr.: 1019198 | Dato: 2026-02-27 | Rev. Dato: | Mål: 1 : 50 | Side: F2-6

www.arteliagroup.dk | Fil:

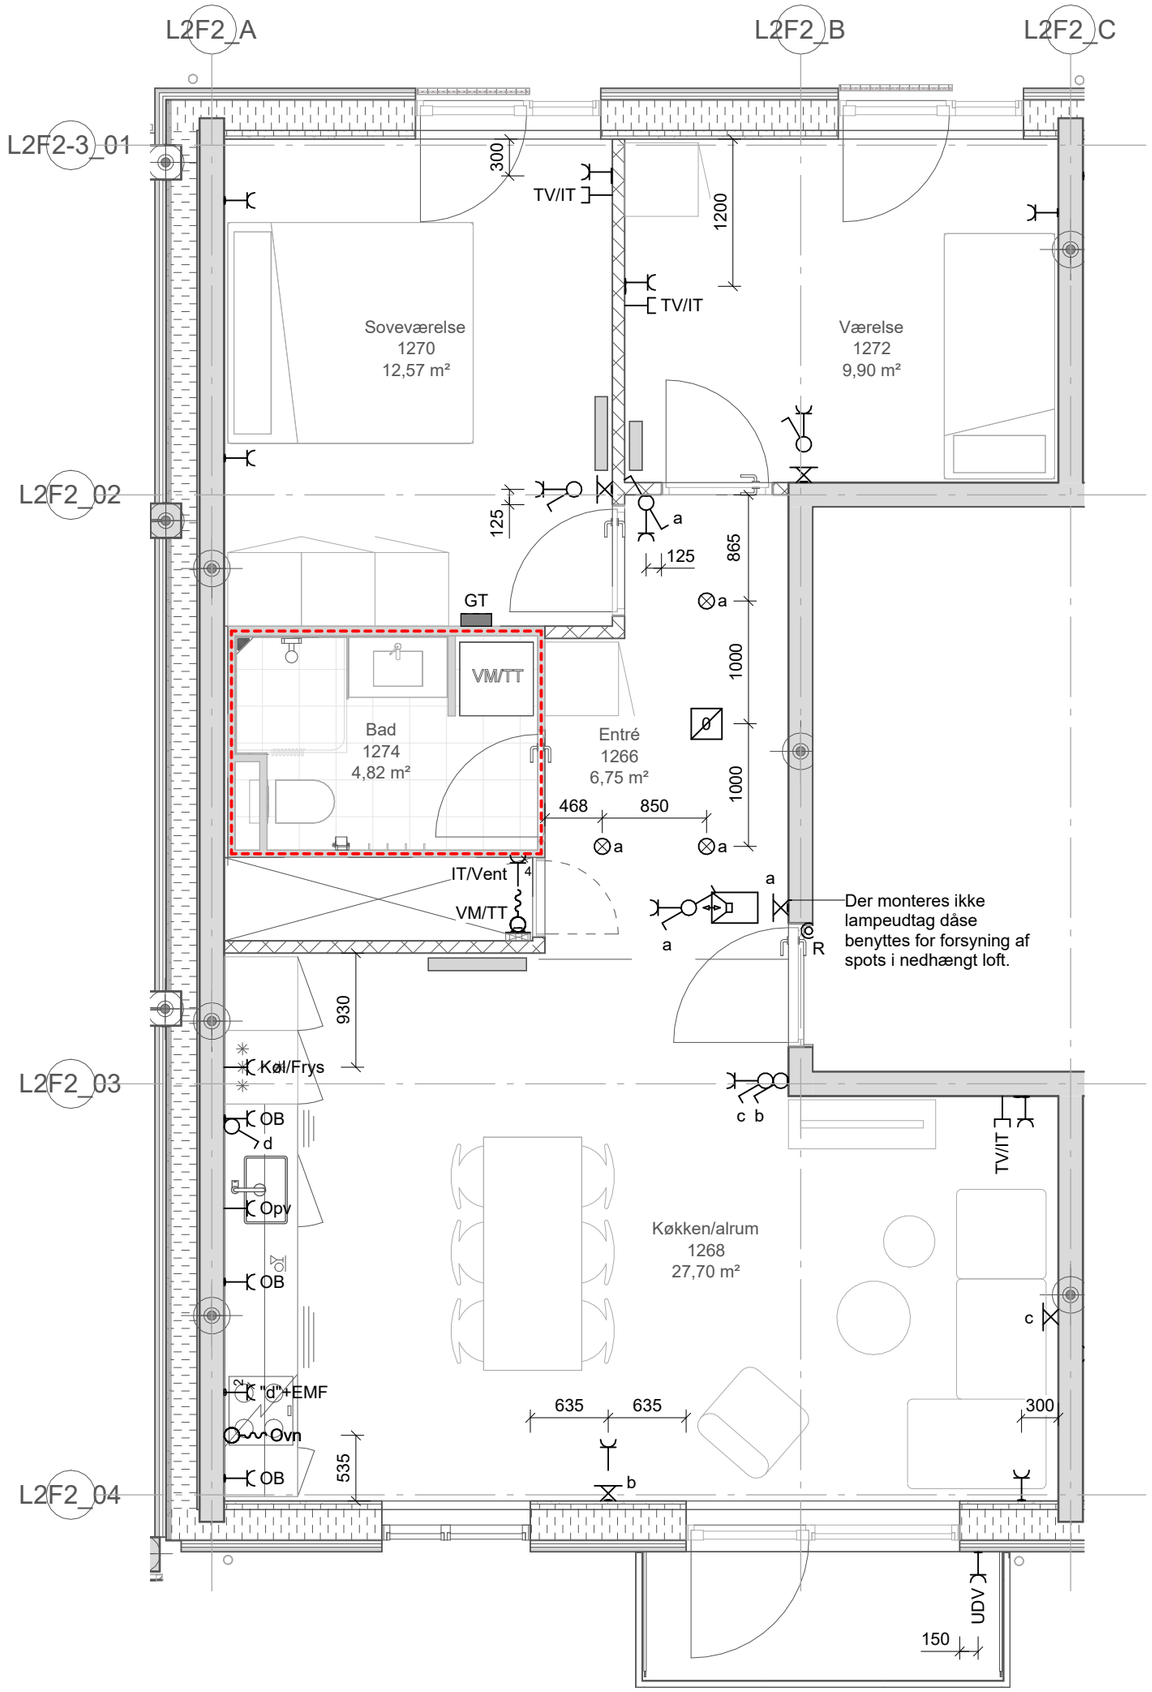

Projekt: Stejlepladsen


Tekst: Elinstallationer -
Byg F2 - 1. Sal, Byg A
OPG_3V_T30 - Side F2-7

Tegningsnr.: ISP2_K07_L2XX_H04_EXX_N931


Rev.:

Projektnr.: 1019198 | Dato: 2026-02-27 | Rev. Dato: | Mål: 1 : 50 | Side: F2-7


www.arteliagroup.dk | Fil:

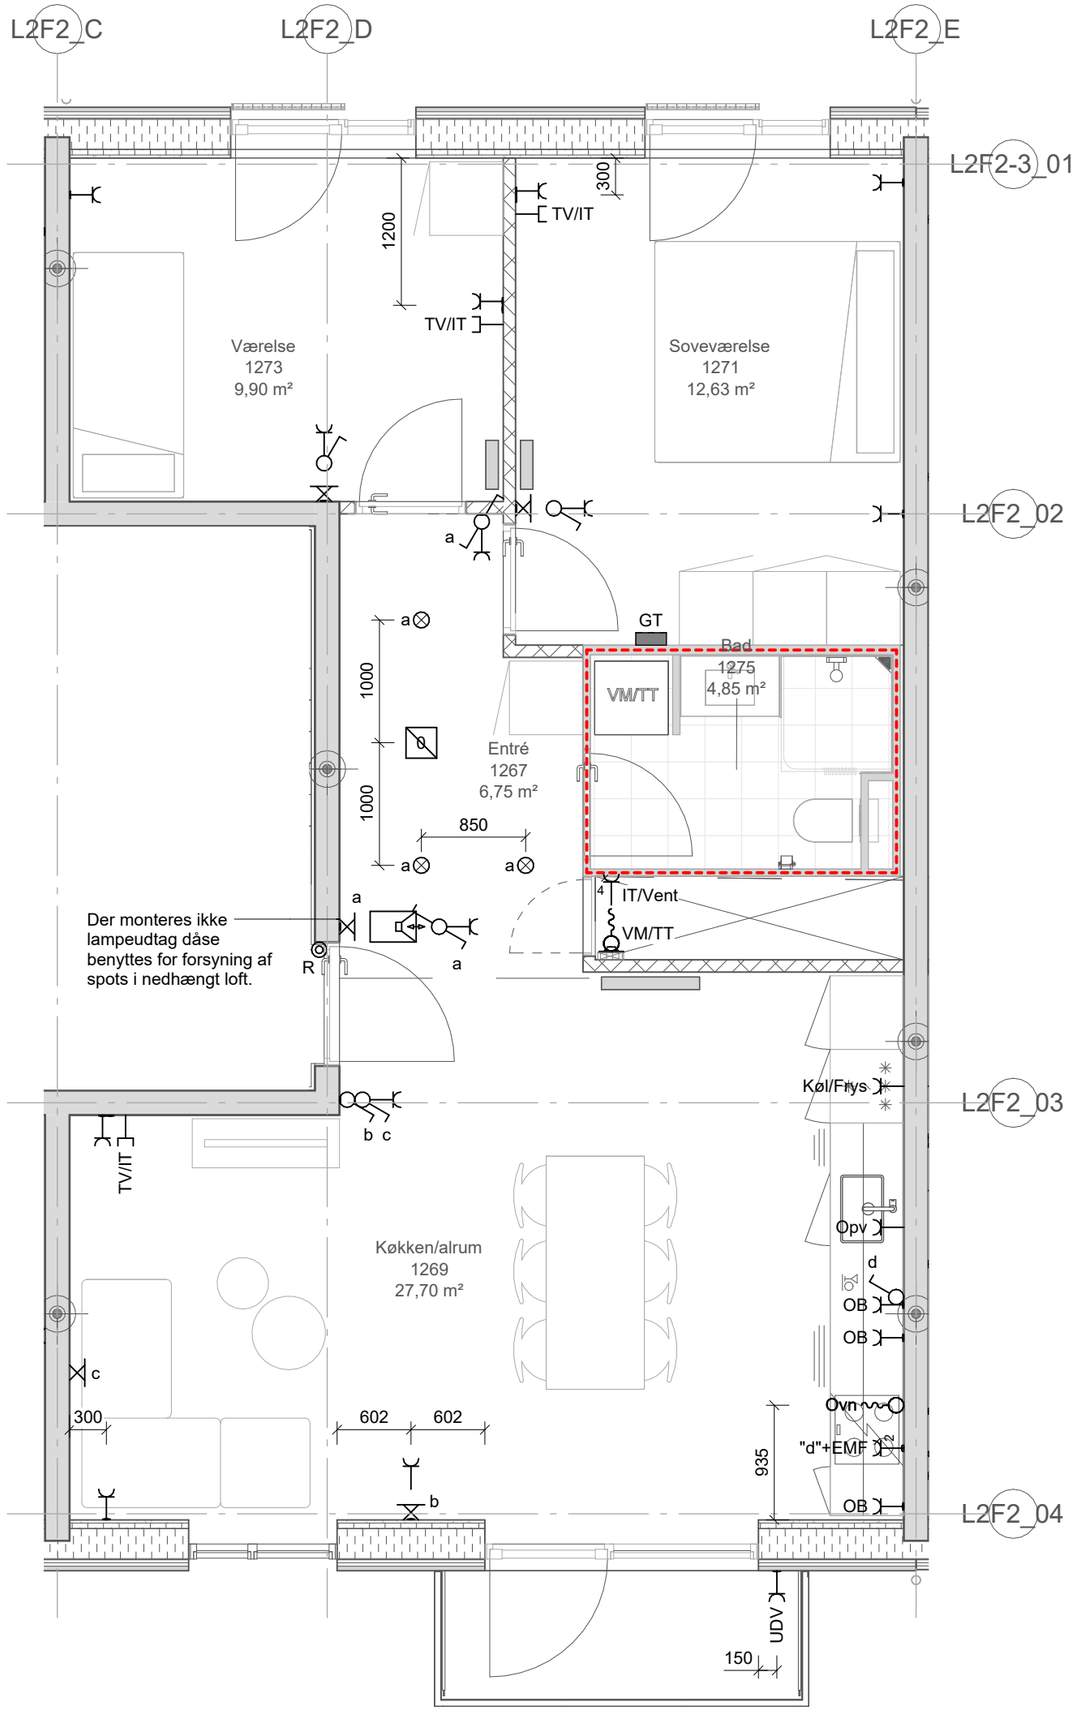


Projekt:	Stejlepladsen				
Tekst:	Elinstallationer - Byg F2 - 1. Sal, Byg A OPG_3V_T30_S - Side F2-8			Tegningsnr.:	Rev.:
			ISP2_K07_L2XX_H04_EFX_N931		
Projektnr.: 1019198	Dato: 2026-02-27	Rev. Dato:		Mål: 1 : 50	Side: F2-8
www.arteliagroup.dk	Fil:				

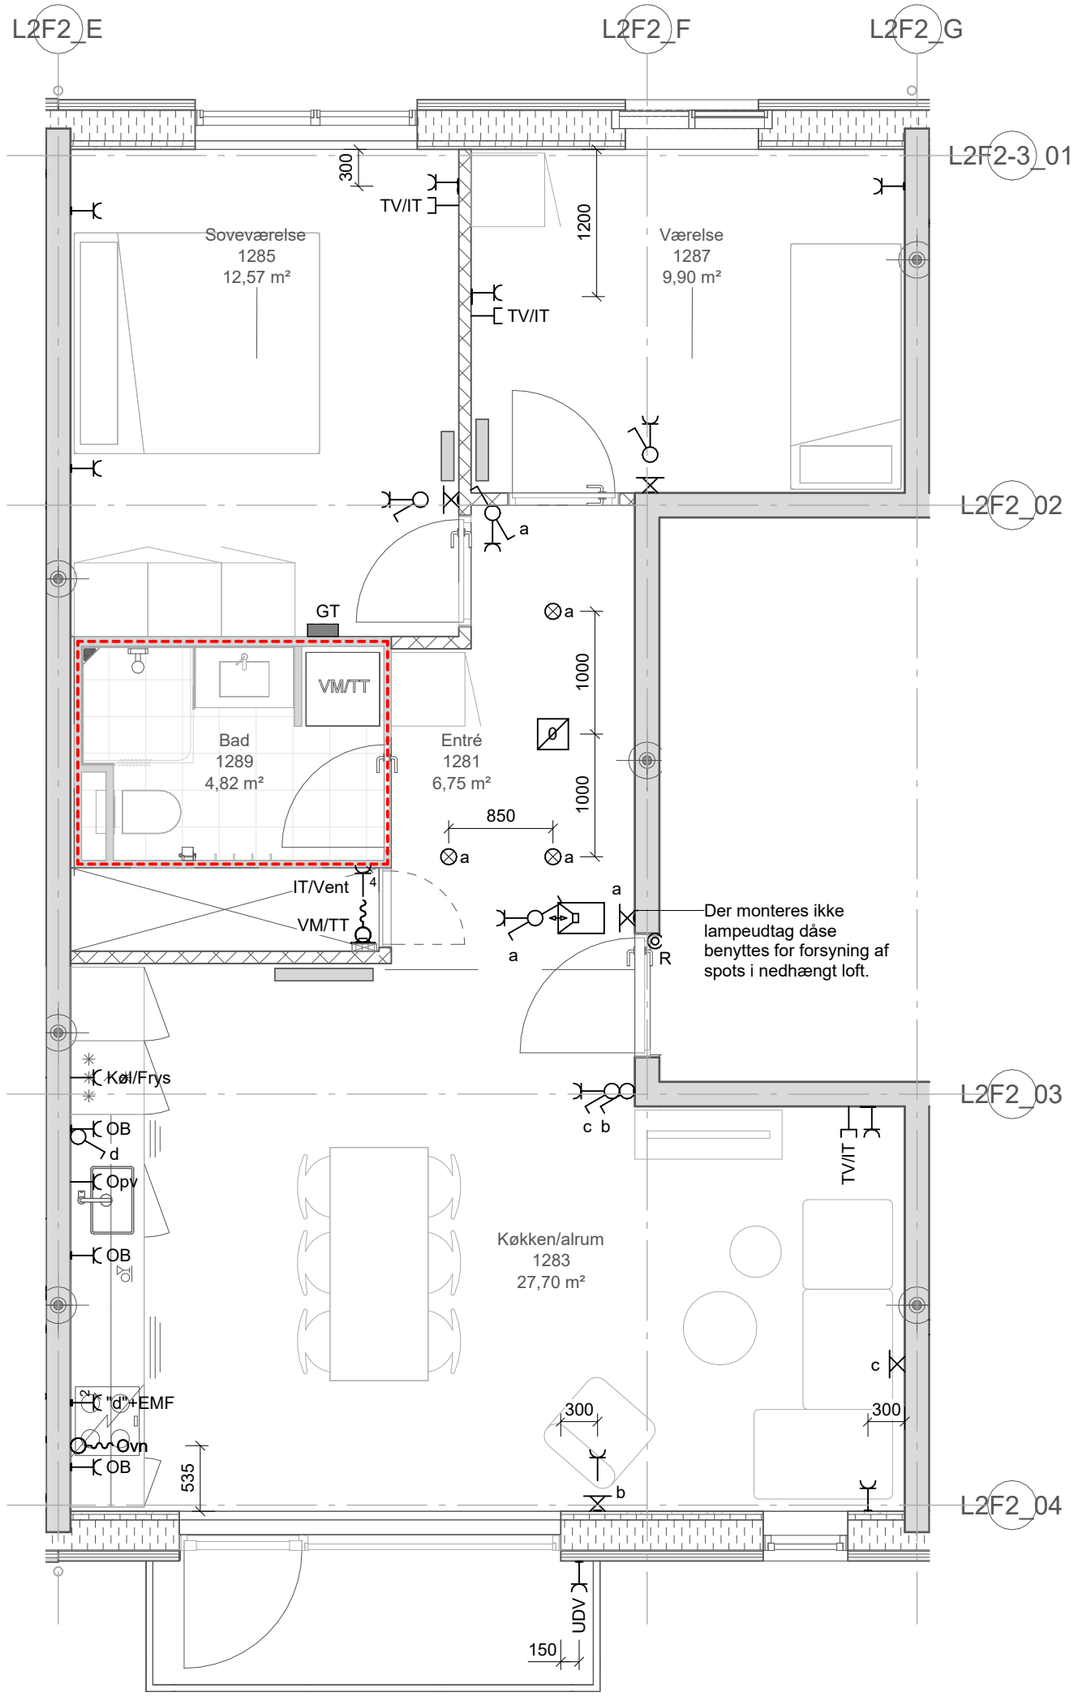

Projekt:	Stejlepladsen				
Tekst:	Elinstallationer - Byg F2 - 1. Sal, Byg B OPG_3V_T30 - Side F2-9			Tegningsnr.:	Rev.:
				ISP2_K07_L2XX_H04_EFX_N931	
Projektnr.: 1019198	Dato: 2026-02-27	Rev. Dato:		Mål: 1 : 50	Side: F2-9
www.arteliagroup.dk	Fil:				

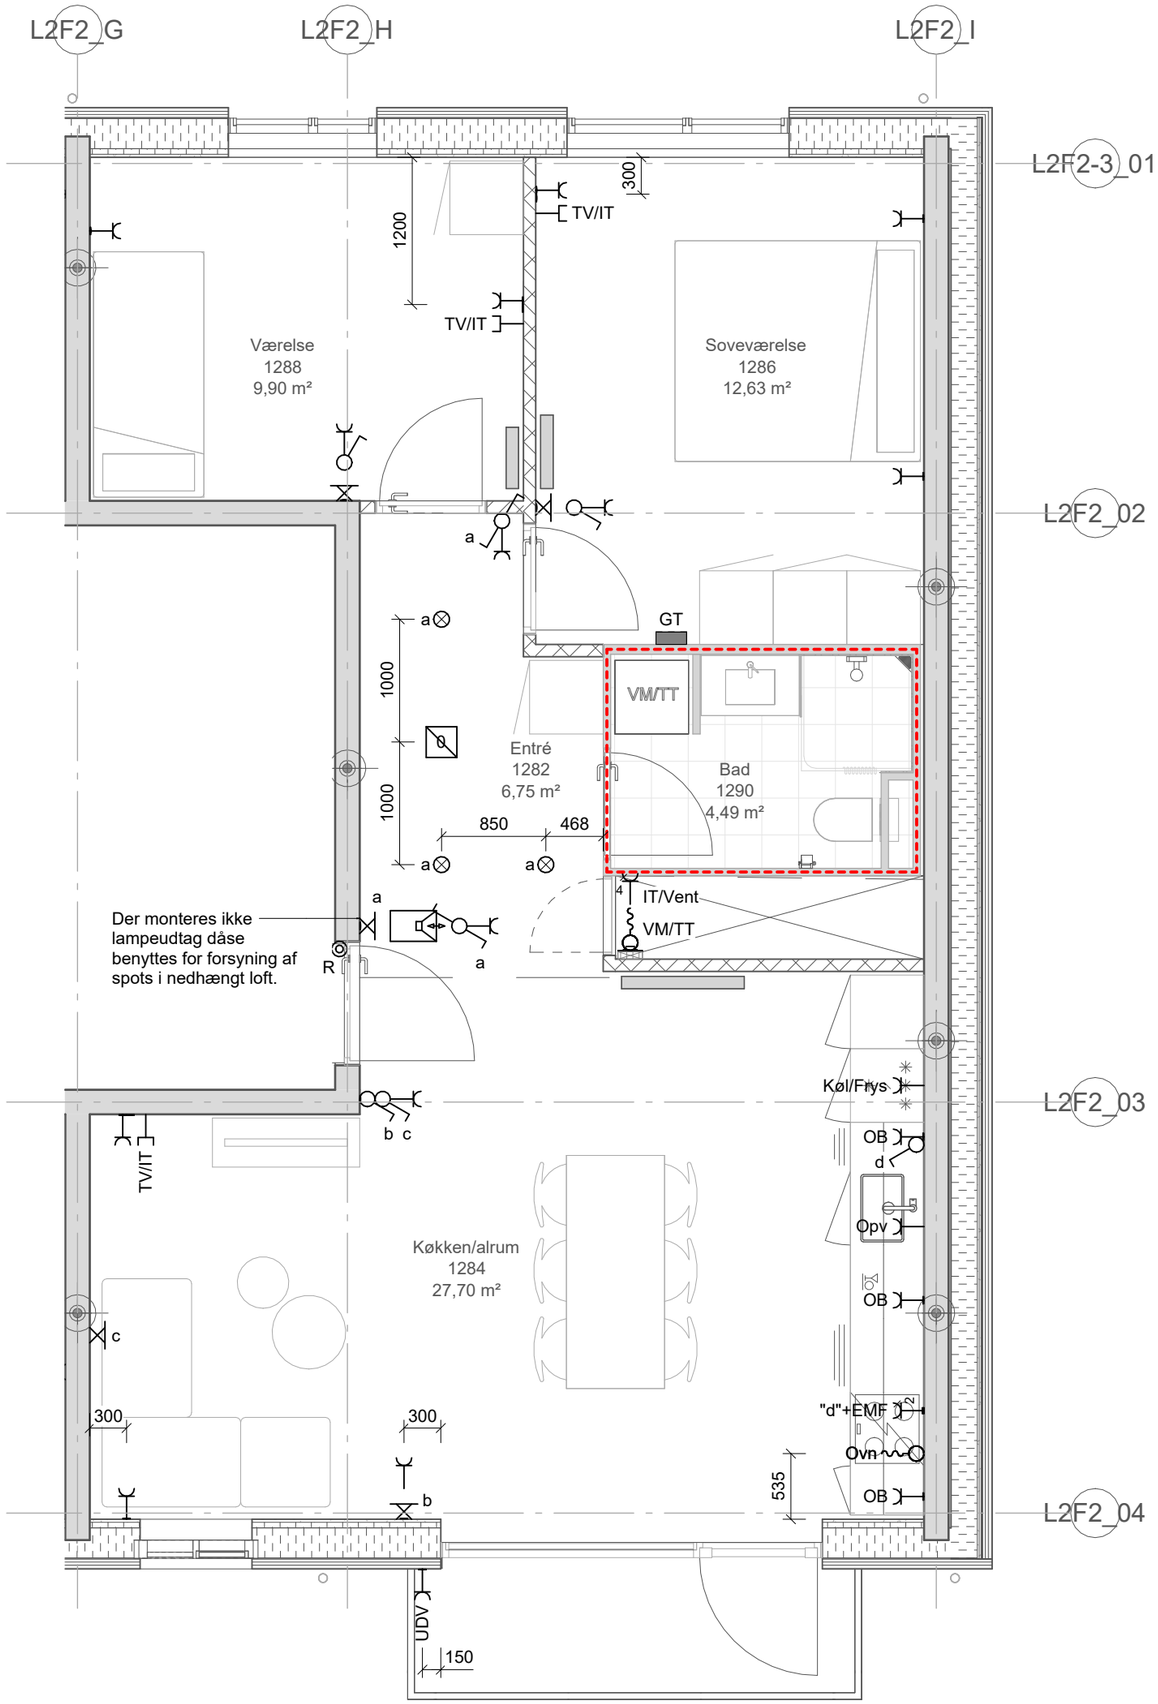

Projekt:	Stejlepladsen				
Tekst:	Elinstallationer - Byg F2 - 1. Sal, Byg B OPG_3V_T30_S - Side F2-10			Tegningsnr.:	Rev.:
				ISP2_K07_L2XX_H04_EFX_N931	
Projektnr.: 1019198	Dato: 2026-02-27	Rev. Dato:		Mål: 1 : 50	Side: F2-10
www.arteliagroup.dk	Fil:				

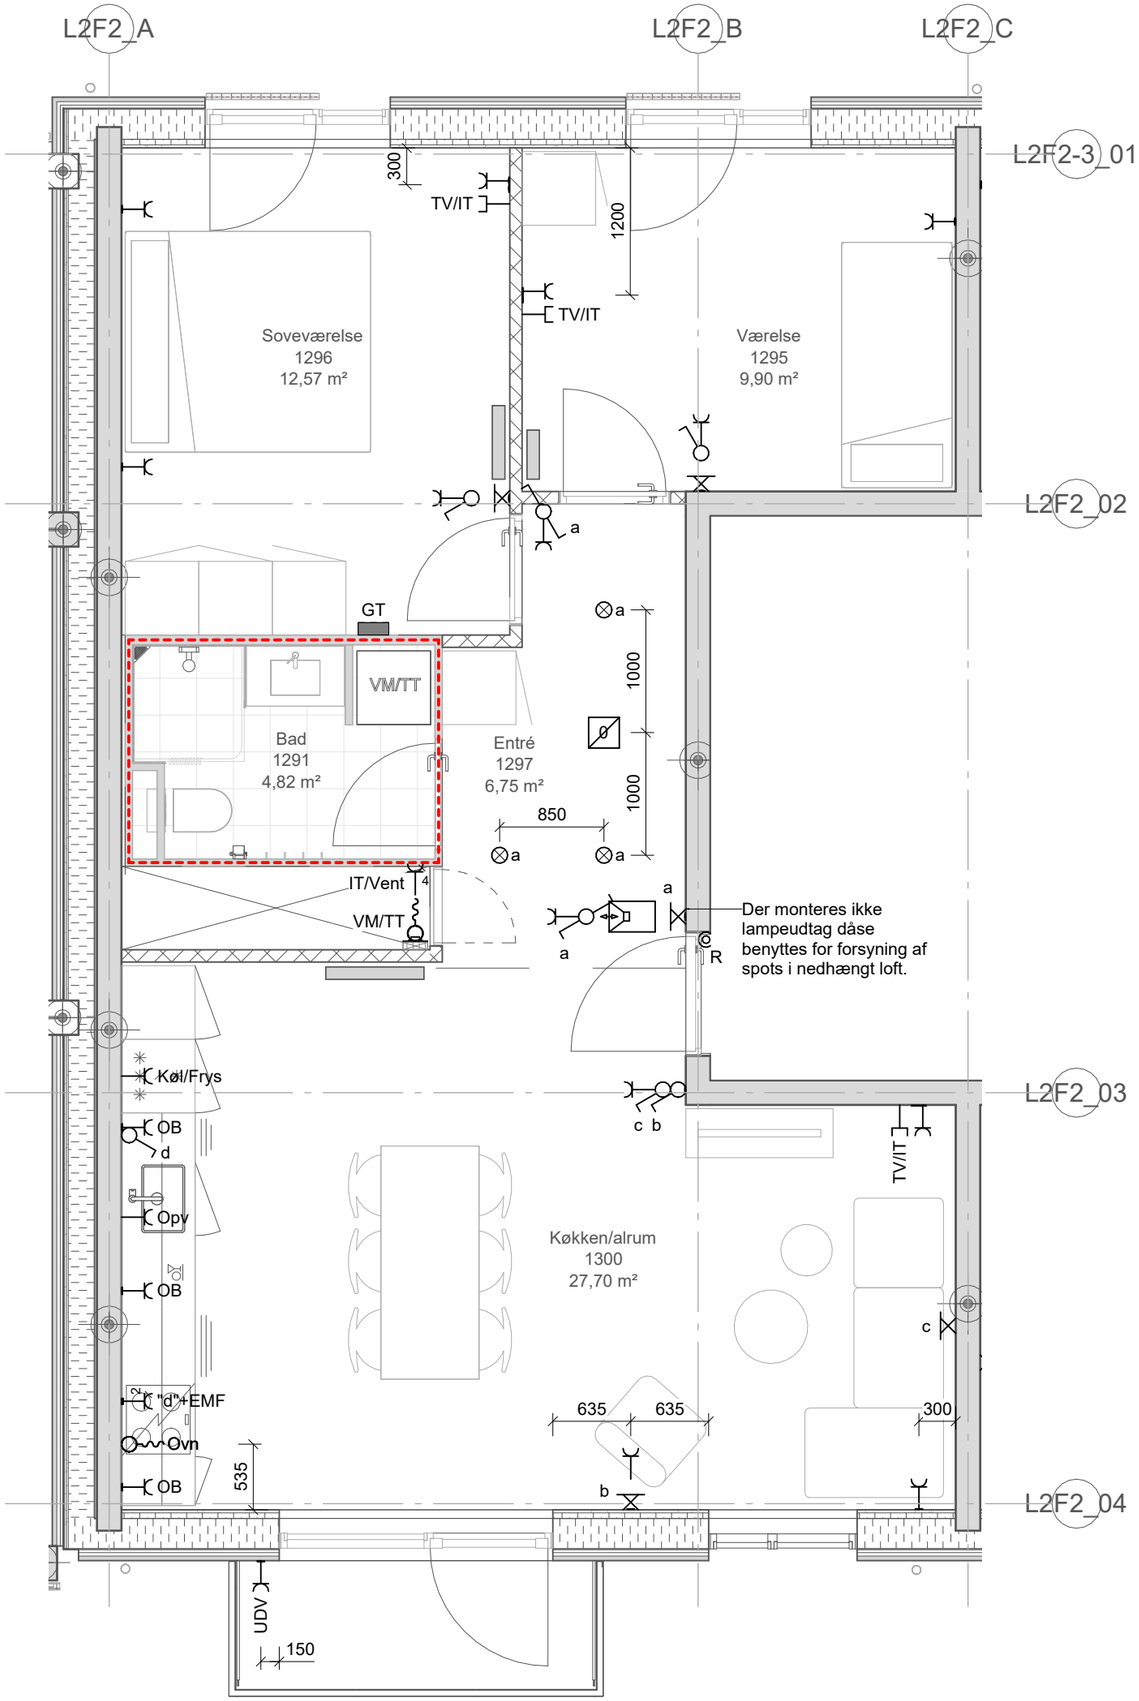

Projekt: Stejlepladsen

ARTELIA


Tekst: Elinstallationer -
Byg F2 - 2. Sal, Byg A
OPG_3V_T30 - Side F2-11

Tegningsnr.: ISP2_K07_L2XX_H04_EFX_N931

Rev.:


Projektnr.: 1019198 | Dato: 2026-02-27 | Rev. Dato: | Mål: 1 : 50 | Side: F2-11

www.arteliagroup.dk | Fil:

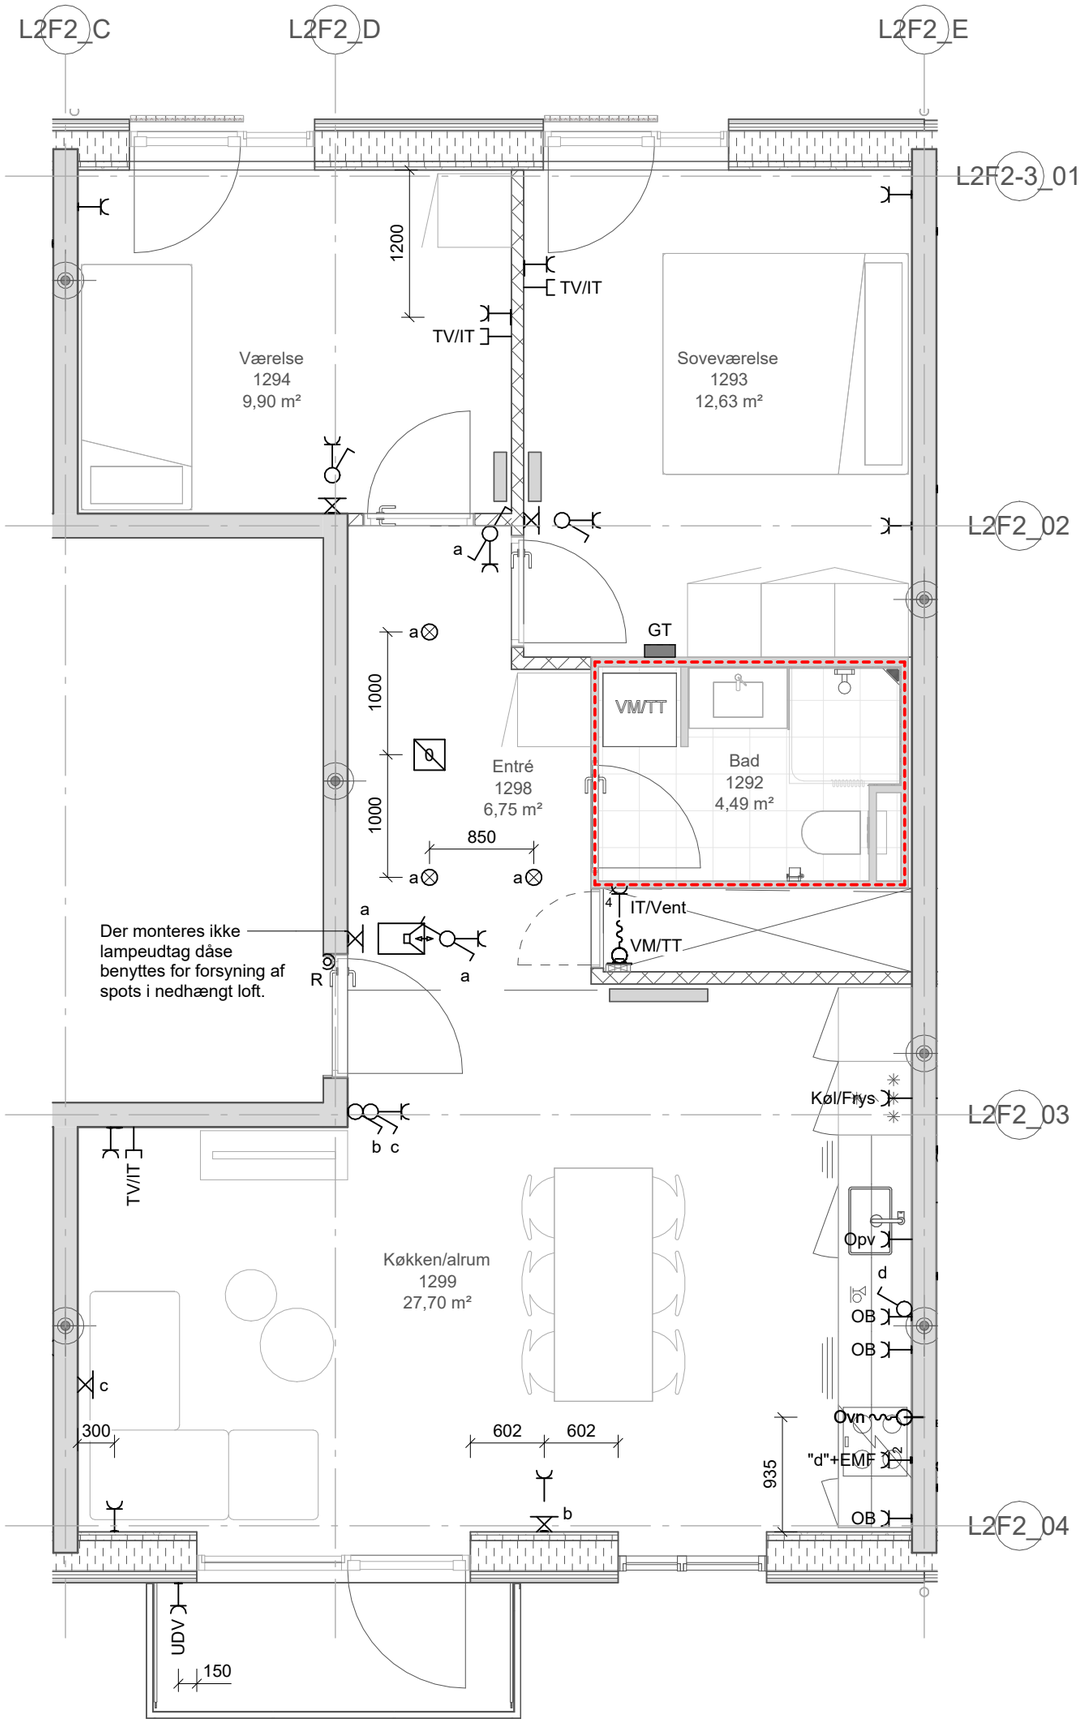

Projekt:	Stejlepladsen		
Tekst:	Elinstallationer - Byg F2 - 2. Sal, Byg A OPG_3V_T30_S - Side F2-12	Tegningsnr.:	ISP2_K07_L2XX_H04_EFX_N931
		Rev.:	

Projektnr.: 1019198	Dato: 2026-02-27	Rev. Dato:	Mål: 1 : 50	Side: F2-12
www.arteliagroup.dk	Fil:			

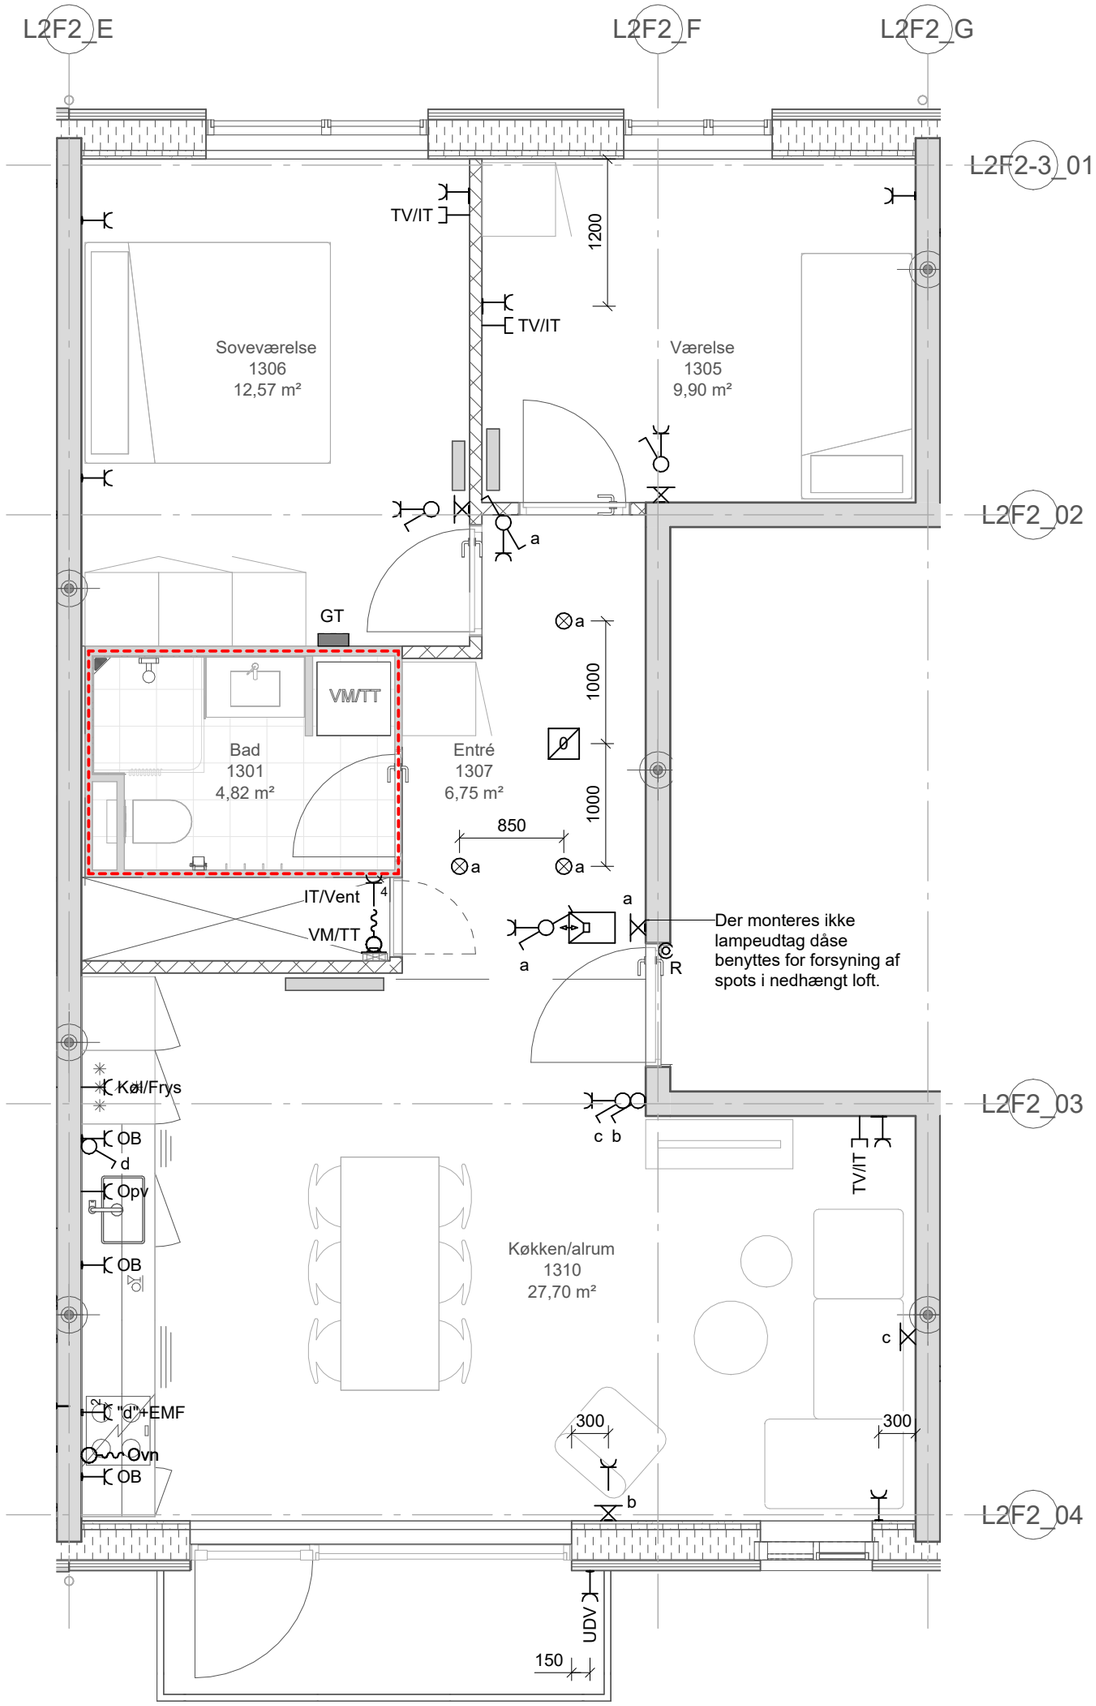

Projekt: Stejlepladsen


Tekst: Elinstallationer -
Byg F2 - 2. Sal, Byg B
OPG_3V_T30 - Side F2-13

Tegningsnr.: ISP2_K07_L2XX_H04_EFX_N931


Rev.:

Projektnr.: 1019198 | Dato: 2026-02-27 | Rev. Dato: | Mål: 1 : 50 | Side: F2-13

www.arteliagroup.dk | Fil:

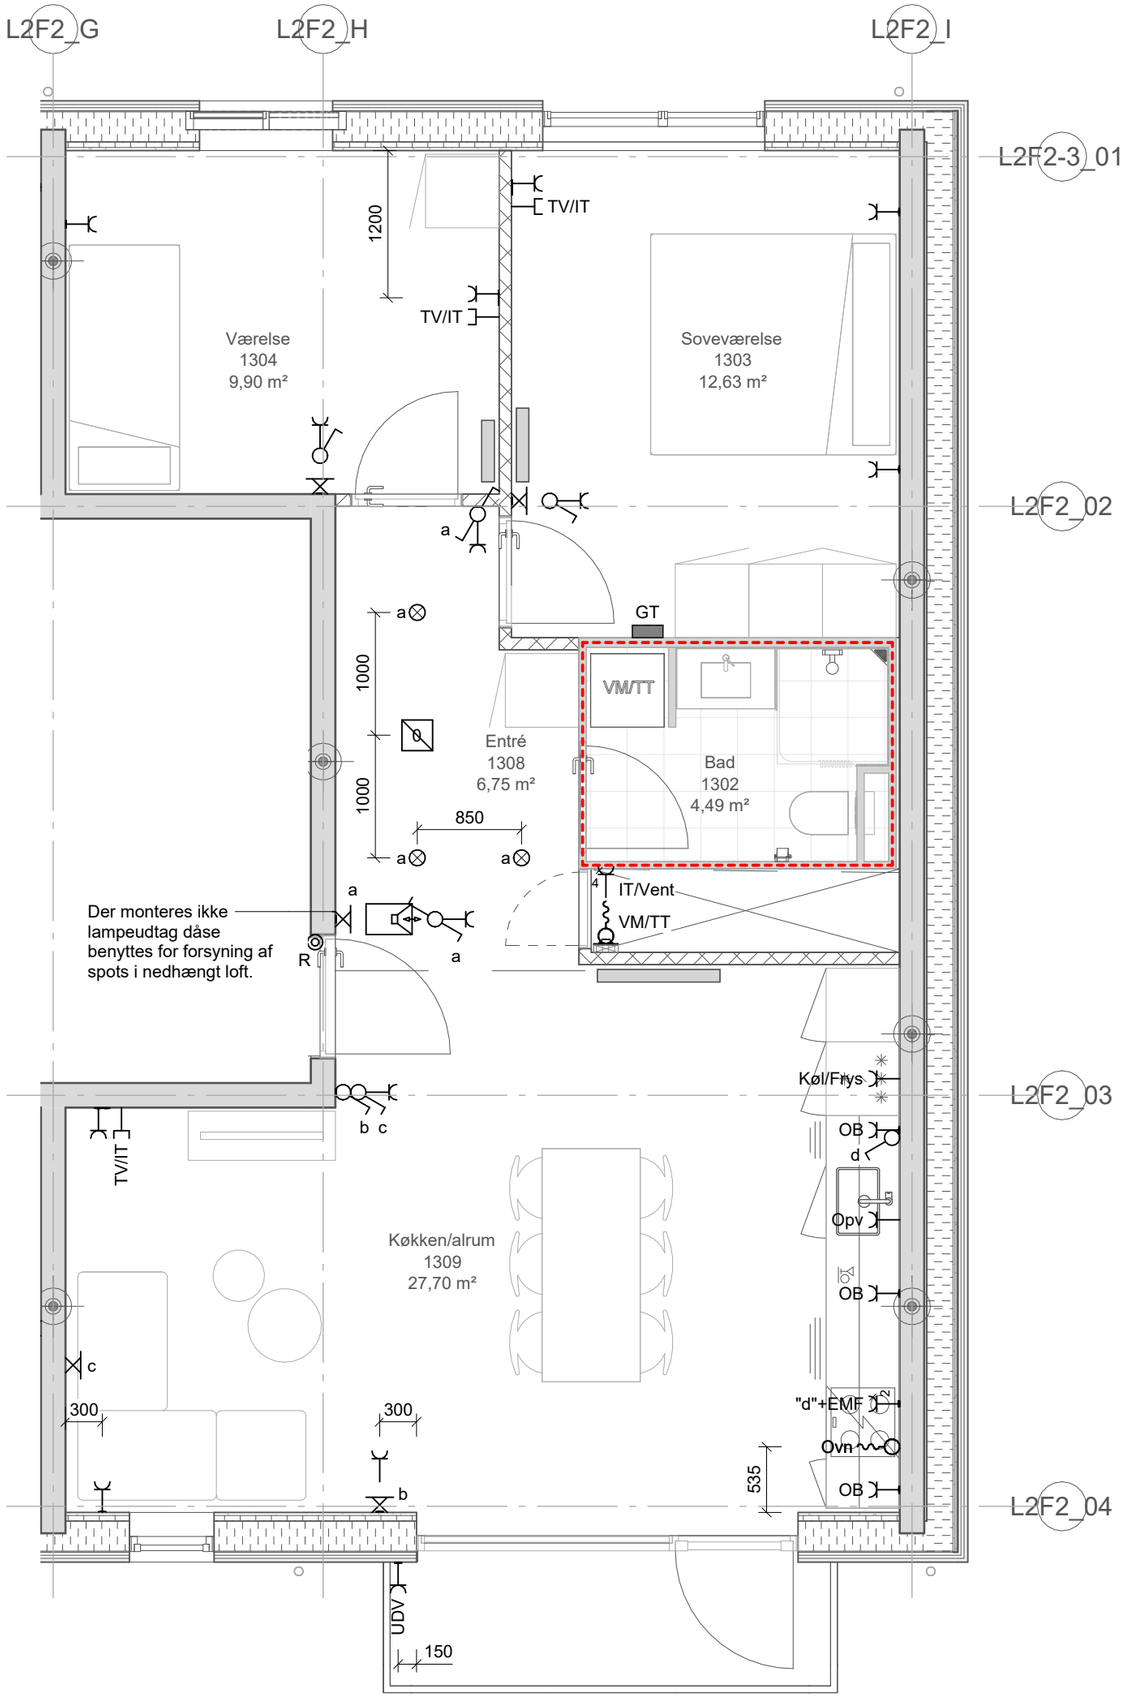

Projekt:	Stejlepladsen				
Tekst:	Elinstallationer - Byg F2 - 2. Sal, Byg B OPG_3V_T30_S - Side F2-14			Tegningsnr.:	Rev.:
				ISP2_K07_L2XX_H04_EFX_N931	
Projektnr.: 1019198	Dato: 2026-02-27	Rev. Dato:		Mål: 1 : 50	Side: F2-14
www.arteliagroup.dk	Fil:				

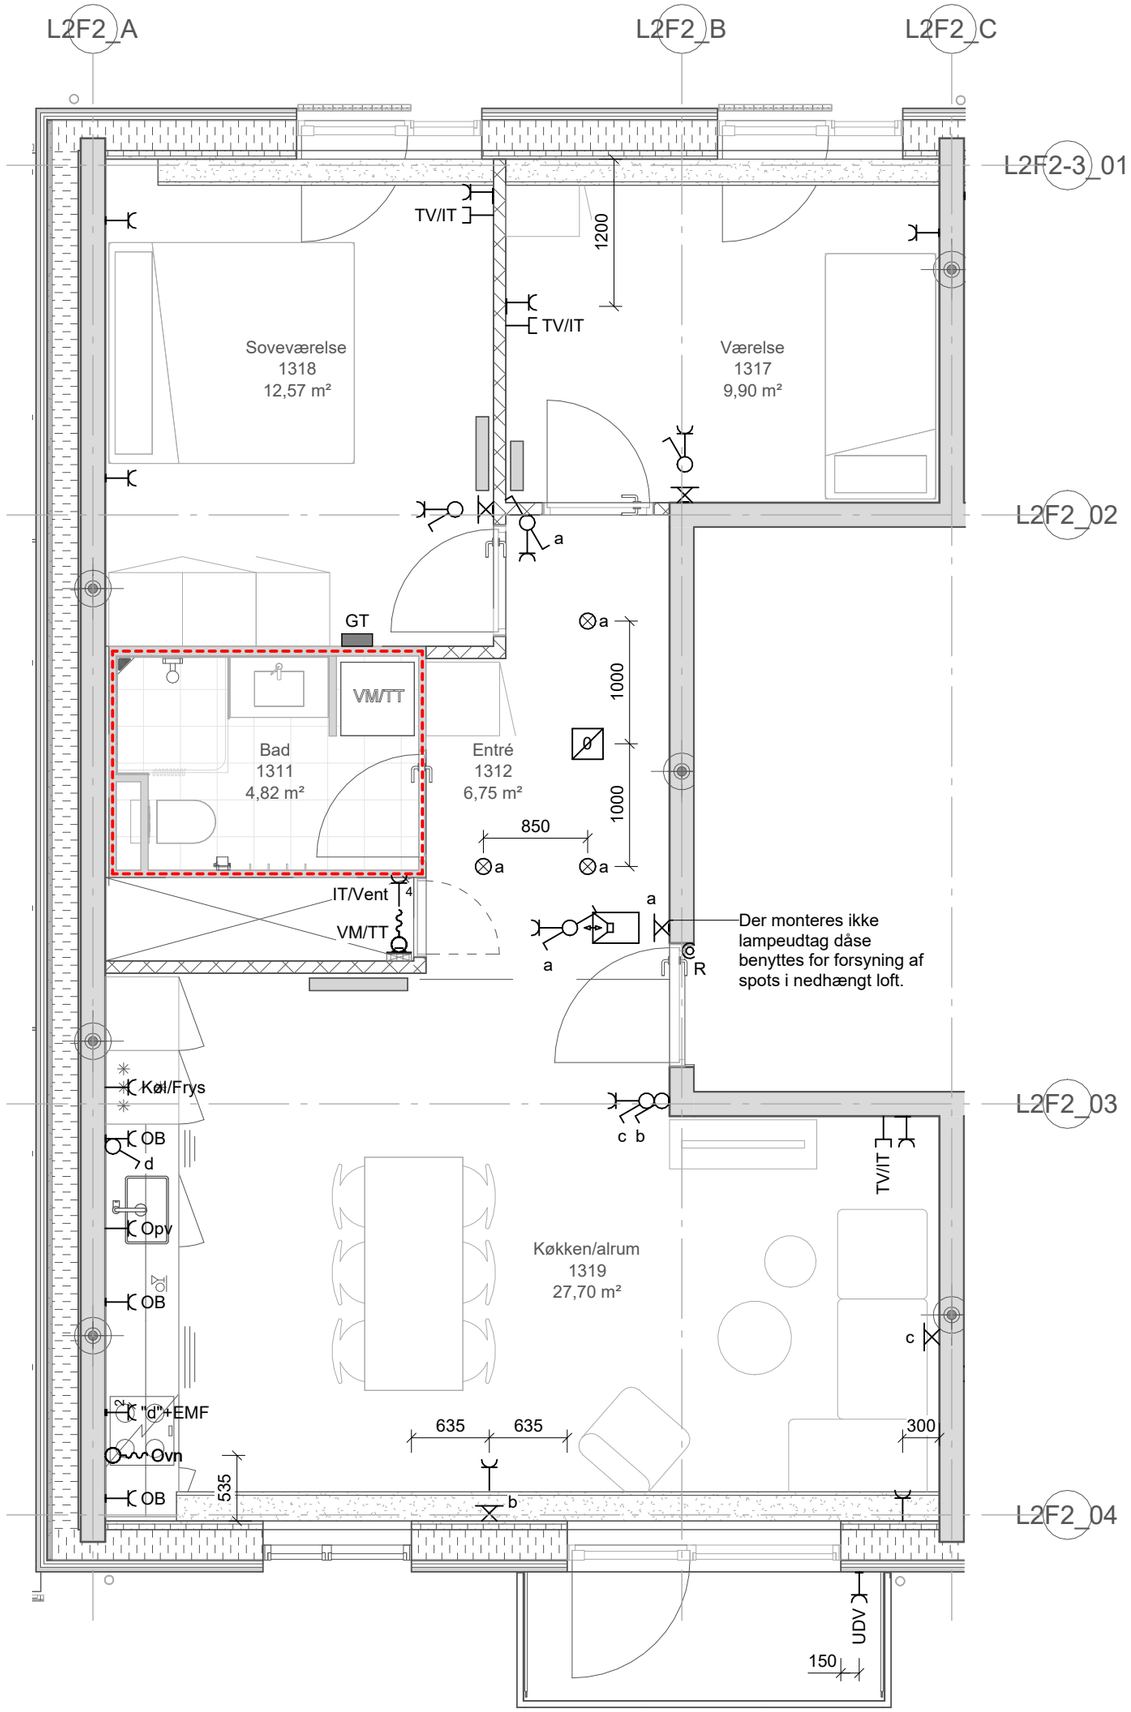

Projekt: Stejlepladsen


Tekst: Elinstallationer -
Byg F2 - 3. Sal, Byg A
OPG_3V_T30 - Side F2-15

Tegningsnr.: ISP2_K07_L2XX_H04_EFX_N931


Rev.:

Projektnr.: 1019198 | Dato: 2026-02-27 | Rev. Dato: | Mål: 1 : 50 | Side: F2-15

www.arteliagroup.dk | Fil:

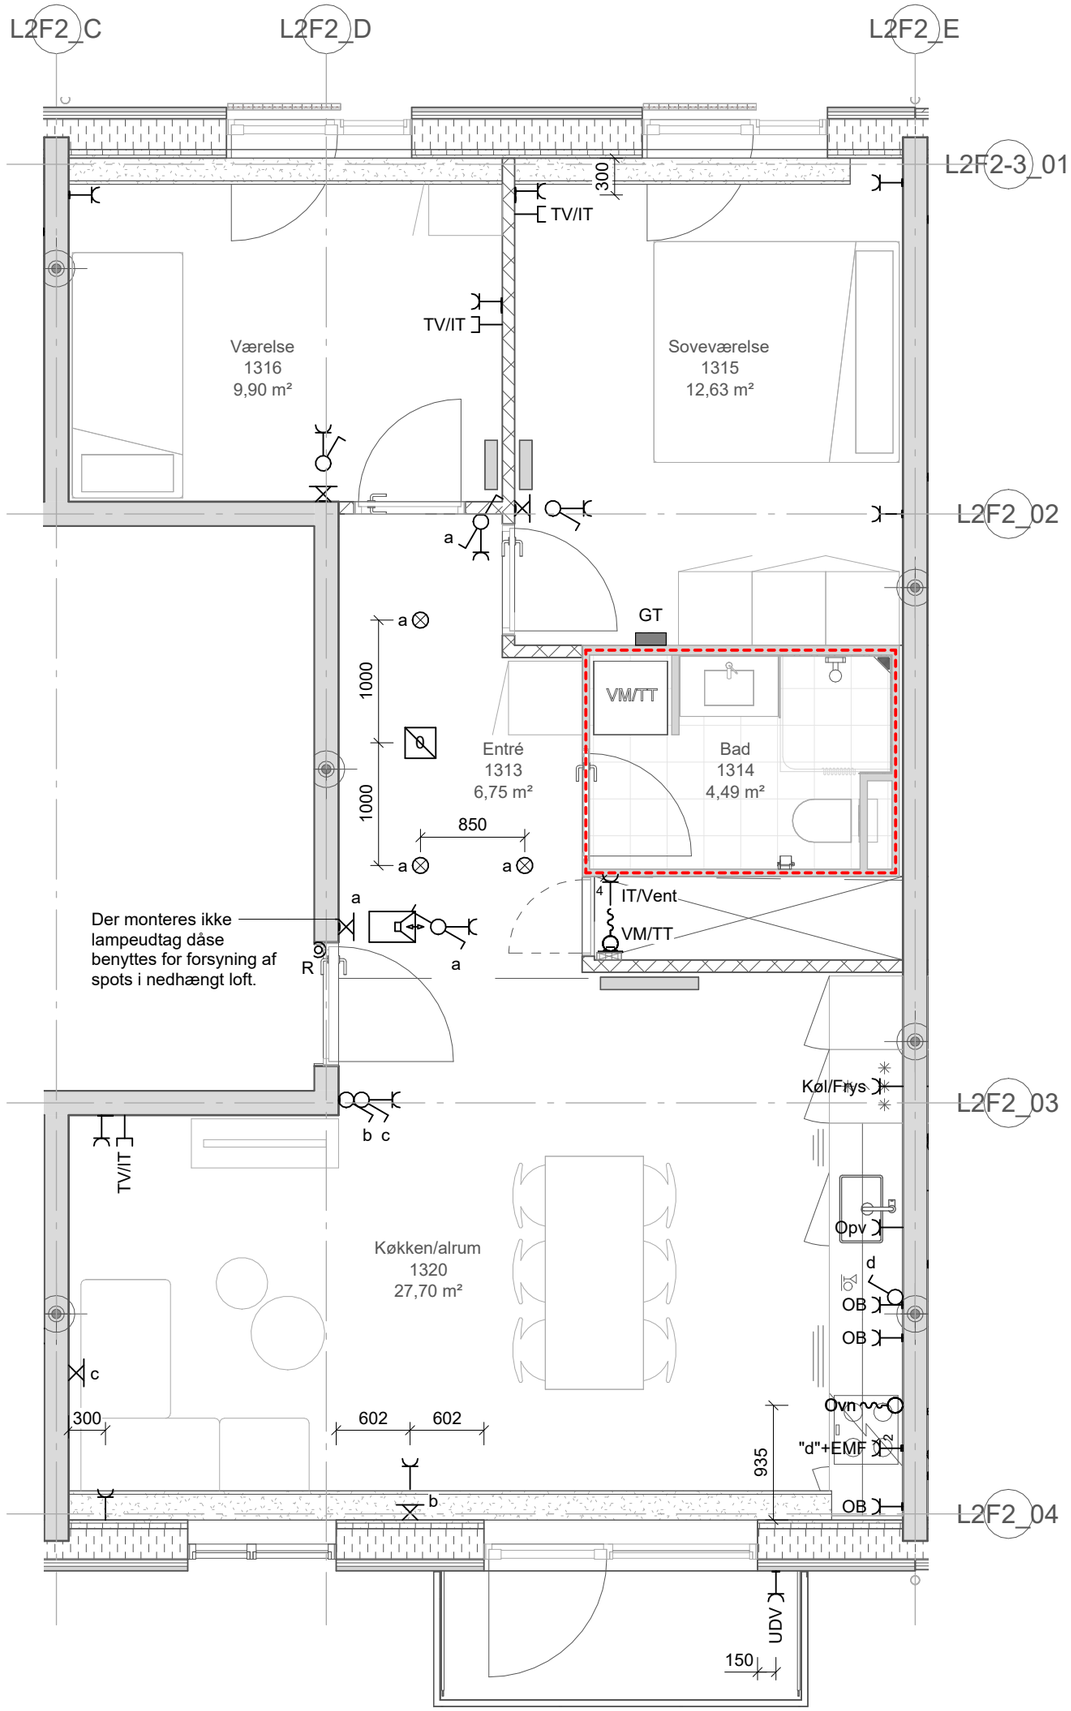

Projekt:	Stejlepladsen				
Tekst:	Elinstallationer - Byg F2 - 3. Sal, Byg A OPG_3V_T30_S - Side F2-16			Tegningsnr.:	Rev.:
			ISP2_K07_L2XX_H04_EFX_N931		
Projektnr.: 1019198	Dato: 2026-02-27	Rev. Dato:		Mål: 1 : 50	Side: F2-16
www.arteliagroup.dk	Fil:				

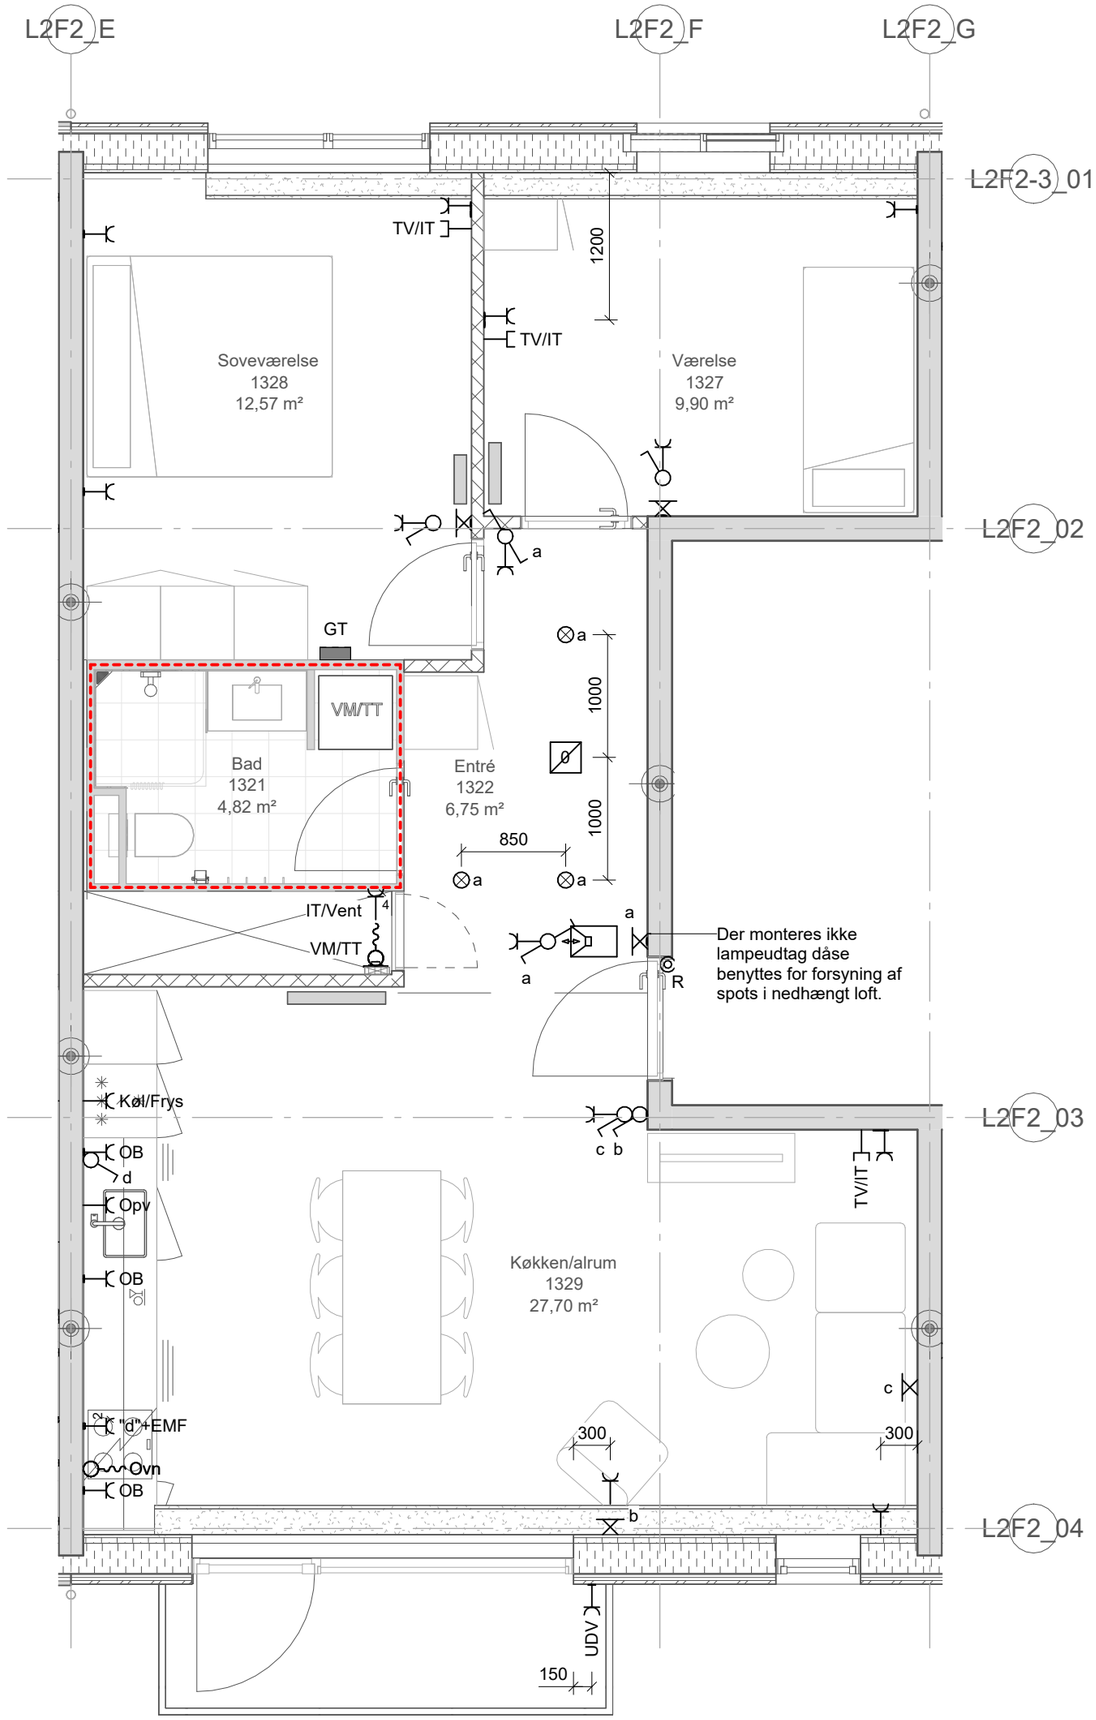

Projekt: Stejlepladsen


Tekst: Elinstallationer -
Byg F2 - 3. Sal, Byg B
OPG_3V_T30 - Side F2-17

Tegningsnr.: ISP2_K07_L2XX_H04_EFX_N931


Rev.:

Projektnr.: 1019198 | Dato: 2026-02-27 | Rev. Dato: | Mål: 1 : 50 | Side: F2-17


www.arteliagroup.dk | Fil:

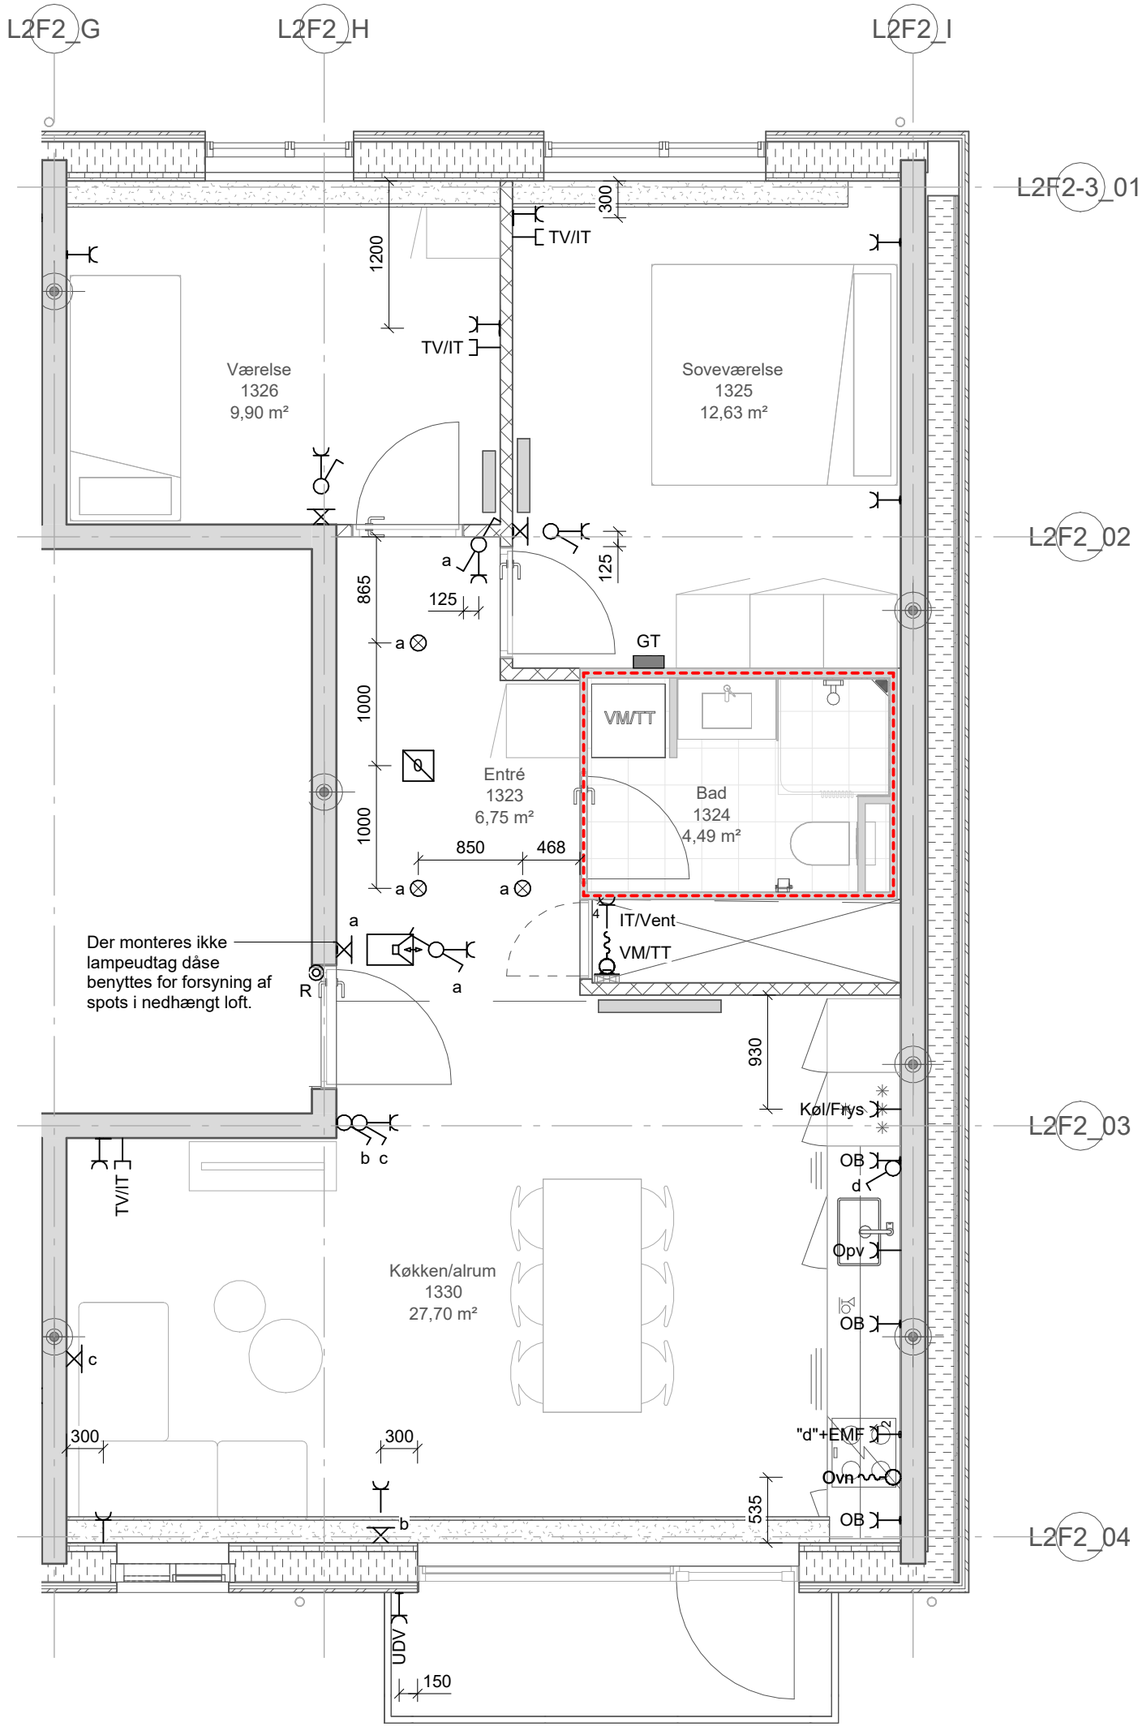

Projekt:	Stejlepladsen				
Tekst:	Elinstallationer - Byg F2 - 3. Sal, Byg B OPG_3V_T30_S - Side F2-18			Tegningsnr.:	Rev.:
				ISP2_K07_L2XX_H04_EFX_N931	
Projektnr.: 1019198	Dato: 2026-02-27	Rev. Dato:		Mål: 1 : 50	Side: F2-18
www.arteliagroup.dk	Fil:				

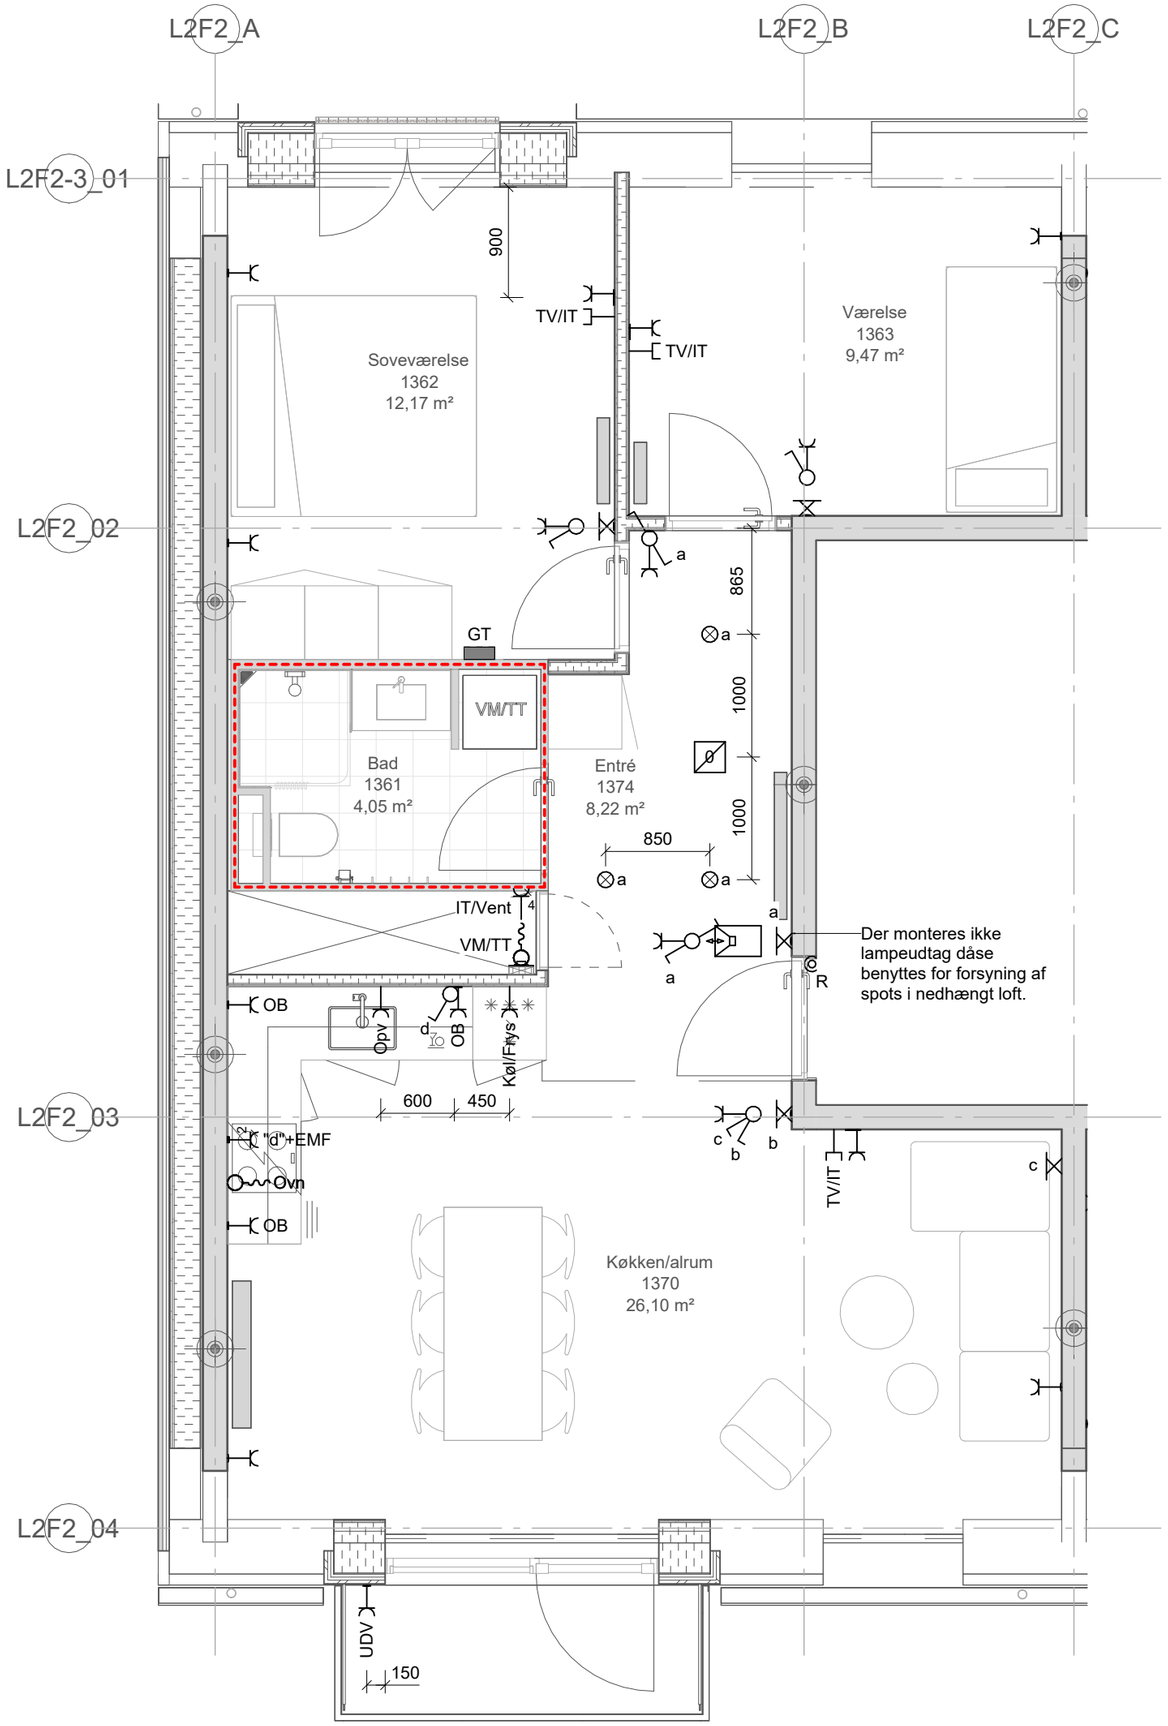

Projekt:	Stejlepladsen				
Tekst:	Elinstallationer - Byg F2 - 4. Sal, Byg A OPG_3V_T31_TA - Side F2-19			Tegningsnr.:	Rev.:
				ISP2_K07_L2XX_H04_EXX_N931	
Projektnr.: 1019198	Dato: 2026-02-27	Rev. Dato:		Mål: 1 : 50	Side: F2-19
www.arteliagroup.dk	Fil:				

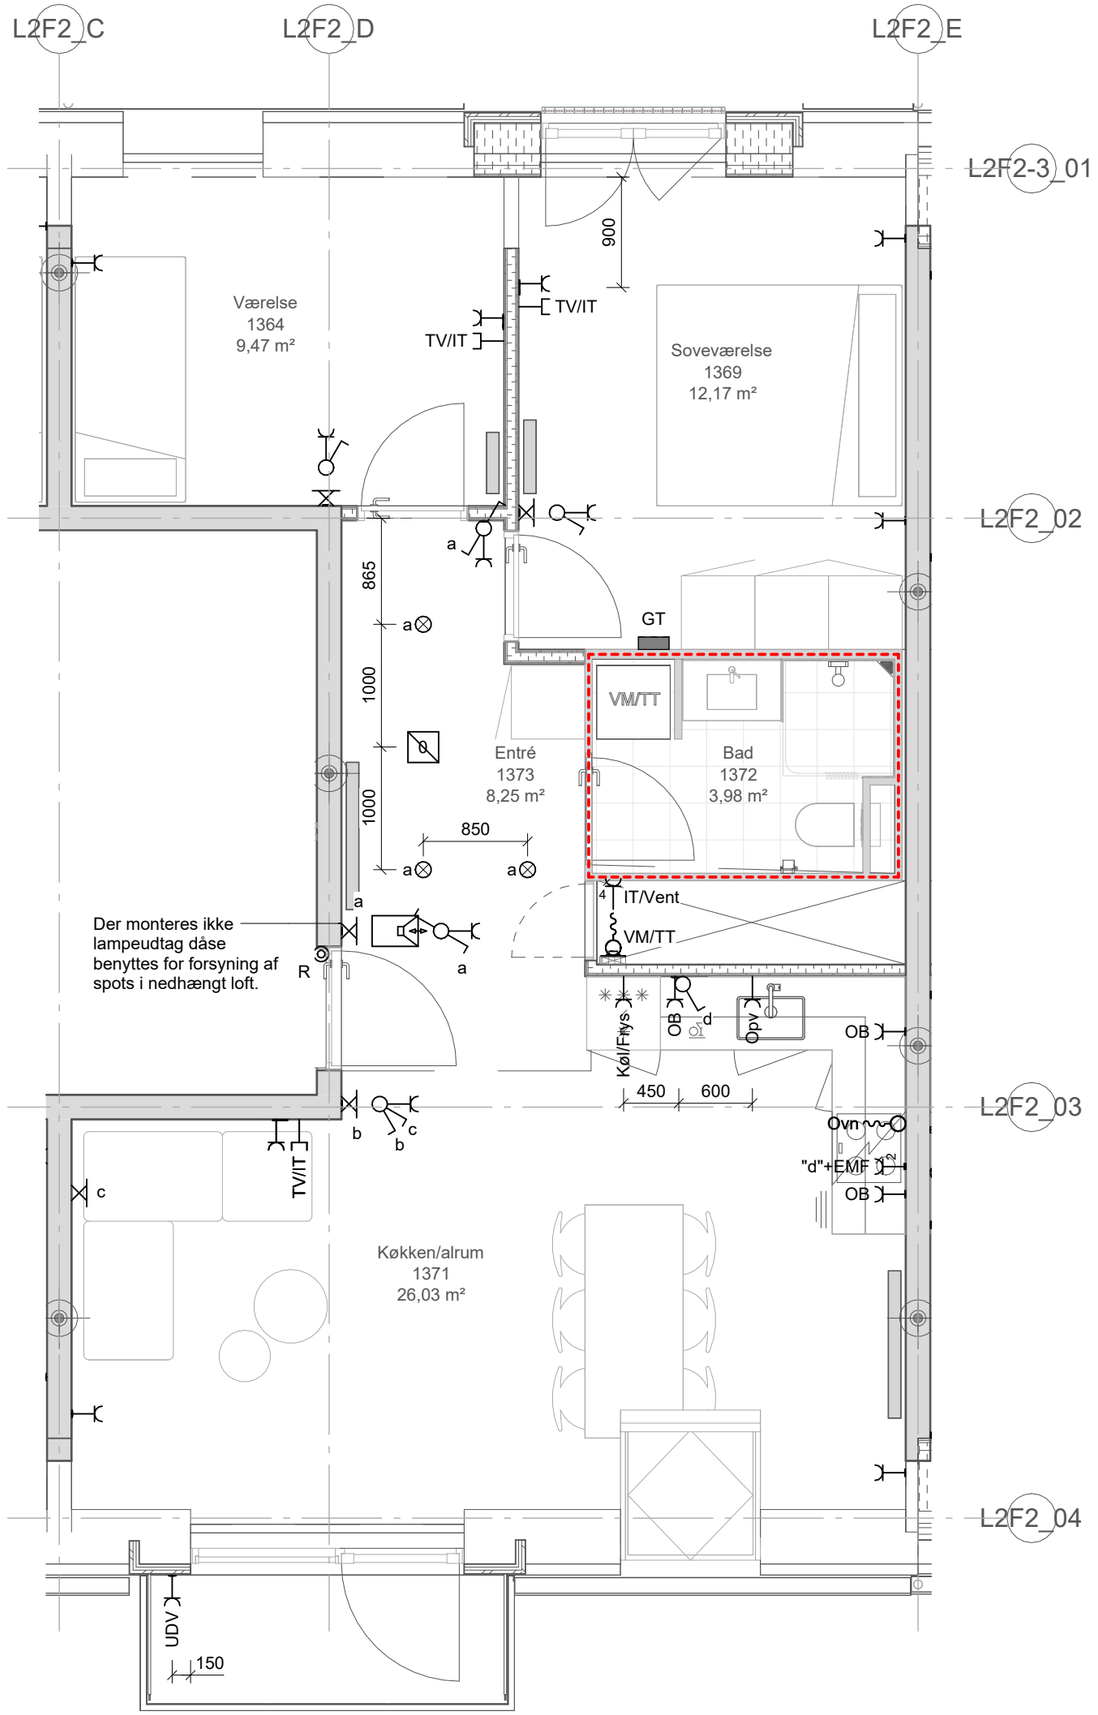

Projekt: Stejlepladsen

ARTELIA


Tekst: Elinstallationer -
Byg F2 - 4. Sal, Byg A
OPG_3V_T31_TA_S - Side F2-20

Tegningsnr.: ISP2_K07_L2XX_H04_EXX_N931

Rev.:

Projektnr.: 1019198 | Dato: 2026-02-27 | Rev. Dato: | Mål: 1 : 50 | Side: F2-20

www.arteliagroup.dk | Fil:

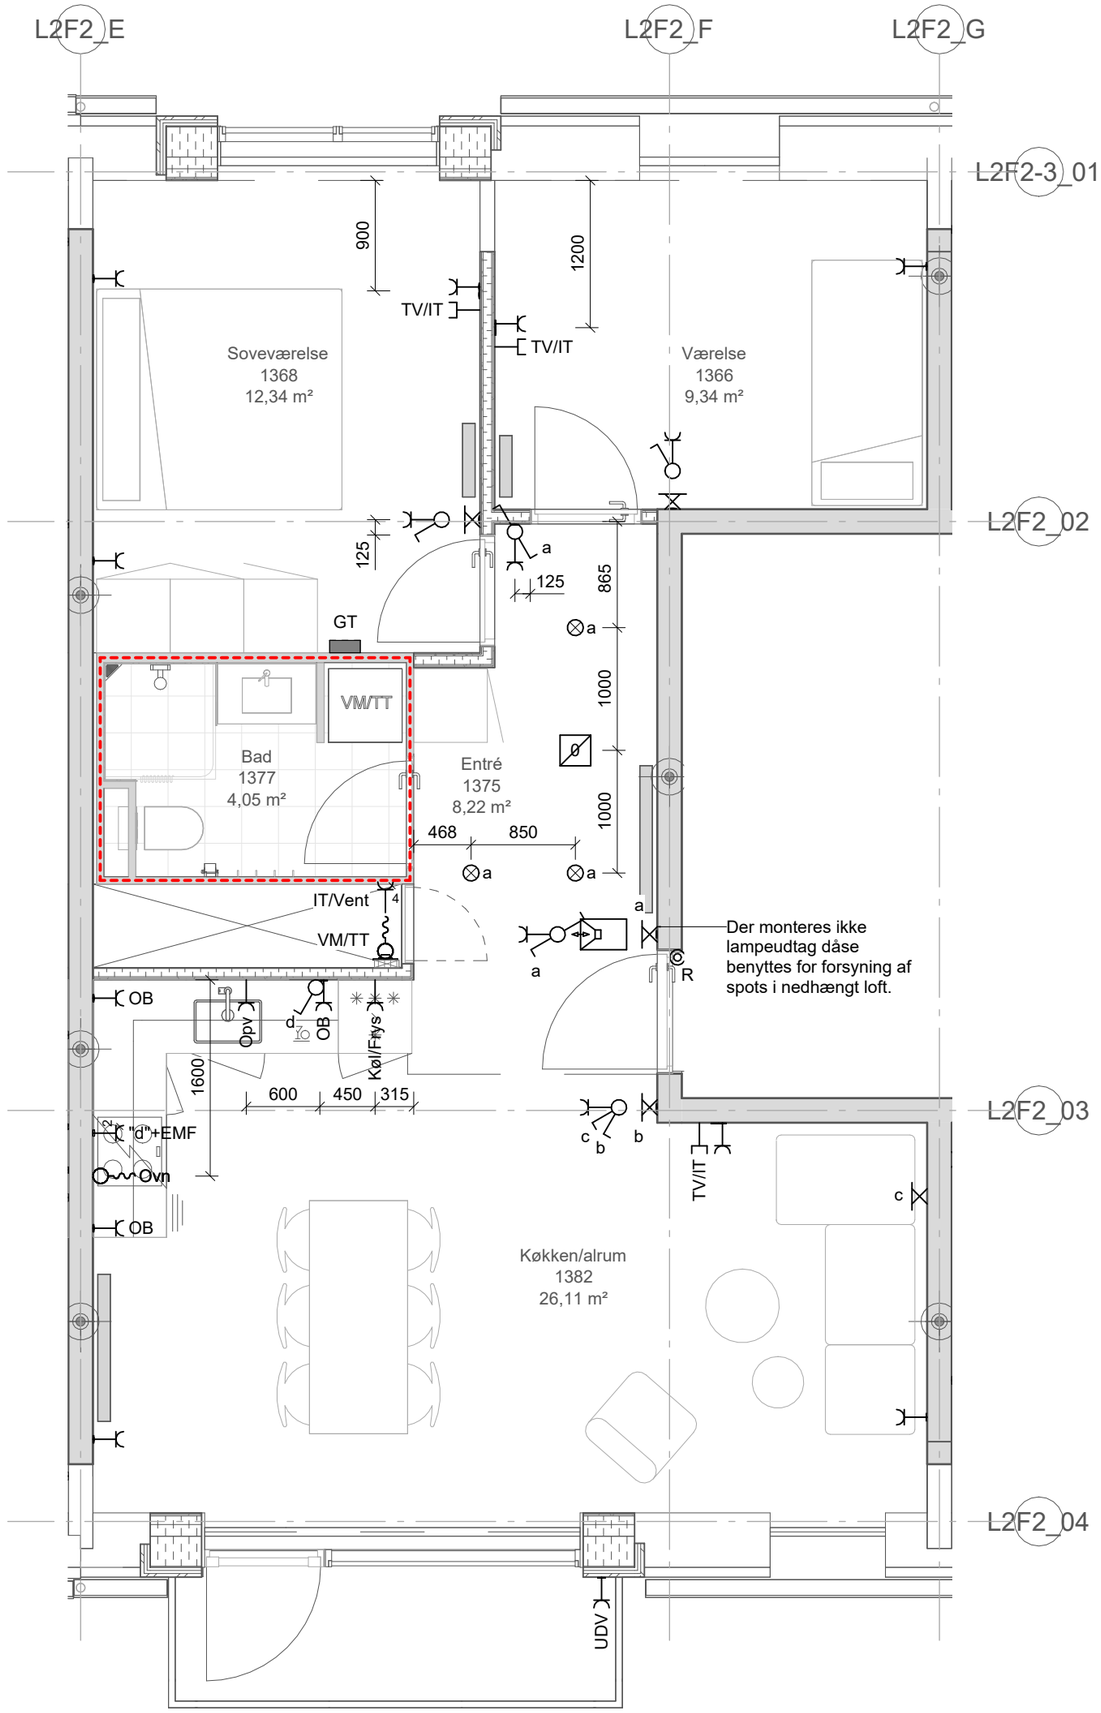

Projekt: Stejlepladsen


Tekst: Elinstallationer -
Byg F2 - 4. Sal, Byg B
OPG_3V_T31_TA - Side F2-21

Tegningsnr.: ISP2_K07_L2XX_H04_EFX_N931

Rev.:

Projektnr.: 1019198 | Dato: 2026-02-27 | Rev. Dato: | Mål: 1 : 50 | Side: F2-21

www.arteliagroup.dk | Fil:

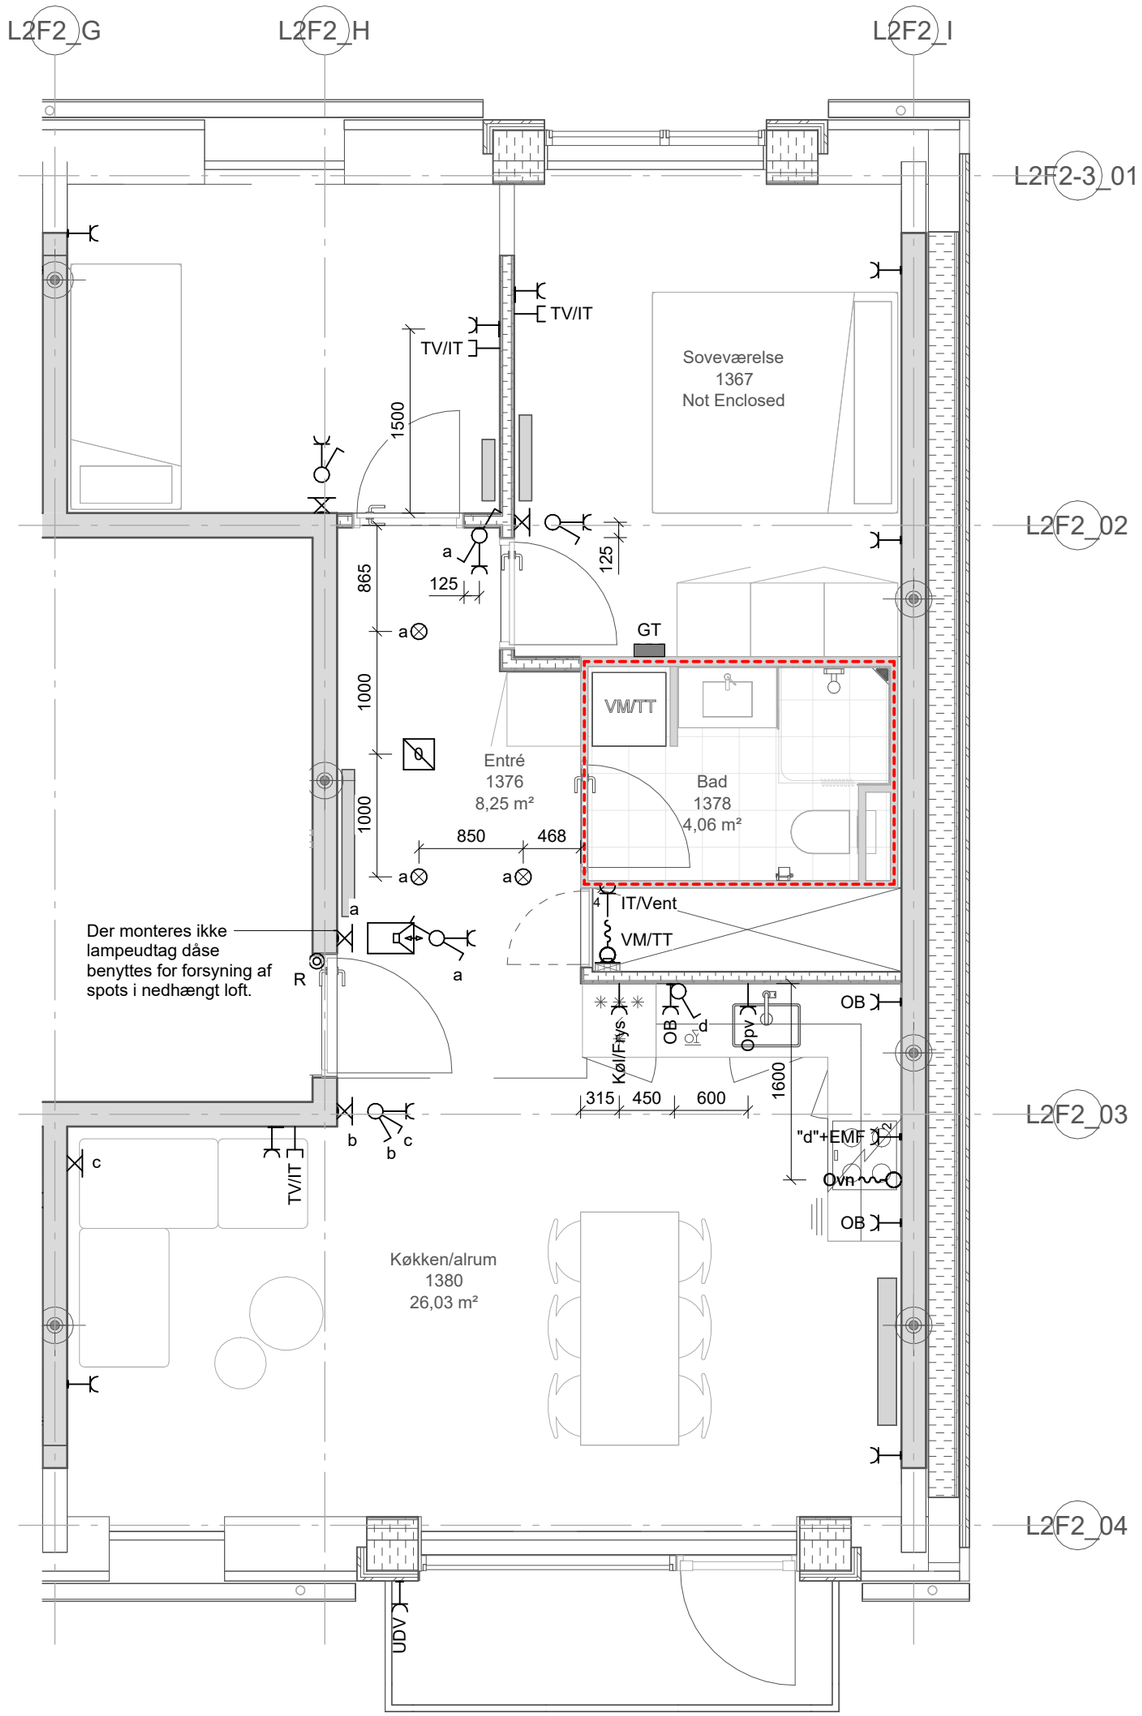

Projekt: Stejlepladsen

Tekst: Elinstallationer -
Byg F2 - 4. Sal, Byg B
OPG_3V_T31_TA_S - Side F2-22

Tegningsnr.: ISP2_K07_L2XX_H04_EFX_N931

Rev.:

Projektnr.: 1019198 | Dato: 2026-02-27 | Rev. Dato: | Mål: 1 : 50 | Side: F2-22

www.arteliagroup.dk | Fil: