Sheet Number	Tekst:	Dato:	Rev.:	Rev. Dato:
ISP2_K07_L2XX_H04_EFX_N931 - Side F3-1	Byg F3 - Index	2026-02-27		
ISP2_K07_L2XX_H04_EFX_N931 - Side F3-2	Byg F3 - Oversigtsplan	2026-02-27		
ISP2_K07_L2XX_H04_EFX_N931 - Side F3-3	Byg F3 - Stueplan, Byg B	2026-02-27		
ISP2_K07_L2XX_H04_EFX_N931 - Side F3-4	Byg F3 - Stueplan, Byg B	2026-02-27		
ISP2_K07_L2XX_H04_EFX_N931 - Side F3-5	Byg F3 - Stueplan, Byg B	2026-02-27		
ISP2_K07_L2XX_H04_EFX_N931 - Side F3-6	Byg F3 - Stueplan, Byg B	2026-02-27		
ISP2_K07_L2XX_H04_EFX_N931 - Side F3-7	Byg F3 - 1. Sal, Byg A	2026-02-27		
ISP2_K07_L2XX_H04_EFX_N931 - Side F3-8	Byg F3 - 1. Sal, Byg A	2026-02-27		
ISP2_K07_L2XX_H04_EFX_N931 - Side F3-9	Byg F3 - 1. Sal, Byg A	2026-02-27		
ISP2_K07_L2XX_H04_EFX_N931 - Side F3-10	Byg F3 - 1. Sal, Byg B	2026-02-27		
ISP2_K07_L2XX_H04_EFX_N931 - Side F3-11	Byg F3 - 1. Sal, Byg B	2026-02-27		
ISP2_K07_L2XX_H04_EFX_N931 - Side F3-12	Byg F3 - 1. Sal, Byg B	2026-02-27		
ISP2_K07_L2XX_H04_EFX_N931 - Side F3-13	Byg F3 - 1. Sal, Byg B	2026-02-27		
ISP2_K07_L2XX_H04_EFX_N931 - Side F3-14	Byg F3 - 2. Sal, Byg A	2026-02-27		
ISP2_K07_L2XX_H04_EFX_N931 - Side F3-15	Byg F3 - 2. Sal, Byg A	2026-02-27		
ISP2_K07_L2XX_H04_EFX_N931 - Side F3-16	Byg F3 - 2. Sal, Byg A	2026-02-27		
ISP2_K07_L2XX_H04_EFX_N931 - Side F3-17	Byg F3 - 2. Sal, Byg B	2026-02-27		
ISP2_K07_L2XX_H04_EFX_N931 - Side F3-18	Byg F3 - 2. Sal, Byg B	2026-02-27		
ISP2_K07_L2XX_H04_EFX_N931 - Side F3-19	Byg F3 - 2. Sal, Byg B	2026-02-27		
ISP2_K07_L2XX_H04_EFX_N931 - Side F3-20	Byg F3 - 2. Sal, Byg B	2026-02-27		
ISP2_K07_L2XX_H04_EFX_N931 - Side F3-21	Byg F3 - 3. Sal, Byg A	2026-02-27		
ISP2_K07_L2XX_H04_EFX_N931 - Side F3-22	Byg F3 - 3. Sal, Byg B	2026-02-27		
ISP2_K07_L2XX_H04_EFX_N931 - Side F3-23	Byg F3 - 3. Sal, Byg B	2026-02-27		
ISP2_K07_L2XX_H04_EFX_N931 - Side F3-24	Byg F3 - 3. Sal, Byg B	2026-02-27		
ISP2_K07_L2XX_H04_EFX_N931 - Side F3-25	Byg F3 - 3. Sal, Byg B	2026-02-27		

Projekt: Stejlepladsen

Tekst: Elinstallationer - Byg F3 - Index


Tegningsnr.: ISP2_K07_L2XX_H04_EFX_N931

Rev.:


Projektnr.: 1019198 | Dato: 2026-02-27 | Rev. Dato: | Mål: | Side: F3-1

www.arteliagroup.dk | Fil:


Stueplan - Byg F3

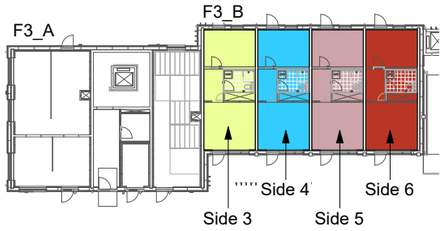


1. sal - Byg F3

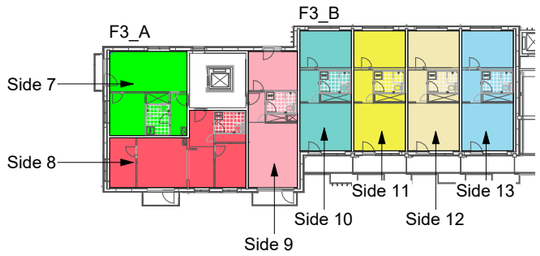

2. sal - Byg F3

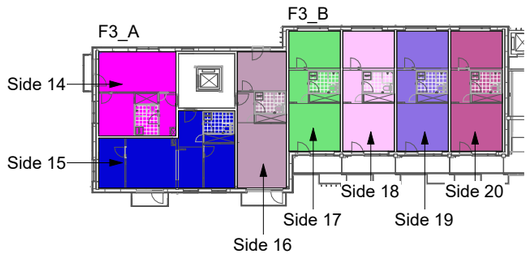

3. sal - Byg F3

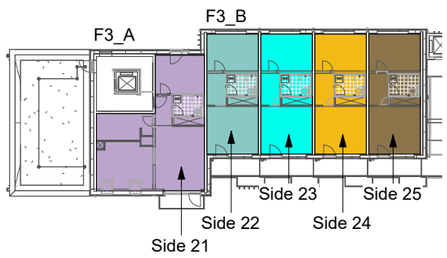

Oversigt, bygning F3:

Side 3: Altangangsbolig, Byg B, st., 2V

Side 4: Altangangsbolig, Byg B, st., 2V

Side 5: Altangangsbolig, Byg B, st., 2V

Side 6: Altangangsbolig, Byg B, st., 2V

Side 7: Opgangsbolig, Byg A, 1.sal 2V

Side 8: Opgangsbolig, Byg A, 1.sal 2V

Side 9: Opgangsbolig, Byg A, 1.sal 2V

Side 10: Altangangsbolig, Byg B, 1.sal 2V

Side 11: Altangangsbolig, Byg B, 1.sal 2V

Side 12: Altangangsbolig, Byg B, 1.sal 2V

Side 13: Altangangsbolig, Byg B, 1.sal 2V

Side 14: Opgangsbolig, Byg A, 2.sal 2V

Side 15: Opgangsbolig, Byg A, 2.sal 2V

Side 16: Opgangsbolig, Byg A, 2.sal 2V

Side 17: Altangangsbolig, Byg B, 2.sal 2V

Side 18: Altangangsbolig, Byg B, 2.sal 2V

Side 19: Altangangsbolig, Byg B, 2.sal 2V

Side 20: Altangangsbolig, Byg B, 2.sal 2V

Side 21: Opgangsbolig, Byg A, 3.sal 3V

Side 22: Altangangsbolig, Byg B, 3.sal 2V

Side 23: Altangangsbolig, Byg B, 3.sal 2V

Side 24: Altangangsbolig, Byg B, 3.sal 2V

Side 25: Altangangsbolig, Byg B, 3.sal 2V

Projekt: Stejlepladsen


Tekst: Elinstallationer - Byg F3 - Oversigtsplan

Tegningsnr.: ISP2_K07_L2XX_H04_EFX_N931

Rev.:

Projektnr.: 1019198 | Dato: 2026-02-27 | Rev. Dato: | Mål: 1 : 500 | Side: F3-2

www.arteliagroup.dk | Fil:

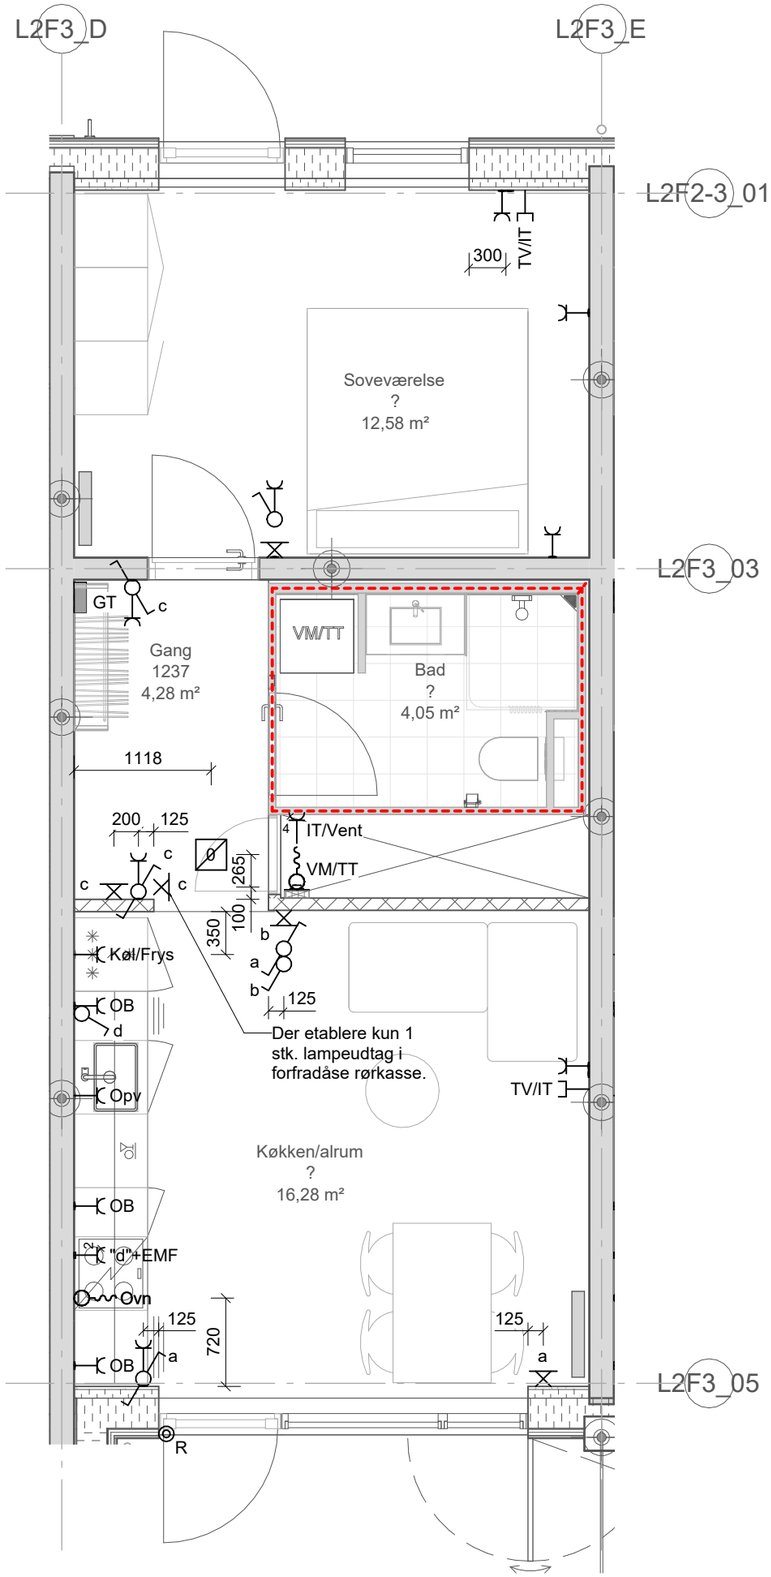

Projekt: Stejlepladsen


Tekst: Elinstallationer -
Byg F3 - Stueplan, Byg B
ALT_2V_T01_ST - Side F3-3

Tegningsnr.: ISP2_K07_L2XX_H04_EXX_N931

Rev.:

Projektnr.: 1019198 | Dato: 2026-02-27 | Rev. Dato: | Mål: 1 : 50 | Side: F3-3

www.arteliagroup.dk | Fil:

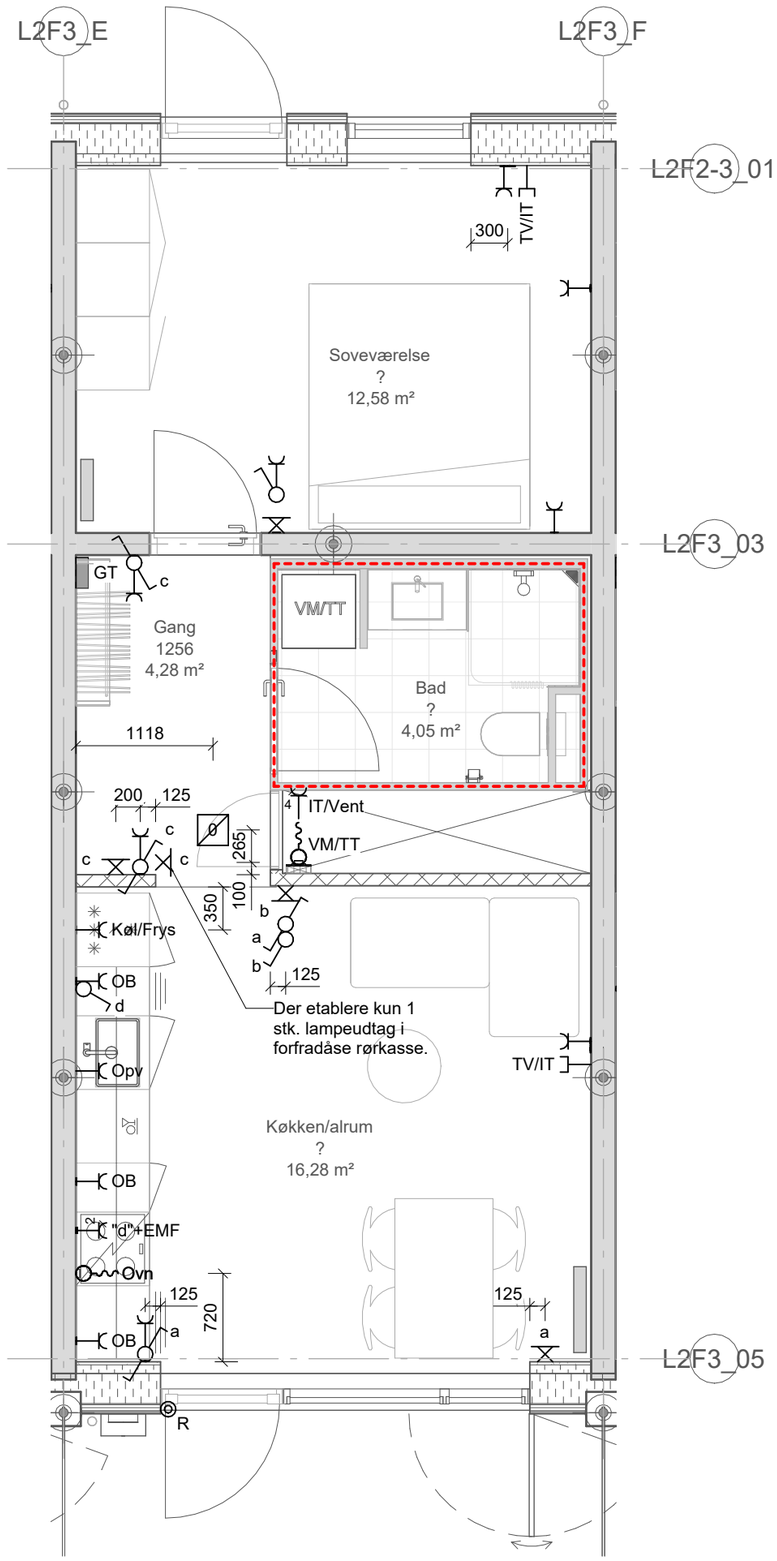

Projekt: Stejlepladsen


Tekst: Elinstallationer -
Byg F3 - Stueplan, Byg B
ALT_2V_T01_ST - Side F3-4

Tegningsnr.: ISP2_K07_L2XX_H04_EFX_N931

Rev.:

Projektnr.: 1019198 | Dato: 2026-02-27 | Rev. Dato: | Mål: 1 : 50 | Side: F3-4

www.arteliagroup.dk | Fil:

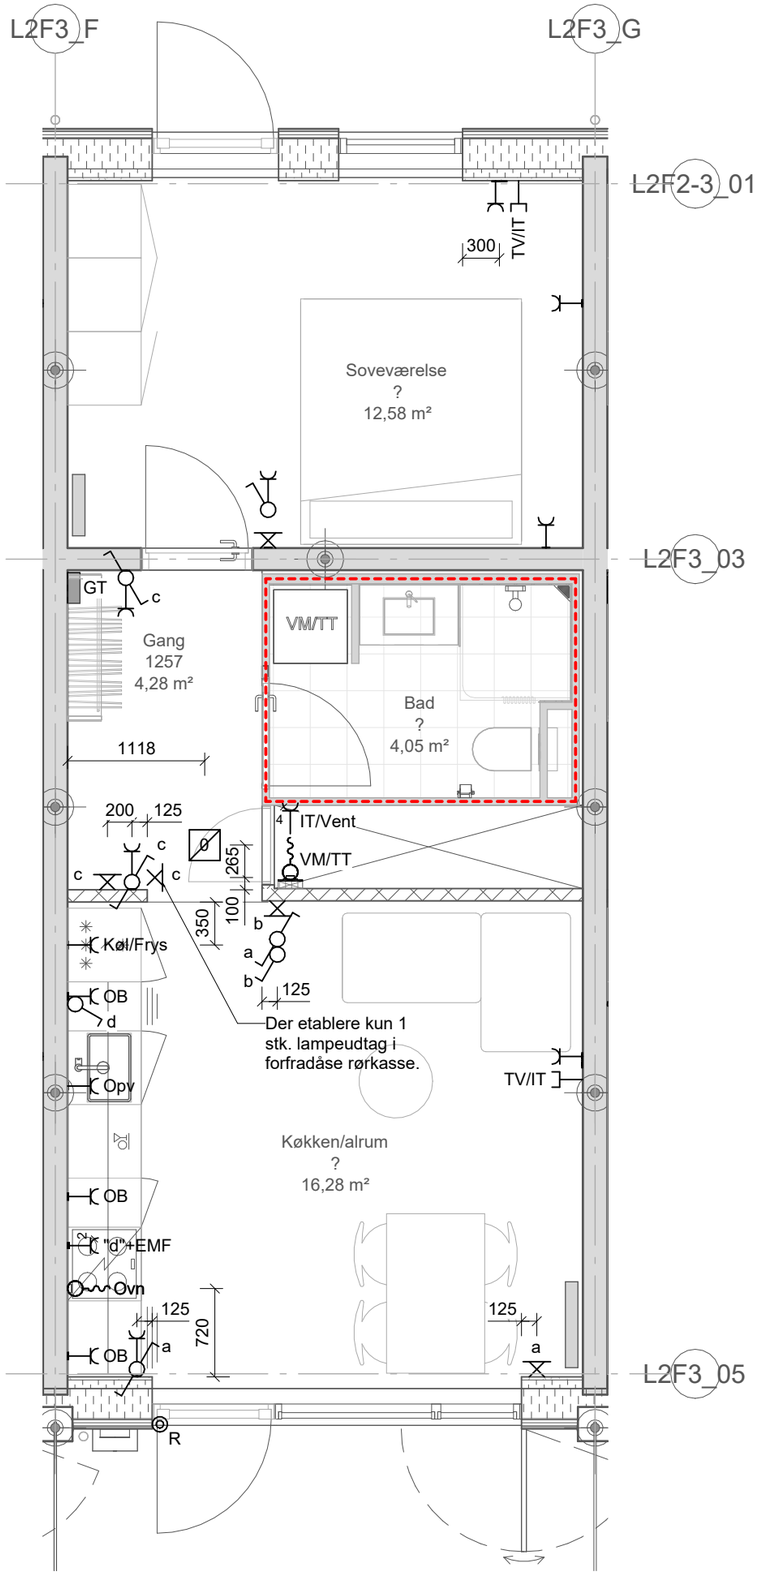

Projekt: Stejlepladsen


Tekst: Elinstallationer -
Byg F3 - Stueplan, Byg B
ALT_2V_T01_ST - Side F3-5

Tegningsnr.: ISP2_K07_L2XX_H04_EFX_N931

Rev.:

Projektnr.: 1019198 | Dato: 2026-02-27 | Rev. Dato: | Mål: 1 : 50 | Side: F3-5

www.arteliagroup.dk | Fil:

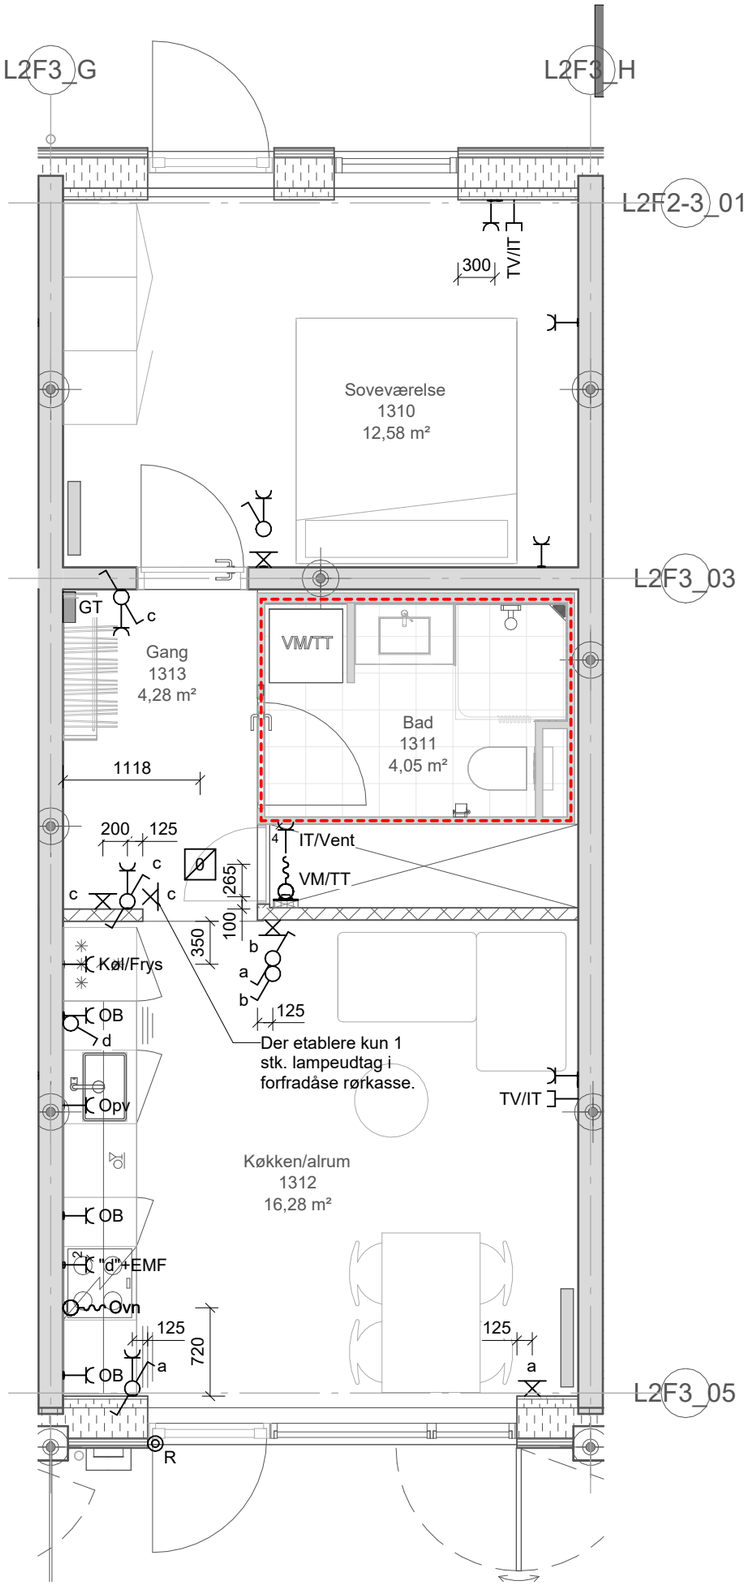

Projekt: Stejlepladsen


Tekst: Elinstallationer -
Byg F3 - Stueplan, Byg B
ALT_2V_T01_ST - Side F3-6

Tegningsnr.: ISP2_K07_L2XX_H04_EFX_N931

Rev.:

Projektnr.: 1019198 | Dato: 2026-02-27 | Rev. Dato: | Mål: 1 : 50 | Side: F3-6

www.arteliagroup.dk | Fil:

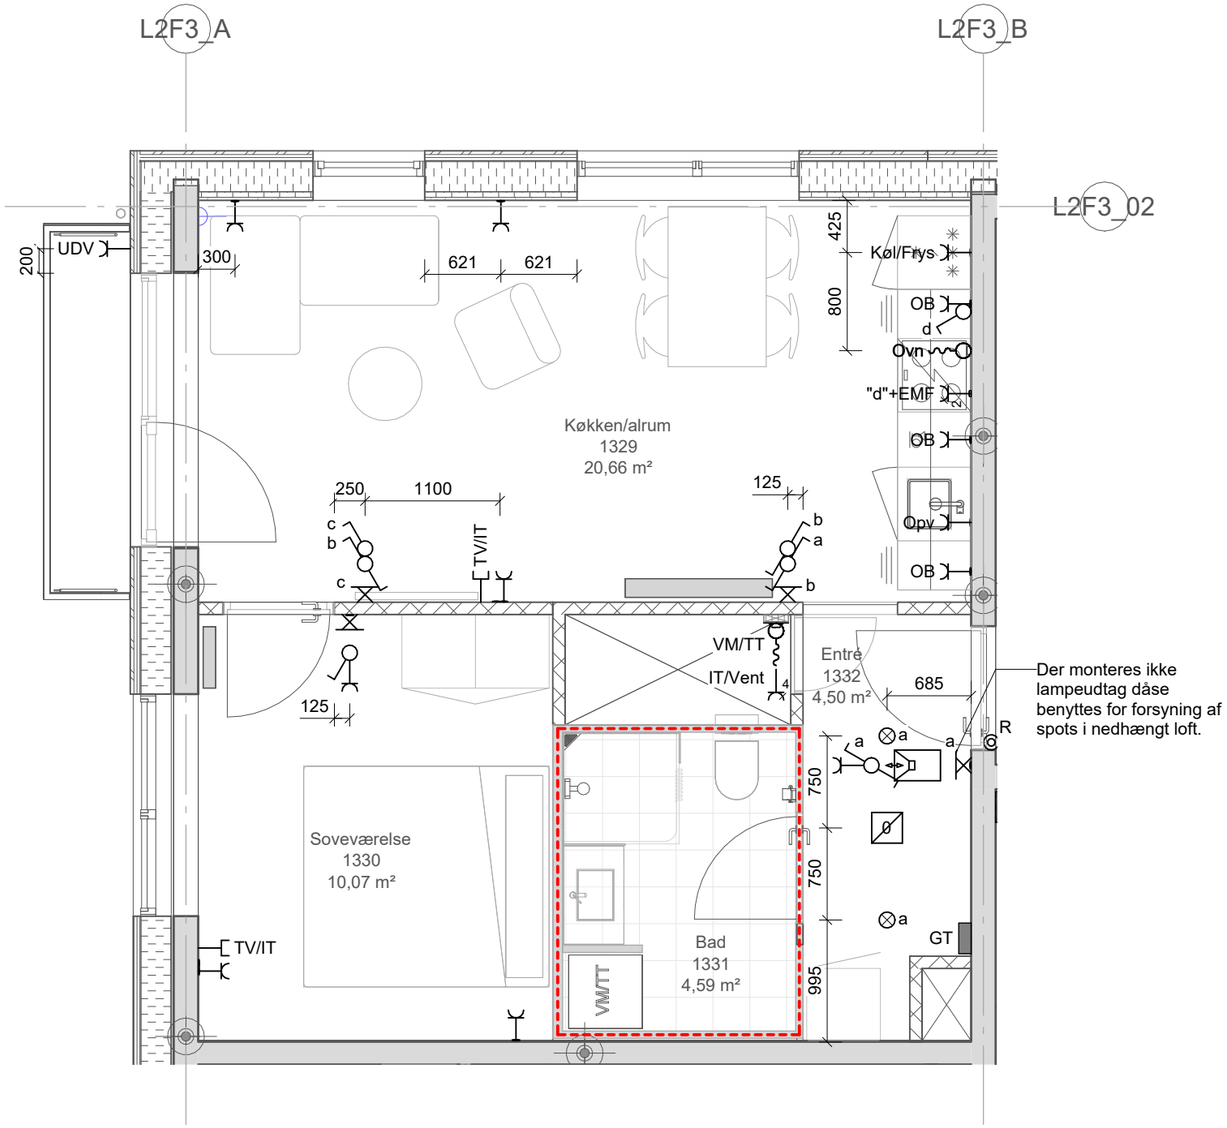

Der monteres ikke lampeudtag dåse benyttes for forsyning af spots i nedhængt loft.

Projekt: Stejlepladsen


Tekst: Elinstallationer -
Byg F3 - 1. Sal, Byg A
OPG_2V_T30 - Side F3-7

Tegningsnr.: ISP2_K07_L2XX_H04_EFX_N931

Rev.:

Projektnr.: 1019198 | Dato: 2026-02-27 | Rev. Dato: | Mål: 1 : 50 | Side: F3-7

www.arteliagroup.dk | Fil:

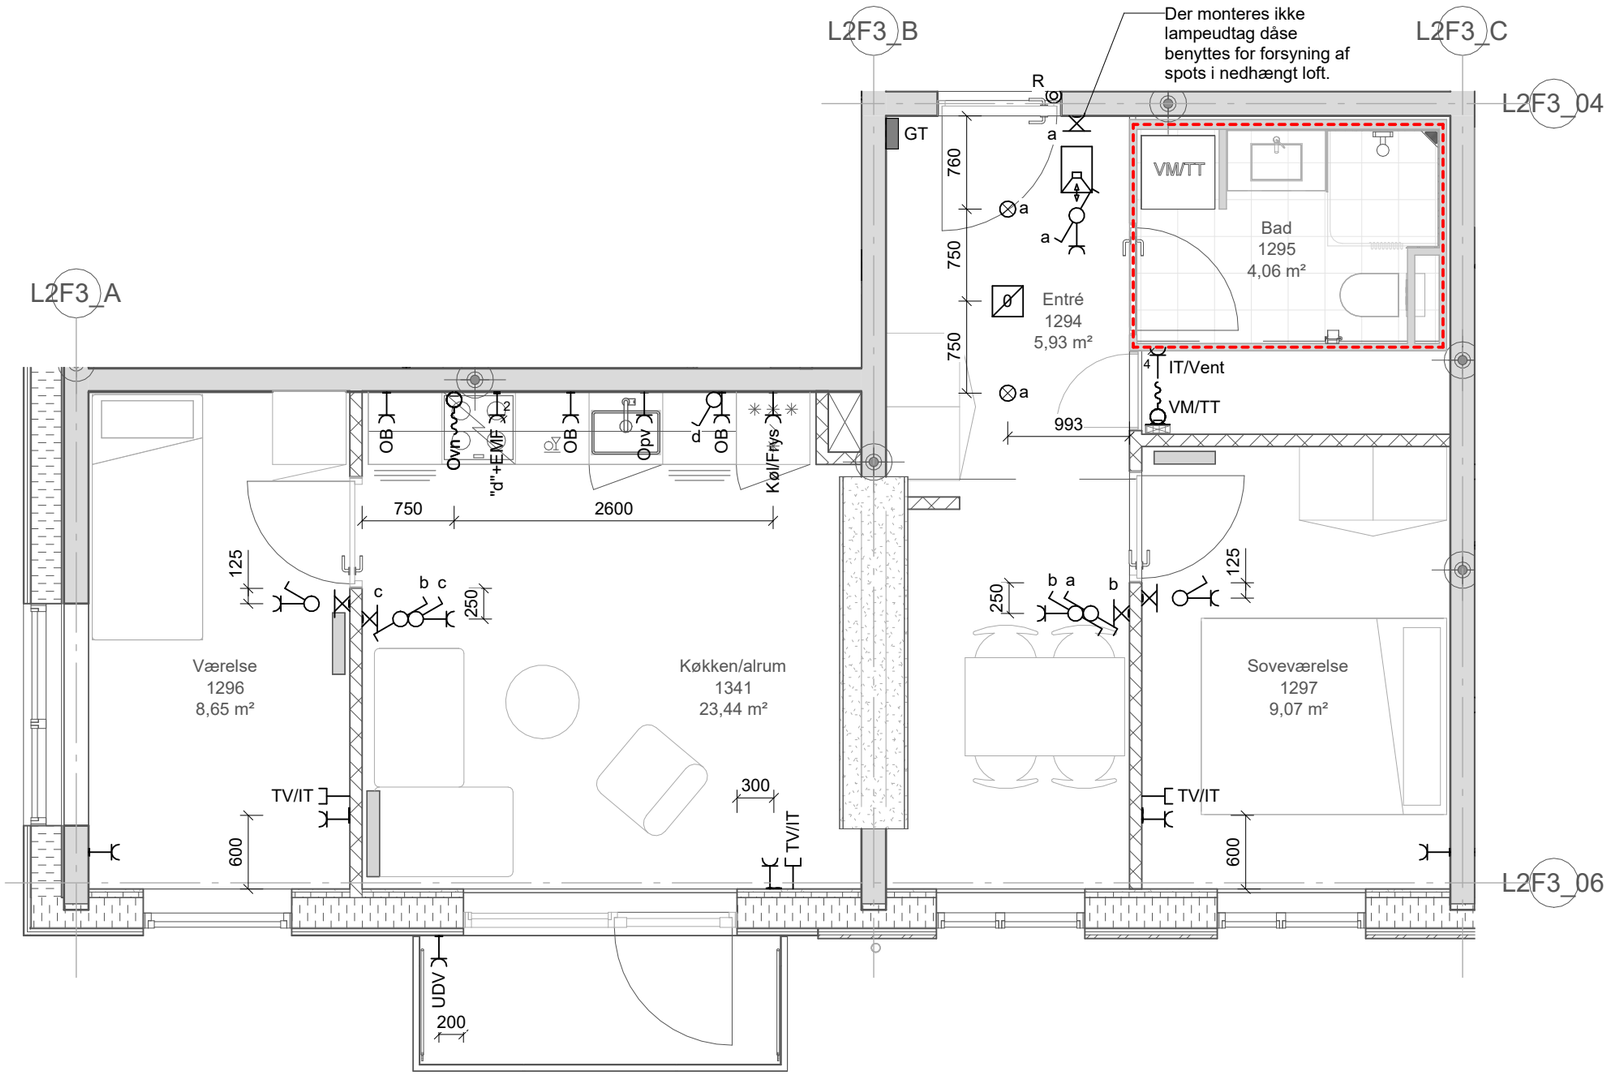

Projekt: Stejlepladsen


Tekst: Elinstallationer -
Byg F3 - 1. Sal, Byg A
OPG_3V_T33_S - Side F3-8

Tegningsnr.: ISP2_K07_L2XX_H04_EXX_N931


Rev.:

Projektnr.: 1019198 | Dato: 2026-02-27 | Rev. Dato: | Mål: 1 : 50 | Side: F3-8

www.arteliagroup.dk | Fil:

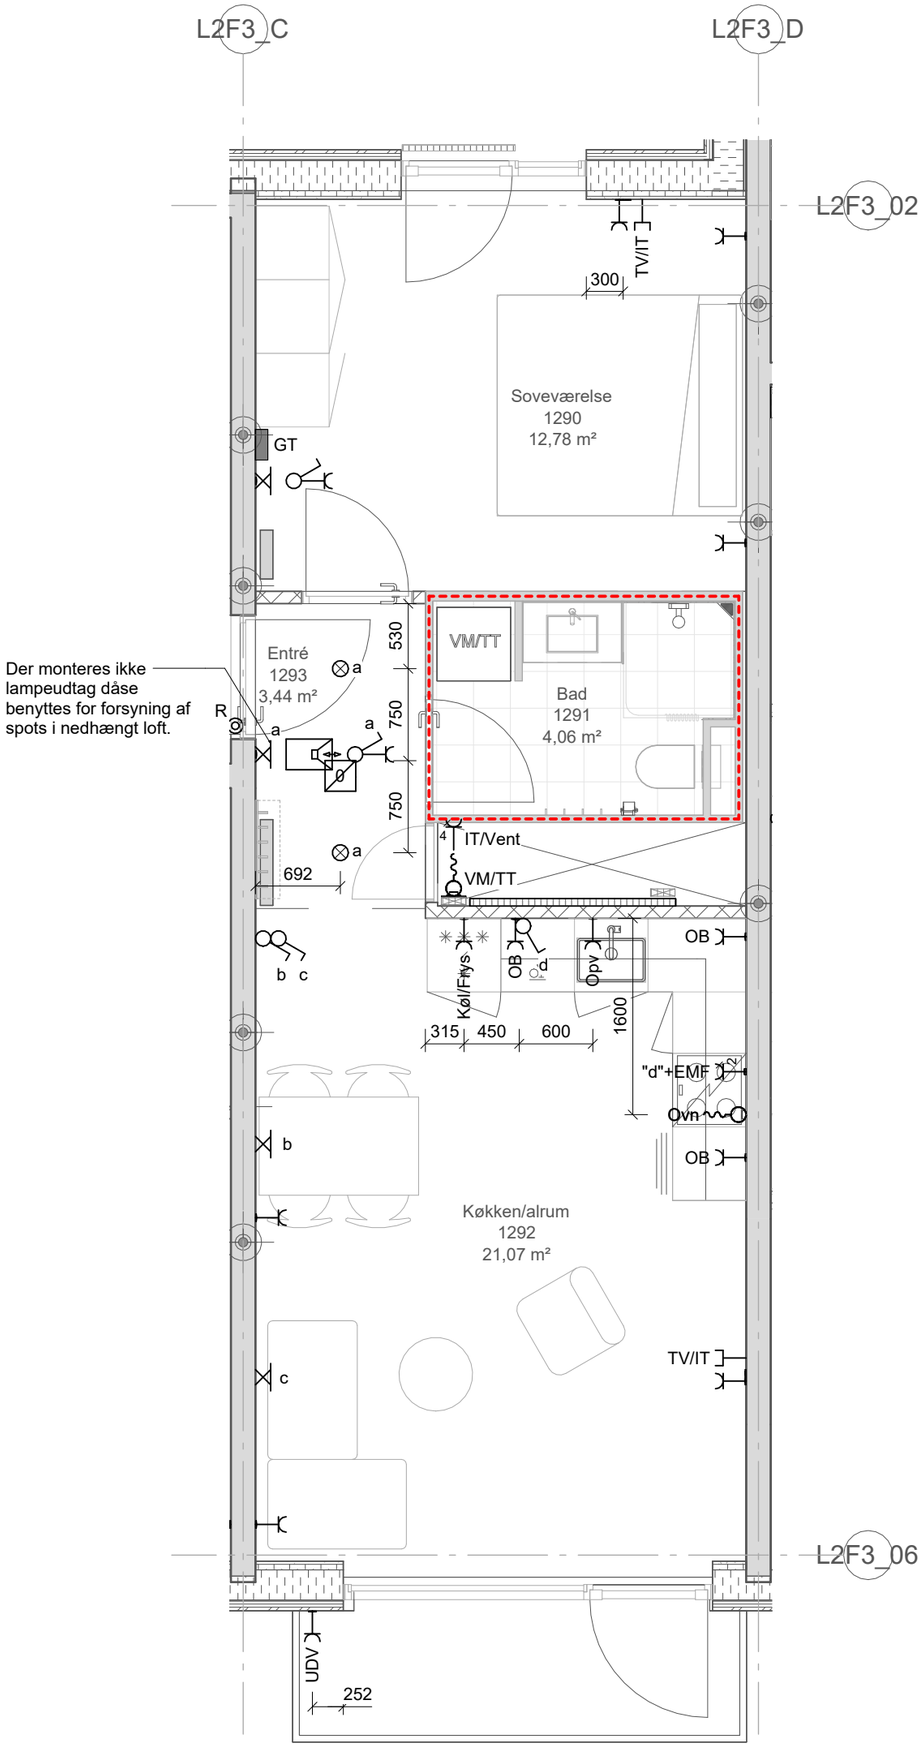

Projekt:	Stejlepladsen				
Tekst:	Elinstallationer - Byg F3 - 1. Sal, Byg A OPG_2V_T31 - Side F3-9			Tegningsnr.:	Rev.:
			ISP2_K07_L2XX_H04_EXX_N931		
Projektnr.: 1019198	Dato: 2026-02-27	Rev. Dato:		Mål: 1 : 50	Side: F3-9
www.arteliagroup.dk	Fil:				

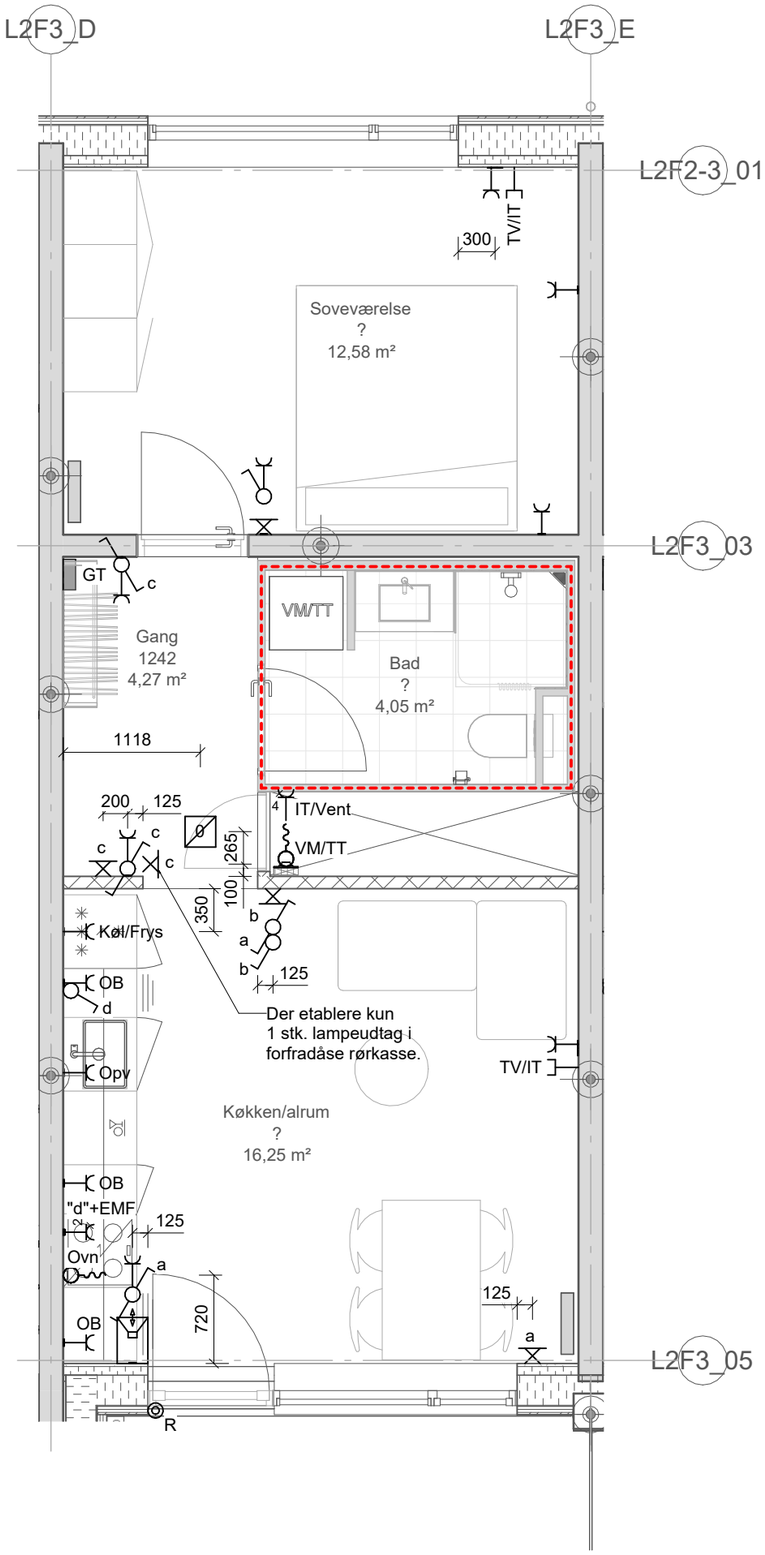

Projekt: Stejlepladsen


Tekst: Elinstallationer -
Byg F3 - 1. Sal, Byg B
ALT_2V_T01 - Side F3-10

Tegningsnr.: ISP2_K07_L2XX_H04_EFX_N931

Rev.:

Projektnr.: 1019198 | Dato: 2026-02-27 | Rev. Dato: | Mål: 1 : 50 | Side: F3-10

www.arteliagroup.dk | Fil:

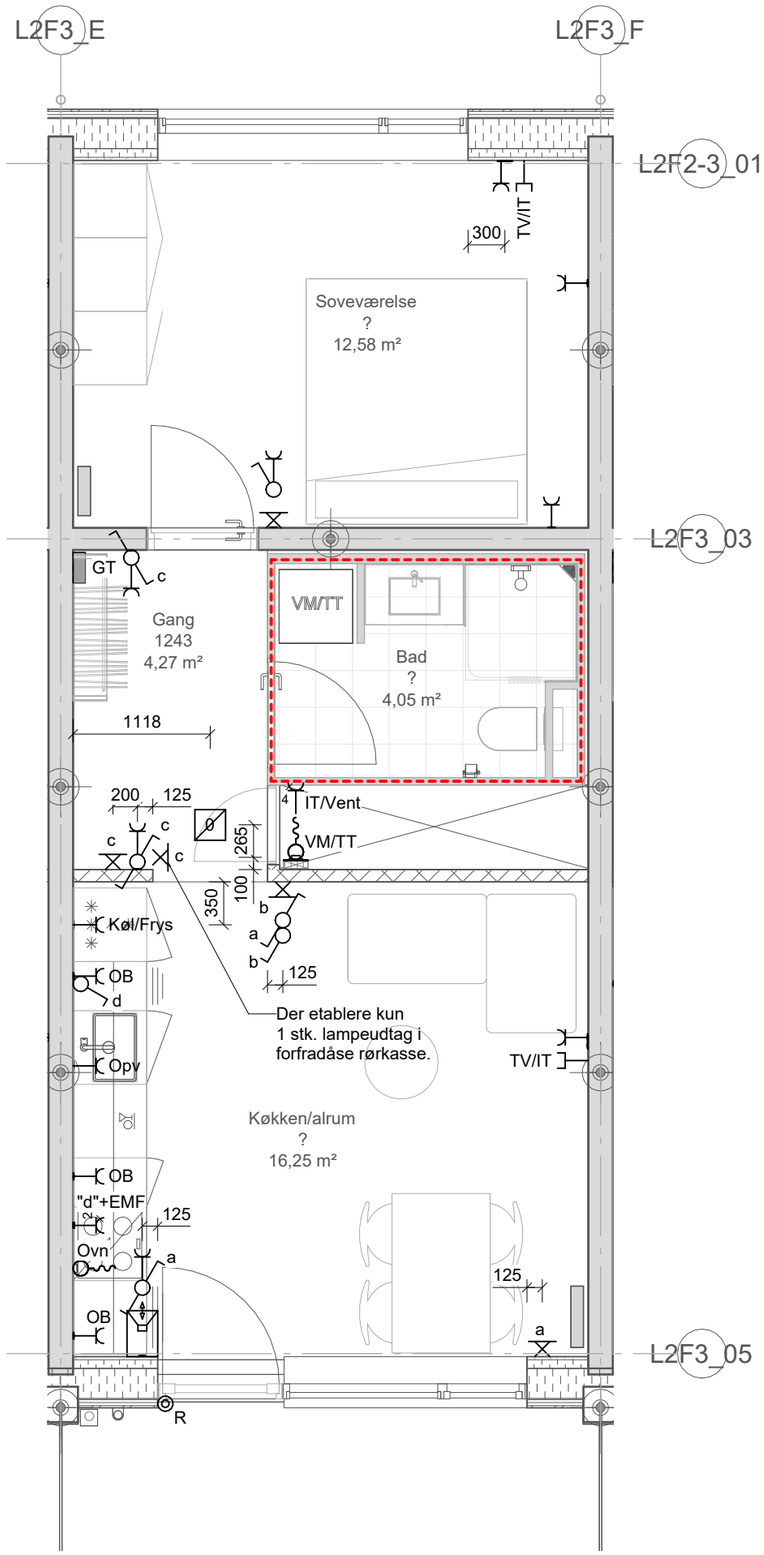

Projekt: Stejlepladsen


Tekst: Elinstallationer -
Byg F3 - 1. Sal, Byg B
ALT_2V_T01 - Side F3-11

Tegningsnr.: ISP2_K07_L2XX_H04_EFX_N931

Rev.:

Projektnr.: 1019198 | Dato: 2026-02-27 | Rev. Dato: | Mål: 1 : 50 | Side: F3-11

www.arteliagroup.dk | Fil:

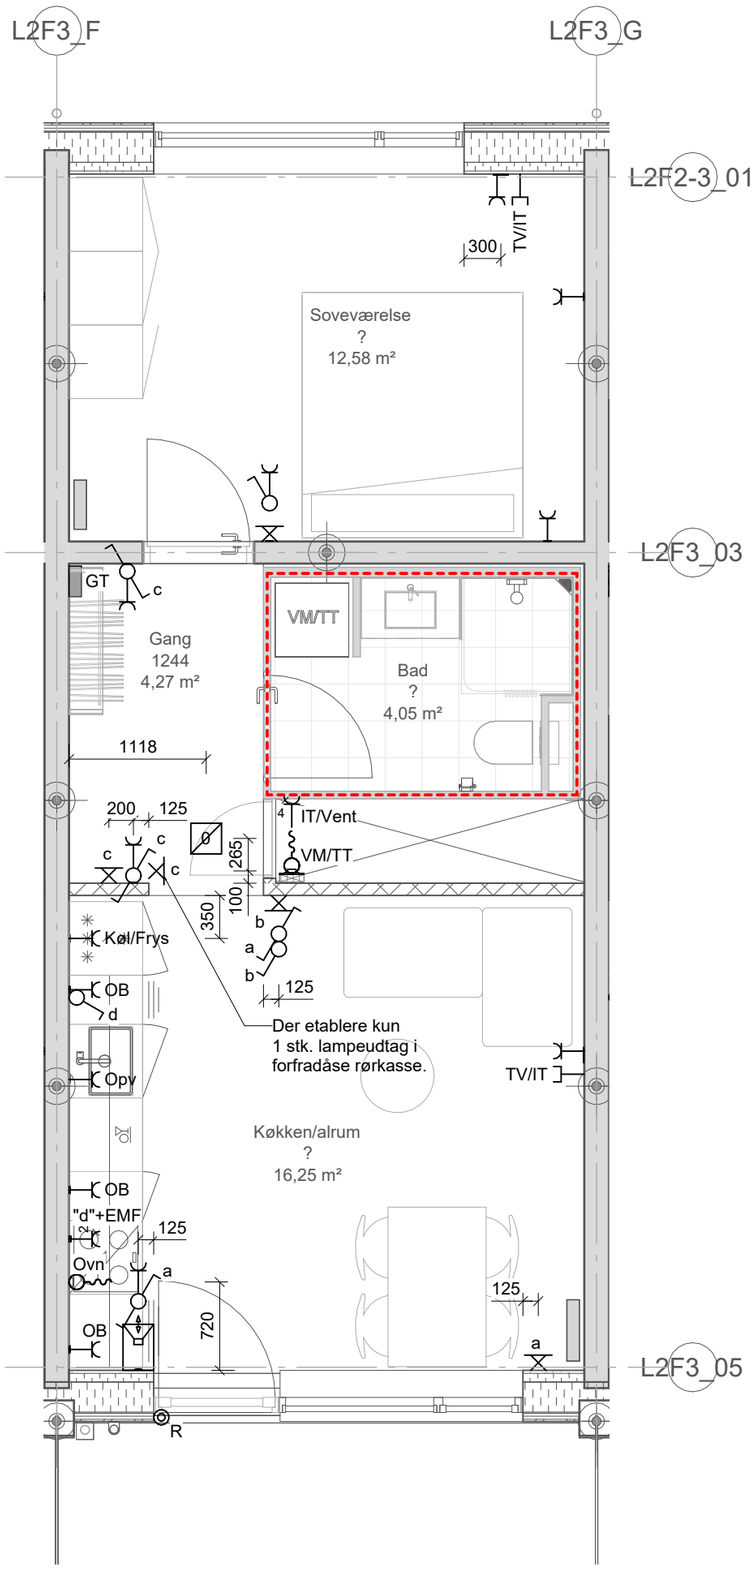

Projekt: Stejlepladsen


Tekst: Elinstallationer -
Byg F3 - 1. Sal, Byg B
ALT_2V_T01 - Side F3-12

Tegningsnr.: ISP2_K07_L2XX_H04_EFX_N931

Rev.:

Projektnr.: 1019198 | Dato: 2026-02-27 | Rev. Dato: | Mål: 1 : 50 | Side: F3-12

www.arteliagroup.dk | Fil:

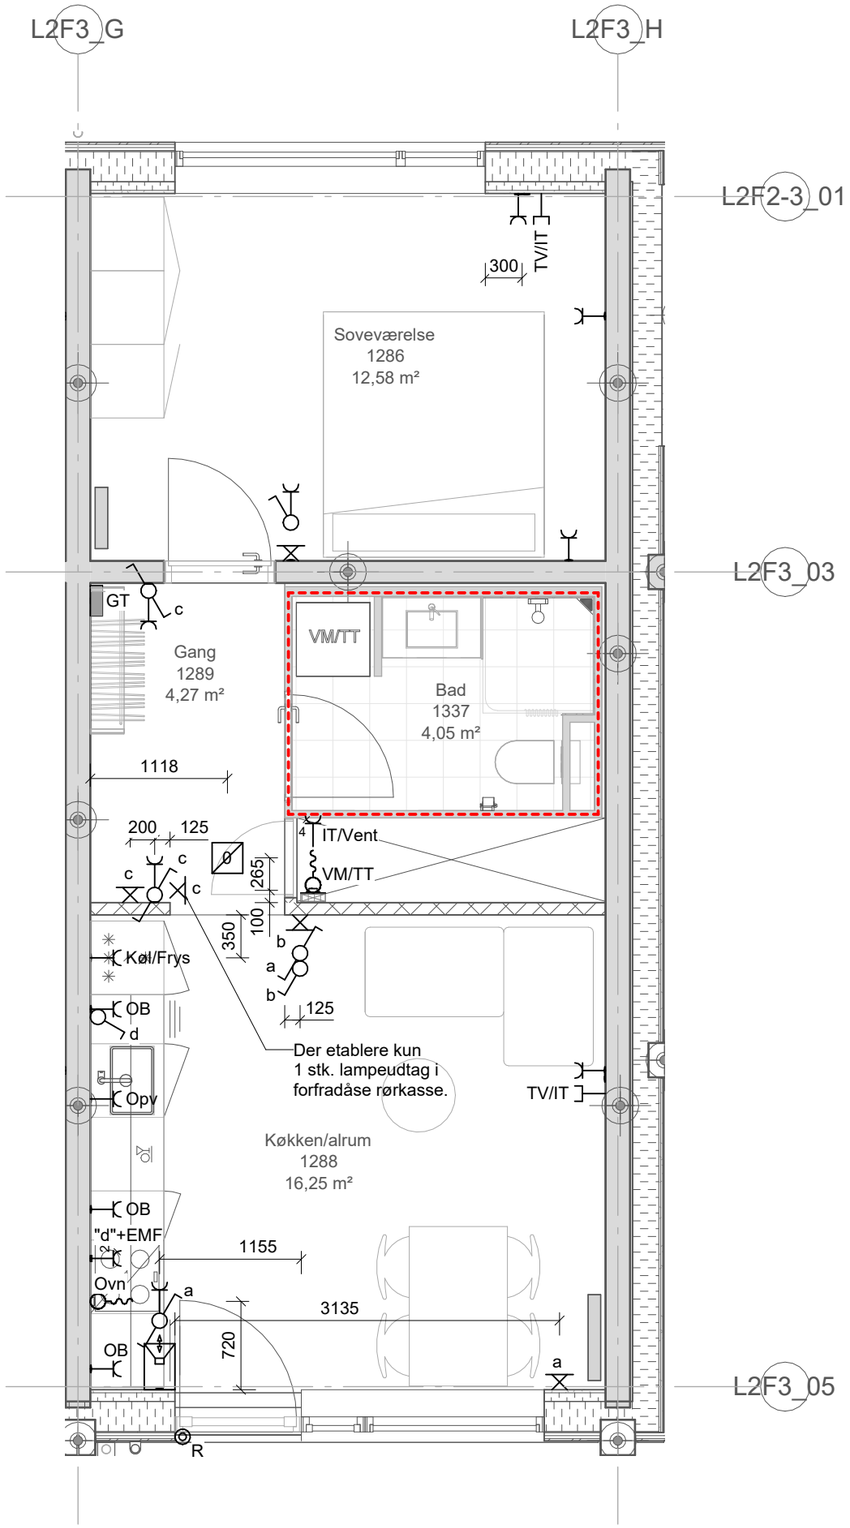

Projekt: Stejlepladsen


Tekst: Elinstallationer -
Byg F3 - 1. Sal, Byg B
ALT_2V_T01 - Side F3-13

Tegningsnr.: ISP2_K07_L2XX_H04_EFX_N931

Rev.:

Projektnr.: 1019198 | Dato: 2026-02-27 | Rev. Dato: | Mål: 1 : 50 | Side: F3-13

www.arteliagroup.dk | Fil:

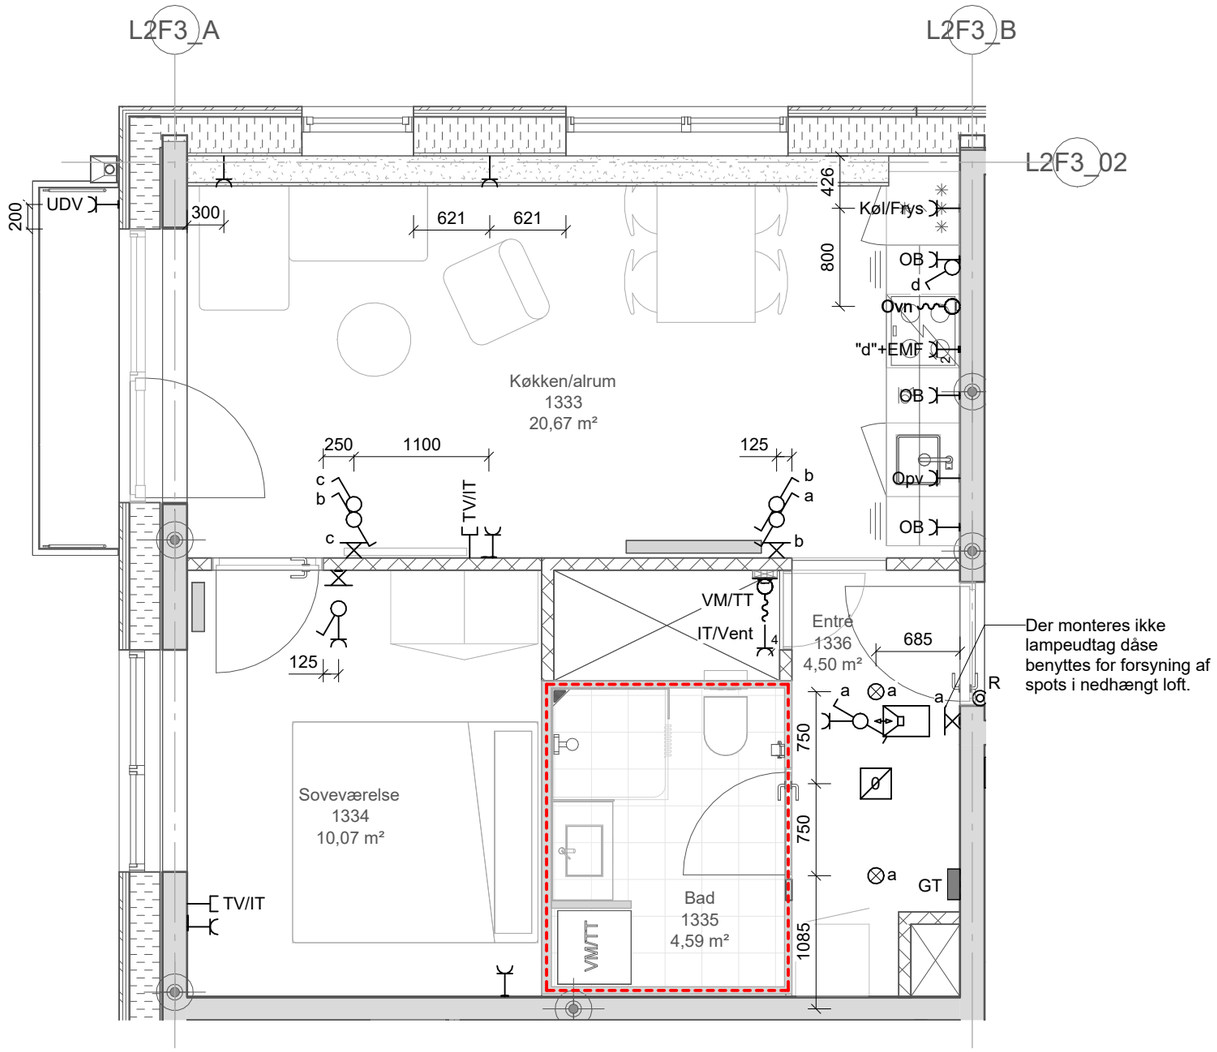

Projekt: Stejlepladsen

ARTELIA


Tekst: Elinstallationer -
Byg F3 - 2. Sal, Byg A
OPG_2V_T30 - Side F3-14

Tegningsnr.: ISP2_K07_L2XX_H04_EFX_N931


Rev.:

Projektnr.: 1019198 | Dato: 2026-02-27 | Rev. Dato: | Mål: 1 : 50 | Side: F3-14


www.arteliagroup.dk | Fil:

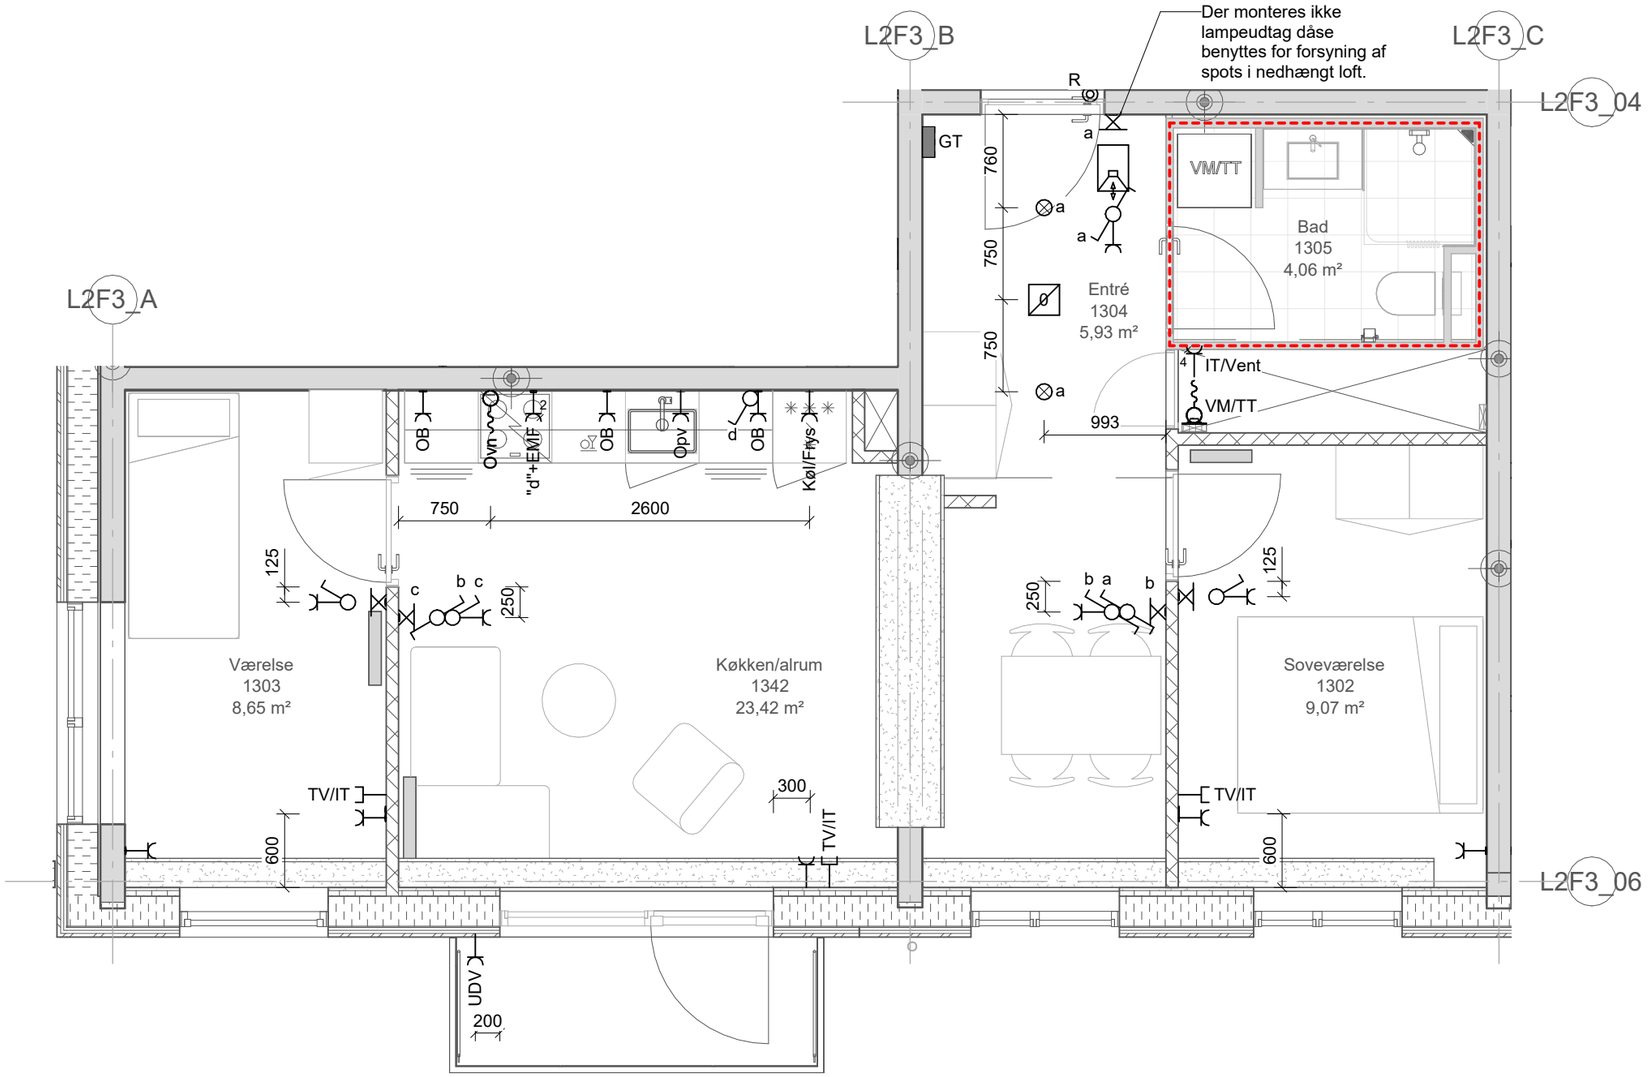

Projekt:	Stejlepladsen				
Tekst:	Elinstallationer - Byg F3 - 2. Sal, Byg A OPG_3V_T33_S - Side F3-15			Tegningsnr.:	Rev.:
				ISP2_K07_L2XX_H04_EFX_N931	
Projektnr.: 1019198	Dato: 2026-02-27	Rev. Dato:		Mål: 1 : 50	Side: F3-15
www.arteliagroup.dk	Fil:				

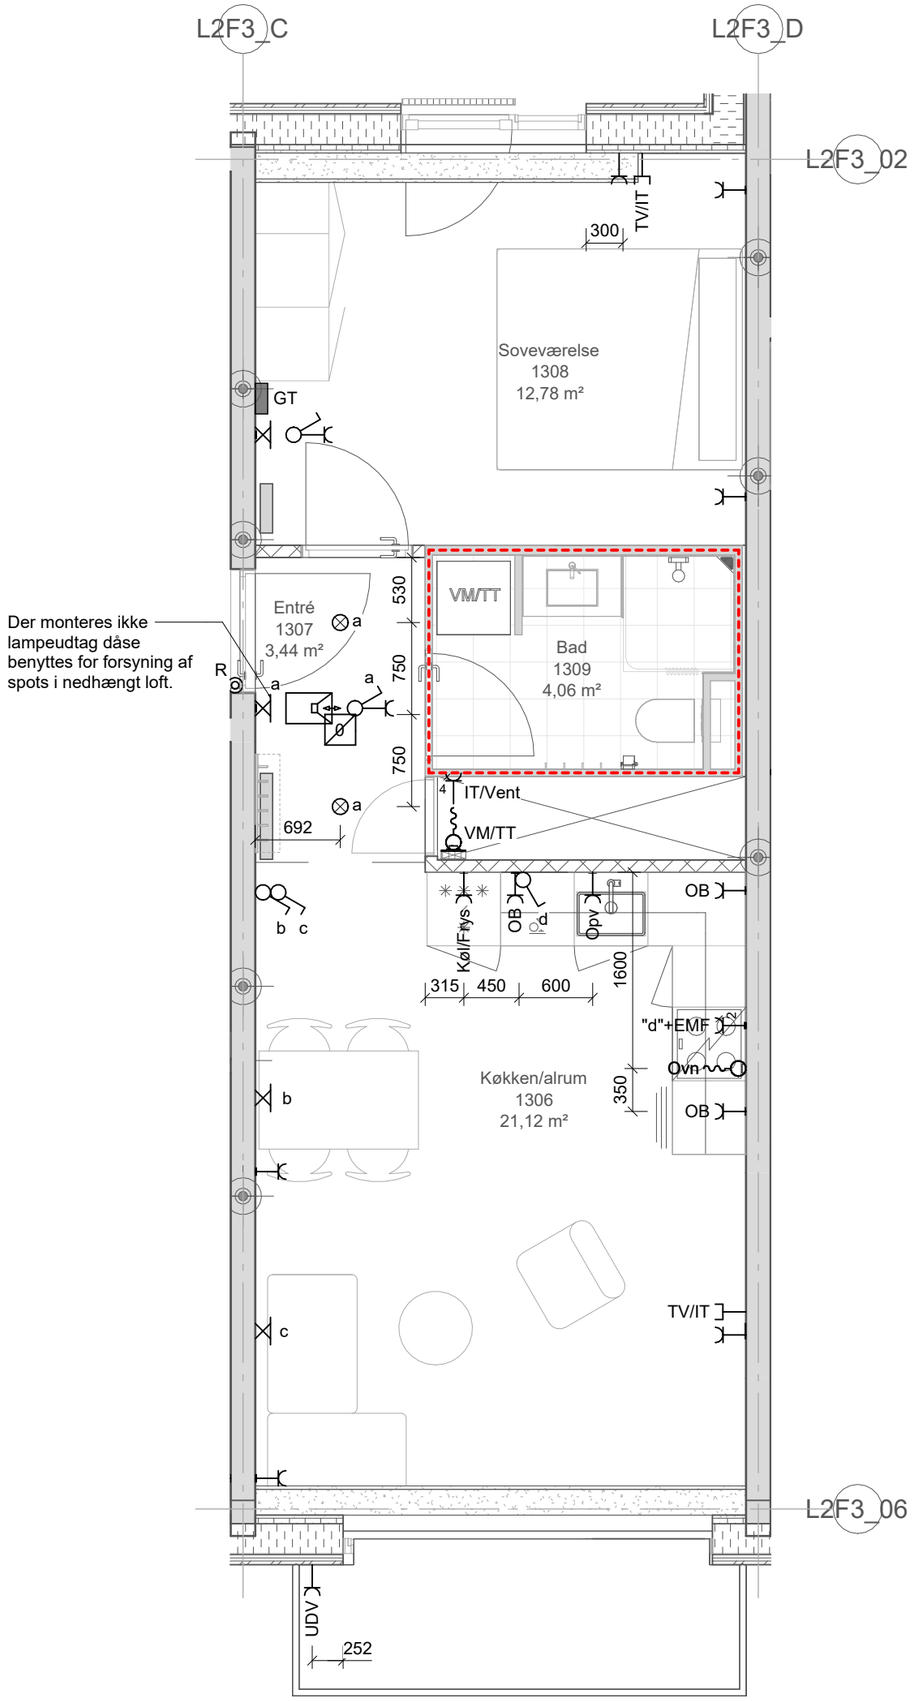

Projekt:	Stejlepladsen				
Tekst:	Elinstallationer - Byg F3 - 2. Sal, Byg A OPG_2V_T31 - Side F3-16			Tegningsnr.:	Rev.:
				ISP2_K07_L2XX_H04_EFX_N931	
Projektnr.: 1019198	Dato: 2026-02-27	Rev. Dato:		Mål: 1 : 50	Side: F3-16
www.arteliagroup.dk	Fil:				

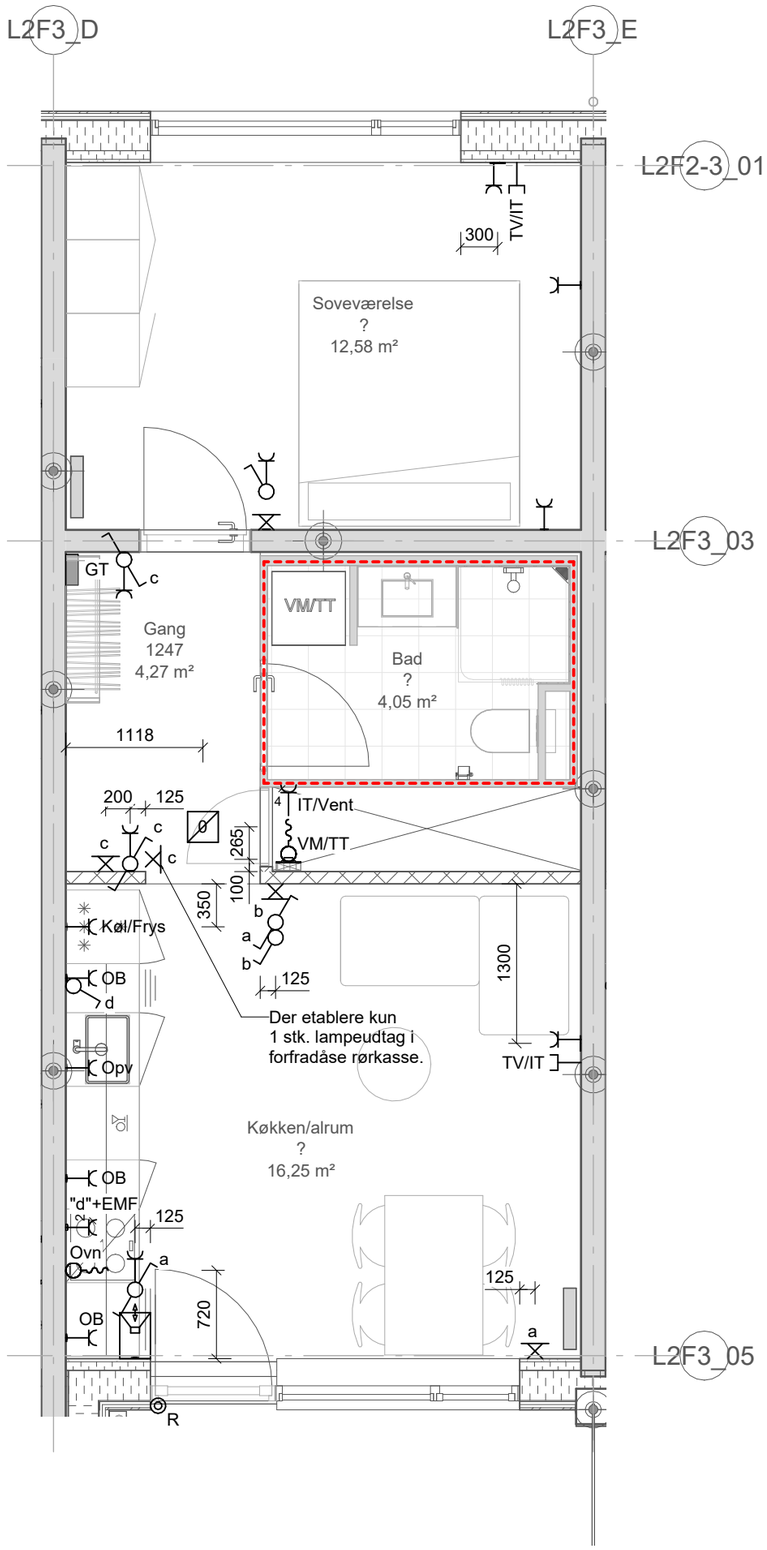

Projekt: Stejlepladsen

ARTELIA


Tekst: Elinstallationer -
Byg F3 - 2. Sal, Byg B
ALT_2V_T01 - Side F3-17

Tegningsnr.: ISP2_K07_L2XX_H04_EFX_N931

Rev.:

Projektnr.: 1019198 | Dato: 2026-02-27 | Rev. Dato: | Mål: 1 : 50 | Side: F3-17

www.arteliagroup.dk | Fil:

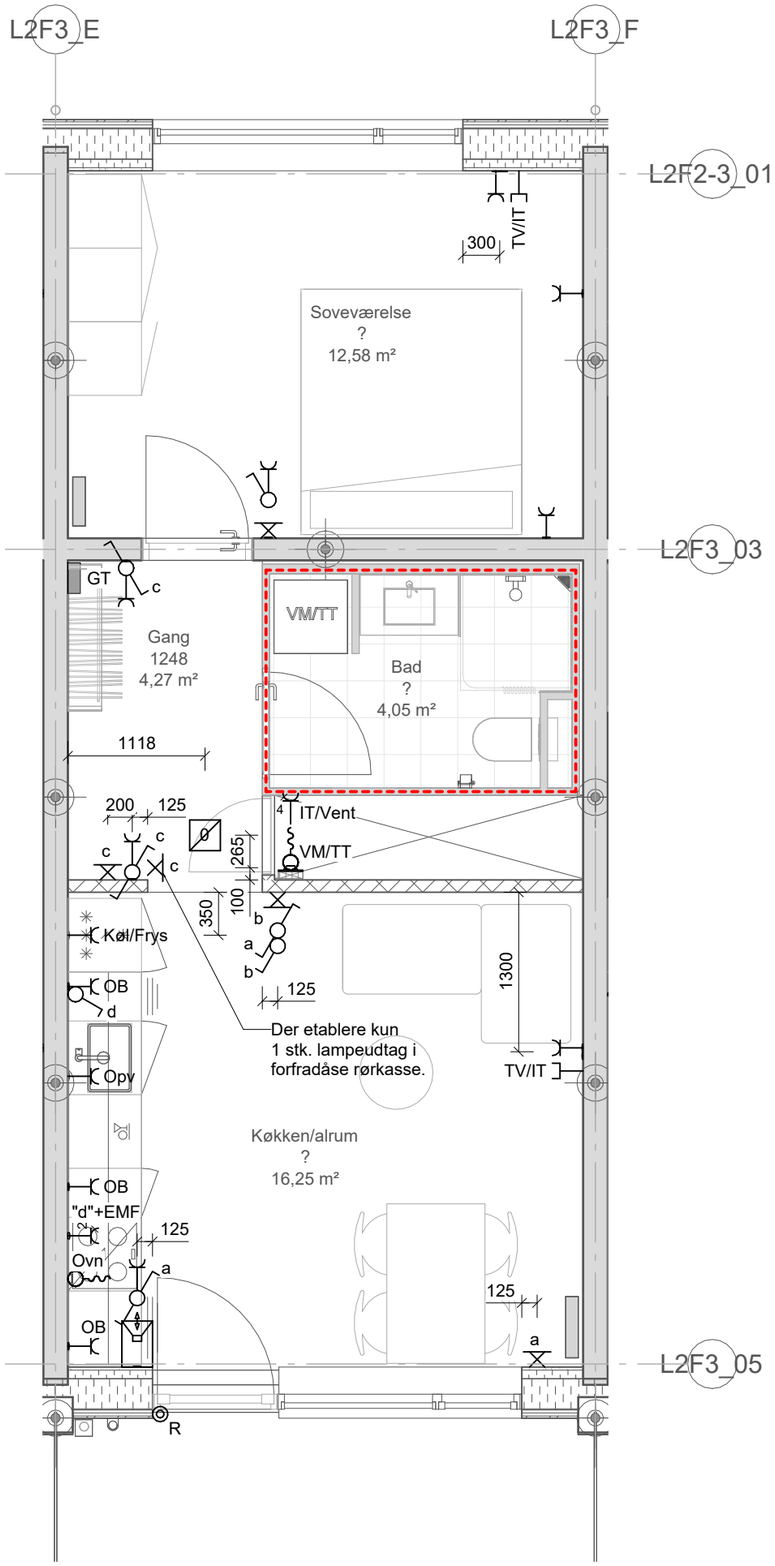

Projekt: Stejlepladsen


Tekst: Elinstallationer -
Byg F3 - 2. Sal, Byg B
ALT_2V_T01 - Side F3-18

Tegningsnr.: ISP2_K07_L2XX_H04_EFX_N931

Rev.:

Projektnr.: 1019198 | Dato: 2026-02-27 | Rev. Dato: | Mål: 1 : 50 | Side: F3-18

www.arteliagroup.dk | Fil:

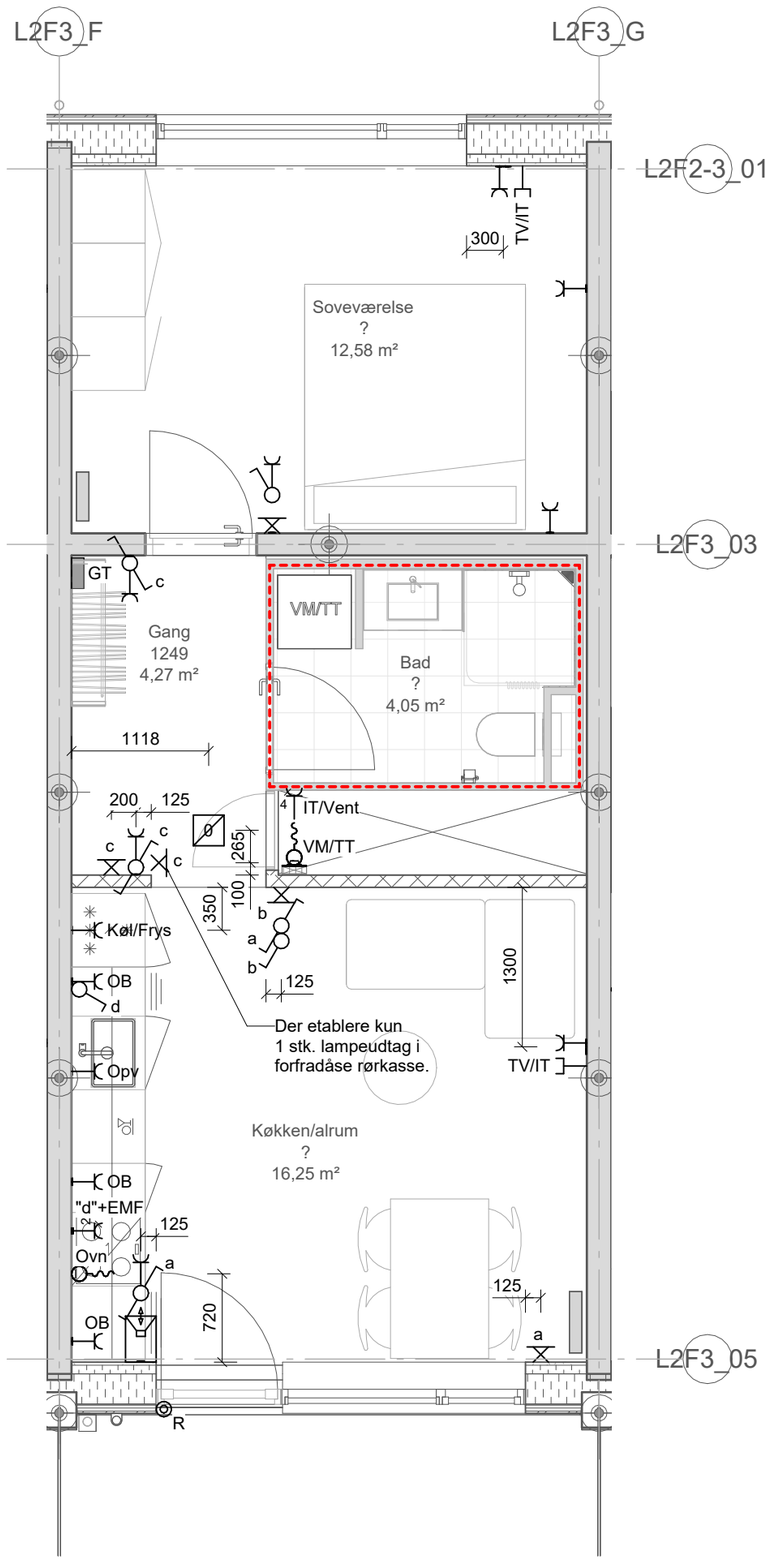

Projekt: Stejlepladsen

ARTELIA


Tekst: Elinstallationer -
Byg F3 - 2. Sal, Byg B
ALT_2V_T01 - Side F3-19

Tegningsnr.: ISP2_K07_L2XX_H04_EFX_N931

Rev.:

Projektnr.: 1019198 | Dato: 2026-02-27 | Rev. Dato: | Mål: 1 : 50 | Side: F3-19

www.arteliagroup.dk | Fil:

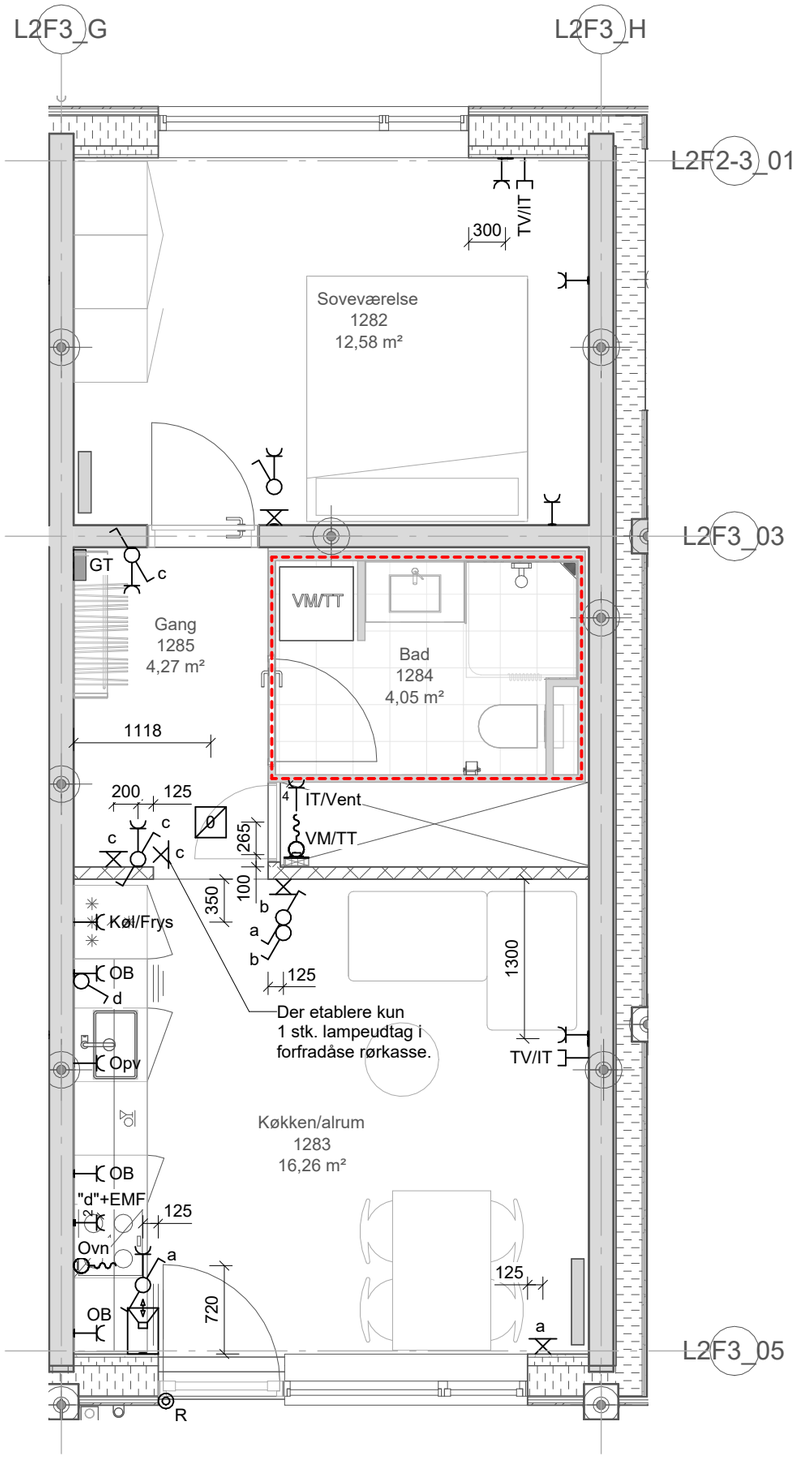

Projekt: Stejlepladsen


Tekst: Elinstallationer -
Byg F3 - 2. Sal, Byg B
ALT_2V_T01 - Side F3-20

Tegningsnr.: ISP2_K07_L2XX_H04_EFX_N931


Rev.:

Projektnr.: 1019198 | Dato: 2026-02-27 | Rev. Dato: | Mål: 1 : 50 | Side: F3-20

www.arteliagroup.dk | Fil:

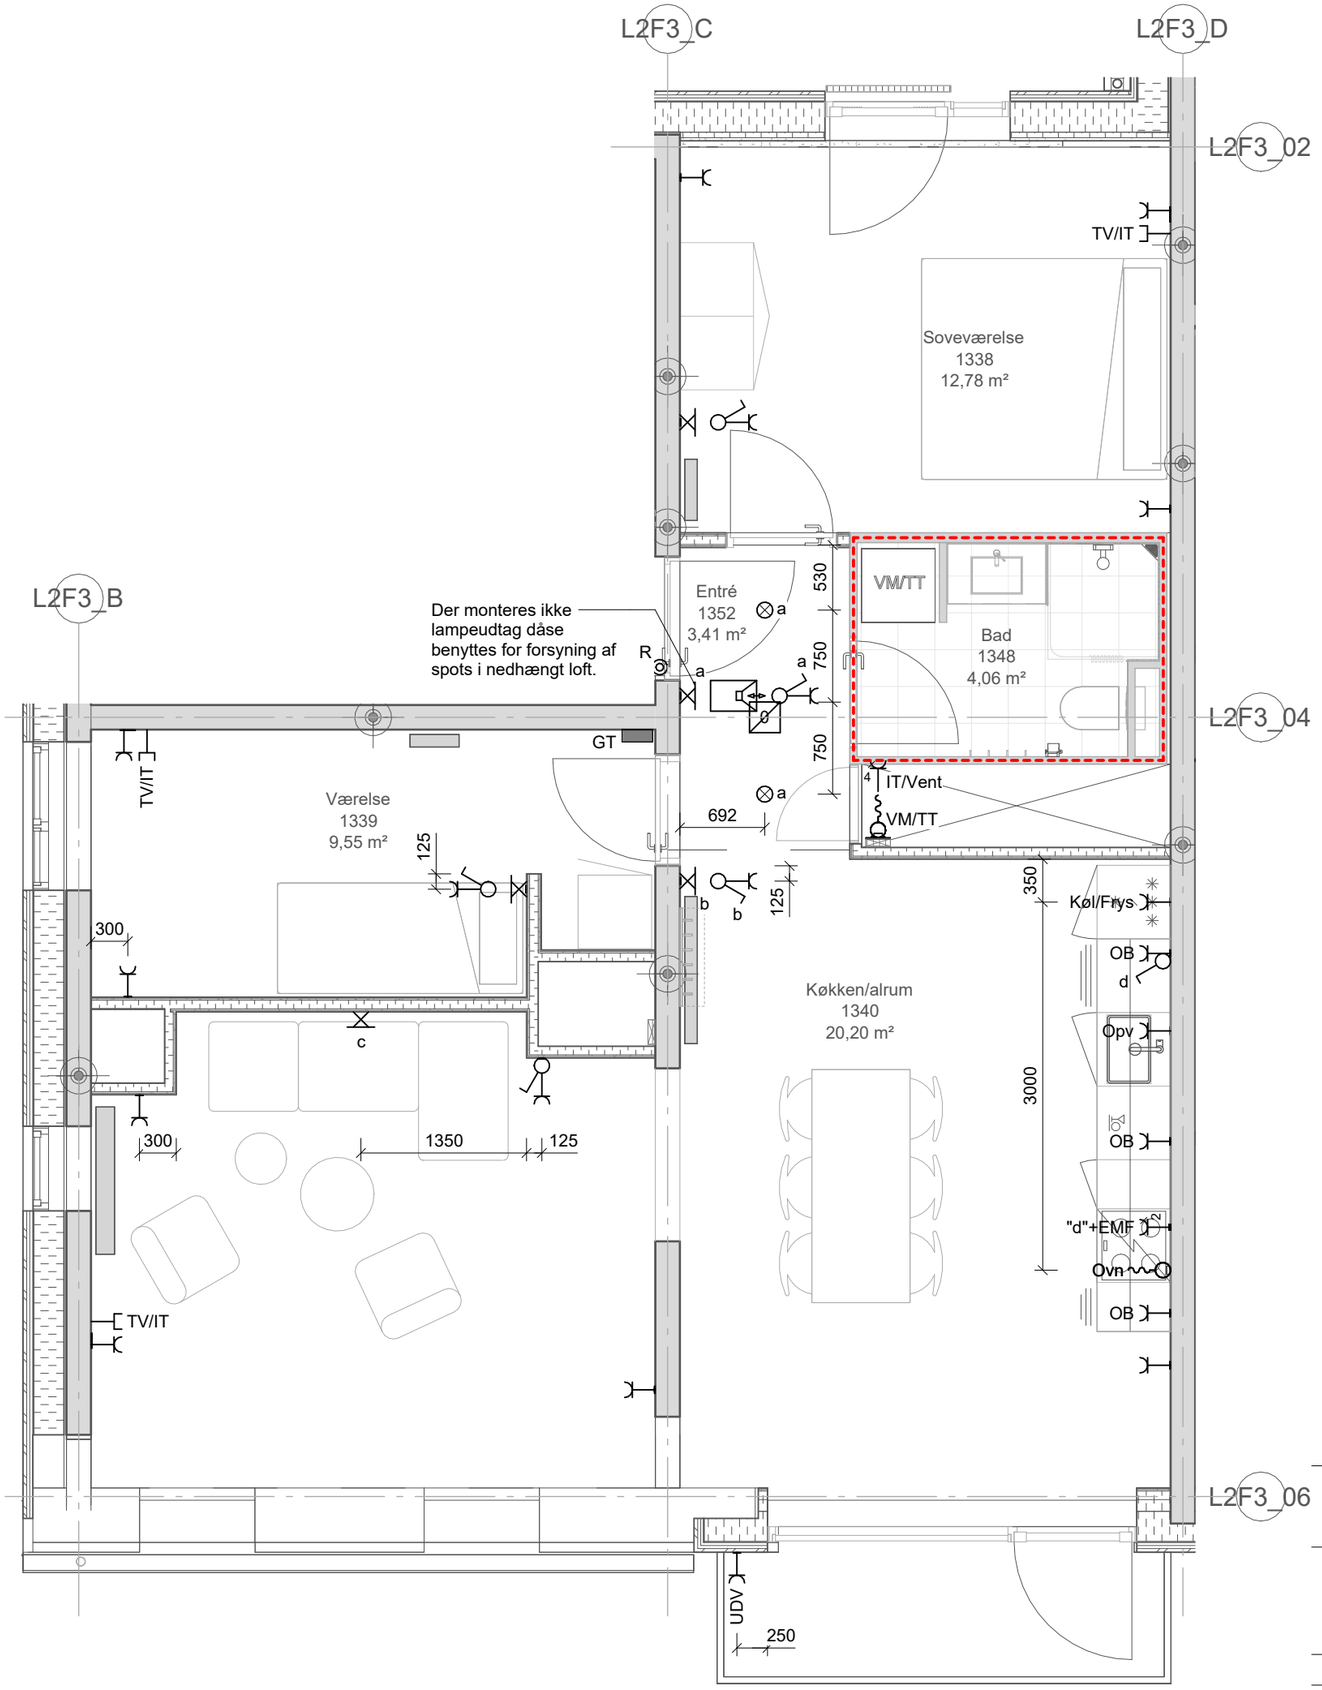

Projekt:	Stejlepladsen				
Tekst:	Elinstallationer - Byg F3 - 3. Sal, Byg A OPG_3V_T33_TA - Side F3-21			Tegningsnr.:	Rev.:
				ISP2_K07_L2XX_H04_EXX_N931	
Projektnr.: 1019198	Dato: 2026-02-27	Rev. Dato:		Mål: 1 : 50	Side: F3-21
www.arteliagroup.dk	Fil:				

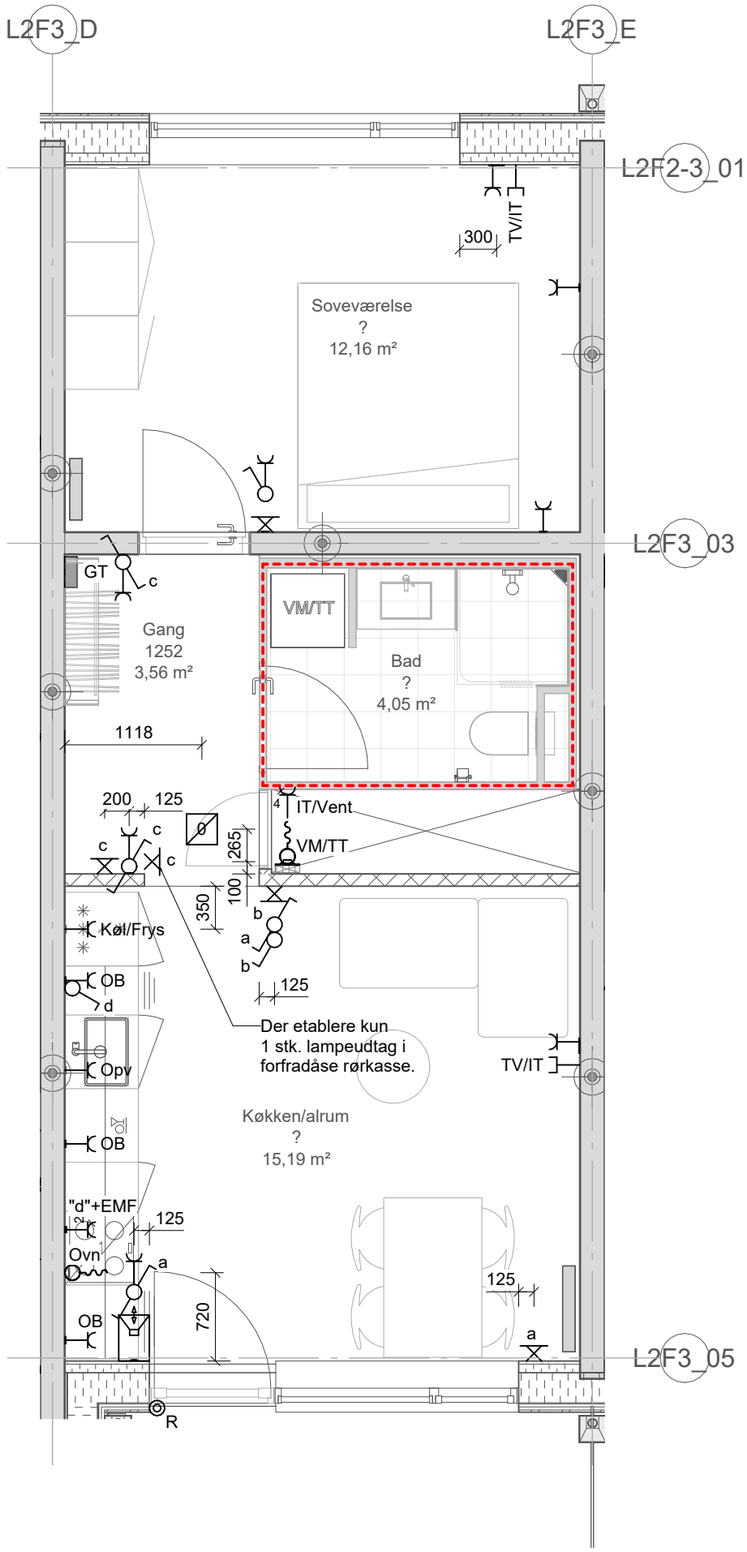

Projekt: Stejlepladsen


Tekst: Elinstallationer -
Byg F3 - 3. Sal, Byg B
ALT_2V_T01 - Side F3-22

Tegningsnr.: ISP2_K07_L2XX_H04_EFX_N931

Rev.:

Projektnr.: 1019198 | Dato: 2026-02-27 | Rev. Dato: | Mål: 1 : 50 | Side: F3-22

www.arteliagroup.dk | Fil:

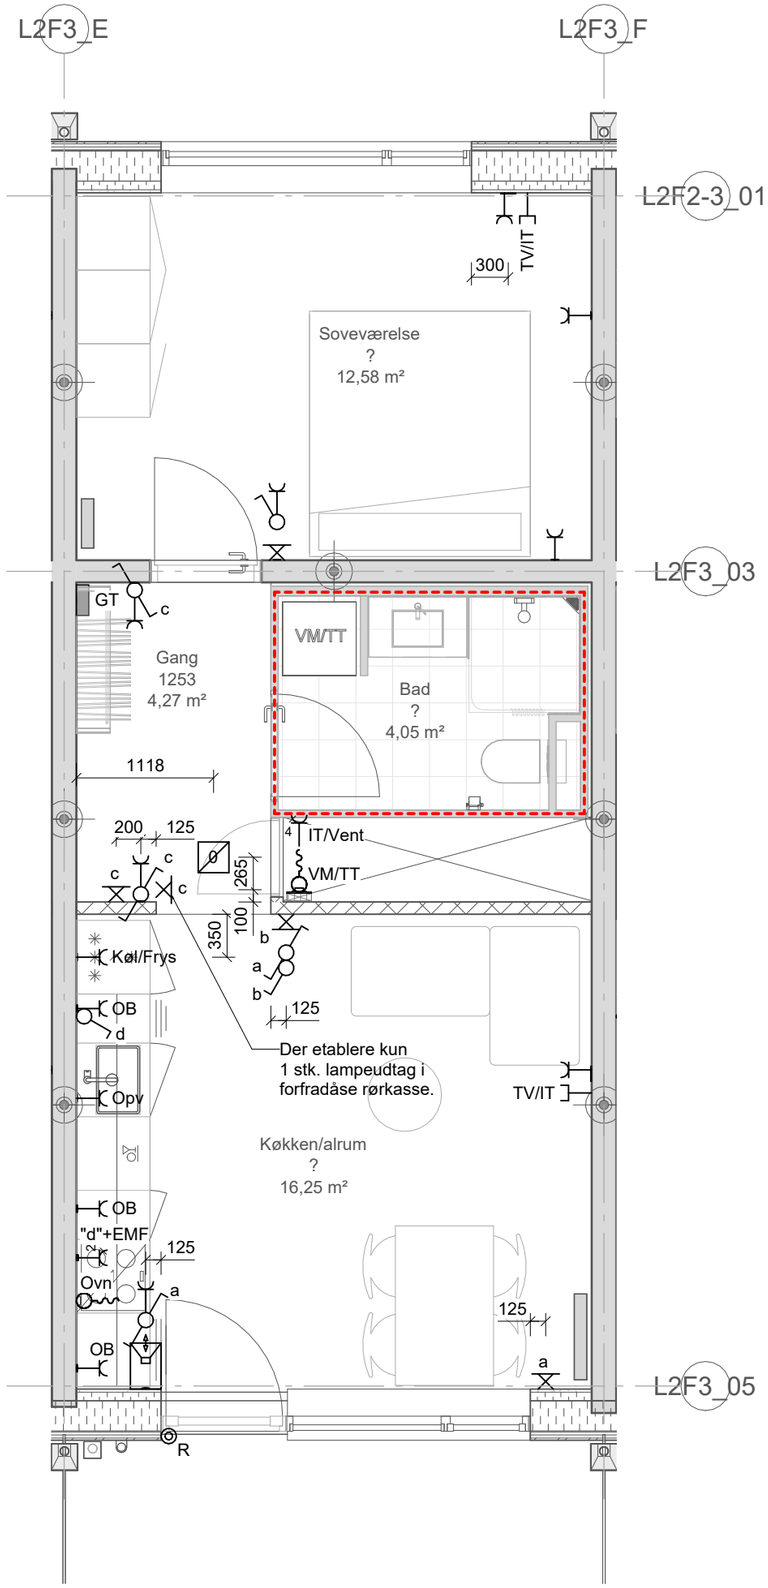

Projekt: Stejlepladsen


Tekst: Elinstallationer -
Byg F3 - 3. Sal, Byg B
ALT_2V_T01 - Side F3-23

Tegningsnr.: ISP2_K07_L2XX_H04_EFX_N931

Rev.:

Projektnr.: 1019198 | Dato: 2026-02-27 | Rev. Dato: | Mål: 1 : 50 | Side: F3-23

www.arteliagroup.dk | Fil:

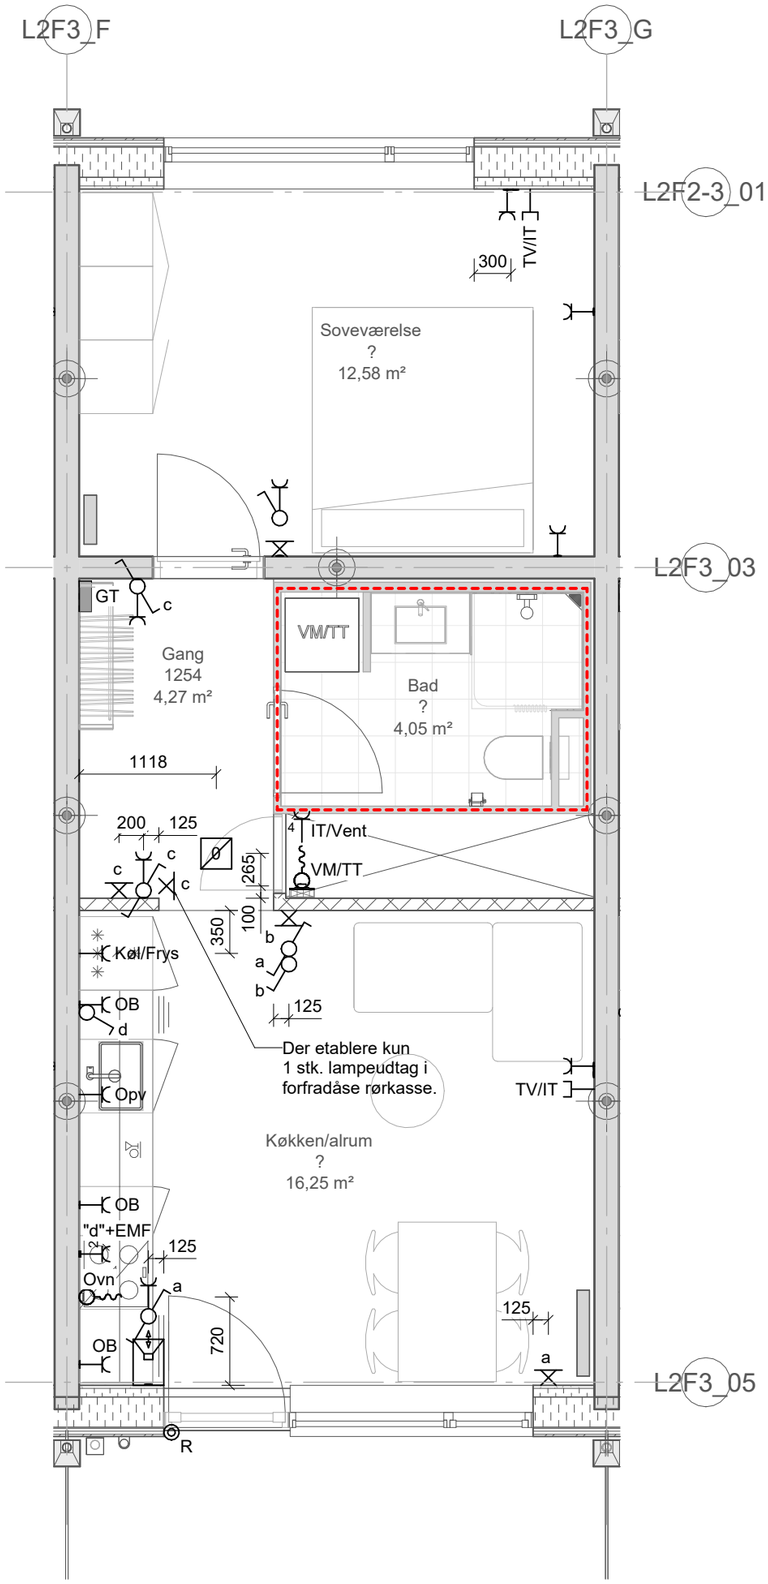

Projekt: Stejlepladsen


Tekst: Elinstallationer -
Byg F3 - 3. Sal, Byg B
ALT_2V_T01 - Side F3-24

Tegningsnr.: ISP2_K07_L2XX_H04_EFX_N931

Rev.:

Projektnr.: 1019198 | Dato: 2026-02-27 | Rev. Dato: | Mål: 1 : 50 | Side: F3-24

www.arteliagroup.dk | Fil:

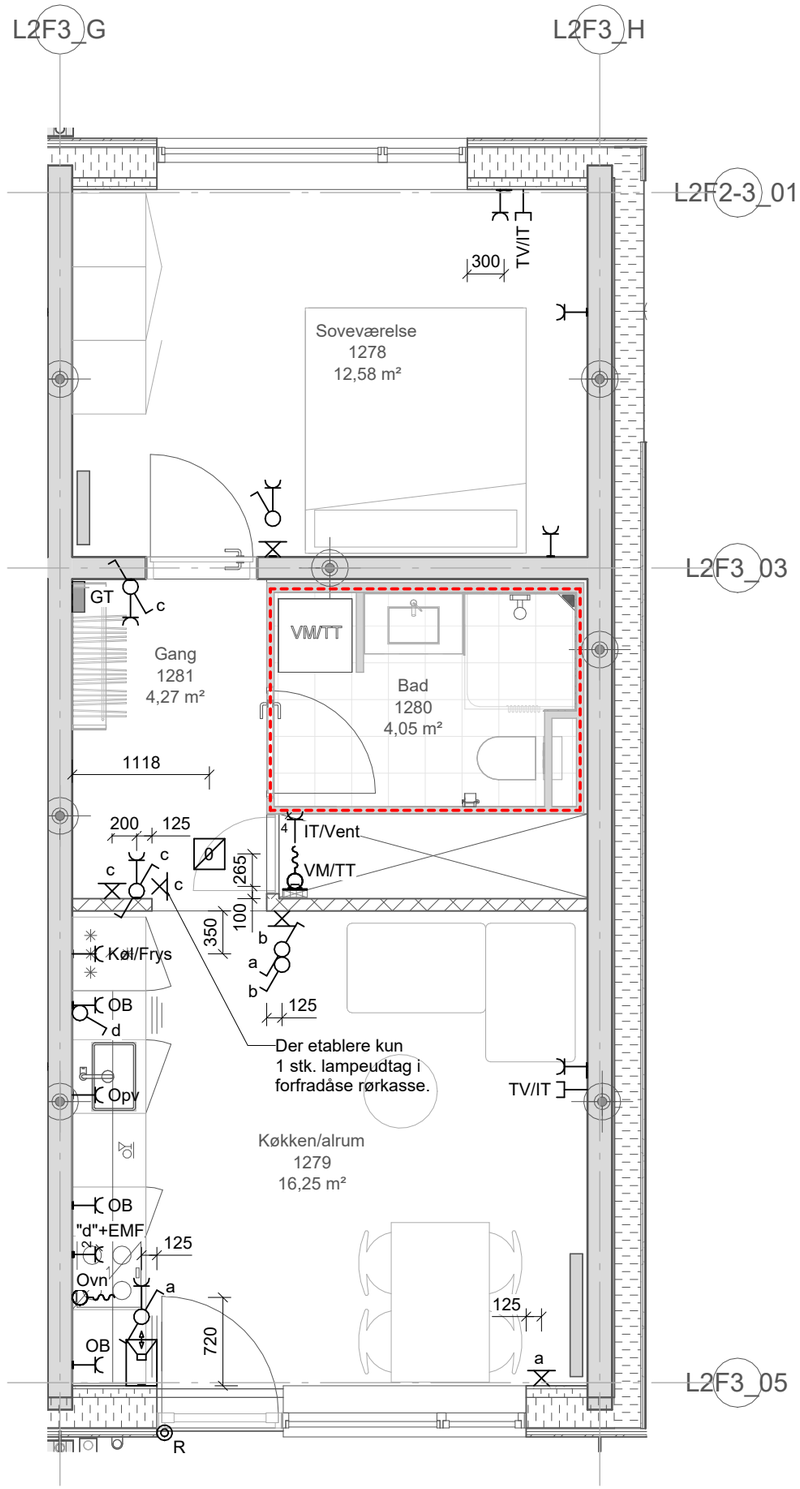

Projekt: Stejlepladsen

Tekst: Elinstallationer -
Byg F3 - 3. Sal, Byg B
ALT_2V_T01 - Side F3-25

Tegningsnr.: ISP2_K07_L2XX_H04_EFX_N931

Rev.:

Projektnr.: 1019198 | Dato: 2026-02-27 | Rev. Dato: | Mål: 1 : 50 | Side: F3-25

www.arteliagroup.dk | Fil: