Sheet Number	Tekst:	Dato:	Rev.:	Rev. Dato:
ISP2_K07_L2XX_H04_EFX_N931 - Side F5-1	Byg F5 - Index	2026-02-27		
ISP2_K07_L2XX_H04_EFX_N931 - Side F5-2	Byg F5 - Oversigtsplan	2026-02-27		
ISP2_K07_L2XX_H04_EFX_N931 - Side F5-3	Byg F5 - Stueplan	2026-02-27		
ISP2_K07_L2XX_H04_EFX_N931 - Side F5-4	Byg F5 - Stueplan	2026-02-27		
ISP2_K07_L2XX_H04_EFX_N931 - Side F5-5	Byg F5 - Stueplan	2026-02-27		
ISP2_K07_L2XX_H04_EFX_N931 - Side F5-6	Byg F5 - Stueplan	2026-02-27		
ISP2_K07_L2XX_H04_EFX_N931 - Side F5-7	Byg F5 - 1. til 3. Sal	2026-02-27	1	2026-05-19
ISP2_K07_L2XX_H04_EFX_N931 - Side F5-8	Byg F5 - 1. til 3. Sal	2026-02-27	1	2026-05-19
ISP2_K07_L2XX_H04_EFX_N931 - Side F5-9	Byg F5 - 1. til 3. Sal	2026-02-27	1	2026-05-19
ISP2_K07_L2XX_H04_EFX_N931 - Side F5-10	Byg F5 - 1. til 3. Sal	2026-02-27		

Projekt: Stejlepladsen

Tekst: Elinstallationer - Byg F5 - Index


Tegningsnr.: ISP2_K07_L2XX_H04_EFX_N931

Rev.:


Projektnr.: 1019198 | Dato: 2026-02-27 | Rev. Dato: | Mål: | Side: F5-1

www.arteliagroup.dk | Fil:


Stueplan - Byg F5

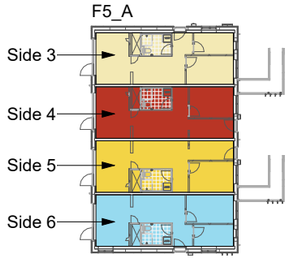


1. sal - Byg F5

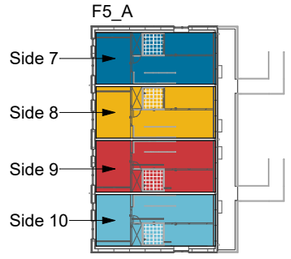

2. sal - Byg F5

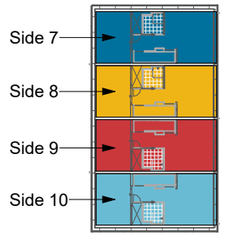

3. sal - Byg F5

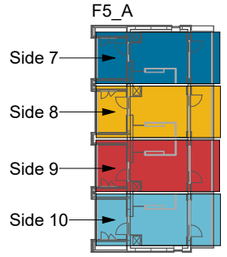

Oversigt, bygning F5:

Side 3:	Duplexhuse, Byg A, st., 2,5V
Side 4:	Duplexhuse, Byg A, st., 2V
Side 5:	Duplexhuse, Byg A, st., 2V
Side 6:	Duplexhuse, Byg A, st., 2,5V
Side 7:	Duplexhuse, Byg A, 1. til 3. Sal, 5V
Side 8:	Duplexhuse, Byg A, 1. til 3. Sal, 5V
Side 9:	Duplexhuse, Byg A, 1. til 3. Sal, 5V
Side 10:	Duplexhuse, Byg A, 1. til 3. Sal, 5V

Projekt: Stejlepladsen


Tekst: Elinstallationer - Byg F5 - Oversigtsplan

Tegningsnr.: ISP2_K07_L2XX_H04_EFX_N931


Rev.:

Projektnr.: 1019198 | Dato: 2026-02-27 | Rev. Dato: | Mål: 1 : 500 | Side: F5-2


www.arteliagroup.dk | Fil:

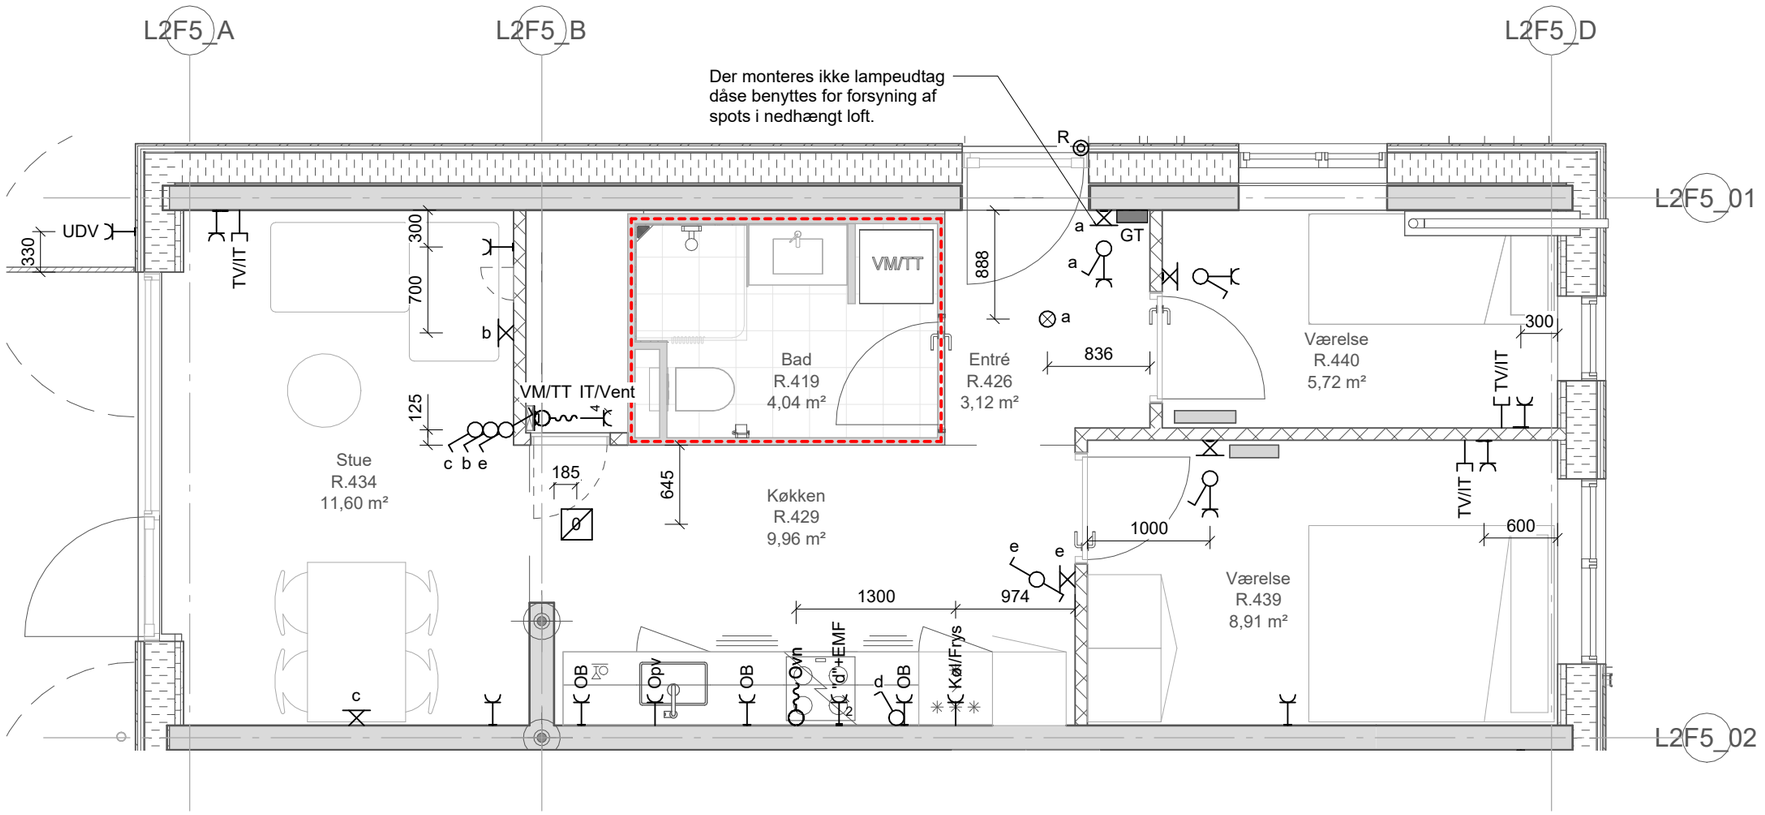


Projekt:	Stejlepladsen				
Tekst:	Elinstallationer - Byg F5 - Stueplan DUP_2,5V_T30_ST - Side F5-3			Tegningsnr.:	Rev.:
				ISP2_K07_L2XX_H04_EXX_N931	
Projektnr.: 1019198	Dato: 2026-02-27	Rev. Dato:		Mål: 1 : 50	Side: F5-3
www.arteliagroup.dk	Fil:				

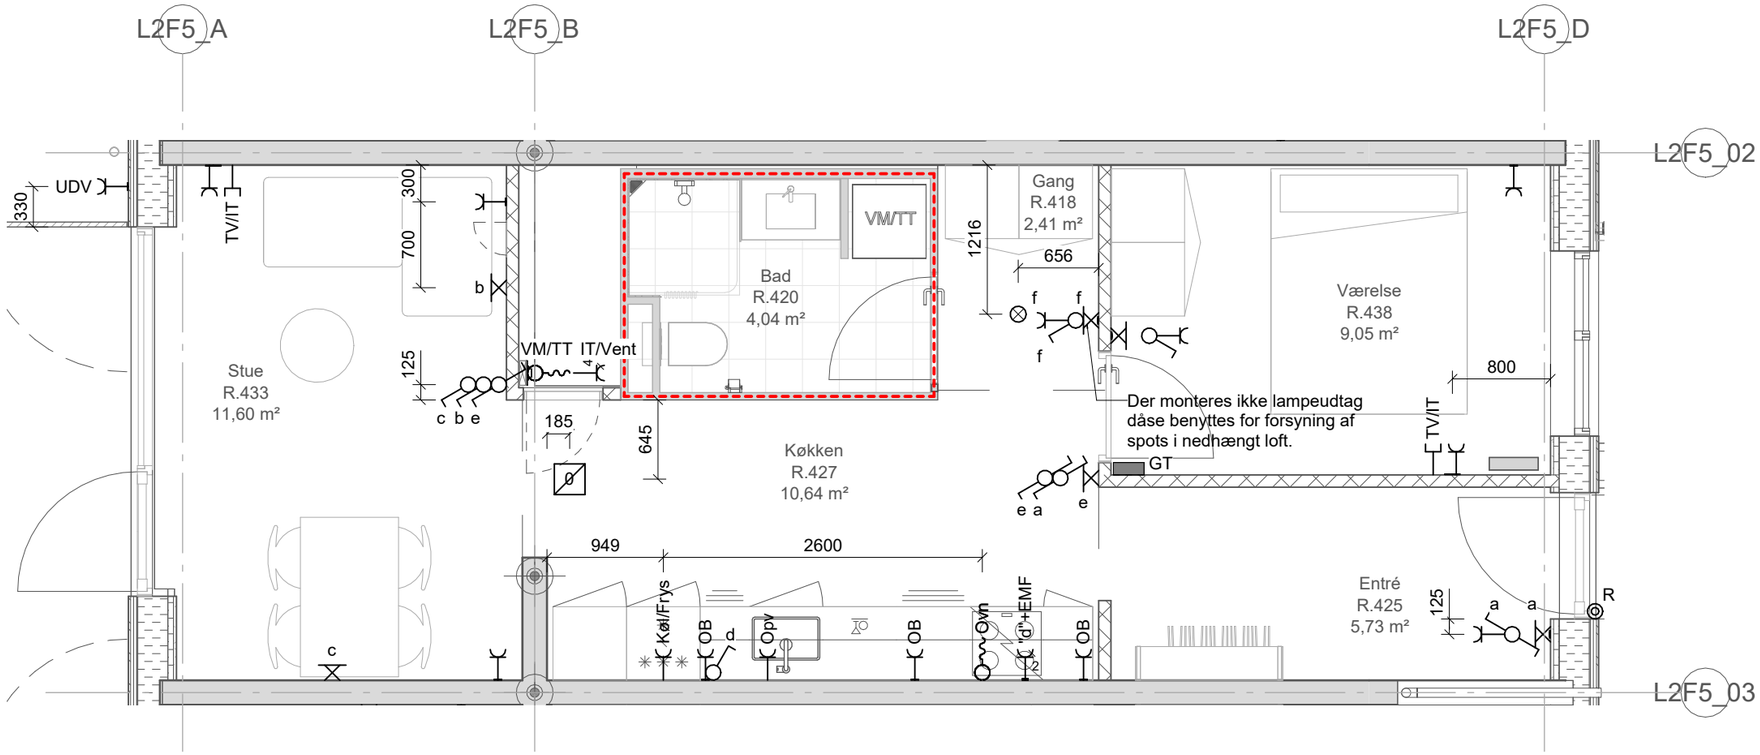

Projekt:	Stejlepladsen				
Tekst:	Elinstallationer - Byg F5 - Stueplan DUP_2V_T30_ST - Side F5-4			Tegningsnr.:	Rev.:
				ISP2_K07_L2XX_H04_EXX_N931	
Projektnr.: 1019198	Dato: 2026-02-27	Rev. Dato:		Mål: 1 : 50	Side: F5-4
www.arteliagroup.dk	Fil:				

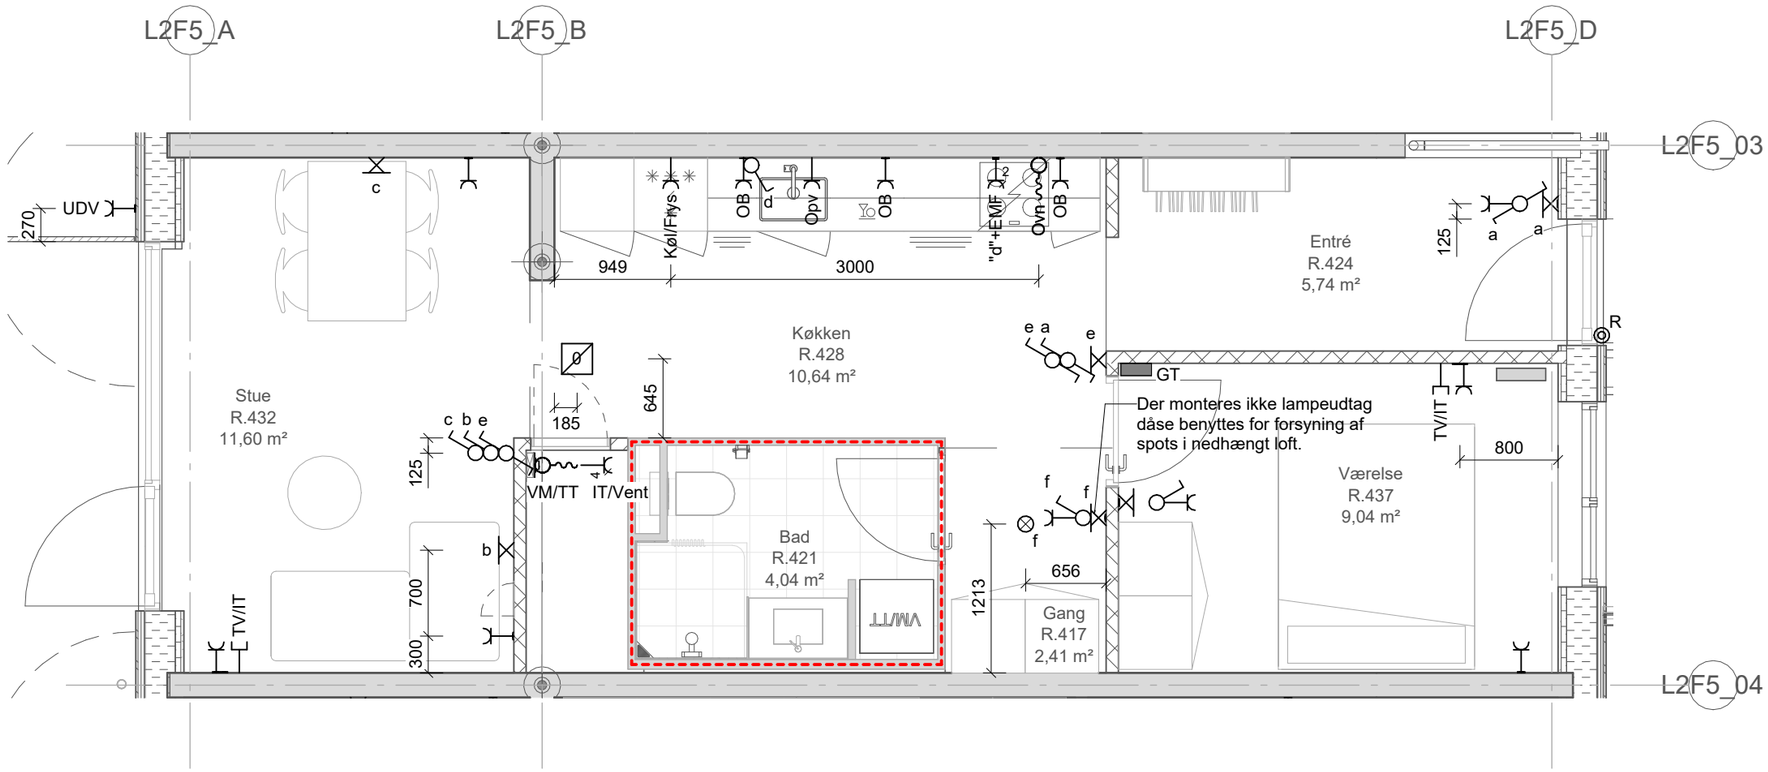

Projekt:	Stejlepladsen				
Tekst:	Elinstallationer - Byg F5 - Stueplan DUP_2V_T30_ST_S - Side F5-5			Tegningsnr.:	Rev.:
			ISP2_K07_L2XX_H04_EXX_N931		
Projektnr.: 1019198	Dato: 2026-02-27	Rev. Dato:		Mål: 1 : 50	Side: F5-5
www.arteliagroup.dk	Fil:				

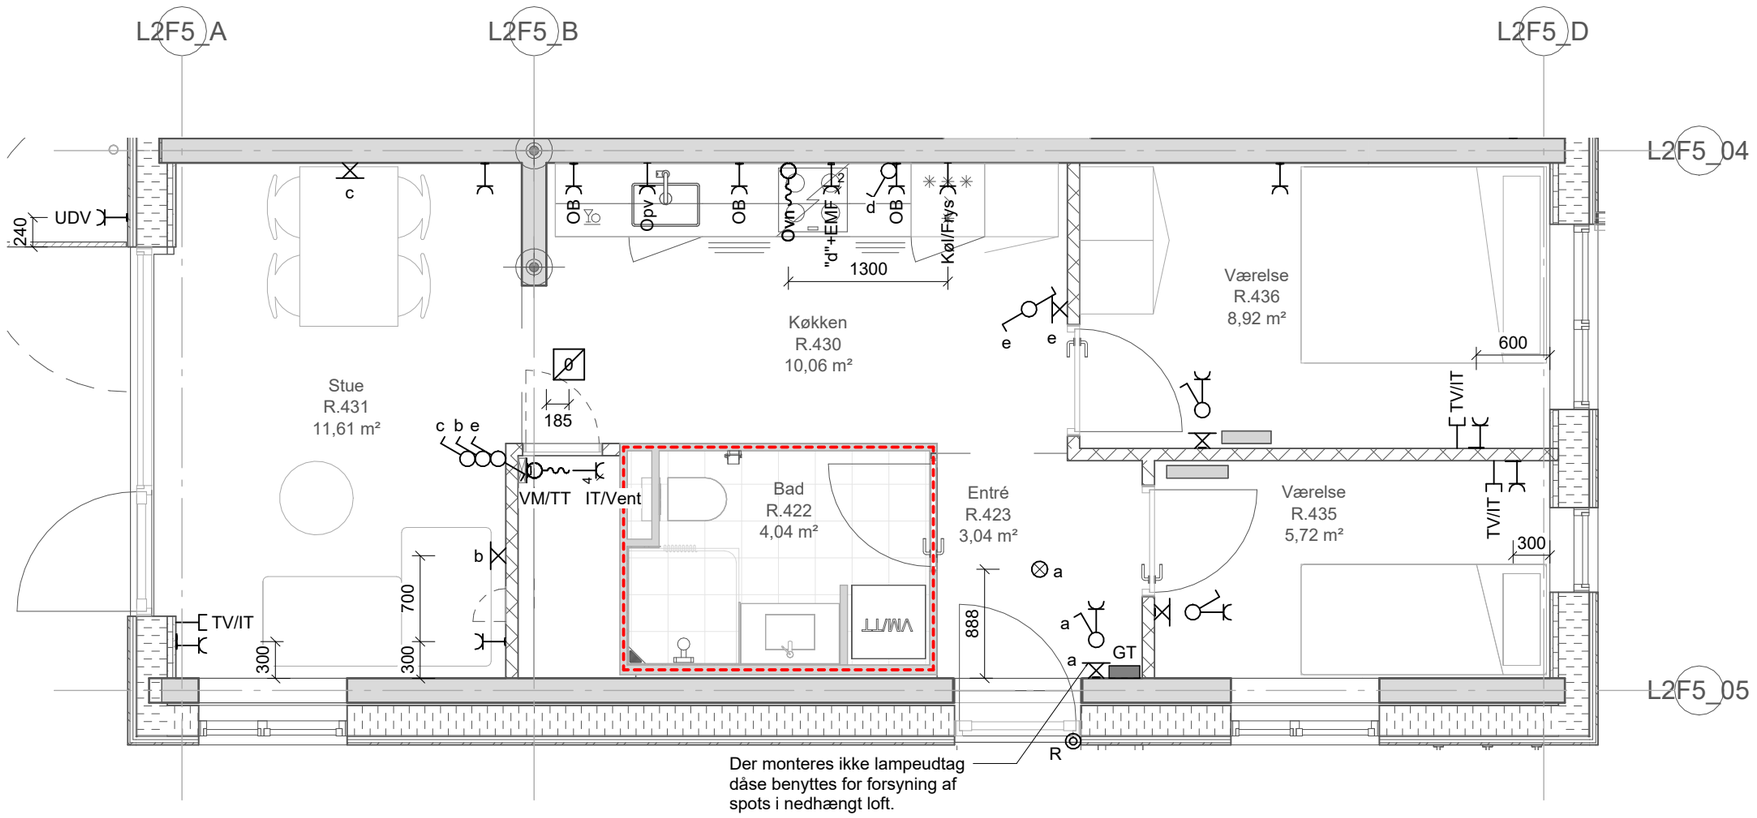

Projekt: Stejlepladsen


Tekst: Elinstallationer -
Byg F5 - Stueplan
DUP_2,5V_T30_ST_S - Side F5-6


Tegningsnr.: ISP2_K07_L2XX_H04_EXX_N931


Rev.:

Projektnr.: 1019198 | Dato: 2026-02-27 | Rev. Dato: | Mål: 1 : 50 | Side: F5-6

www.arteliagroup.dk | Fil:

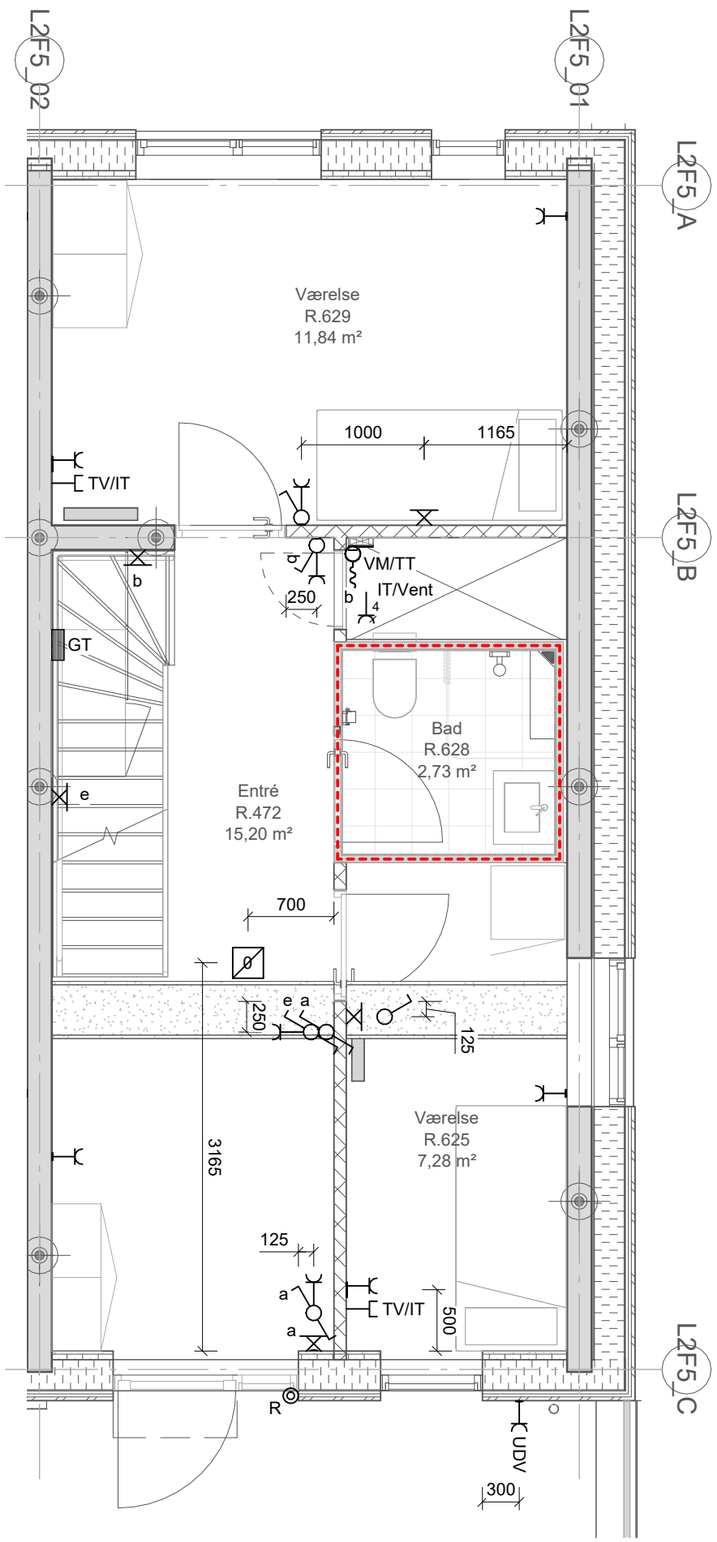

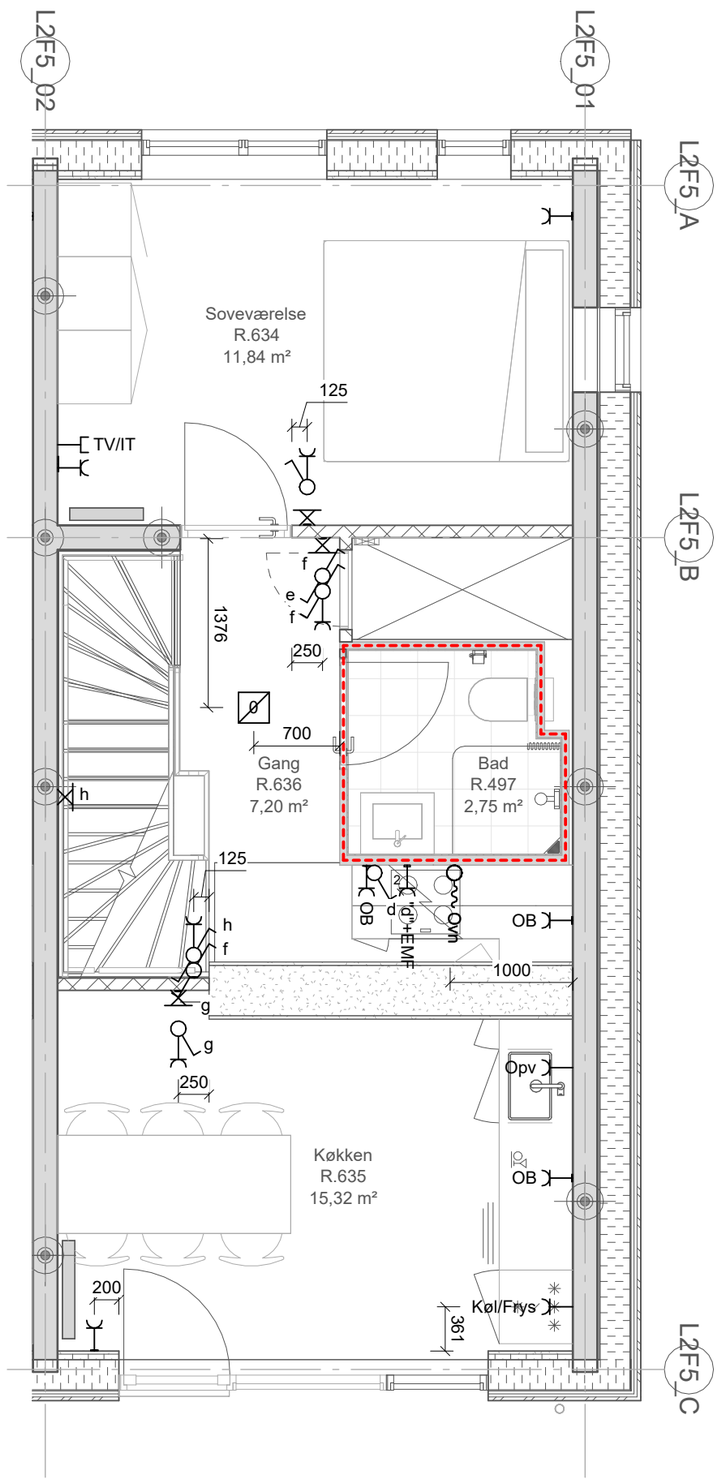

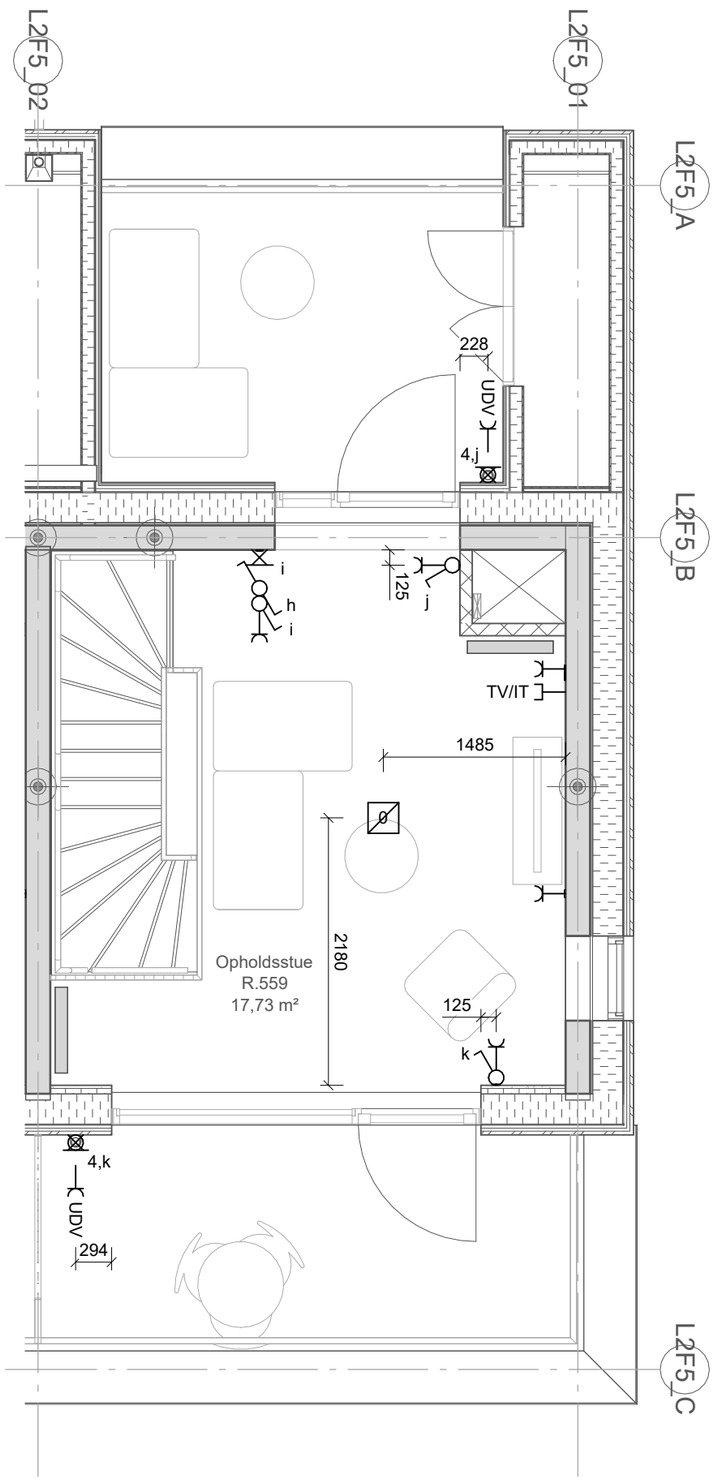

Projekt: Stejlepladsen


Tekst: Elinstallationer -
Byg F5 - 1. til 3. Sal
DUP_5V_T31_S - Side F5-7


Tegningsnr.: ISP2_K07_L2XX_H04_EFX_N931


Rev.: 1

Projektnr.: 1019198 | Dato: 2026-02-27 | Rev. Dato: 2026-05-19 | Mål: 1 : 50 | Side: F5-7

www.arteliagroup.dk | Fil:

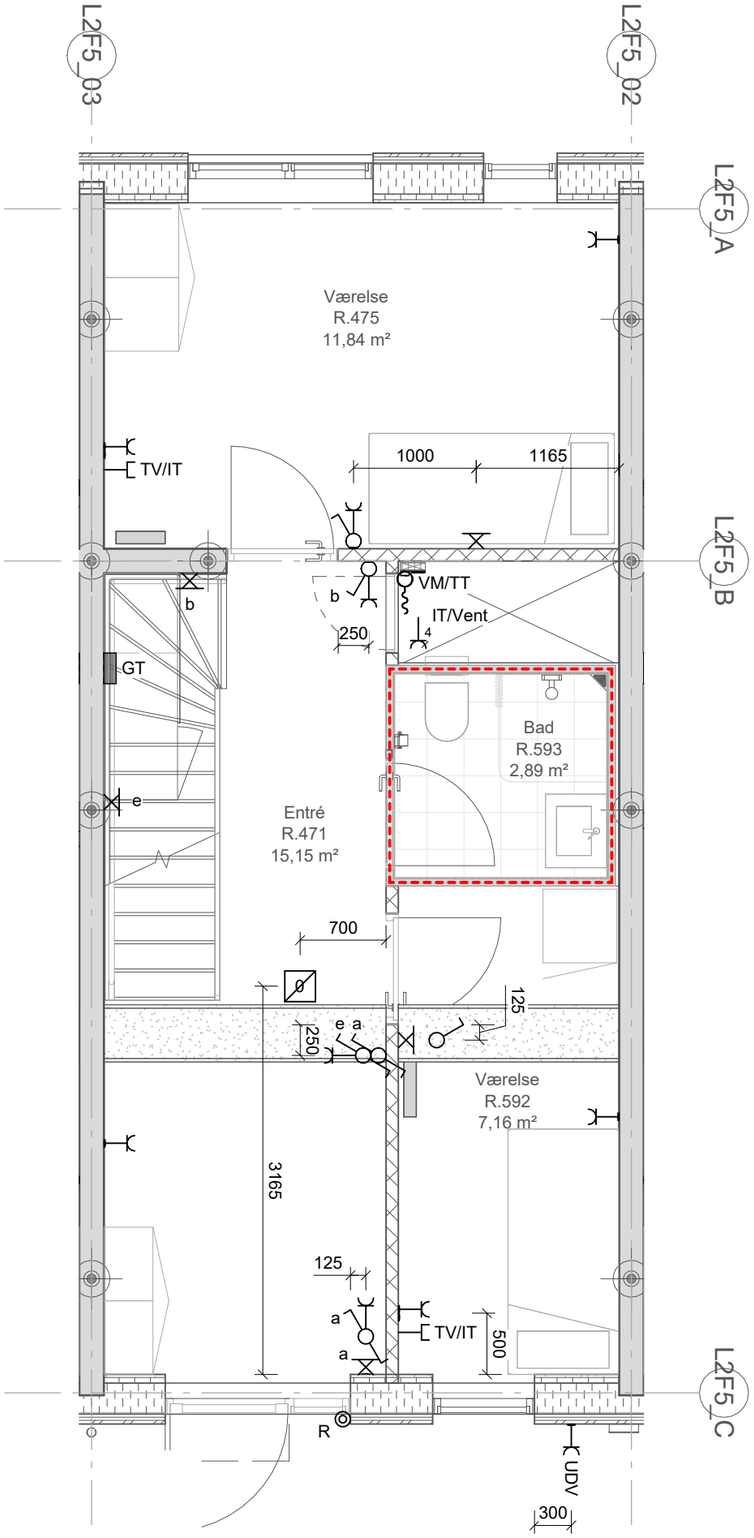

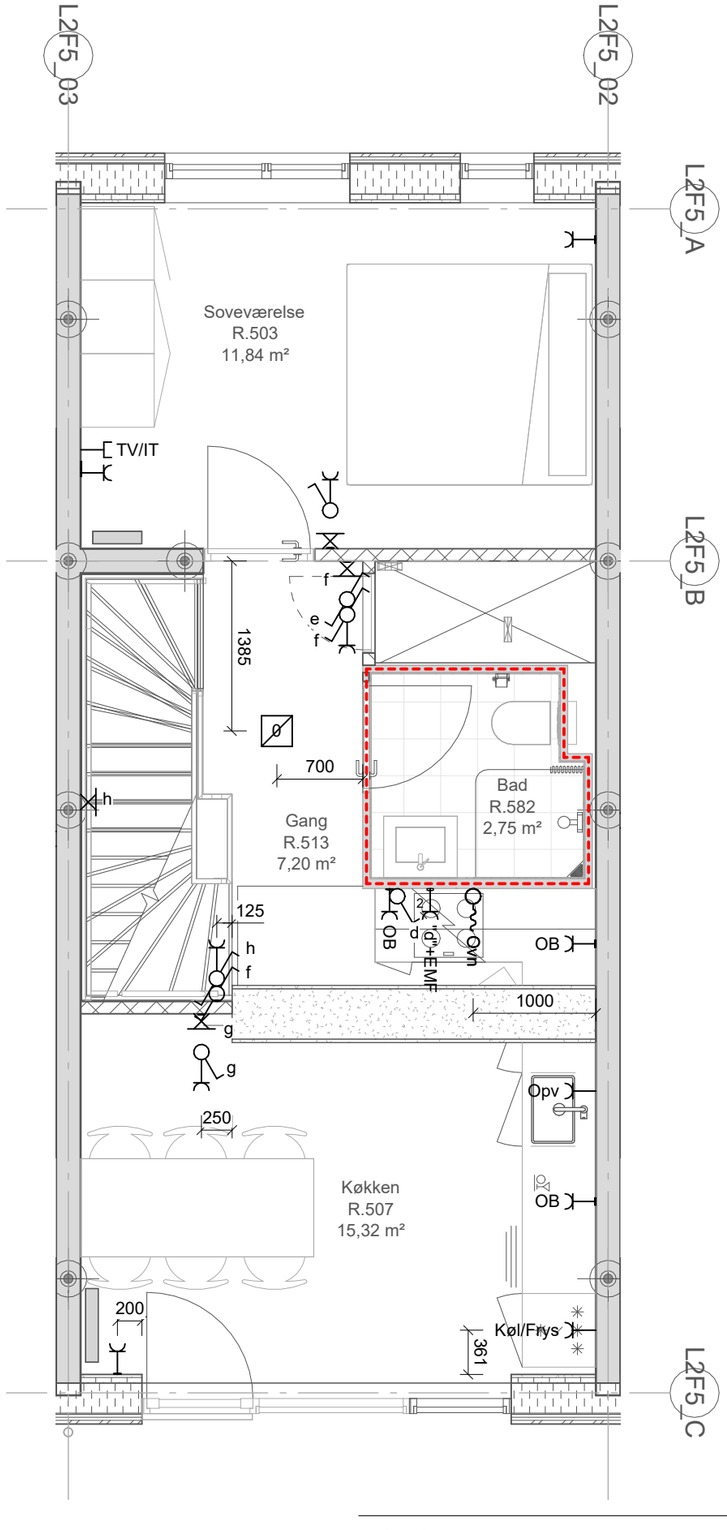

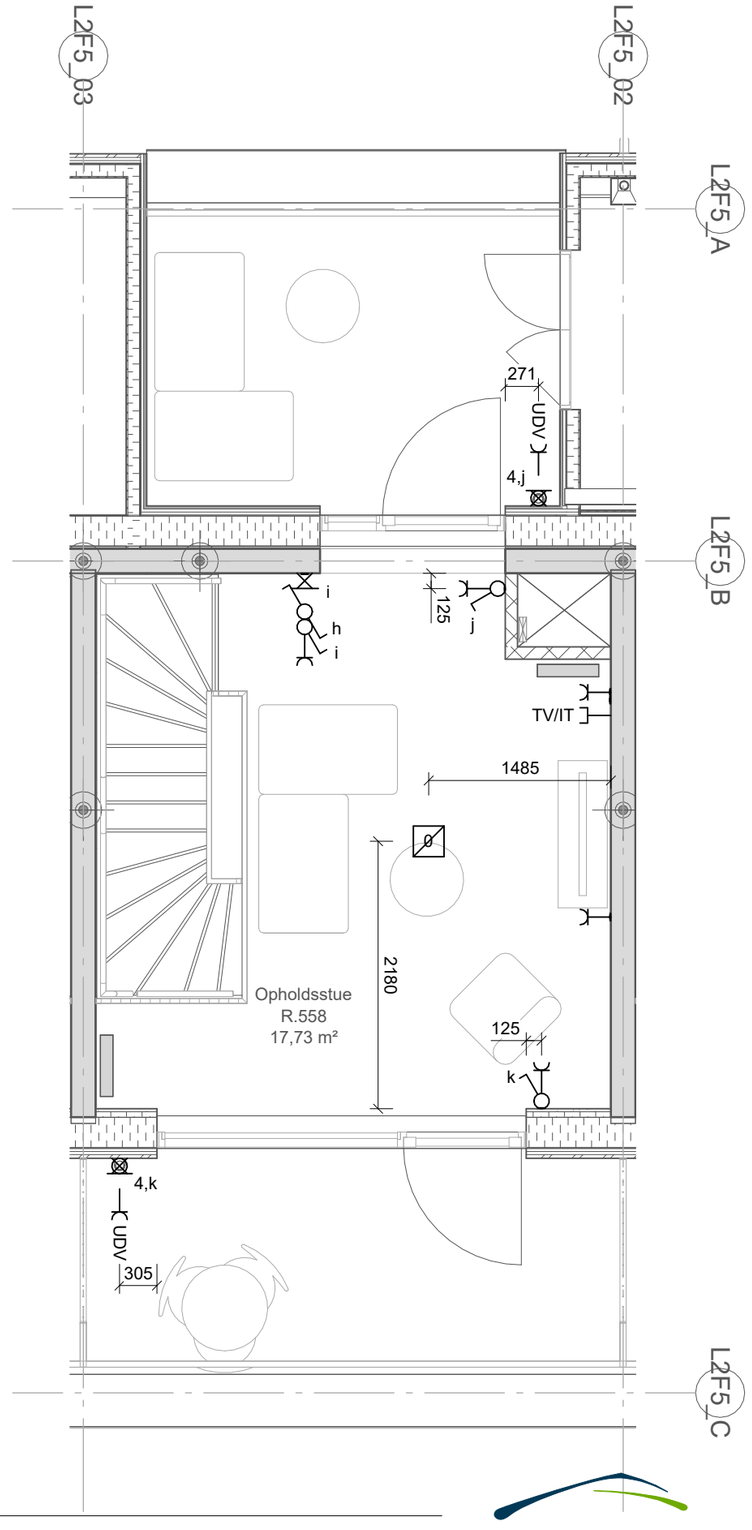

Projekt: Stejlepladsen


Tekst: Elinstallationer -
Byg F5 - 1. til 3. Sal
DUP_5V_T32_S - Side F5-8


Tegningsnr.: ISP2_K07_L2XX_H04_EXX_N931


Rev.: 1

Projektnr.: 1019198 | Dato: 2026-02-27 | Rev. Dato: 2026-05-19 | Mål: 1 : 50 | Side: F5-8

www.arteliagroup.dk | Fil:

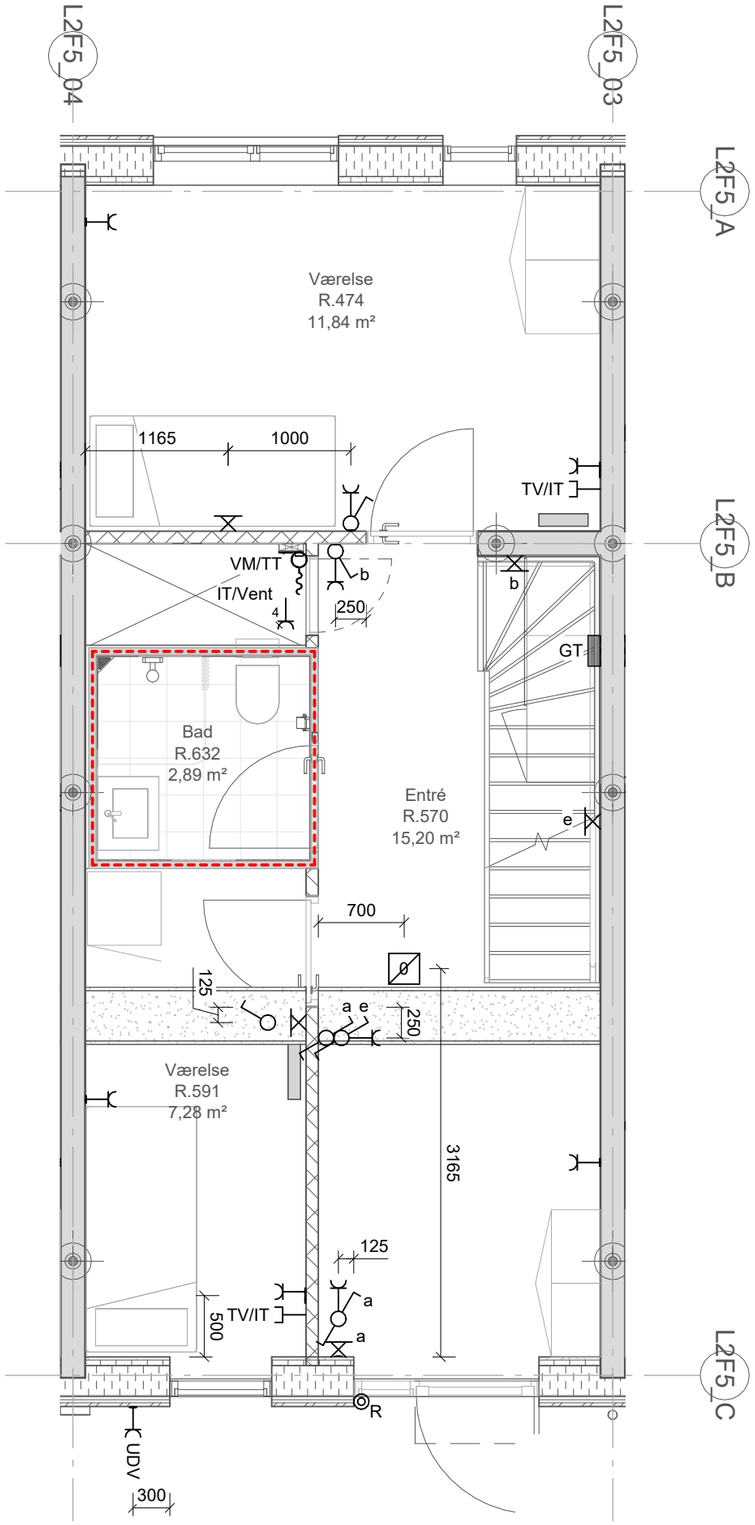

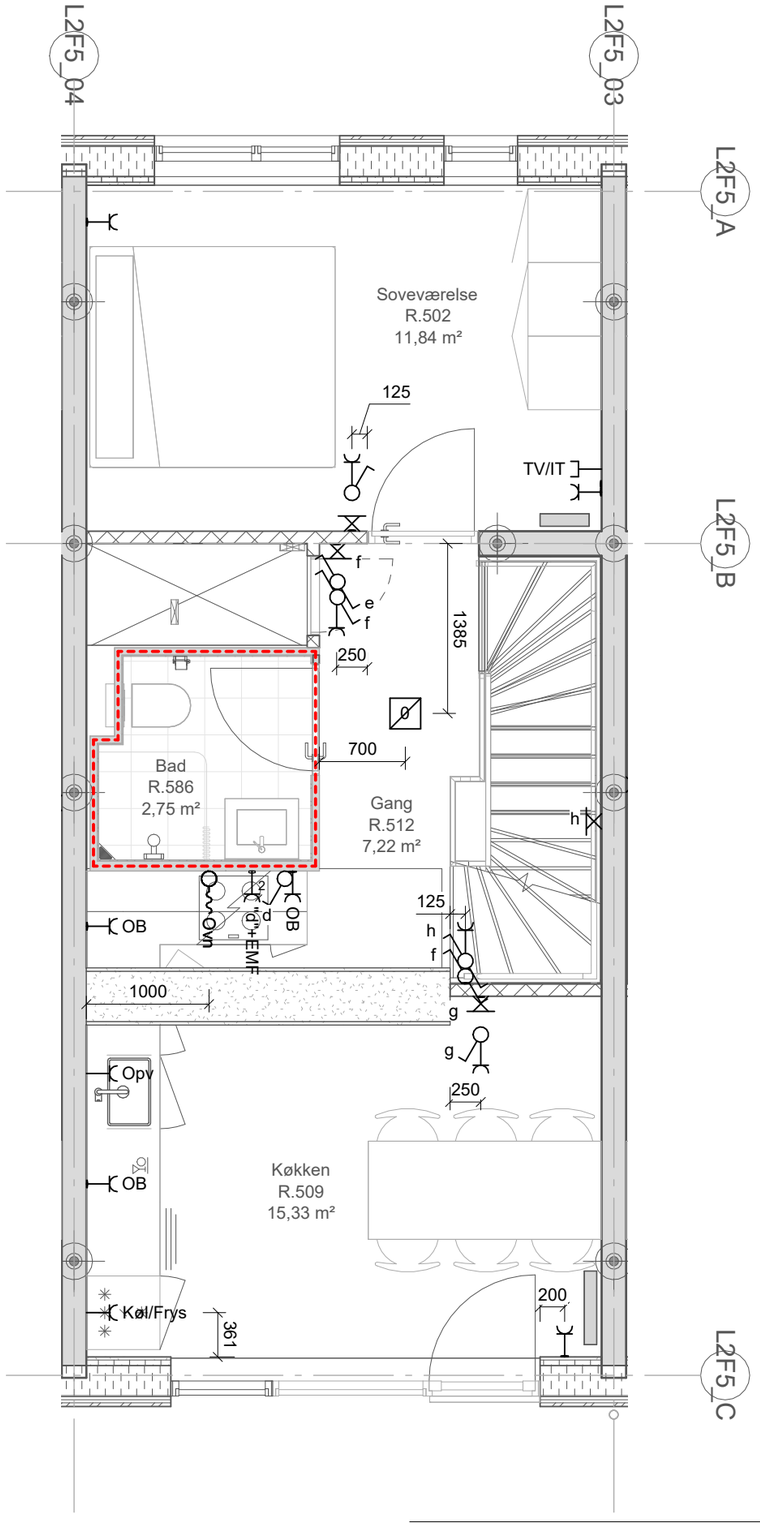

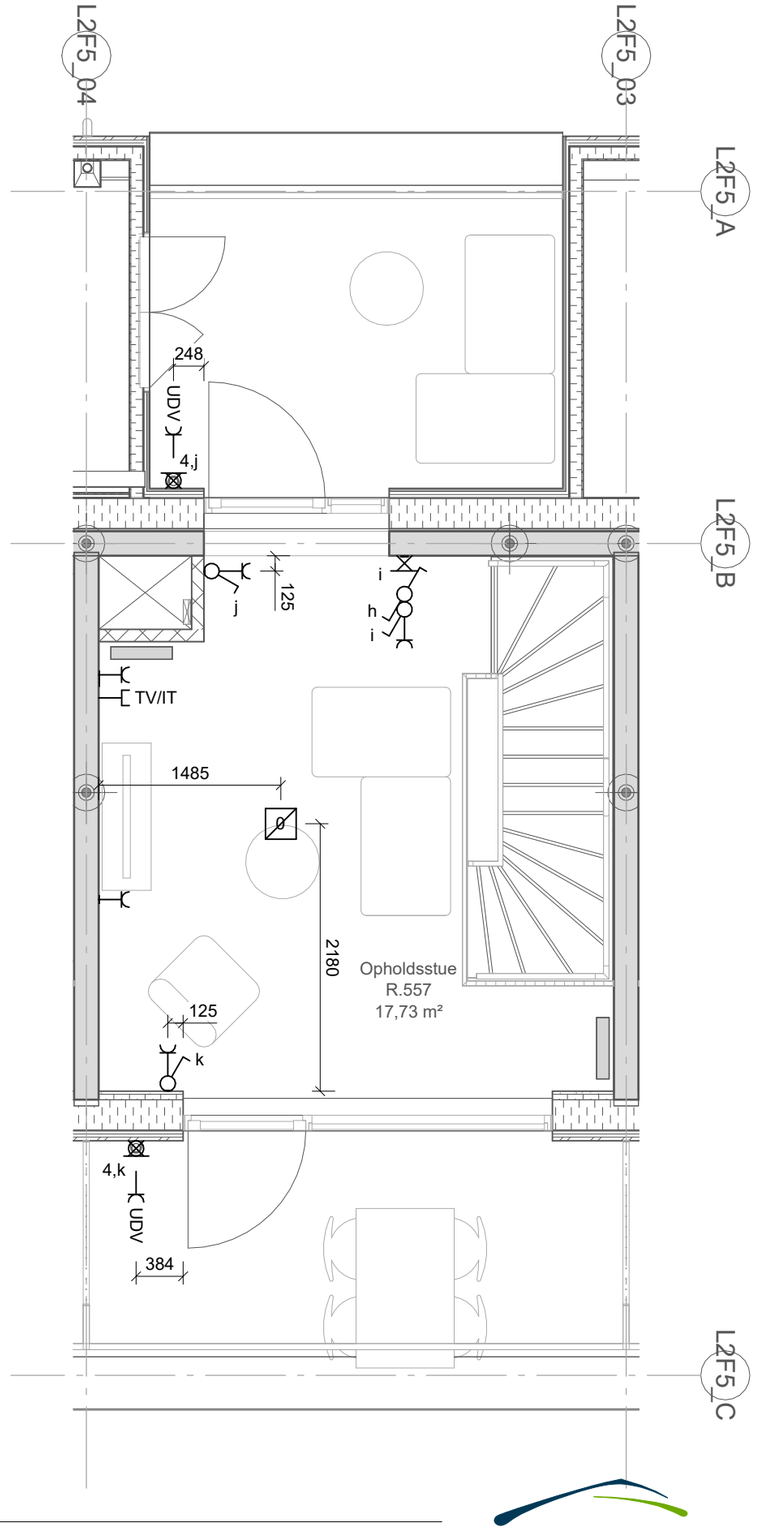

Projekt: Stejlepladsen


Tekst: Elinstallationer -
Byg F5 - 1. til 3. Sal
DUP_5V_T32 - Side F5-9


Tegningsnr.: ISP2_K07_L2XX_H04_EFX_N931


Rev.: 1

Projektnr.: 1019198 | Dato: 2026-02-27 | Rev. Dato: 2026-05-19 | Mål: 1 : 50 | Side: F5-9

www.arteliagroup.dk | Fil:

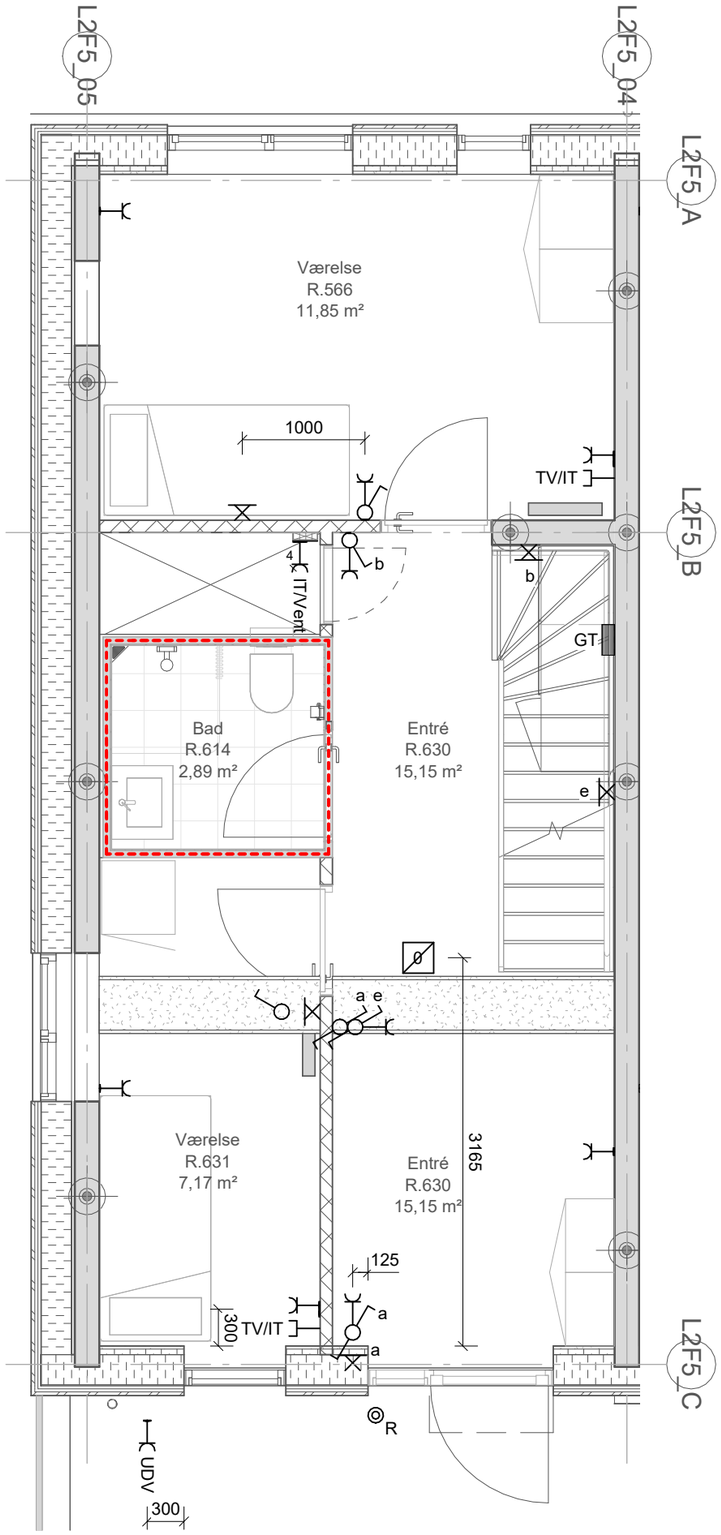

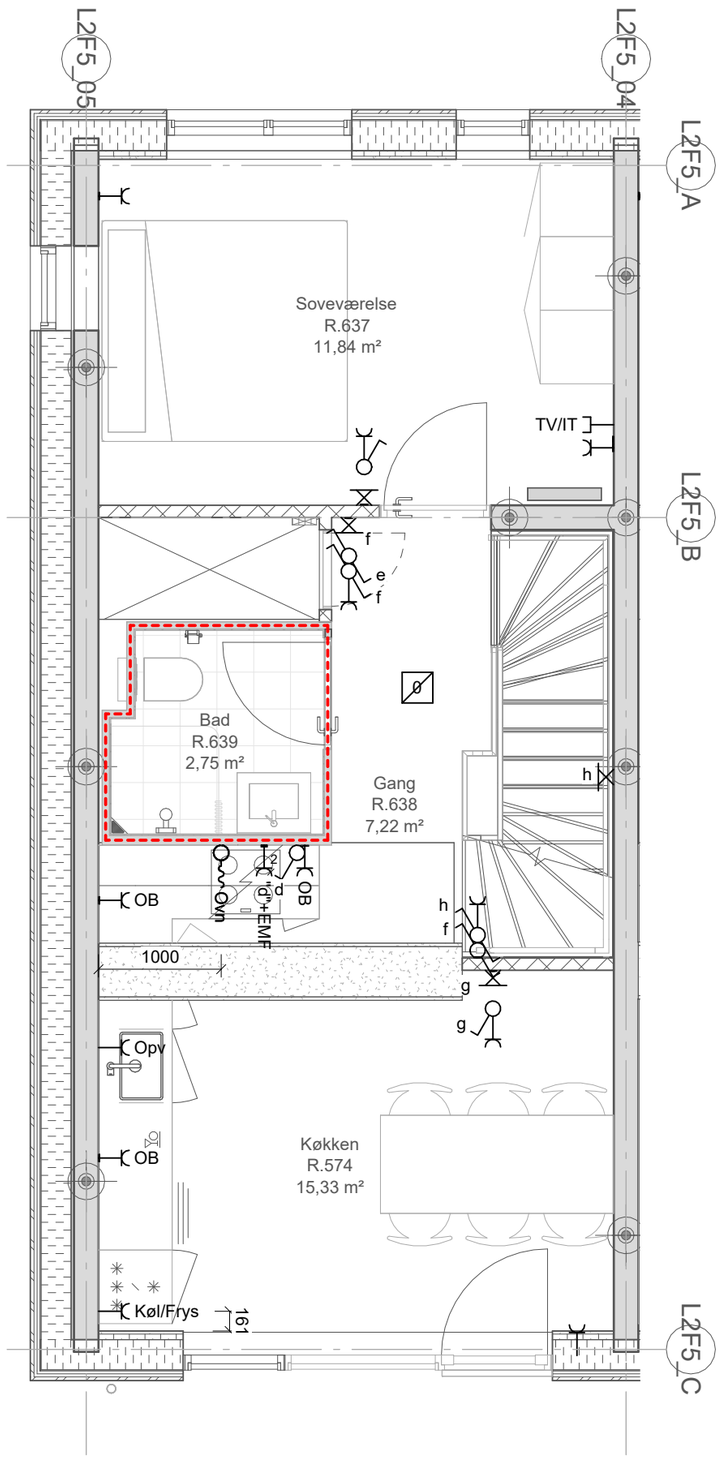

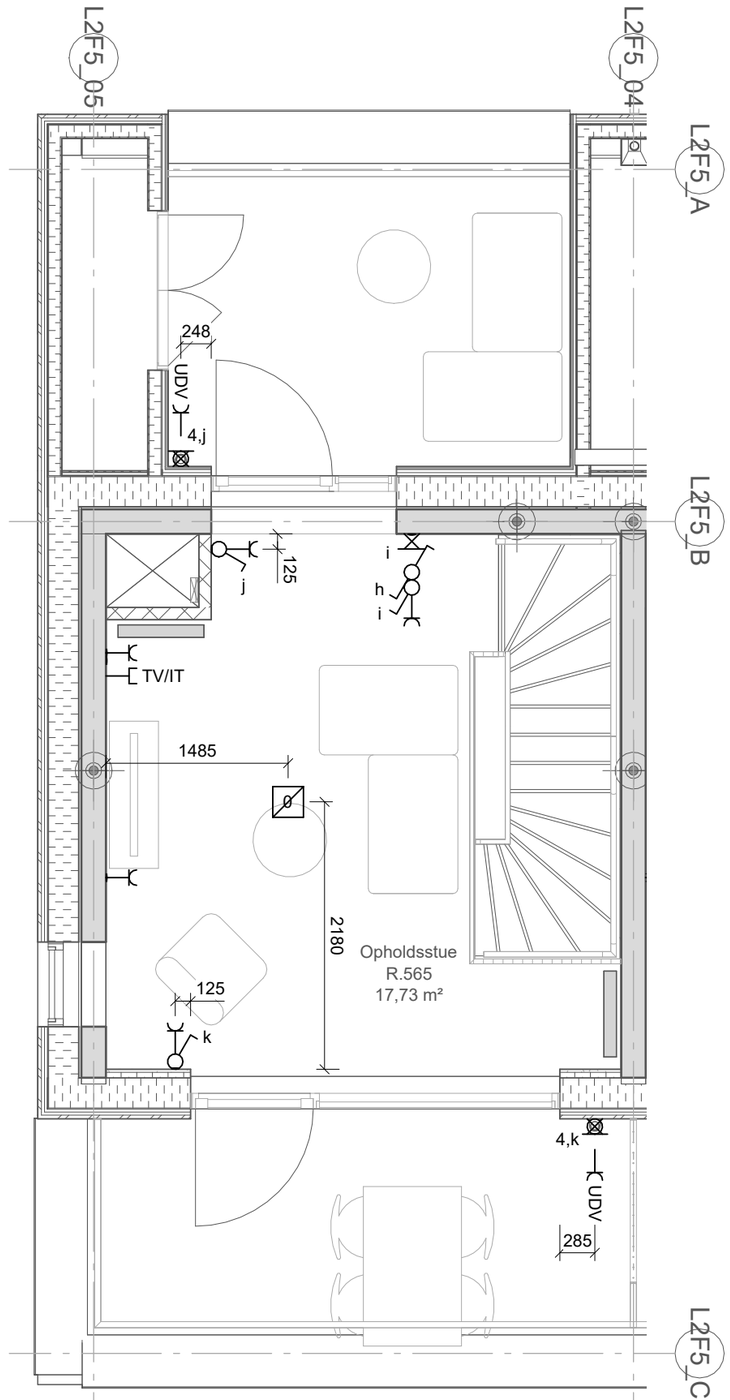

Projekt: Stejlepladsen

Tekst: Elinstallationer -
Byg F5 - 1. til 3. Sal
DUP_5V_T31 - Side F5-10

Tegningsnr.: ISP2_K07_L2XX_H04_EXX_N931

Rev.:

Projektnr.: 1019198 | Dato: 2026-02-27 | Rev. Dato: | Mål: 1 : 50 | Side: F5-10

www.arteliagroup.dk | Fil: