Sheet Number	Tekst:	Dato:	Rev.:	Rev. Dato:
ISP2_K07_L2XX_H04_EFX_N931 - Side F6-1	Byg F6 - Index	2026-02-27		
ISP2_K07_L2XX_H04_EFX_N931 - Side F6-2	Byg F6 - Oversigtsplan	2026-02-27		
ISP2_K07_L2XX_H04_EFX_N931 - Side F6-3	Byg F6 - Stueplan	2026-02-27		
ISP2_K07_L2XX_H04_EFX_N931 - Side F6-4	Byg F6 - Stueplan	2026-02-27		
ISP2_K07_L2XX_H04_EFX_N931 - Side F6-5	Byg F6 - Stueplan	2026-02-27		
ISP2_K07_L2XX_H04_EFX_N931 - Side F6-6	Byg F6 - Stueplan	2026-02-27		
ISP2_K07_L2XX_H04_EFX_N931 - Side F6-7	Byg F6 - 1. til 3. Sal	2026-02-27	1	2026-05-19
ISP2_K07_L2XX_H04_EFX_N931 - Side F6-8	Byg F6 - 1. til 3. Sal	2026-02-27	1	2026-05-19
ISP2_K07_L2XX_H04_EFX_N931 - Side F6-9	Byg F6 - 1. til 3. Sal	2026-02-27	1	2026-05-19
ISP2_K07_L2XX_H04_EFX_N931 - Side F6-10	Byg F6 - 1. til 3. Sal	2026-02-27	1	2026-05-19

Projekt: Stejlepladsen

Tekst: Elinstallationer - Byg F6 - Index

Tegningsnr.: ISP2_K07_L2XX_H04_EFX_N931


Rev.:

Projektnr.: 1019198 | Dato: 2026-02-27 | Rev. Dato: | Mål: | Side: F6-1

www.arteliagroup.dk | Fil:


Stueplan - Byg F6

F6_A

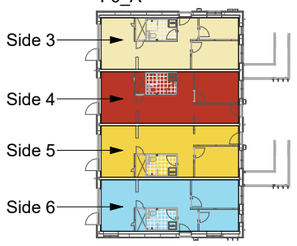


1. sal - Byg F6

F6_A

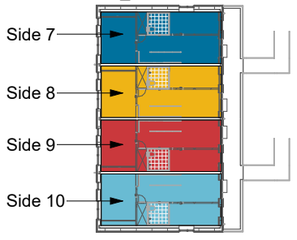


2. sal - Byg F6

F6_A

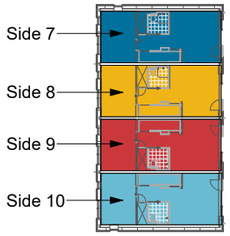

3. sal - Byg F6

F6_A

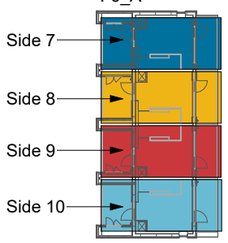

Oversigt, bygning F6:

Side 3:		Duplexhuse, Byg A, st., 2,5V
Side 4:		Duplexhuse, Byg A, st., 2V
Side 5:		Duplexhuse, Byg A, st., 2V
Side 6:		Duplexhuse, Byg A, st., 2,5V
Side 7:		Duplexhuse, Byg A, 1. til 3. Sal, 5V
Side 8:		Duplexhuse, Byg A, 1. til 3. Sal, 5V
Side 9:		Duplexhuse, Byg A, 1. til 3. Sal, 5V
Side 10:		Duplexhuse, Byg A, 1. til 3. Sal, 5V

Projekt: Stejlepladsen


Tekst: Elinstallationer -
Byg F6 - Oversigtsplan

Tegningsnr.: ISP2_K07_L2XX_H04_EFX_N931


Rev.:

Projektnr.: 1019198 | Dato: 2026-02-27 | Rev. Dato: | Mål: 1 : 500 | Side: F6-2


www.arteliagroup.dk | Fil:

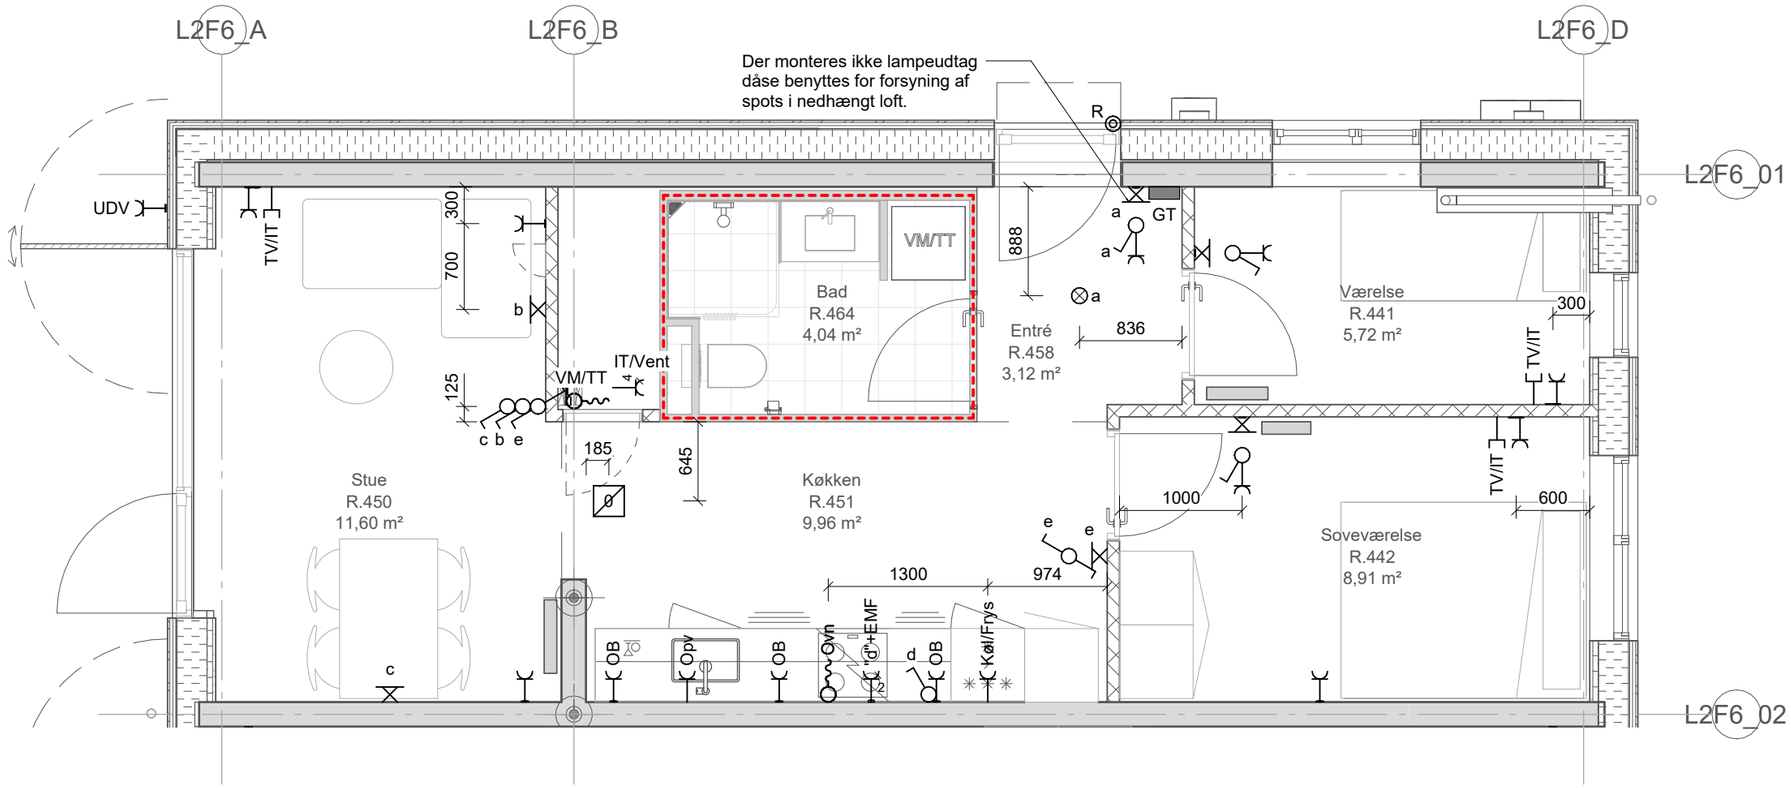

Projekt:	Stejlepladsen				
Tekst:	Elinstallationer - Byg F6 - Stueplan DUP_2,5V_T30_ST - Side F6-3			Tegningsnr.:	Rev.:
				ISP2_K07_L2XX_H04_EFX_N931	
Projektnr.: 1019198	Dato: 2026-02-27	Rev. Dato:		Mål: 1 : 50	Side: F6-3
www.arteliagroup.dk	Fil:				

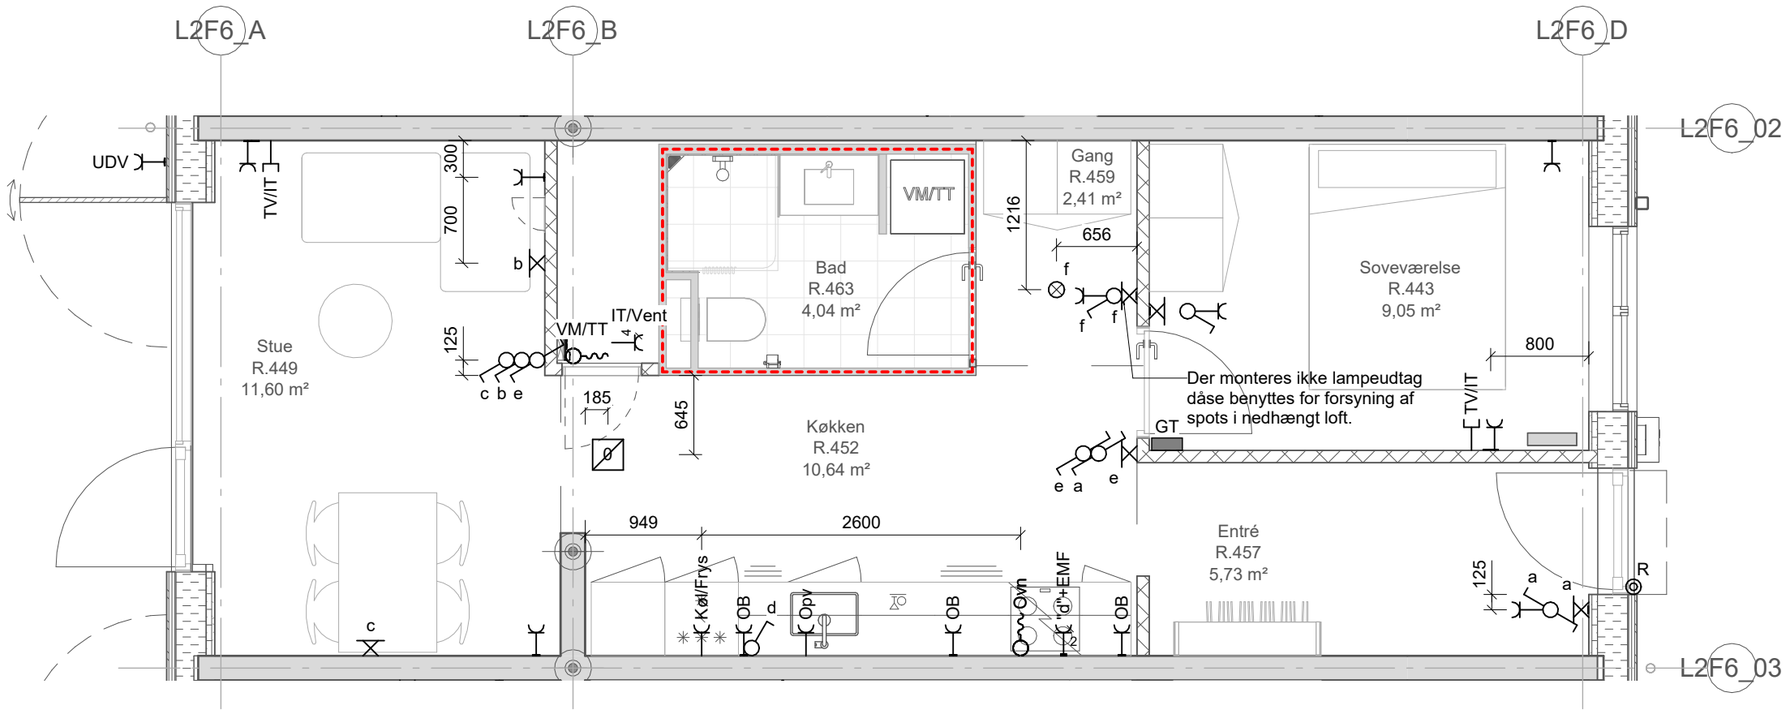

Projekt:	Stejlepladsen				
Tekst:	Elinstallationer - Byg F6 - Stueplan DUP_2V_T30_ST - Side F6-4			Tegningsnr.:	Rev.:
				ISP2_K07_L2XX_H04_EFX_N931	
Projektnr.: 1019198	Dato: 2026-02-27	Rev. Dato:		Mål: 1 : 50	Side: F6-4
www.arteliagroup.dk	Fil:				

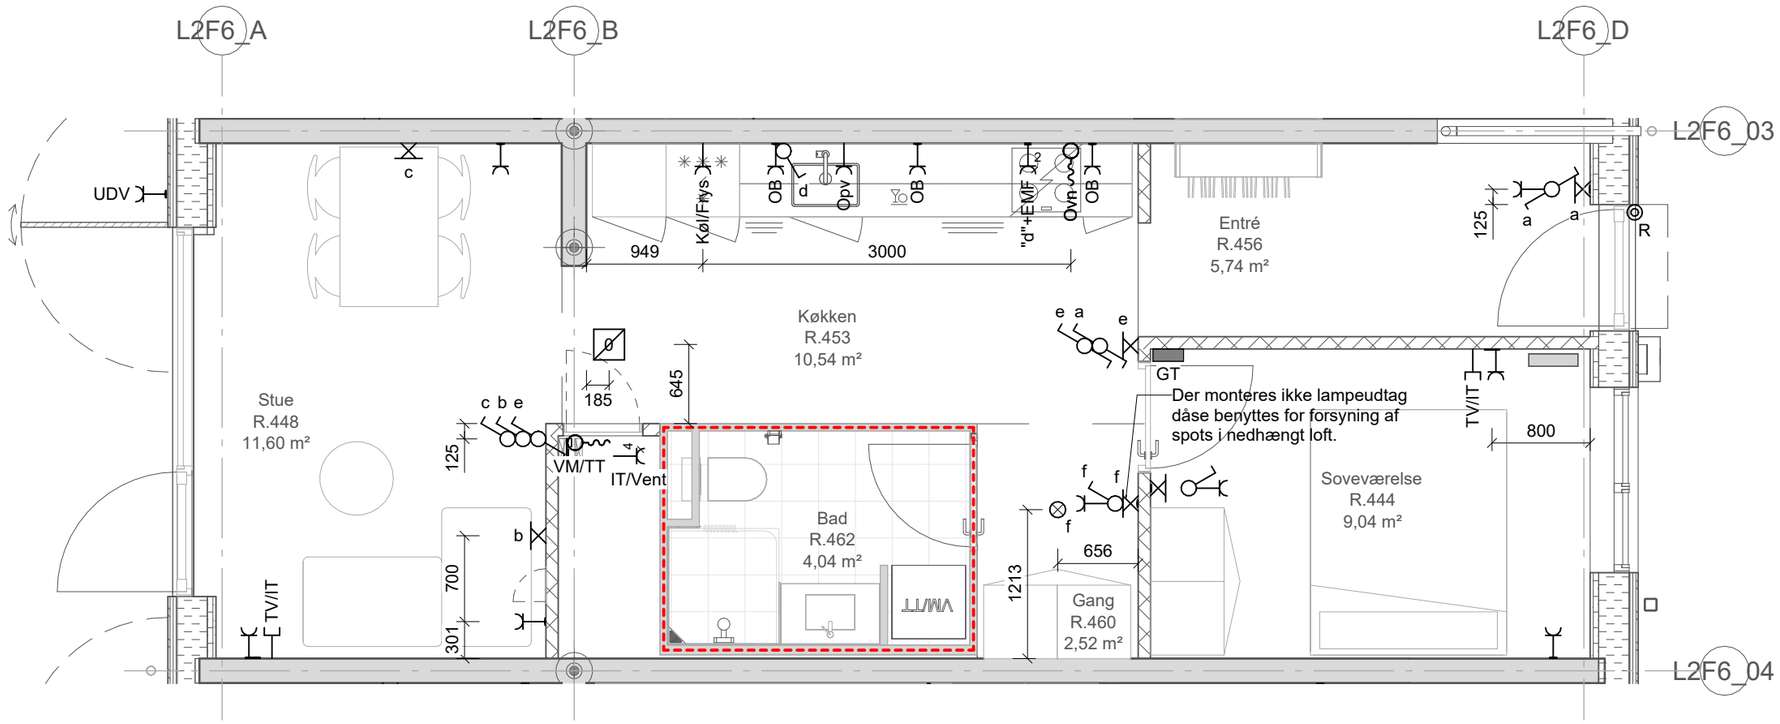

Projekt: Stejlepladsen


Tekst: Elinstallationer -
Byg F6 - Stueplan
DUP_2V_T30_ST_S - Side F6-5

Tegningsnr.: ISP2_K07_L2XX_H04_EFX_N931

Rev.:

Projektnr.: 1019198 | Dato: 2026-02-27 | Rev. Dato: | Mål: 1 : 50 | Side: F6-5

www.arteliagroup.dk | Fil:

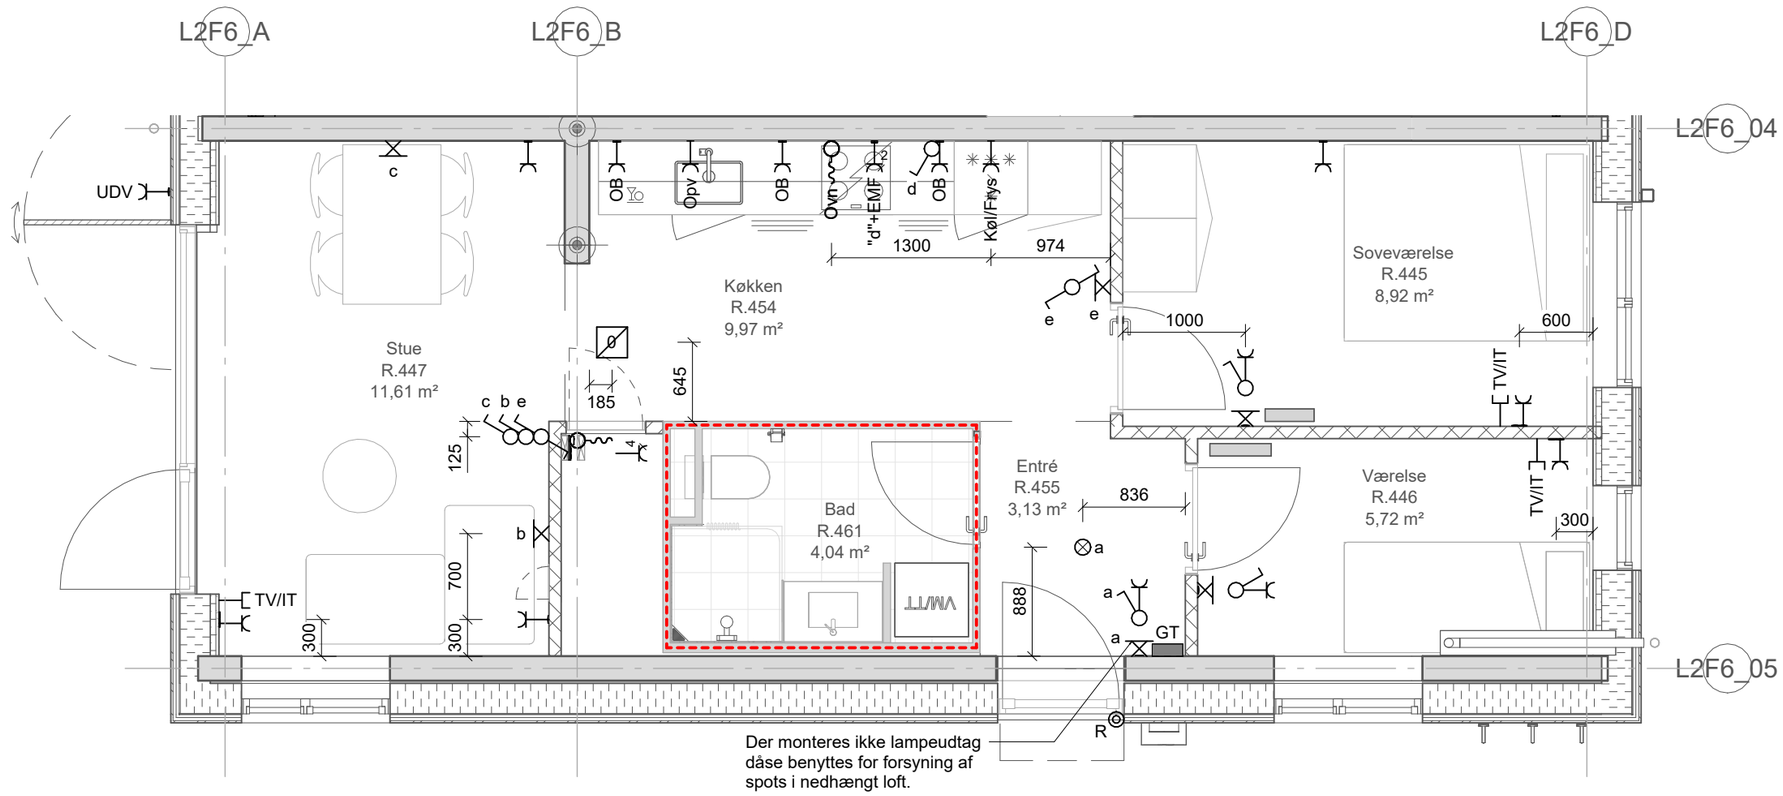

Projekt: Stejlepladsen


Tekst: Elinstallationer -
Byg F6 - Stueplan
DUP_2,5V_T30_ST_S - Side F6-6


Tegningsnr.: ISP2_K07_L2XX_H04_EFX_N931


Rev.:

Projektnr.: 1019198 | Dato: 2026-02-27 | Rev. Dato: | Mål: 1 : 50 | Side: F6-6

www.arteliagroup.dk | Fil:

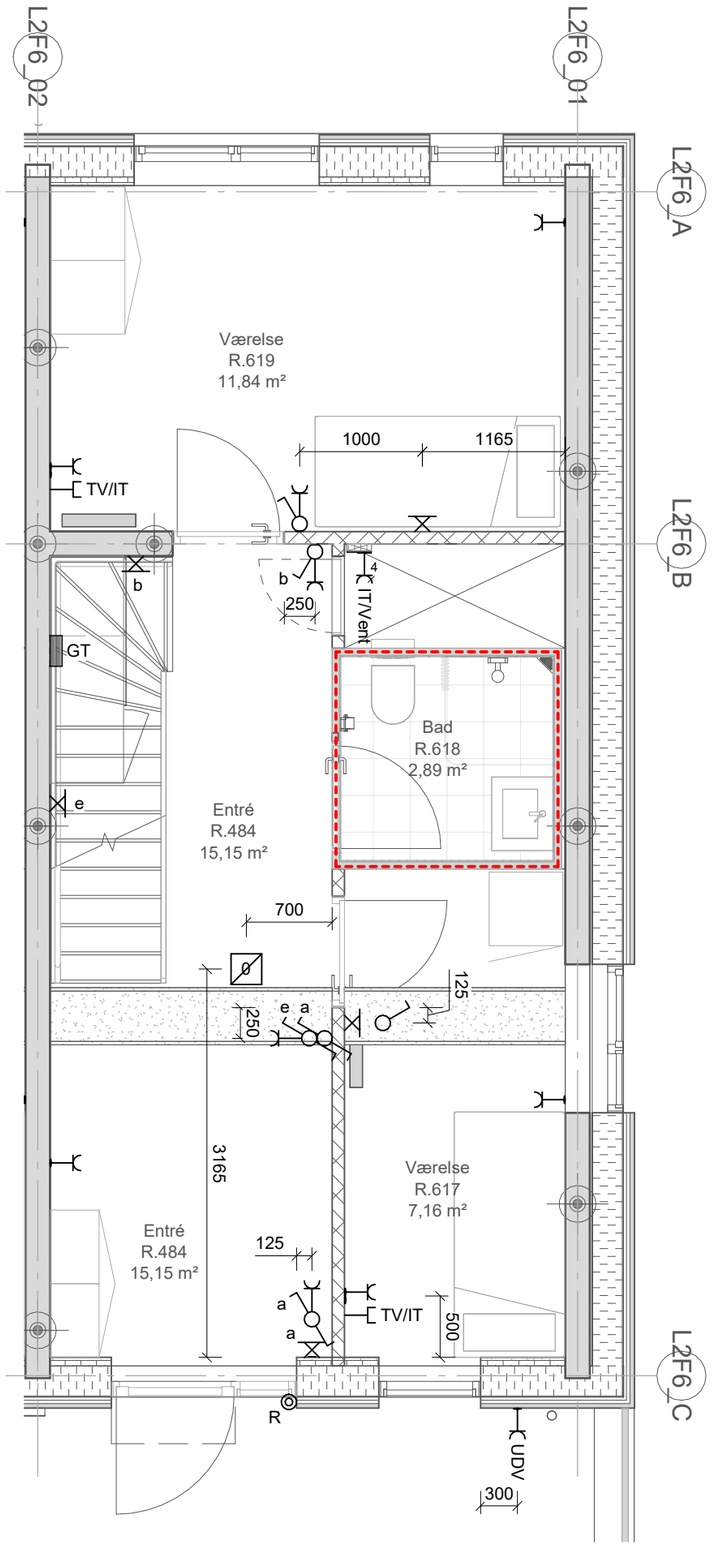

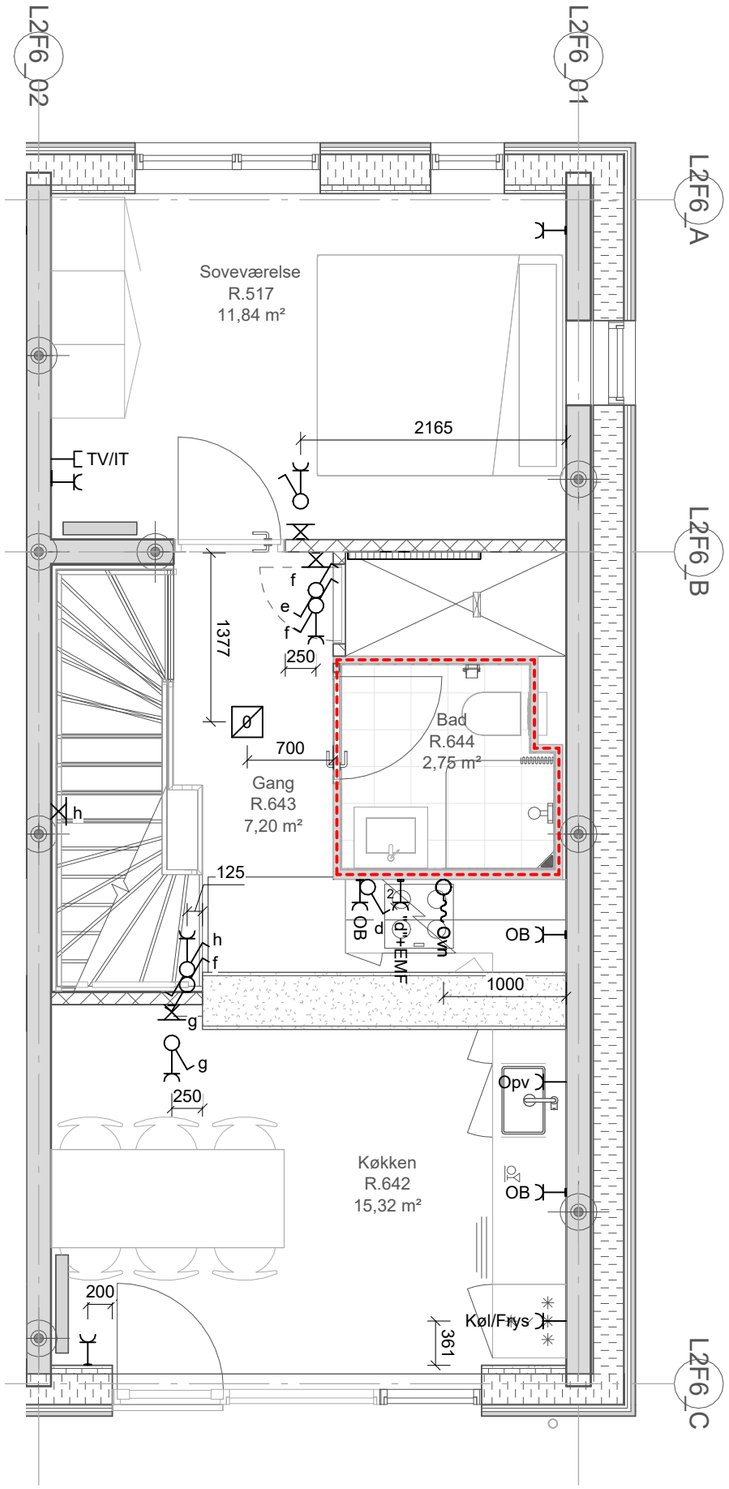

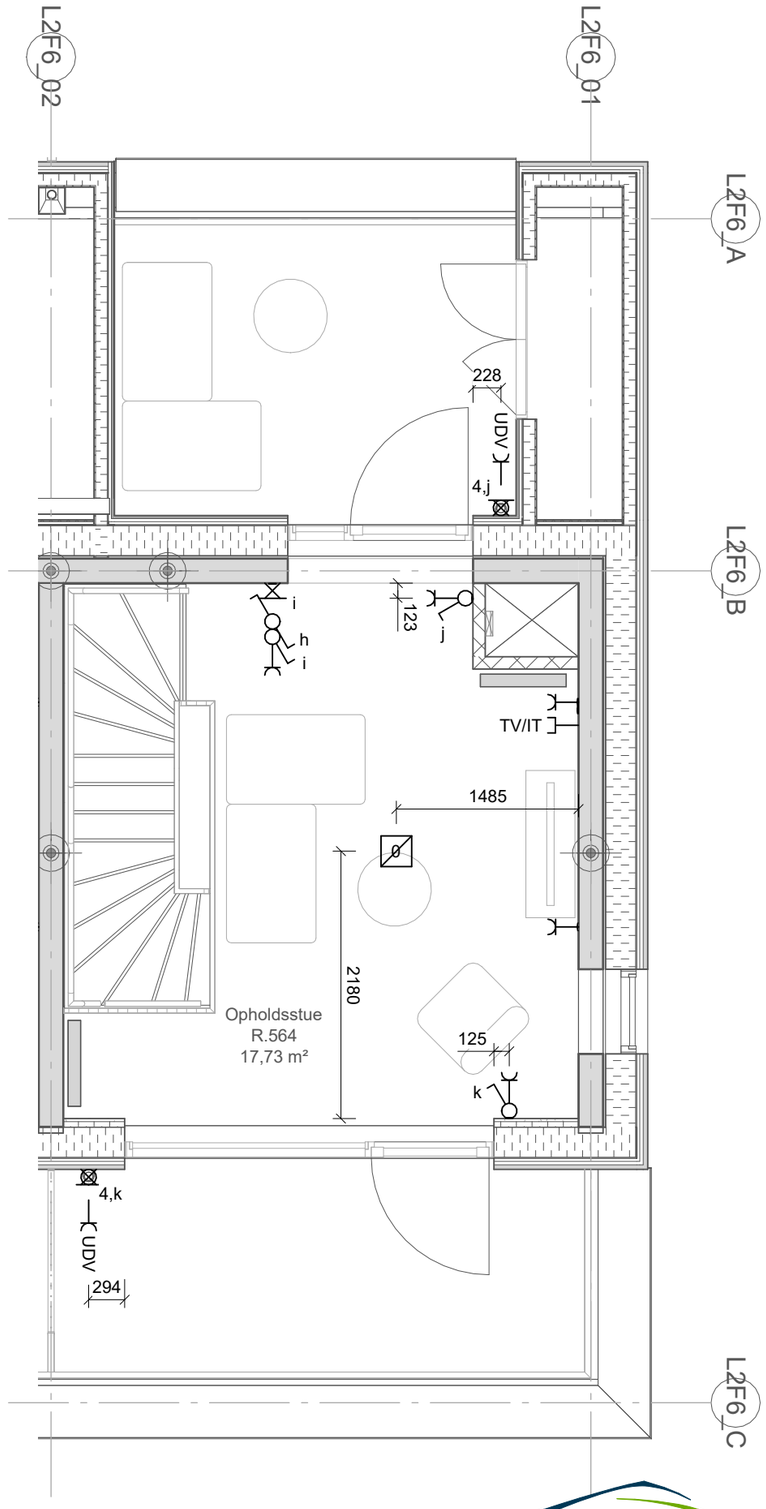

Projekt: Stejlepladsen

ARTELIA


Tekst: Elinstallationer -
Byg F6 - 1. til 3. Sal
DUP_5V_T31_S - Side F6-7


Tegningsnr.: ISP2_K07_L2XX_H04_EFX_N931


Rev.: 1

Projektnr.: 1019198 | Dato: 2026-02-27 | Rev. Dato: 2026-05-19 | Mål: 1 : 50 | Side: F6-7

www.arteliagroup.dk | Fil:

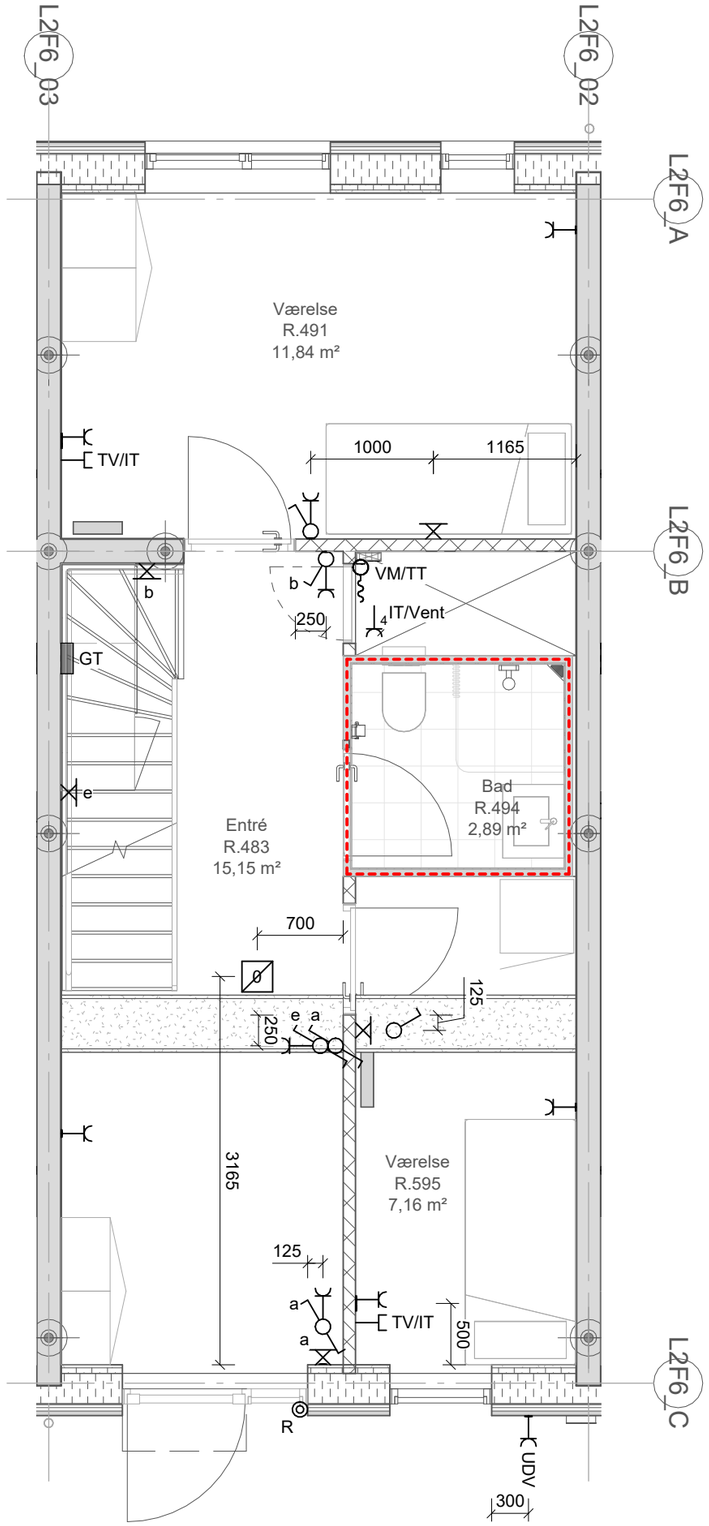

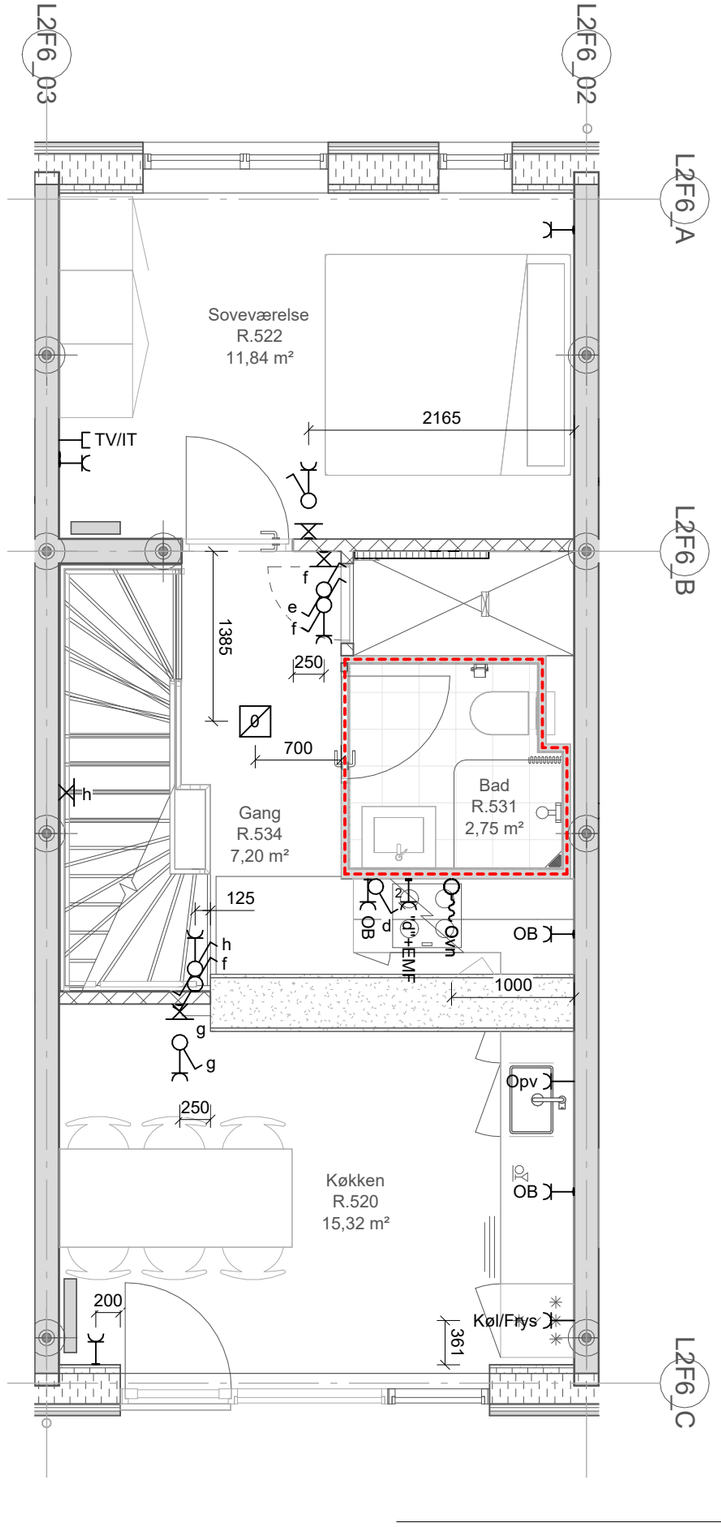

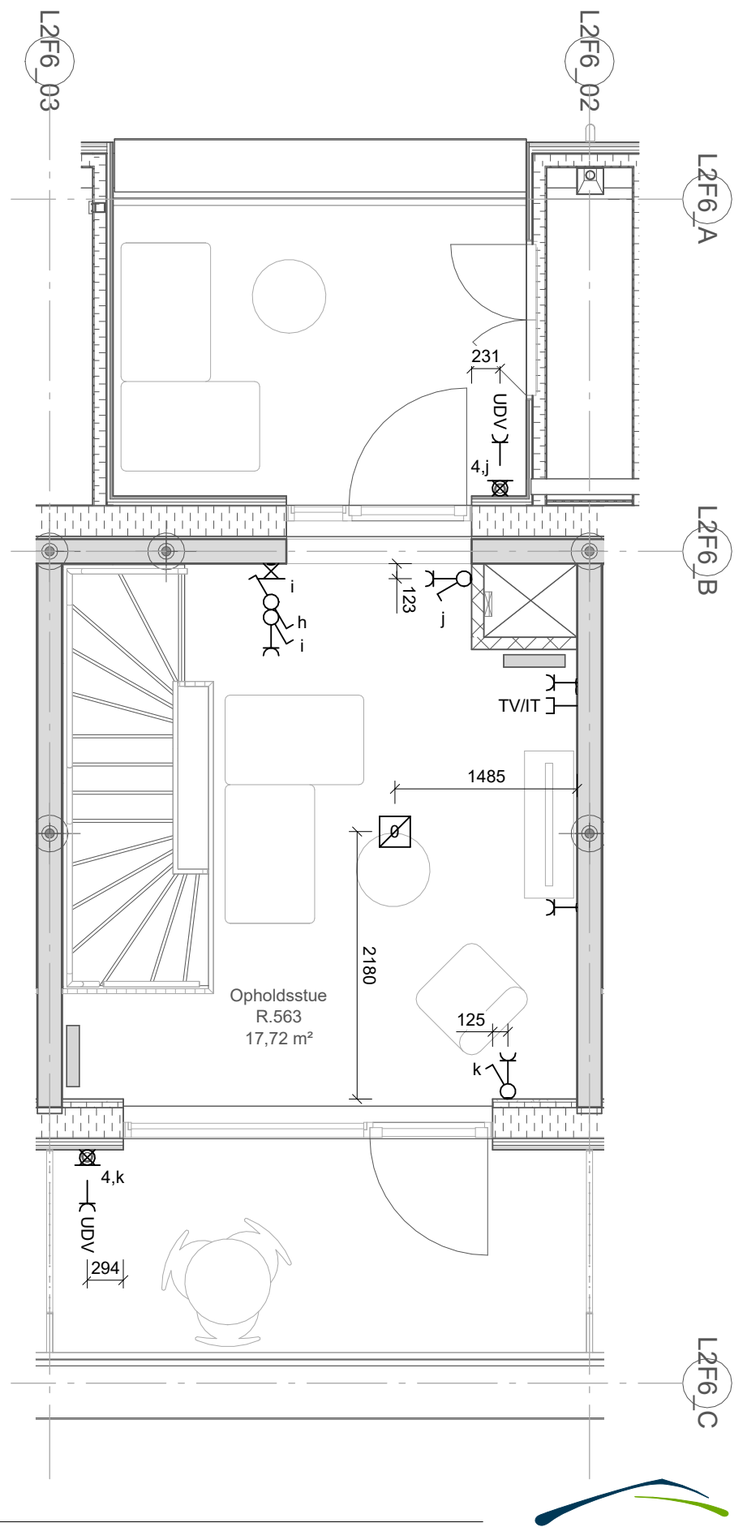

Projekt: Stejlepladsen


Tekst: Elinstallationer -
Byg F6 - 1. til 3. Sal
DUP_5V_T32_S - Side F6-8


Tegningsnr.: ISP2_K07_L2XX_H04_EFX_N931


Rev.: 1

Projektnr.: 1019198 | Dato: 2026-02-27 | Rev. Dato: 2026-05-19 | Mål: 1 : 50 | Side: F6-8

www.arteliagroup.dk | Fil:

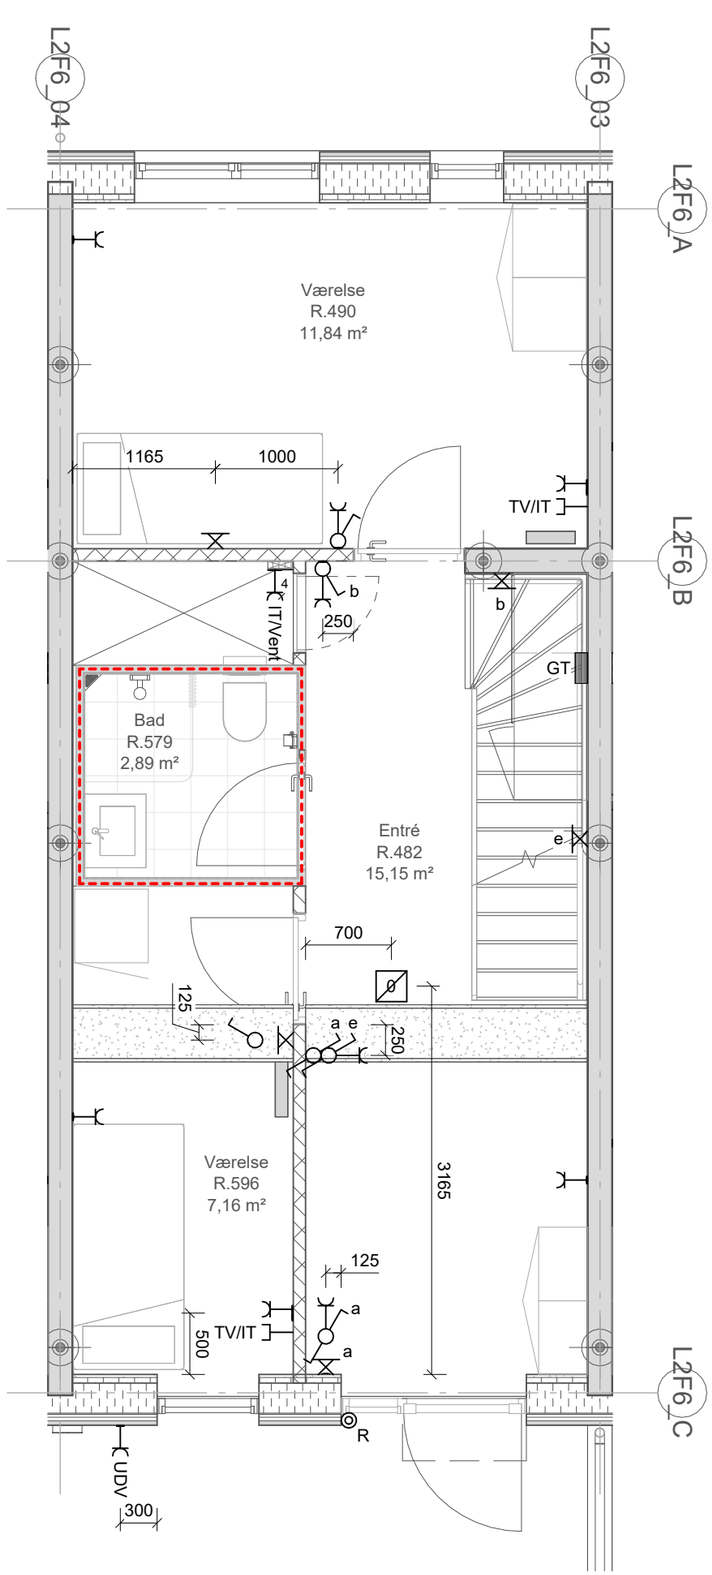

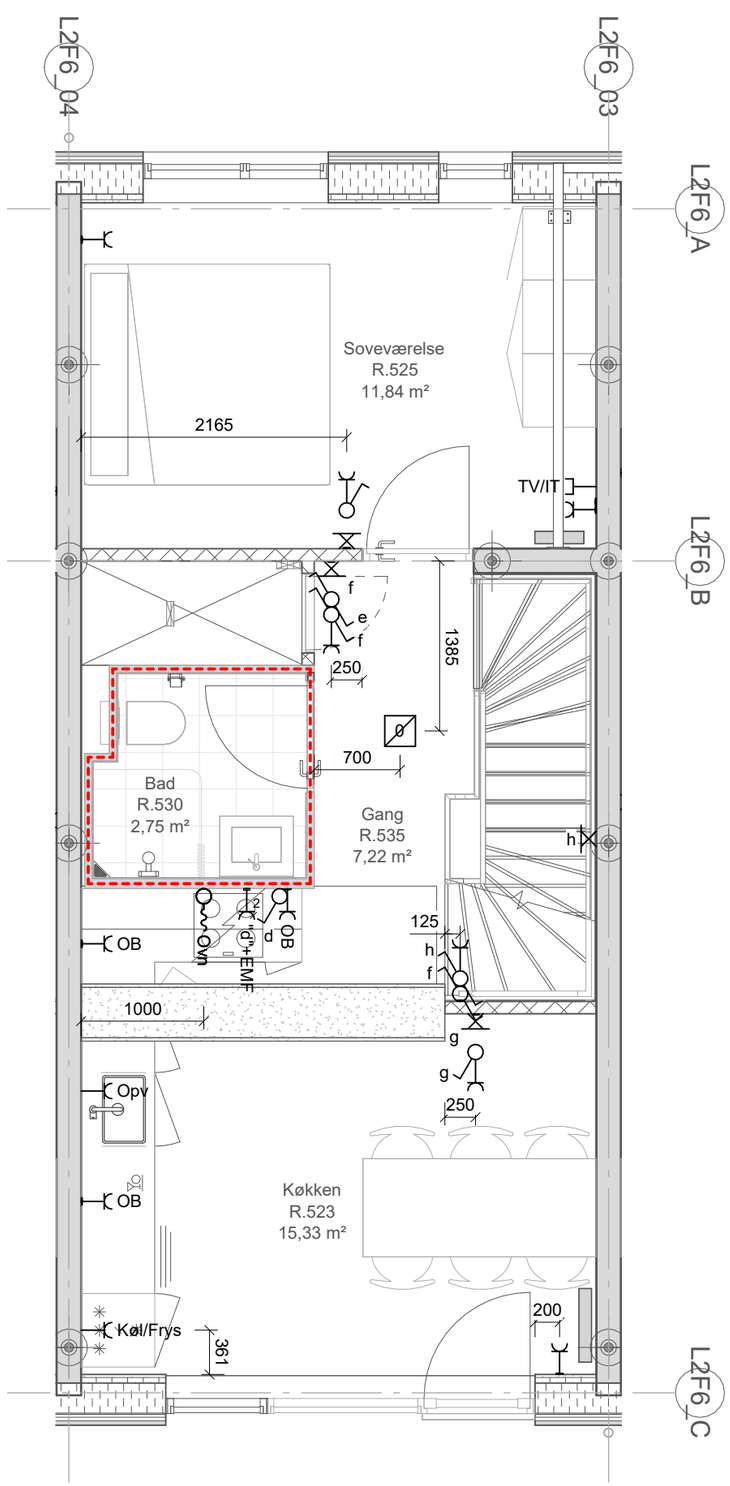

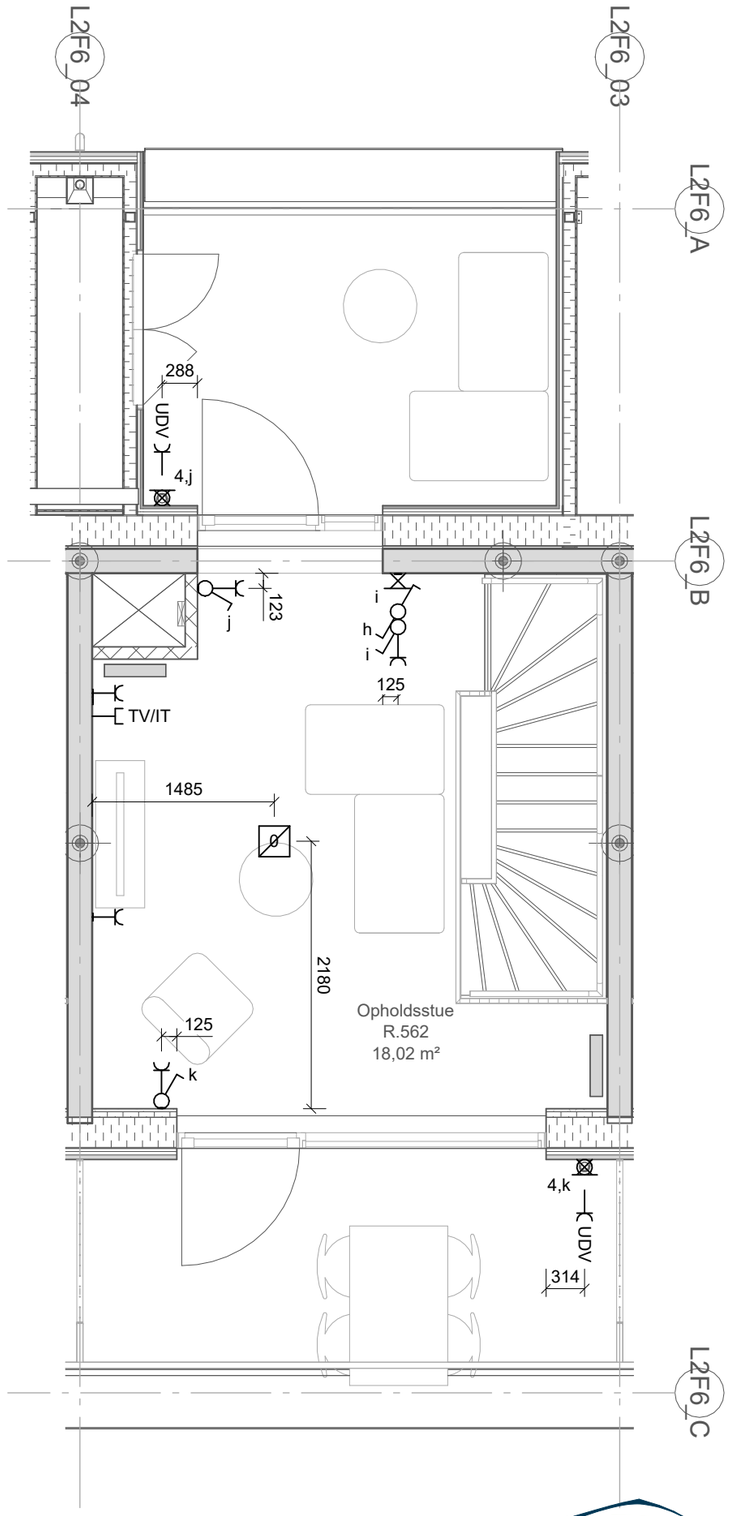

Projekt: Stejlepladsen


Tekst: Elinstallationer -
Byg F6 - 1. til 3. Sal
DUP_5V_T32 - Side F6-9


Tegningsnr.: ISP2_K07_L2XX_H04_EFX_N931


Rev.: 1

Projektnr.: 1019198 | Dato: 2026-02-27 | Rev. Dato: 2026-05-19 | Mål: 1 : 50 | Side: F6-9

www.arteliagroup.dk | Fil:

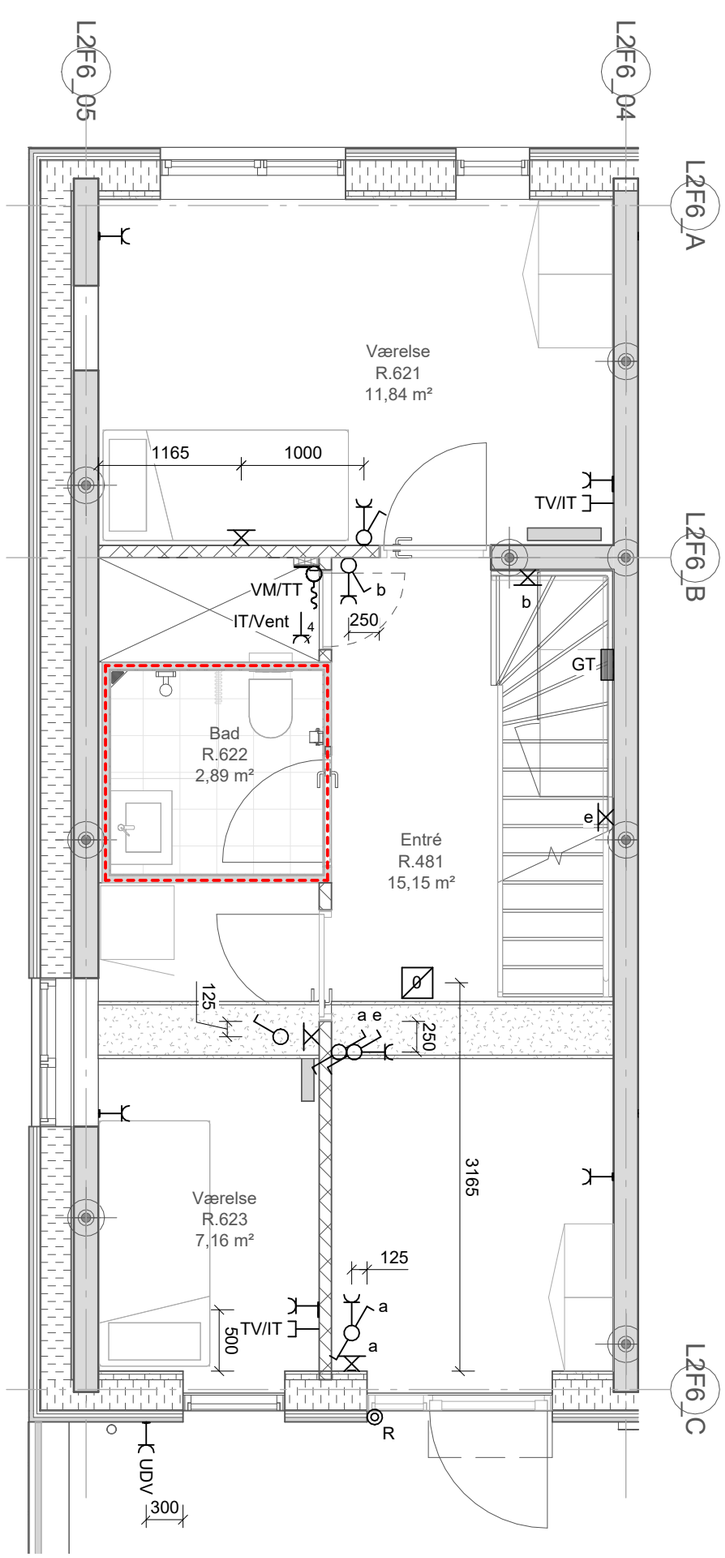

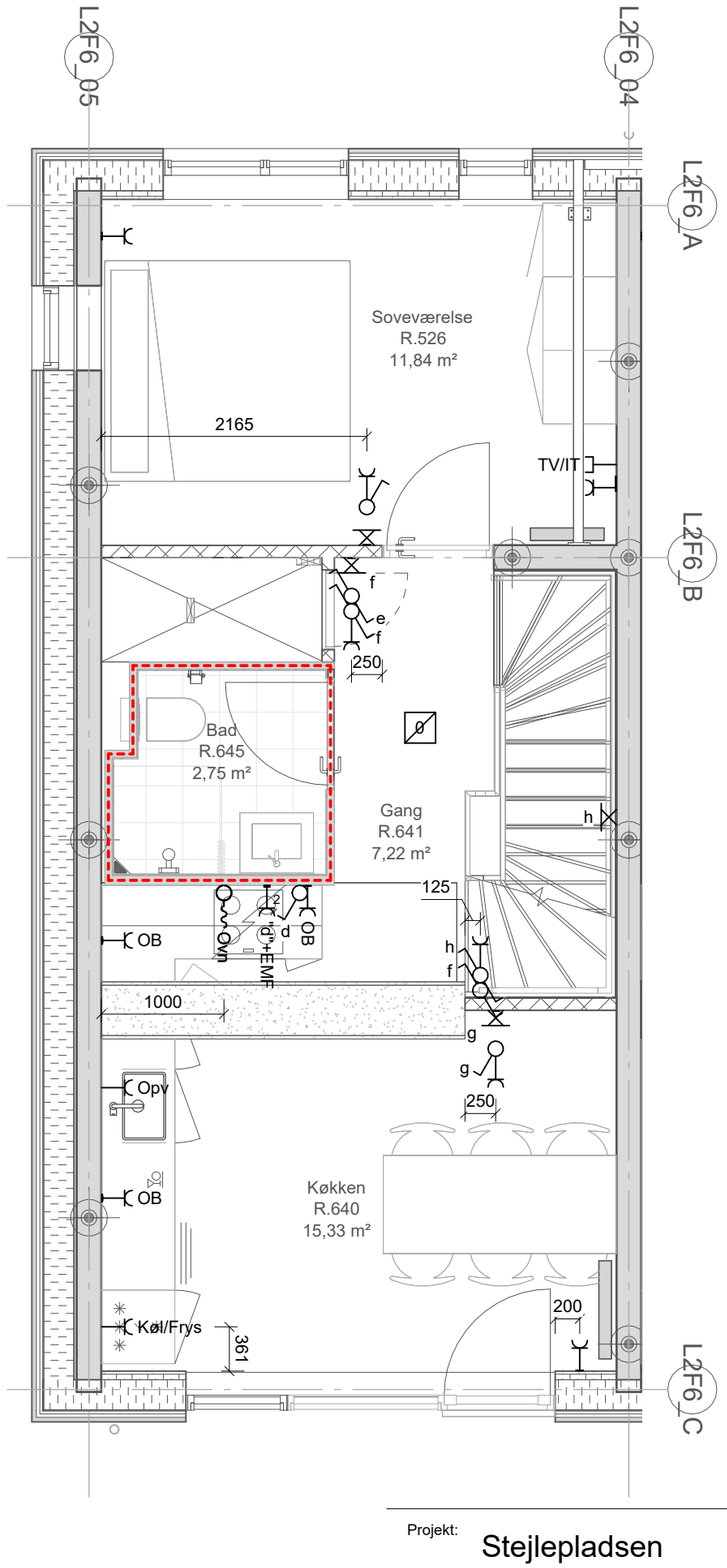

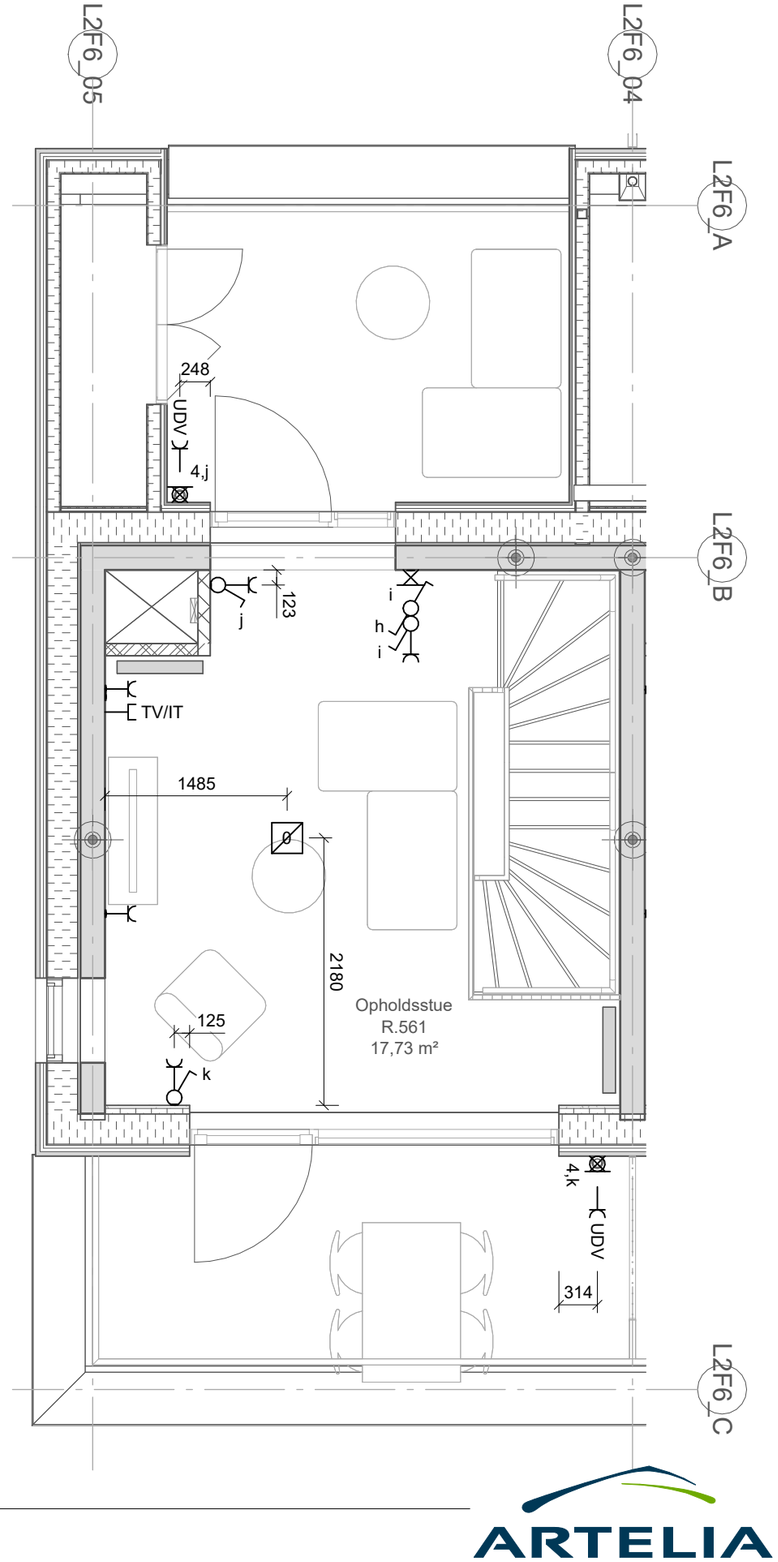

Projekt: Stejlepladsen

Tekst: Elinstallationer -
Byg F6 - 1. til 3. Sal
DUP_5V_T31 - Side F6-10

Tegningsnr.: ISP2_K07_L2XX_H04_EFX_N931

Rev.: 1

Projektnr.: 1019198 | Dato: 2026-02-27 | Rev. Dato: 2026-05-19 | Mål: 1 : 50 | Side: F6-10

www.arteliagroup.dk | Fil: